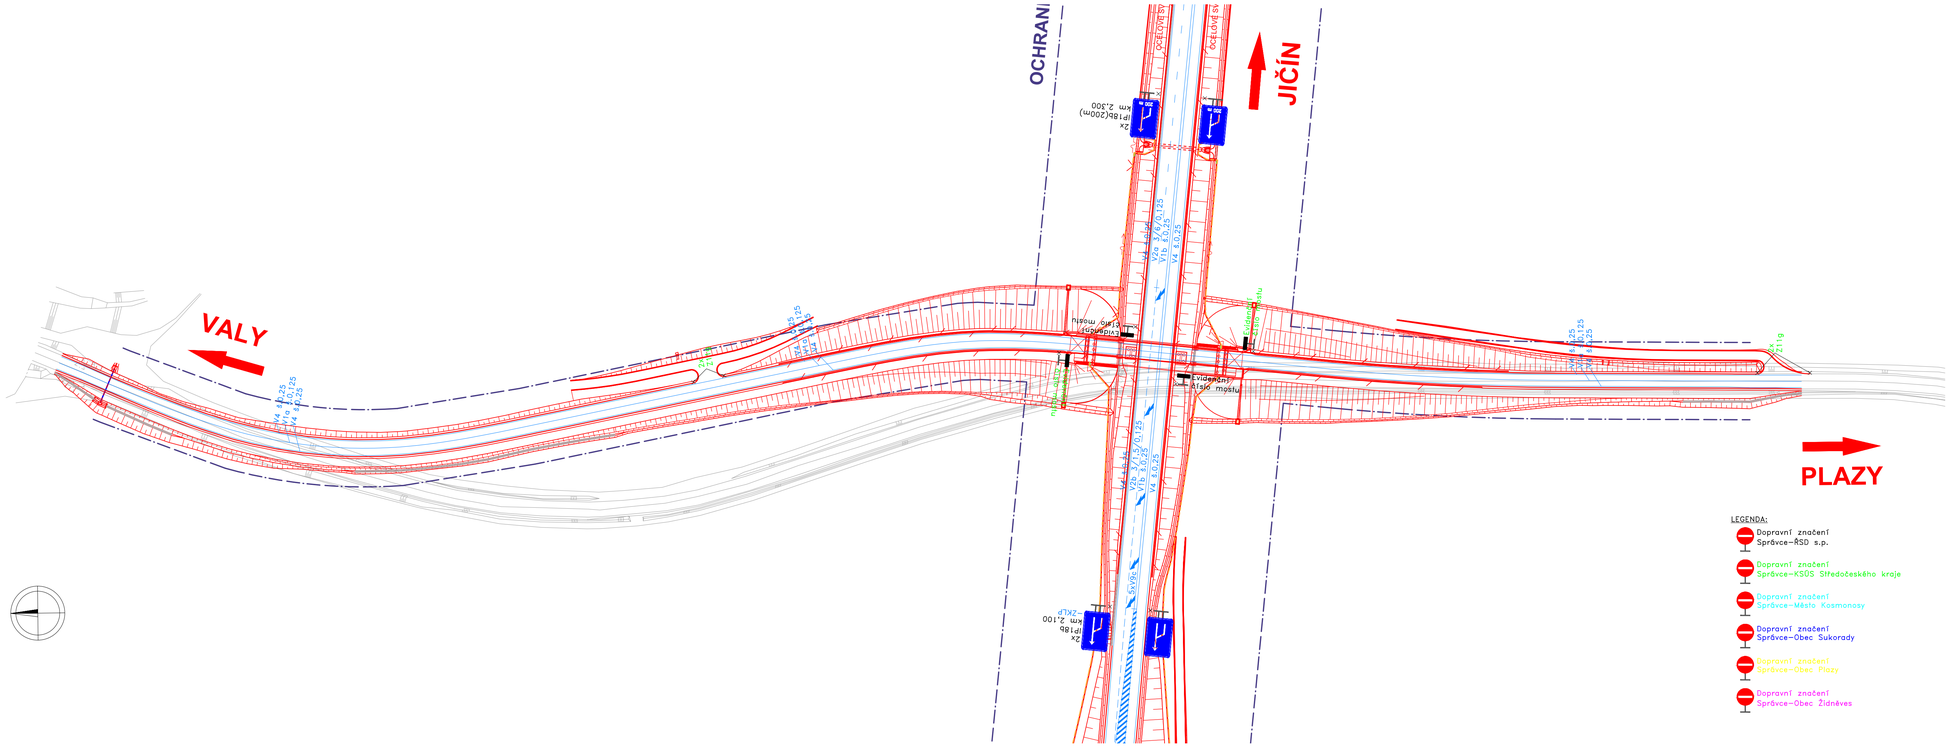

LEGENDA:

- Dopravní značení Správce–ŘSD s.p.
- Dopravní značení Správce–KSÚS Středočeského kraje
- Dopravní značení Správce–Město Kosmonosy
- Dopravní značení Správce–Obec Sukorady
- Dopravní značení Správce–Obec Plazy
- Dopravní značení Správce–Obec Žíděves

Souřadnicový systém: S-JTSK
Výškový systém: Bpv

SO 121 Přeložka silnice III/2768 v km 2,200

Objednatel:
ŘEDITELSTVÍ SILNIC A DÁLNIC
Ředitelství silnic a dálnic s. p.
Čerčanská 2023/12, Krč, 140 00 Praha 4

Zhotovitel:
Valbek
Valbek, spol. s r.o.
Vaňurova 505/17
460 07 Liberec 3

DISK	**Vypracoval**	STANISLAV KRUPIČKA	**Zak. číslo**	024-24
	Zodp. projektant	ING. PETER HAJOŠ	**Datum**	02/2025
	Tech. kontrola	ANTONÍN SEIDL	**Stupeň**	PDPS
	Akce	**I/16 MLADÁ BOLESLAV - MARTINOVICE**	**Počet formátů**	5 x A4
			Měřítko	1 : 1000
			Č. přílohy	Pare
Zhotovitel: DISK s.r.o. Merklovská 1239/10 160 00 Praha 6	**Příloha**	DOPRAVNÍ ZNAČENÍ	7	