


I/16 MLADÁ BOLESLAV - MARTINOVICE
SO 121 PŘELOŽKA SILNICE III/2768 V KM 2,200
VEGETAČNÍ ÚPRAVY M 1:1 000

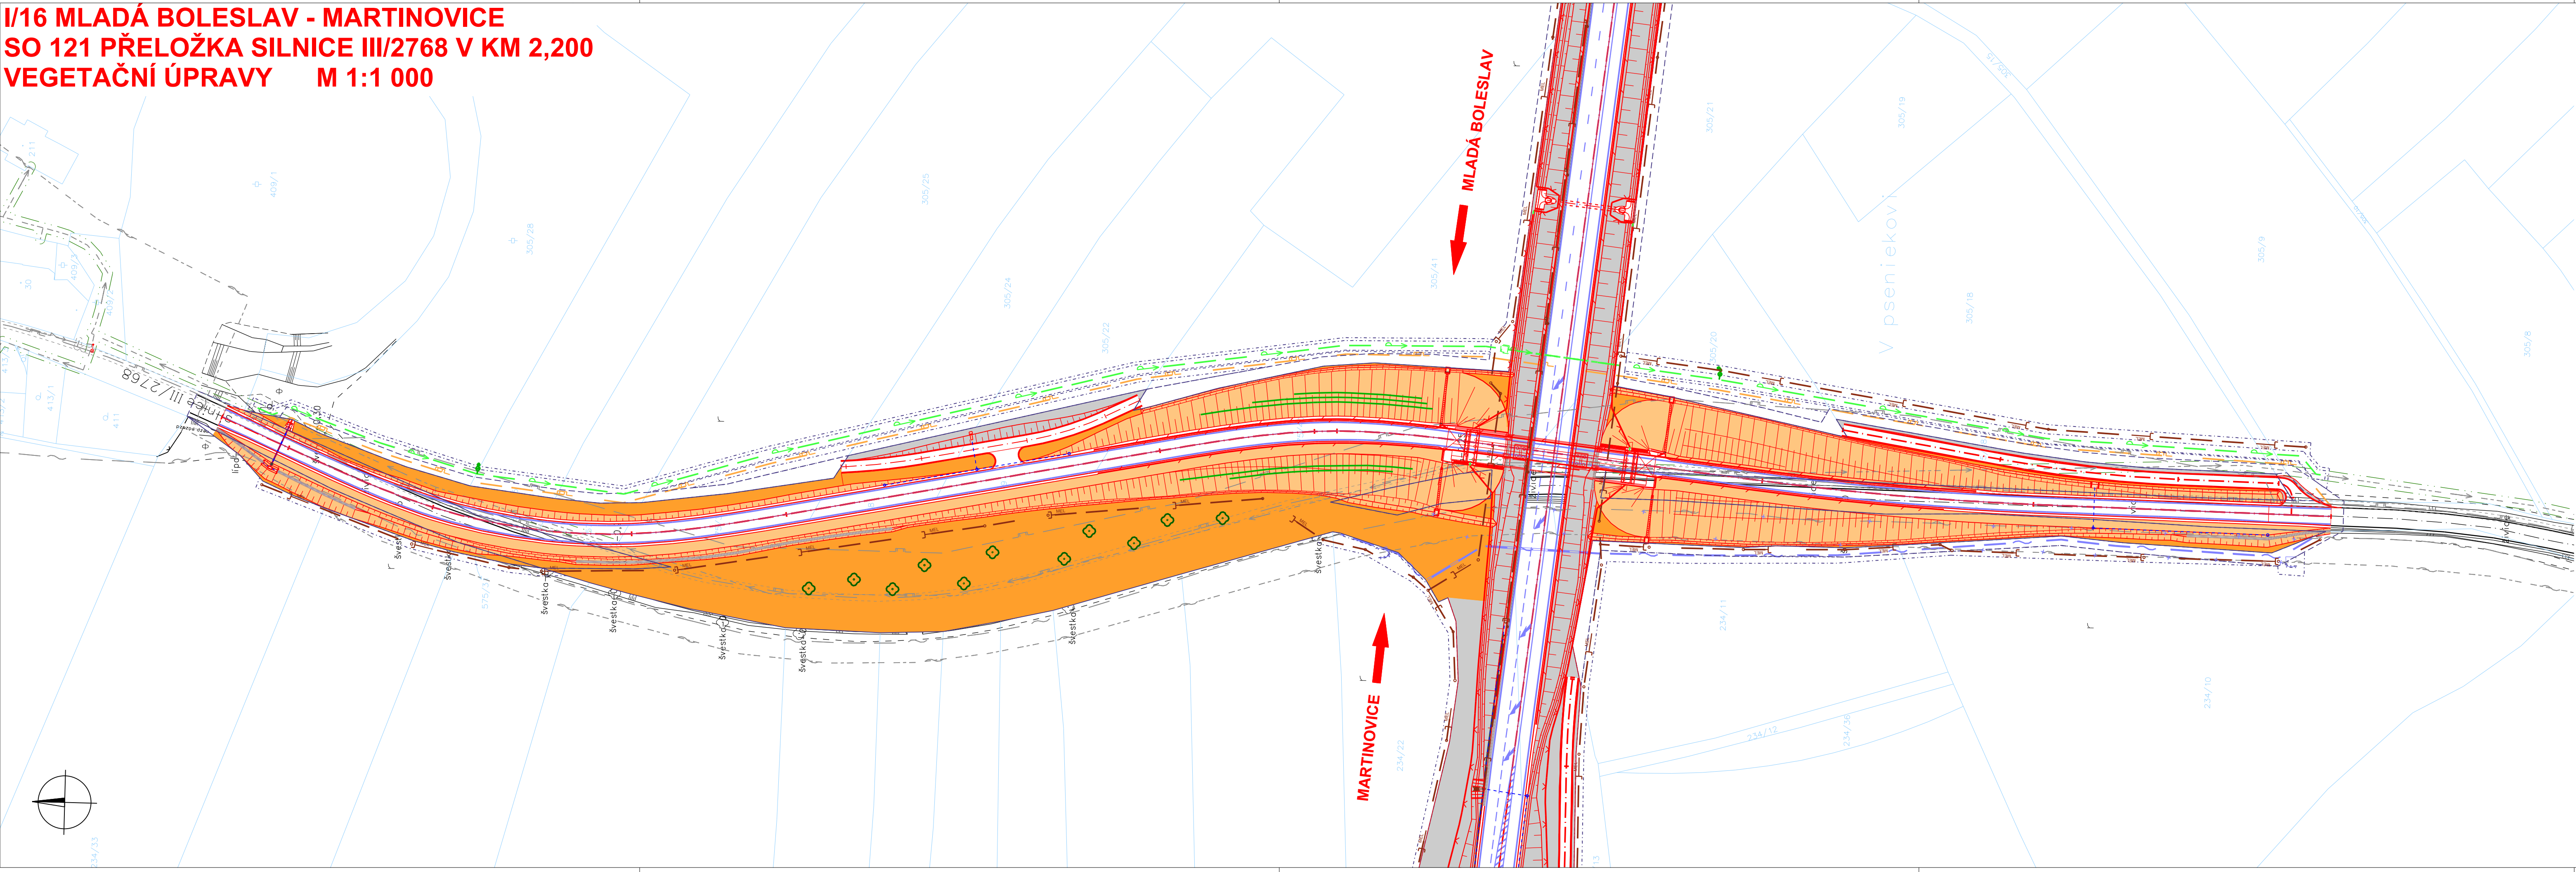

- LEGENDA
- Vegetační úpravy
- ZATRAVNĚNÍ V ROVINĚ
 - ZATRAVNĚNÍ VE SVAHU
 - VÝSADBA KEŘŮ PLOŠNĚ
 - VÝSADBA KEŘŮ V PÁSECH
 - VÝSADBA STROMŮ
- Vegetační úpravy ostatních správců
- ZATRAVNĚNÍ
 - VÝSADBA KEŘŮ PLOŠNĚ
 - VÝSADBA KEŘŮ V PÁSECH
 - VÝSADBA STROMŮ LISTNATÝCH
 - VÝSADBA STROMŮ JEHLIČNATÝCH
 - MULČOVÁNÍ ŠTĚRKEM

Souřadnicový systém: S-JTSK
Výškový systém: Bpv

SO 121 Přeložka silnice III/2768 v km 2,200

Objednatel:



**ŘEDITELSTVÍ
SILNIC
A DÁLNIC**

Ředitelství silnic a dálnic s. p.
Čerčanská 2023/12, Krč, 140 00 Praha 4

Zhotovitel:	Valbek, spol. s r.o. Vaňurova 505/17 460 07 Liberec 3	HIP:
		ING. T. KLIMENT

	Vypracoval	ING. Š. SOKOLÁŘOVÁ		Zak. číslo	21-LI13-001
	Zodp. projektant	ING. T. KLIMENT		Datum	02/2025
	Tech. kontrola	ING. M. HANŽL		Stupeň	PDPS
	Akce I/16 MLADÁ BOLESLAV - MARTINOVICE			Počet formátů	5 x A4
				Měřítko	1 : 1000
Zhotovitel: Valbek, spol. s r.o. Vaňurova 505/17 460 07 Liberec 3	Příloha VEGETAČNÍ ÚPRAVY			Č. přílohy	Paré
				8	