


SO 122 - PŘELOŽKA SILNICE III/27612 V km 6,080
SITUACE, M 1 : 1 000

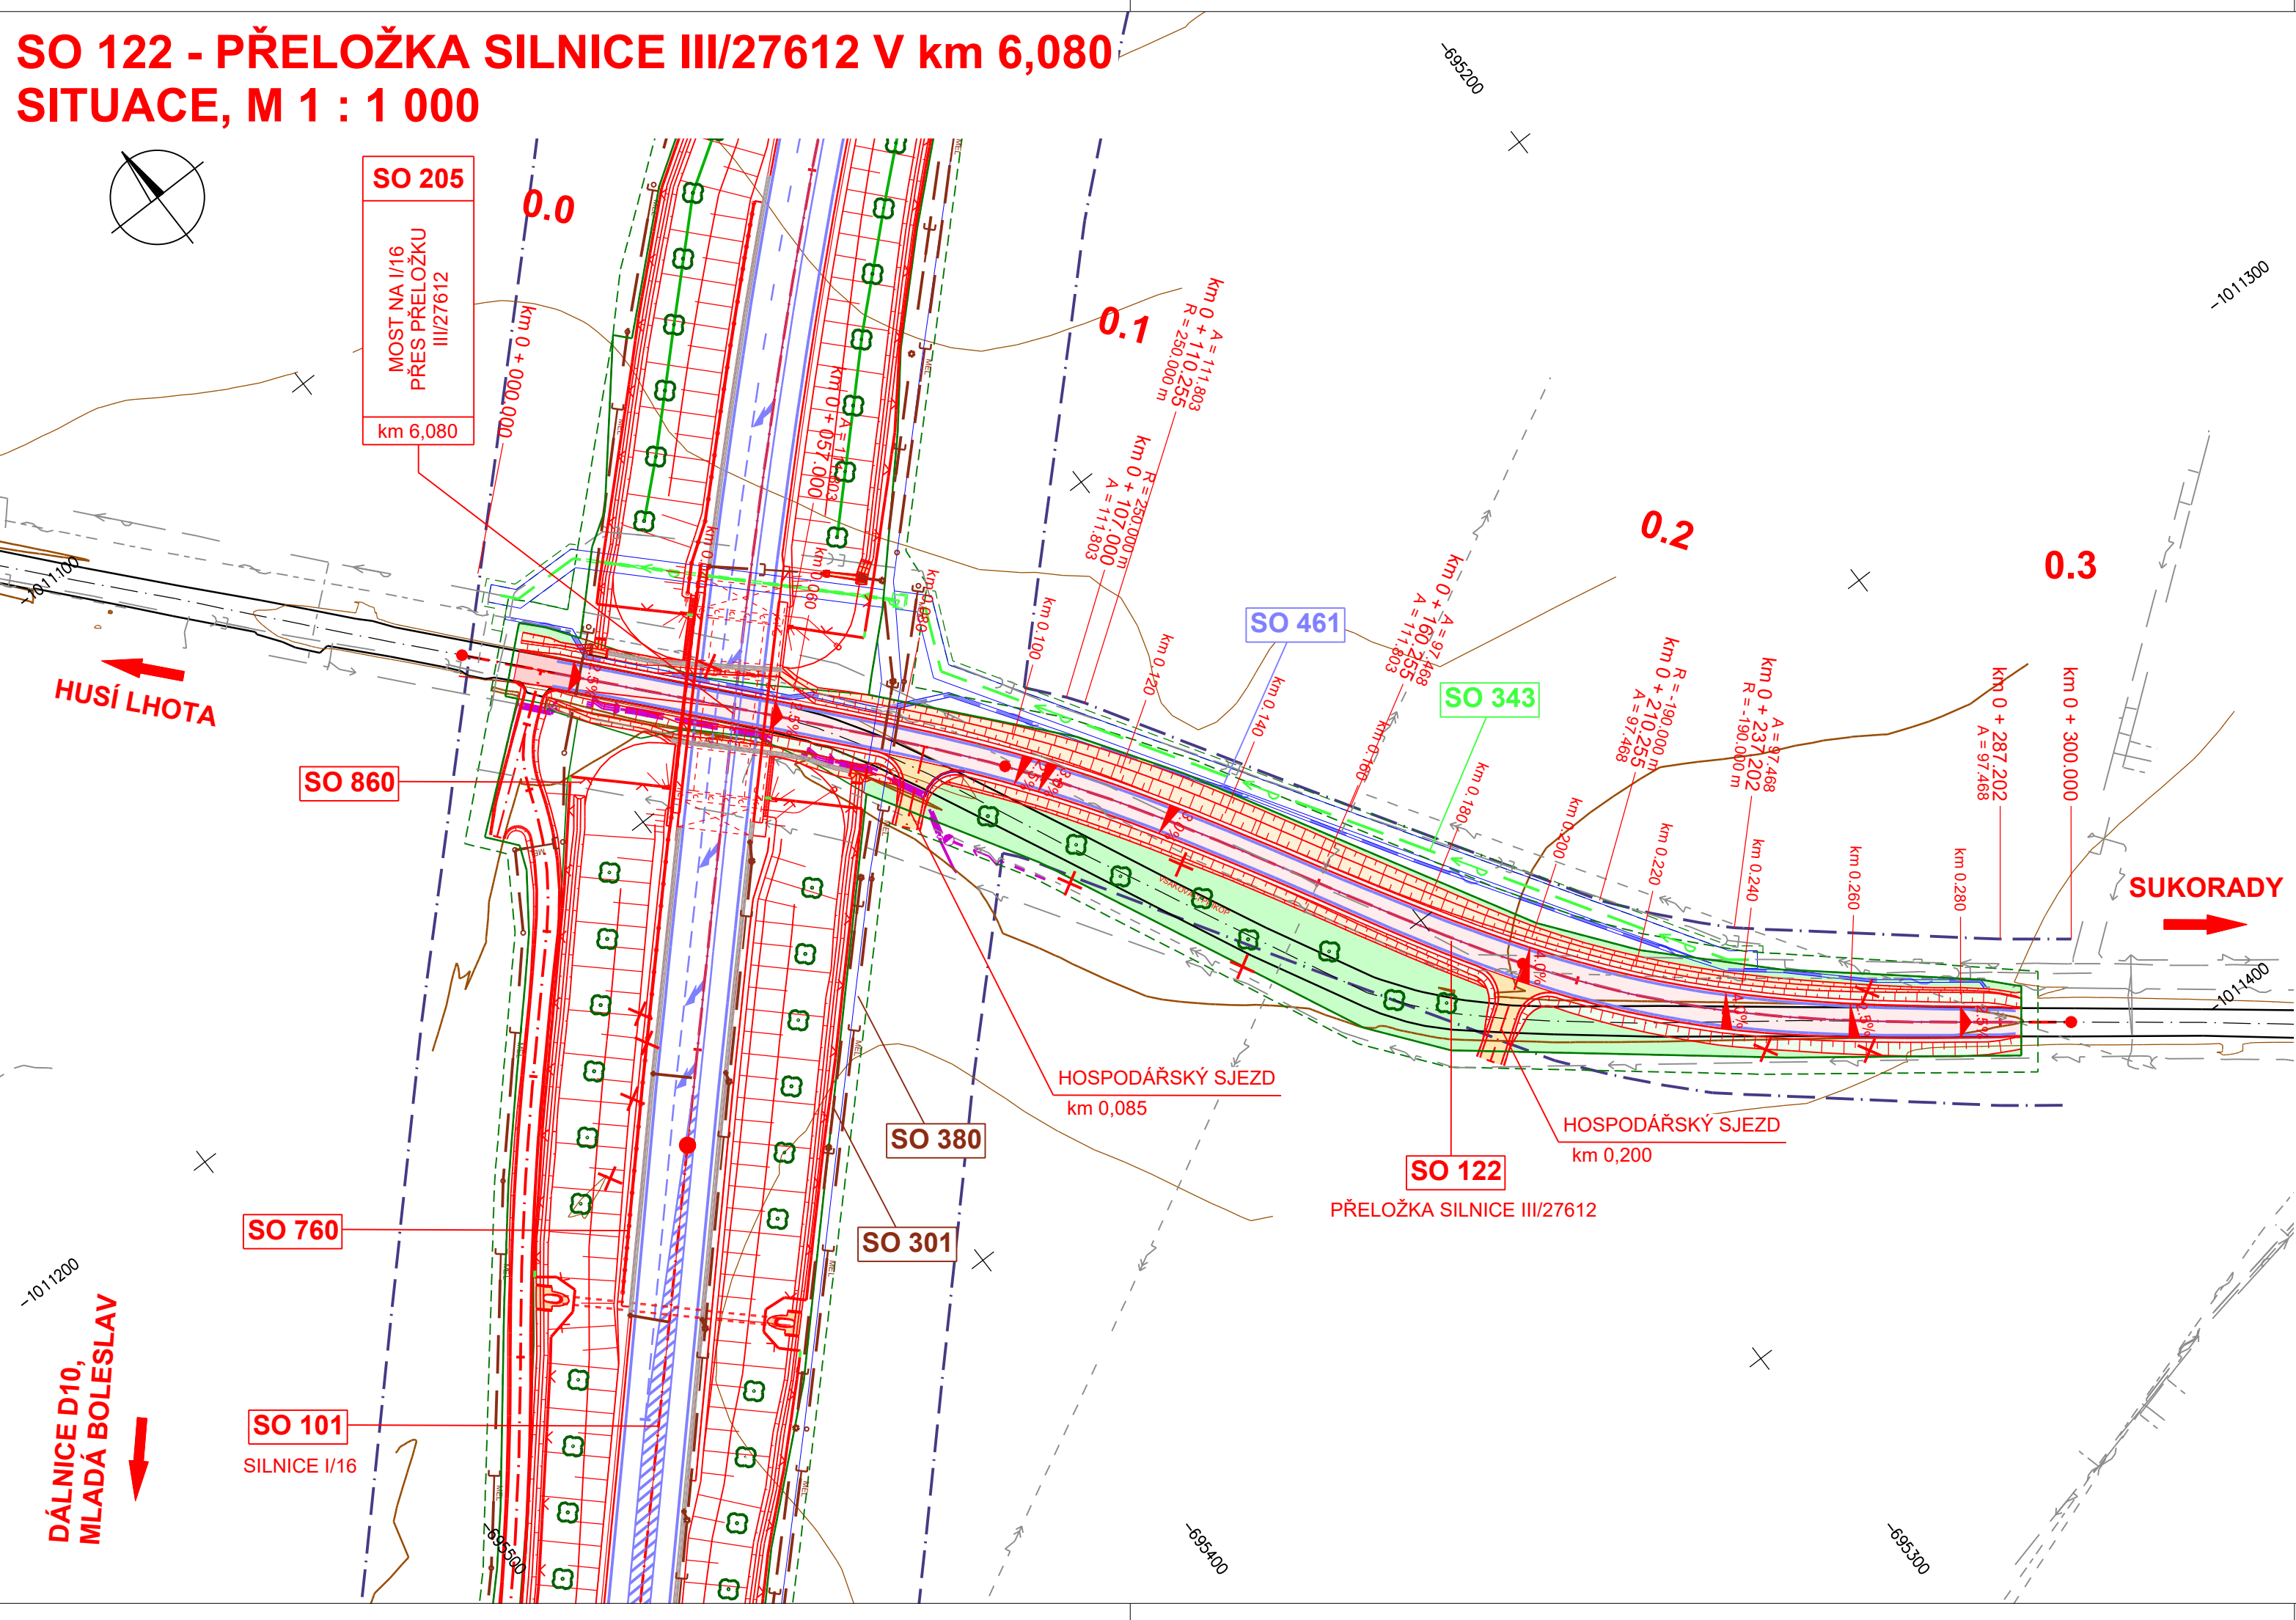

LEGENDA:

PLOCHY

- VOZOVKA - ASFALTOVÝ KRYT
- VOZOVKA - FRÉZOVANÁ
- VOZOVKA - POLNÍ CESTY
- CHODNÍK
- DLAŽBA VOZOVKY
- SVAHY VÝKOPU
- SVAHY NÁSYPU
- VEGETAČNÍ ÚPRAVY

OBVOD STAVBY

- TRVALÝ ZÁBOR
- DOČASNÝ ZÁBOR

NOVÉ IS

- DEŠŤOVÁ KANALIZACE
- MELIORACE
- VÝTLAK
- VODOVOD
- NADZEMNÍ VEDENÍ NN
- NADZEMNÍ VEDENÍ VN
- PODZEMNÍ VEDENÍ NN
- PODZEMNÍ SDĚLOVACÍ VEDENÍ
- PLYNOVOD - STL

STÁVAJÍCÍ IS - INFORMATIVNÍ ZÁKRES

- PODZEMNÍ VEDENÍ NN
- PODZEMNÍ VEDENÍ VN
- NADZEMNÍ VEDENÍ NN
- NADZEMNÍ VEDENÍ VN
- NADZEMNÍ VEDENÍ VVN
- DEŠŤOVÁ KANALIZACE
- PLYNOVOD - STL
- PODZEMNÍ SDĚLOVACÍ VEDENÍ
- VODOVOD

Souřadnicový systém: S-JSTK
Výškový systém Bpv

SO 122 Přeložka silnice III/27612 V km 6,080

Objednatel:



ŘEDITELSTVÍ
SILNIC
A DÁLNIC

Ředitelství silnic a dálnic s. p.
Čerčanská 2023/12, Krč, 140 00 Praha 4

Zhotovitel:



Valbek, spol. s r.o.
Vaňurova 505/17
460 07 Liberec 3

HIP:

ING. T. KLIMENT



Vypracoval
Zodp. projektant
Tech. kontrola

ING. A. DUMANSKA
ING. T. KLIMENT
ING. M. HANŽL

Akce
I/16 MLADÁ BOLESLAV - MARTINOVICE

Příloha
SITUACE

Zak. číslo
Datum
Stupeň
Počet formátů
Měřítko
Č. přílohy

21-LI13-001
02/2025
PDPS
3 x A4
1 : 1 000
Paré

Zhotovitel:
Valbek, spol. s r.o.
Vaňurova 505/17
460 07 Liberec 3

2