
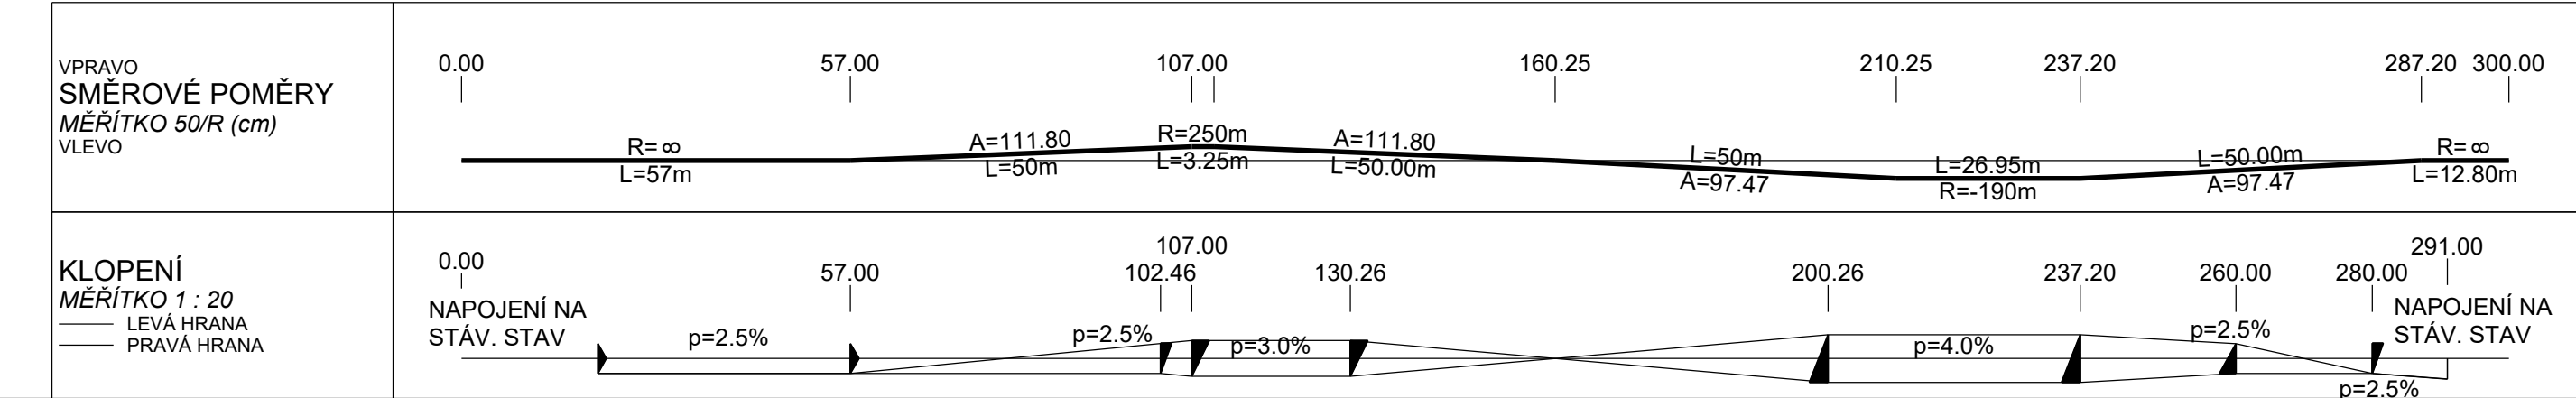


SO 122 - PŘELOŽKA SILNICE III/27612 V km 6,080
PODÉLNÝ PROFIL, M 1 : 1 000 / 100

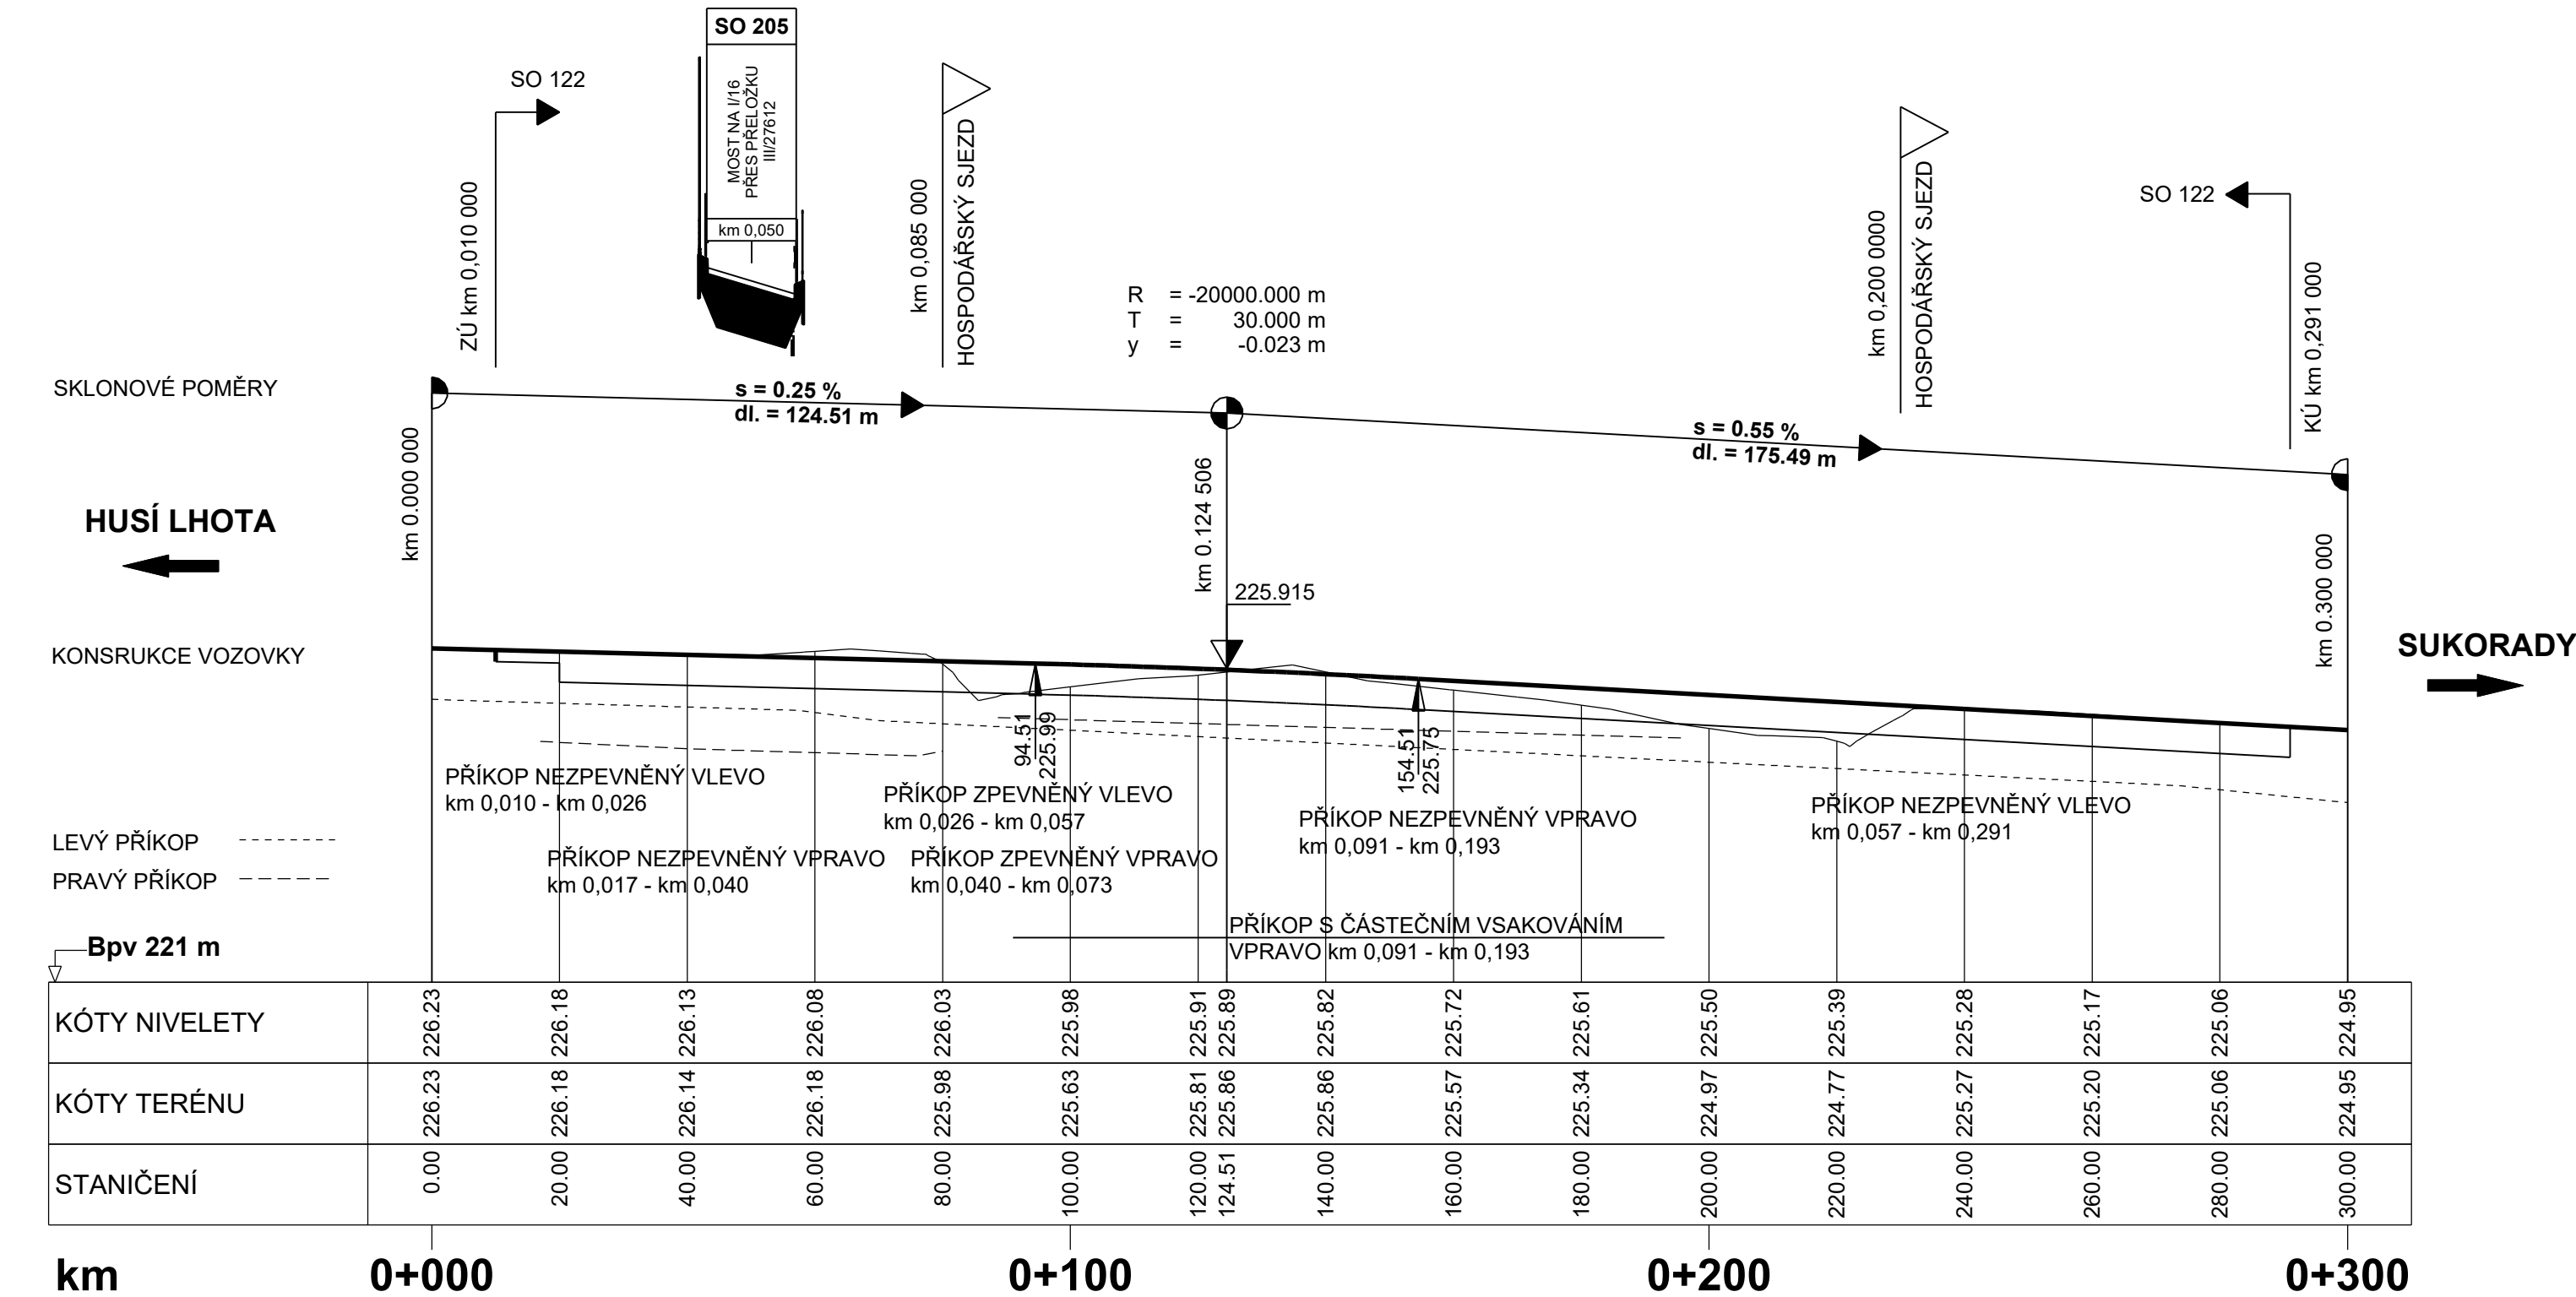

Výškový systém Bpv

SO 122 Přeložka silnice III/27612 v km 6,080

Objednatel:



ŘEDITELSTVÍ
SILNIC
A DÁLNIC

Ředitelství silnic a dálnic s. p.

Čerčanská 2023/12, Krč, 140 00 Praha 4

Zhotovitel:



Valbek, spol. s r.o.

Vaňurova 505/17
460 07 Liberec 3

HIP:

ING. T. KLIMENT



Vypracoval ING. A. DUMANSKA

Zodp. projektant ING. T. KLIMENT

Tech. kontrola ING. M. HANŽL

Akce

I/16 MLADÁ BOLESLAV - MARTINOVICE

Zhotovitel:

Valbek, spol. s r.o.
Vaňurova 505/17
460 07 Liberec 3

Příloha

PODÉLNÝ PROFIL

Zak. číslo 21-LI13-001

Datum 02/2025

Stupeň PDPS

Počet formátů 3 x A4

Měřítko 1 : 1 000 / 100

Č. přílohy Paré

3