



SO 122 - PŘELOŽKA SILNICE III/27612 V km 6,080
VZOROVÉ PŘÍČNÉ ŘEZY, M 1:50

NÁVRHOVÁ KATEGORIE S 6,5/50

TŘÍDA DOPRAVNÍHO ZATÍŽENÍ IV
NÁVRHOVÁ ÚROVEŇ PORUŠENÍ D1
TYP PODLOŽÍ PIII (D1-A-2)

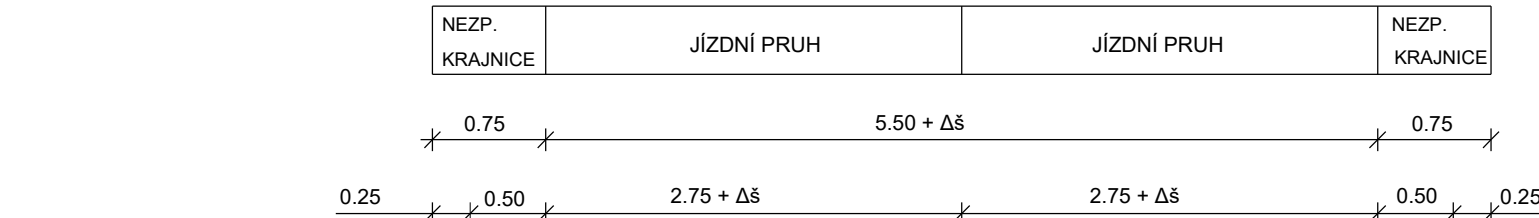


HUSÍ LHOTA SUKORADY

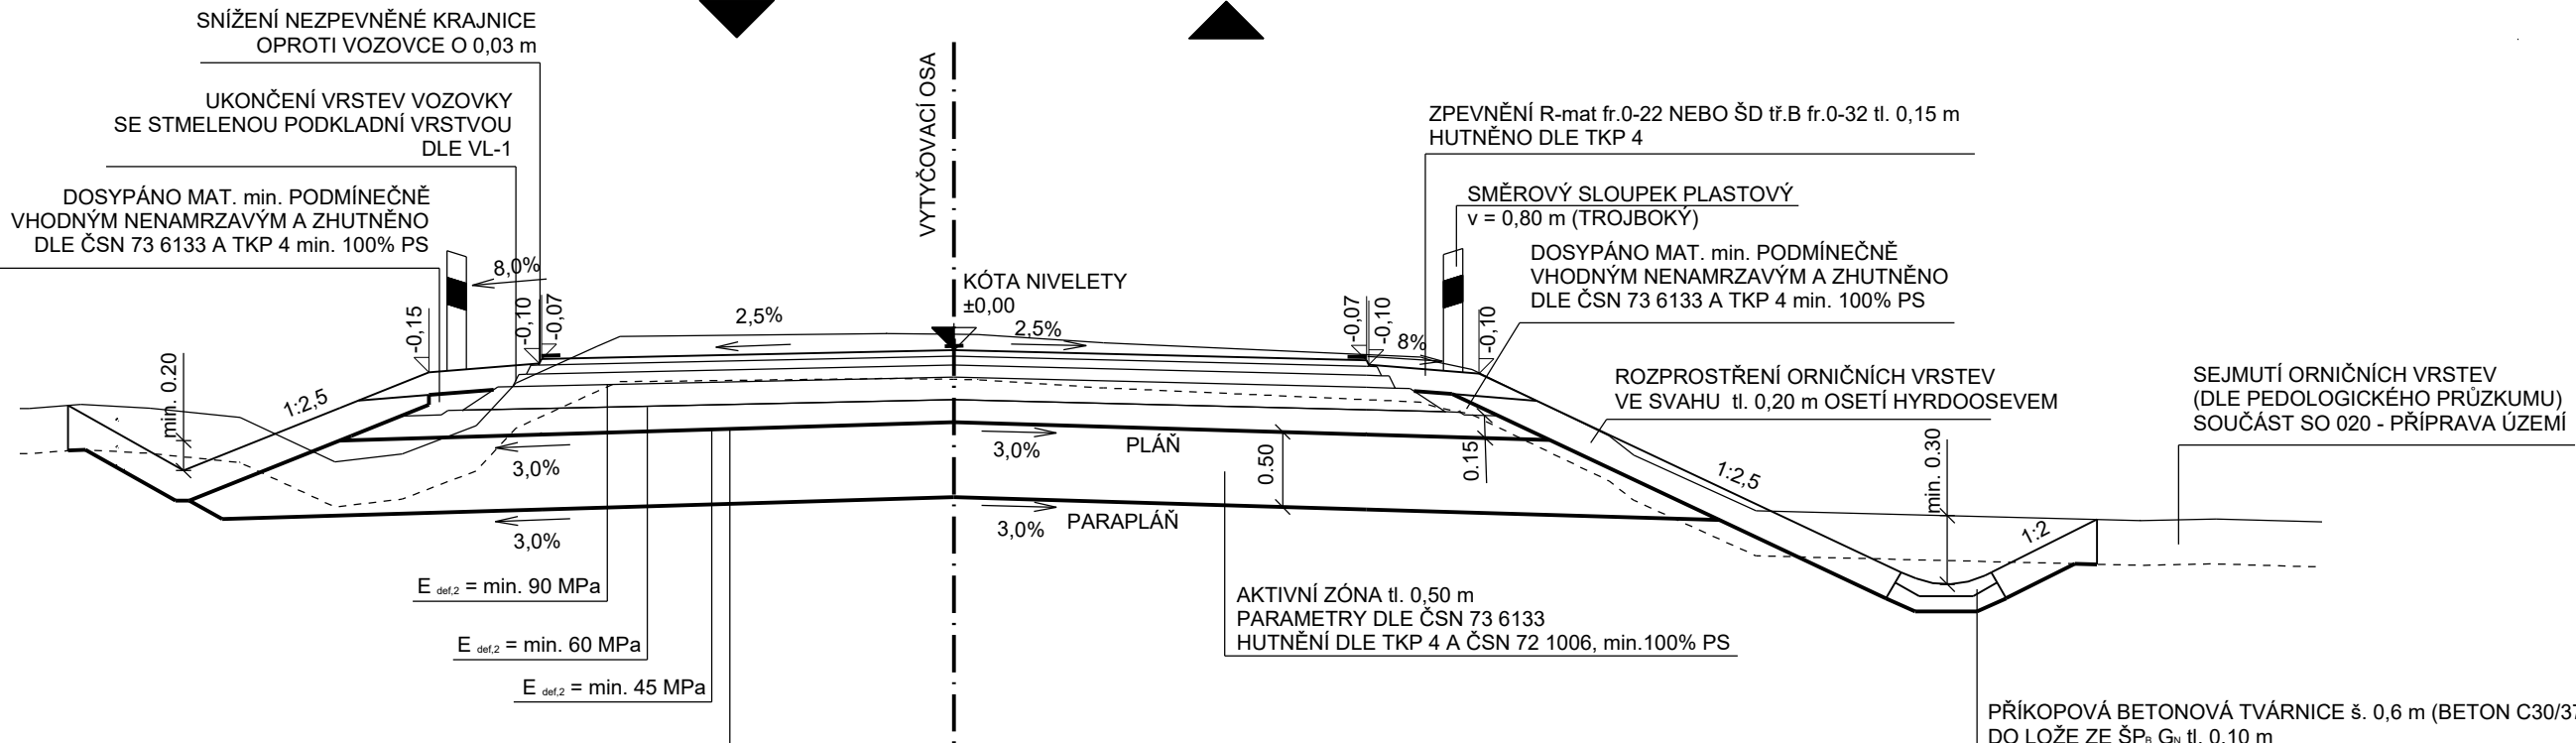

ASFALTOVÝ BETON PRO OBROUSNOU VRSTVU ASFALT 50/70 SPOJOVACÍ POSTŘÍK EMULZNÍ STŘEDNĚŠTĚPNÝ	ACO 11	40 mm	ČSN EN 13 108-1, ČSN 73 6121
ASFALTOVÝ BETON PRO LOŽNÍ VRSTVU ASFALT 50/70 POSTŘÍK EMULZNÍ STŘEDNĚŠTĚPNÝ	PS-C	0,35 kg/m²	ČSN EN 13 808, ČSN 73 6129, ČSN 73 6132
ASFALTOVÝ BETON PRO PODKLADNÍ VRSTVU ASFALT 50/70 INFILTRAČNÍ POSTŘÍK EMULZNÍ VČETNĚ PODRCENÍ KAMENIVEM fr. 2/4 V MNOŽSTVÍ 3,0 kg/m²	PI-C	1,00 kg/m²	ČSN 73 6129
ŠTĚRKODRT' tř. A, (0/32 GE)	ŠD _a	150 mm	ČSN EN 13 285, ČSN 73 6126-1
ŠTĚRKODRT' tř. A, (0/32 GE)	ŠD _a	min. 150 mm	ČSN EN 13 285, ČSN 73 6126-1
CELKEM		min. 480 mm	

HOSPODÁŘSKÝ SJEZD


TŘÍDA DOPRAVNÍHO ZATÍŽENÍ VI
NÁVRHOVÁ ÚROVEŇ PORUŠENÍ D2
TYP PODLOŽÍ PIII (D2-N-1)

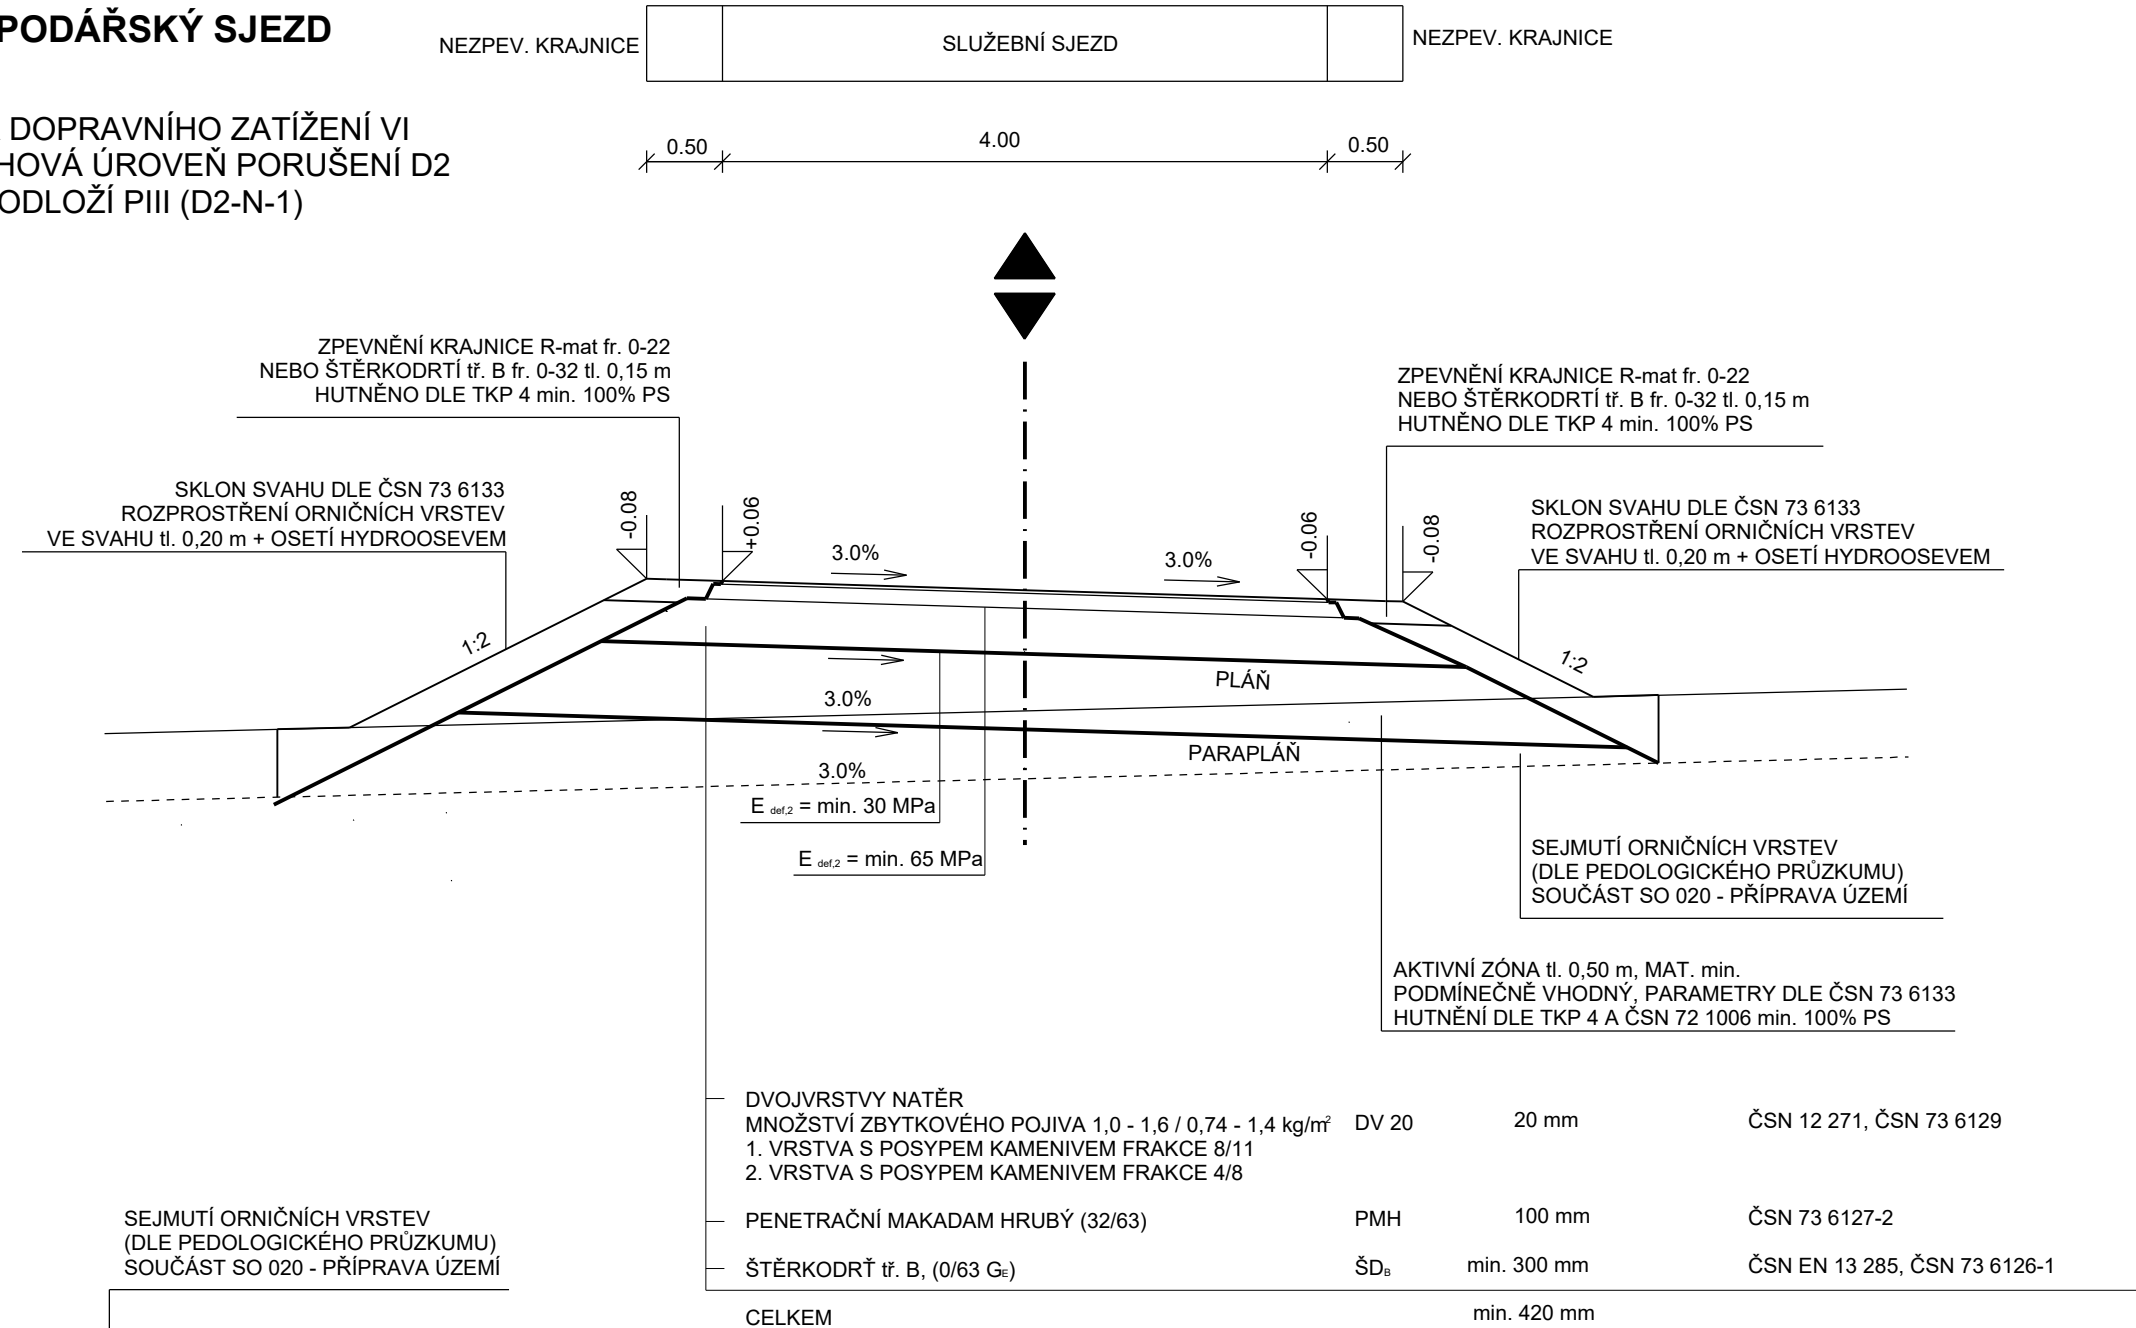


DETAIL PŘÍKOPU V MÍSTĚ VSAKOVÁNÍ

POZNÁMKA:


ROZSAH RETENČNÍHO PŘÍKOPU S ČÁSTEČNÝM
VSAKOVÁNÍM - VIZ TECHNICKÁ ZPRÁVA

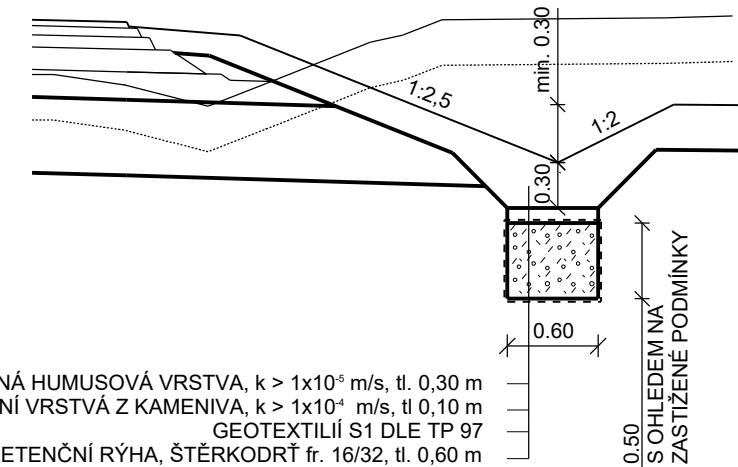

DETAIL NAPOJENÍ NOVÉ
KONSTRUKCE NA STÁVAJÍCÍ
V PŘÍČNÉM SMĚRU

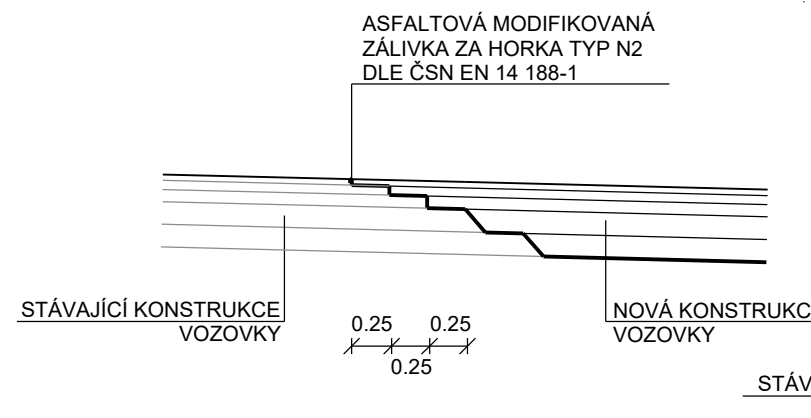

DETAIL NAPOJENÍ NOVÉ
KONSTRUKCE NA STÁVAJÍCÍ
V PODÉLNÉM SMĚRU

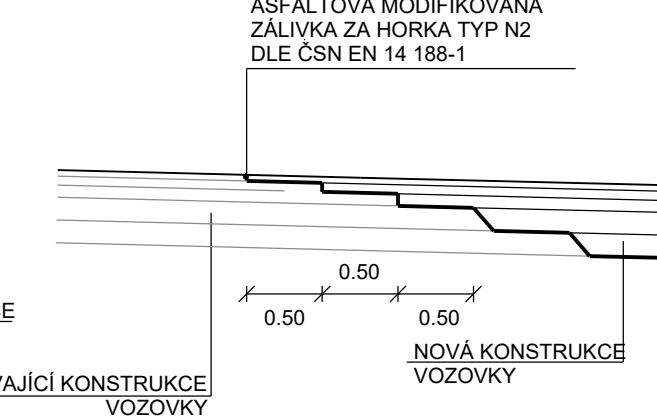

SO 122 Přeložka silnice III/27612 v km 6,080

Objednatel:



Ředitelství silnic a dálnic s. p.
Čerčanská 203/12, Krč, 140 00 Praha 4

Zhotovitel:



Valbek, spol. s r.o.
Vaňurova 505/17
460 07 Liberec 3

HIP:

ING. T. KLIMENT



Wypracoval	ING. A. DUMANSKA	Zak. číslo	21-L113-001
Zodp. projektant	ING. T. KLIMENT	Datum	02/2025
Tech. kontrola	ING. M. HANŽL	Stupeň	PDPS
Akce		Počet formátů	4 x A4
I/16 MLADÁ BOLESLAV - MARTINOVICE		Měřitko	1 : 50
Č. přílohy		Paré	
Příloha		VZOROVÉ PŘÍČNÉ ŘEZY	
Zhotovitel: Valbek, spol. s r.o. Vaňurova 505/17 460 07 Liberec 3		4	