
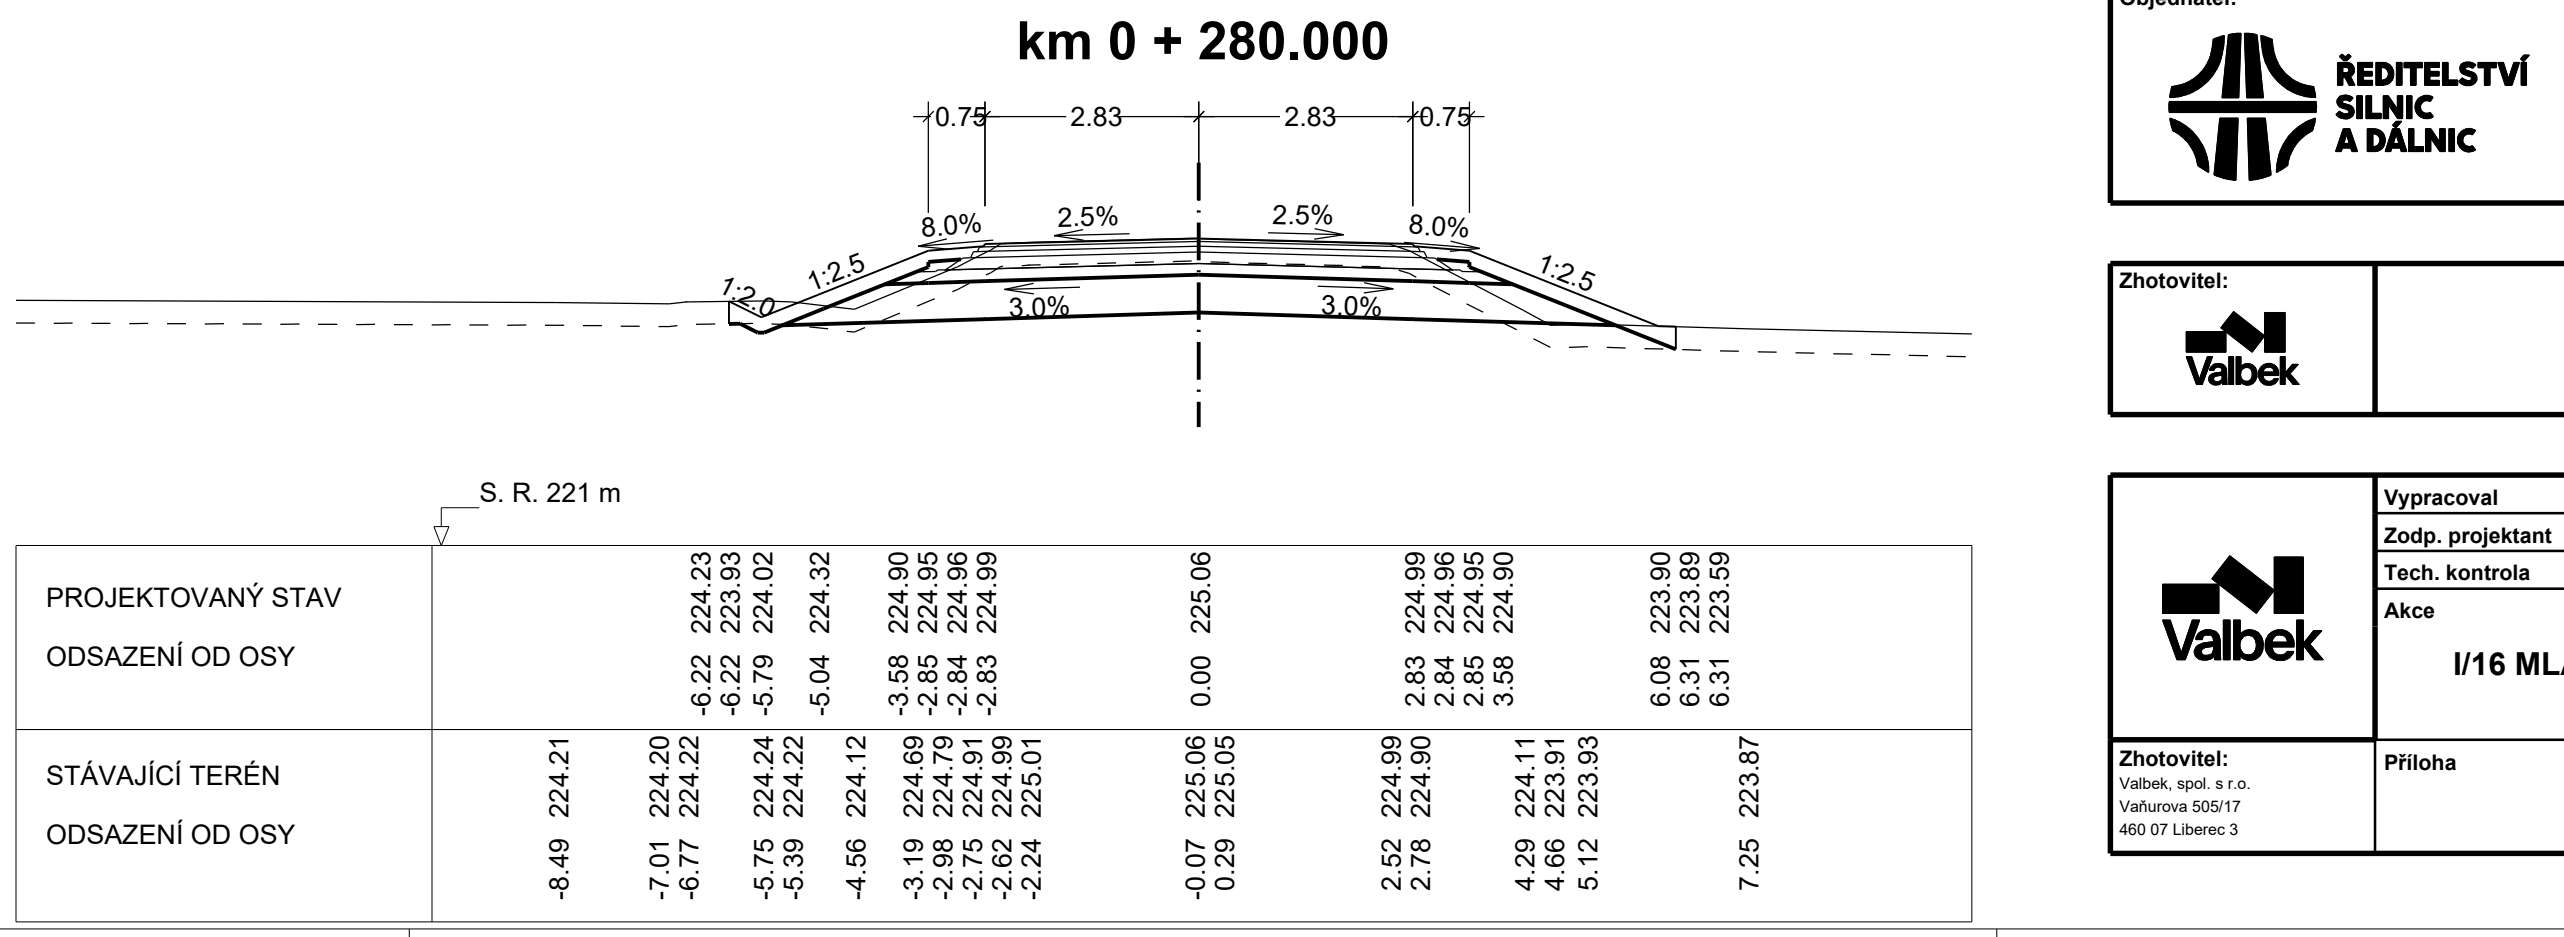
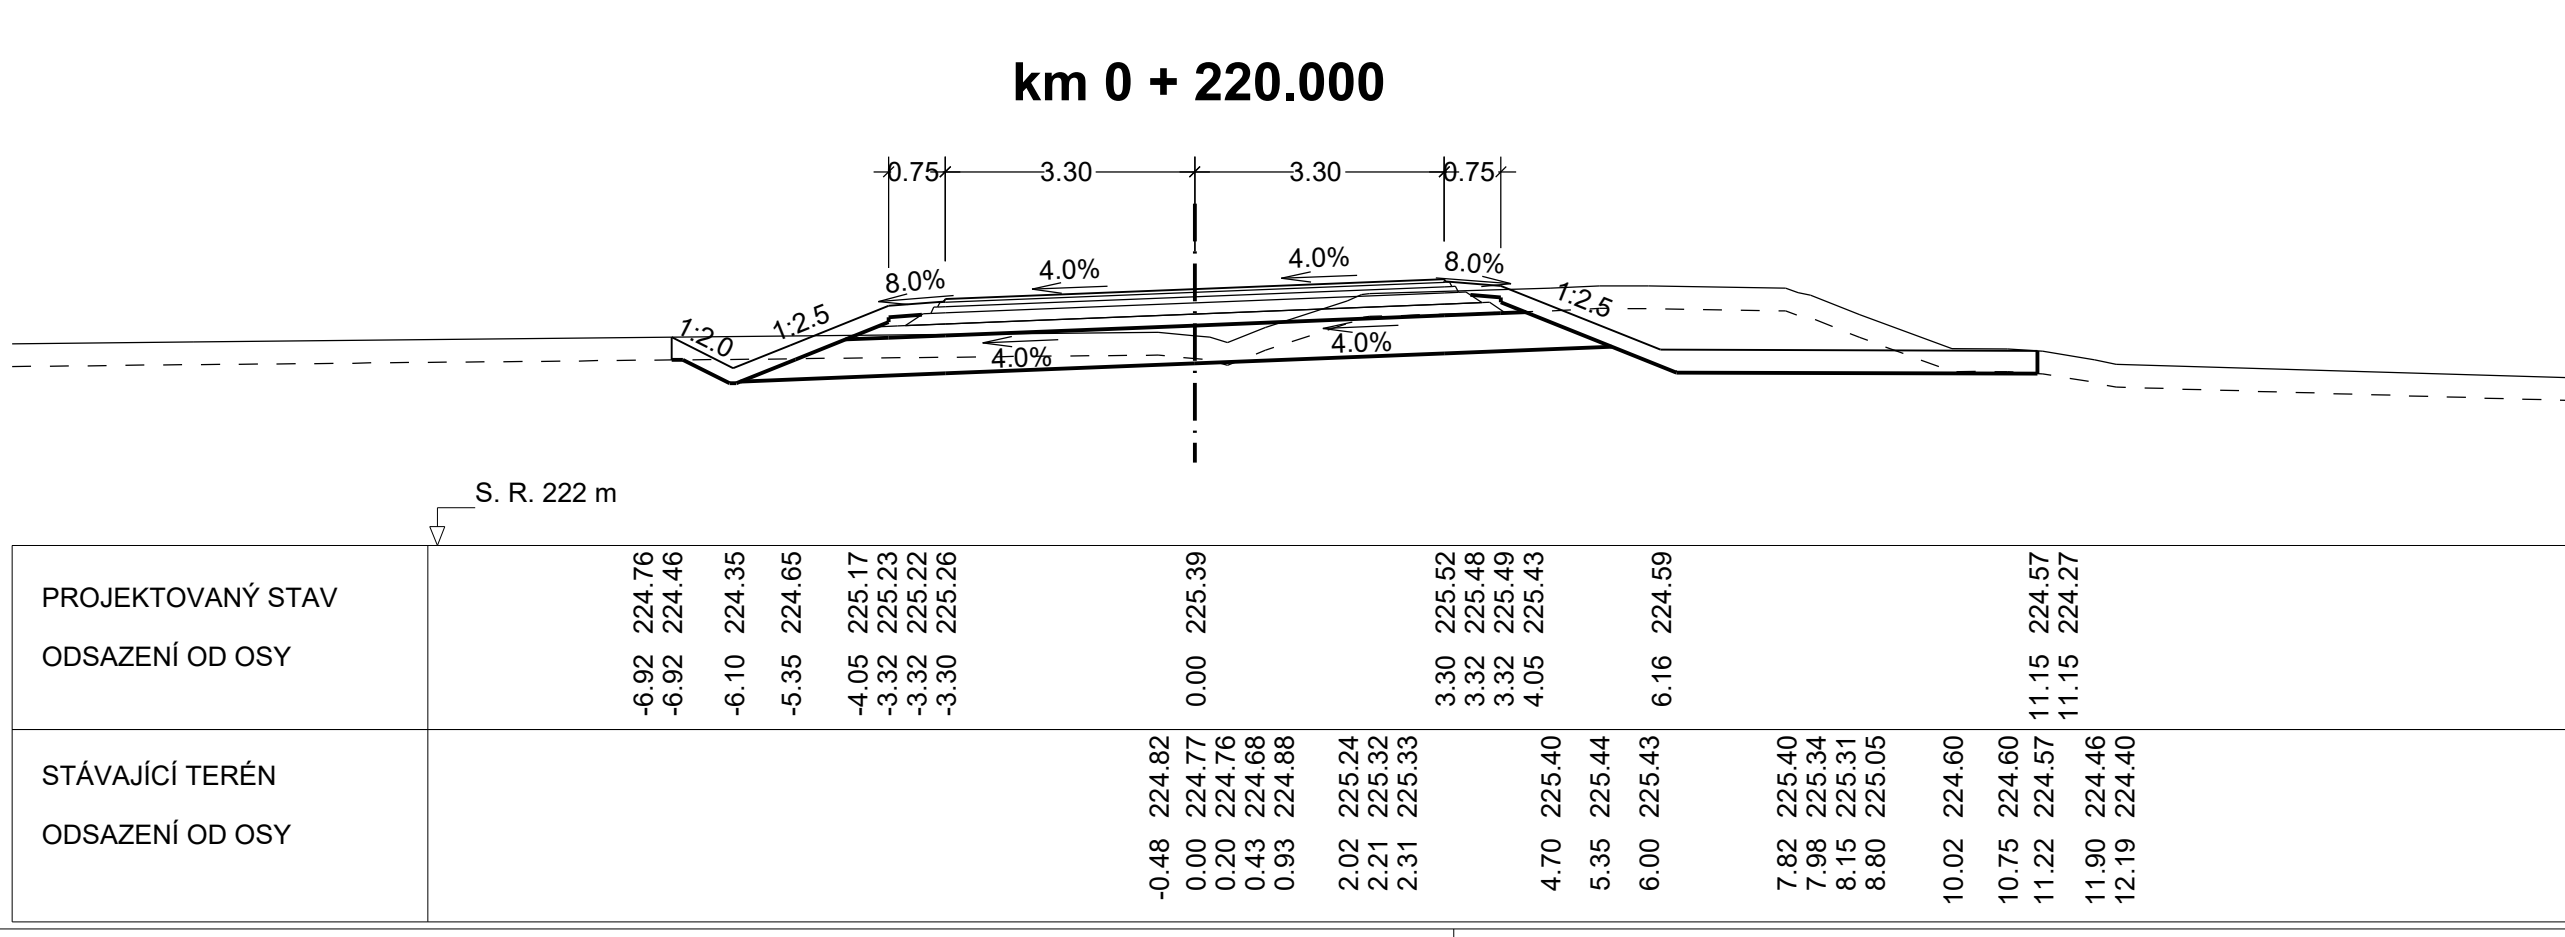
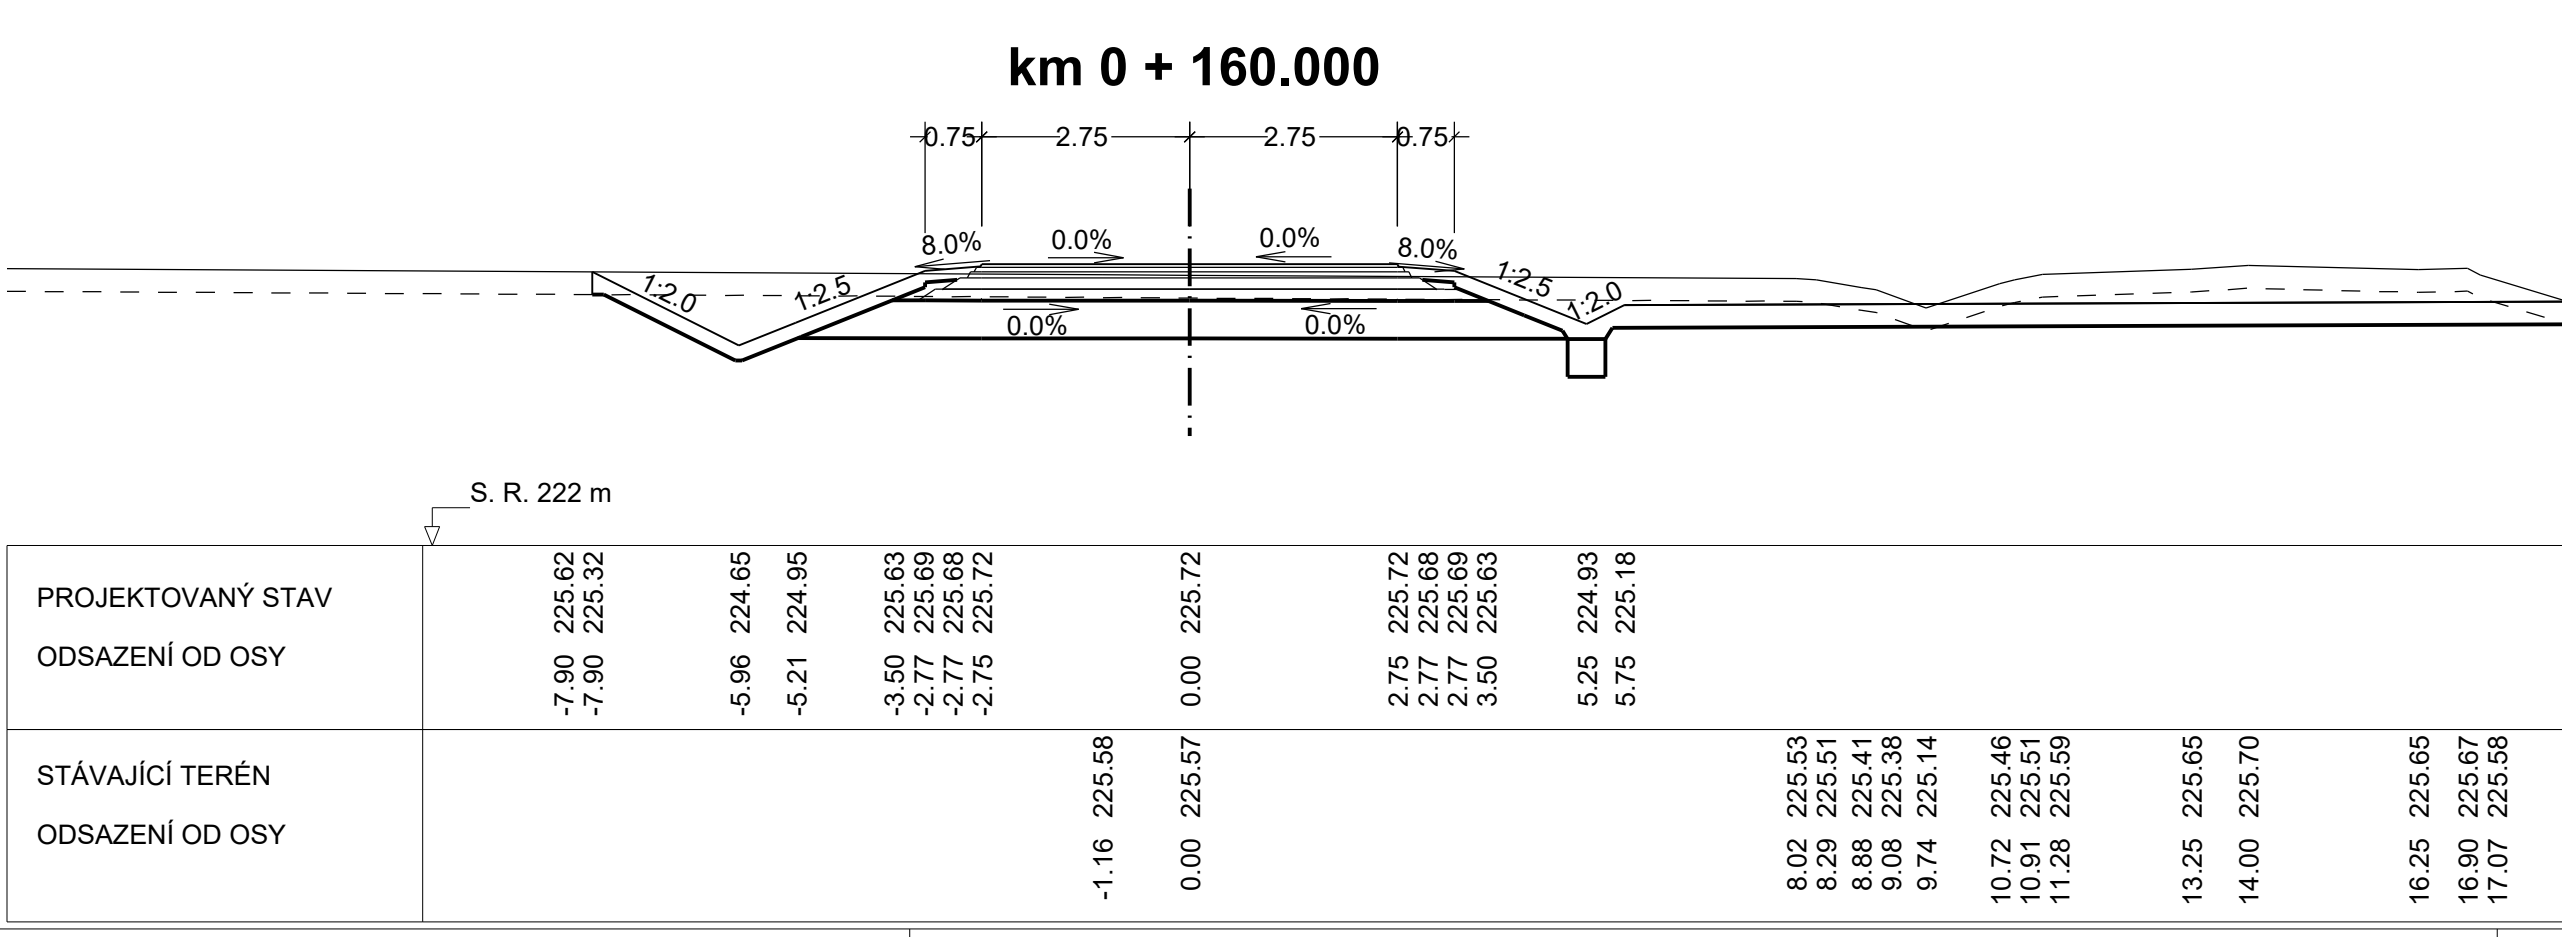
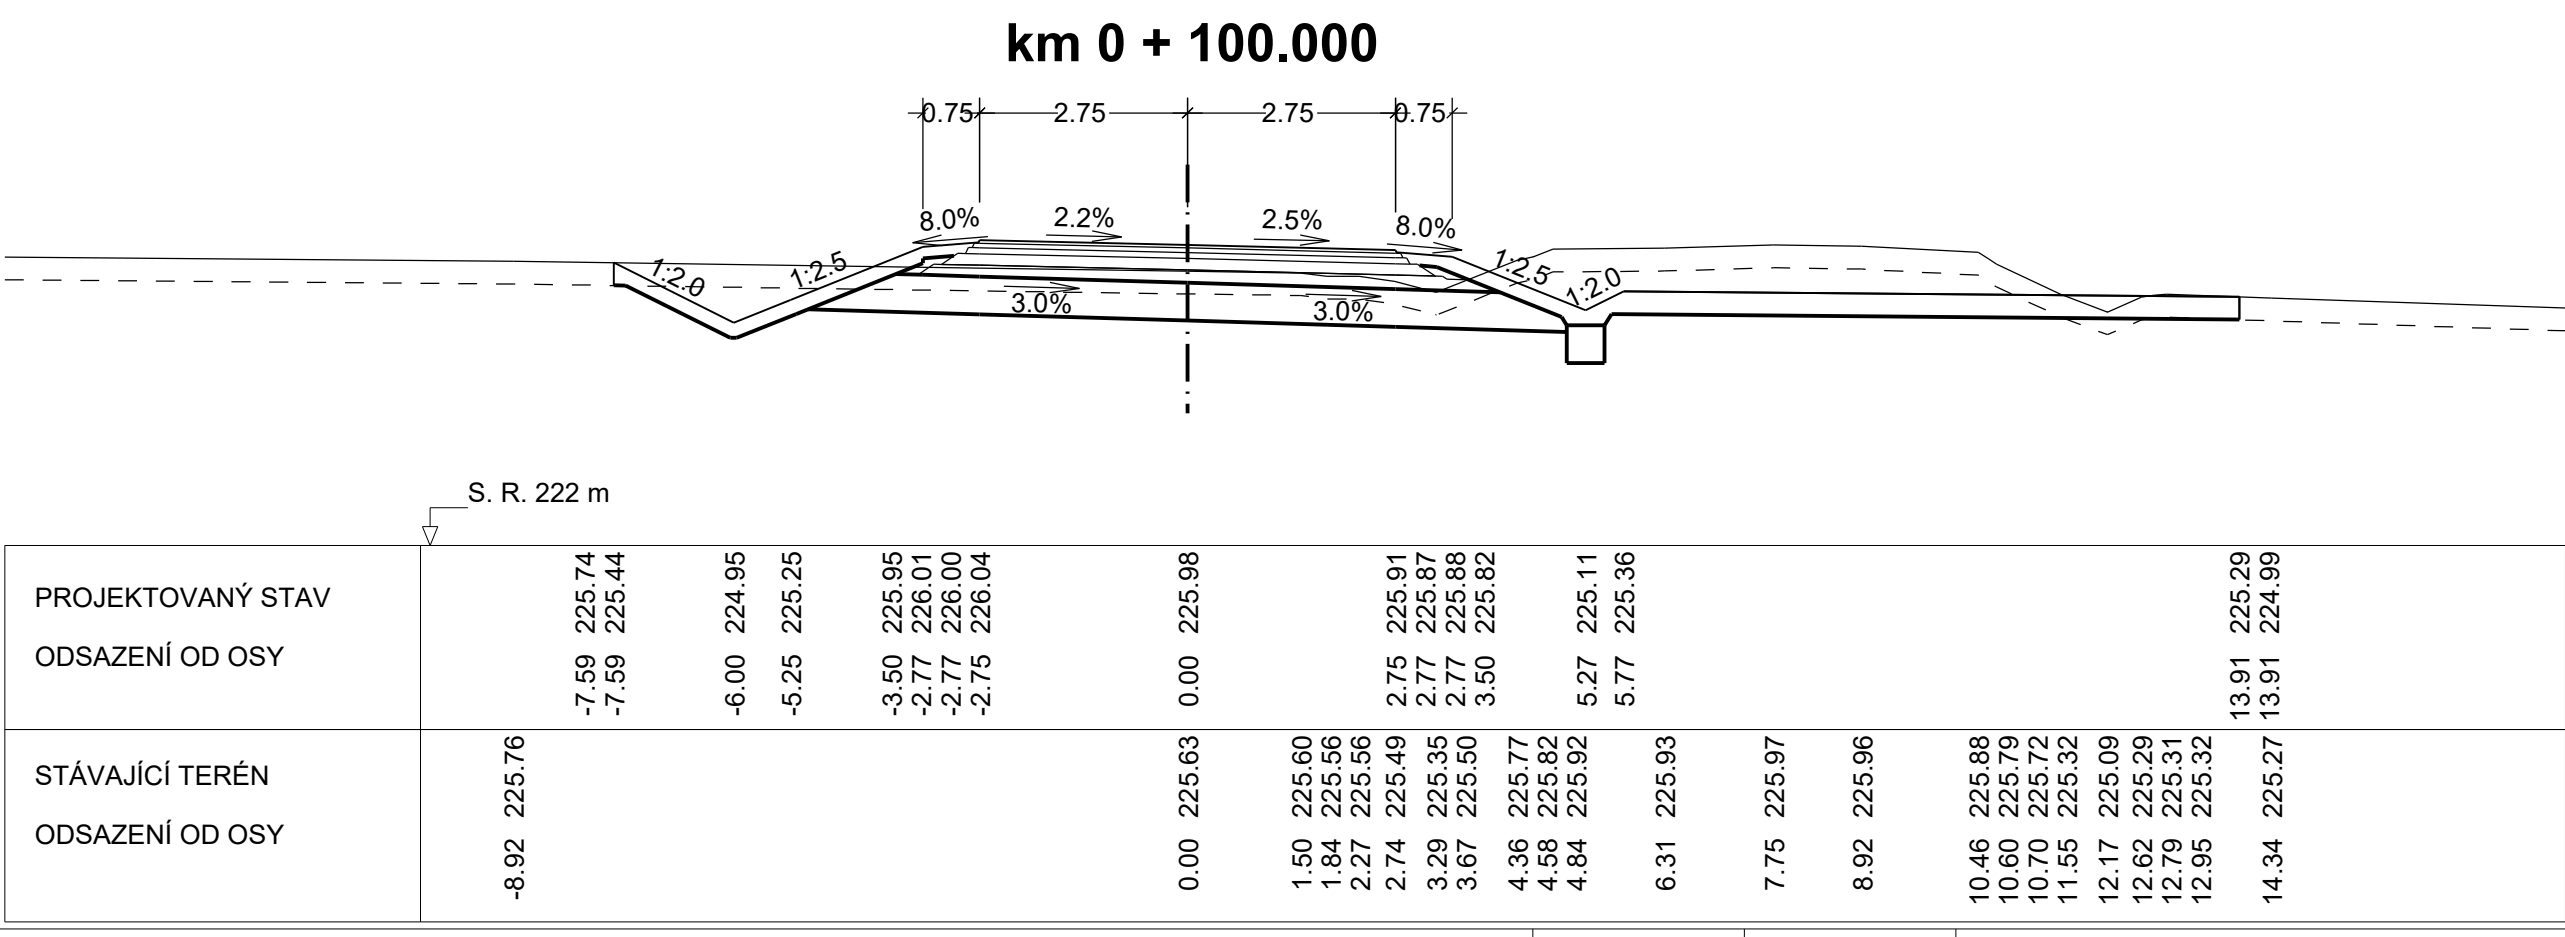
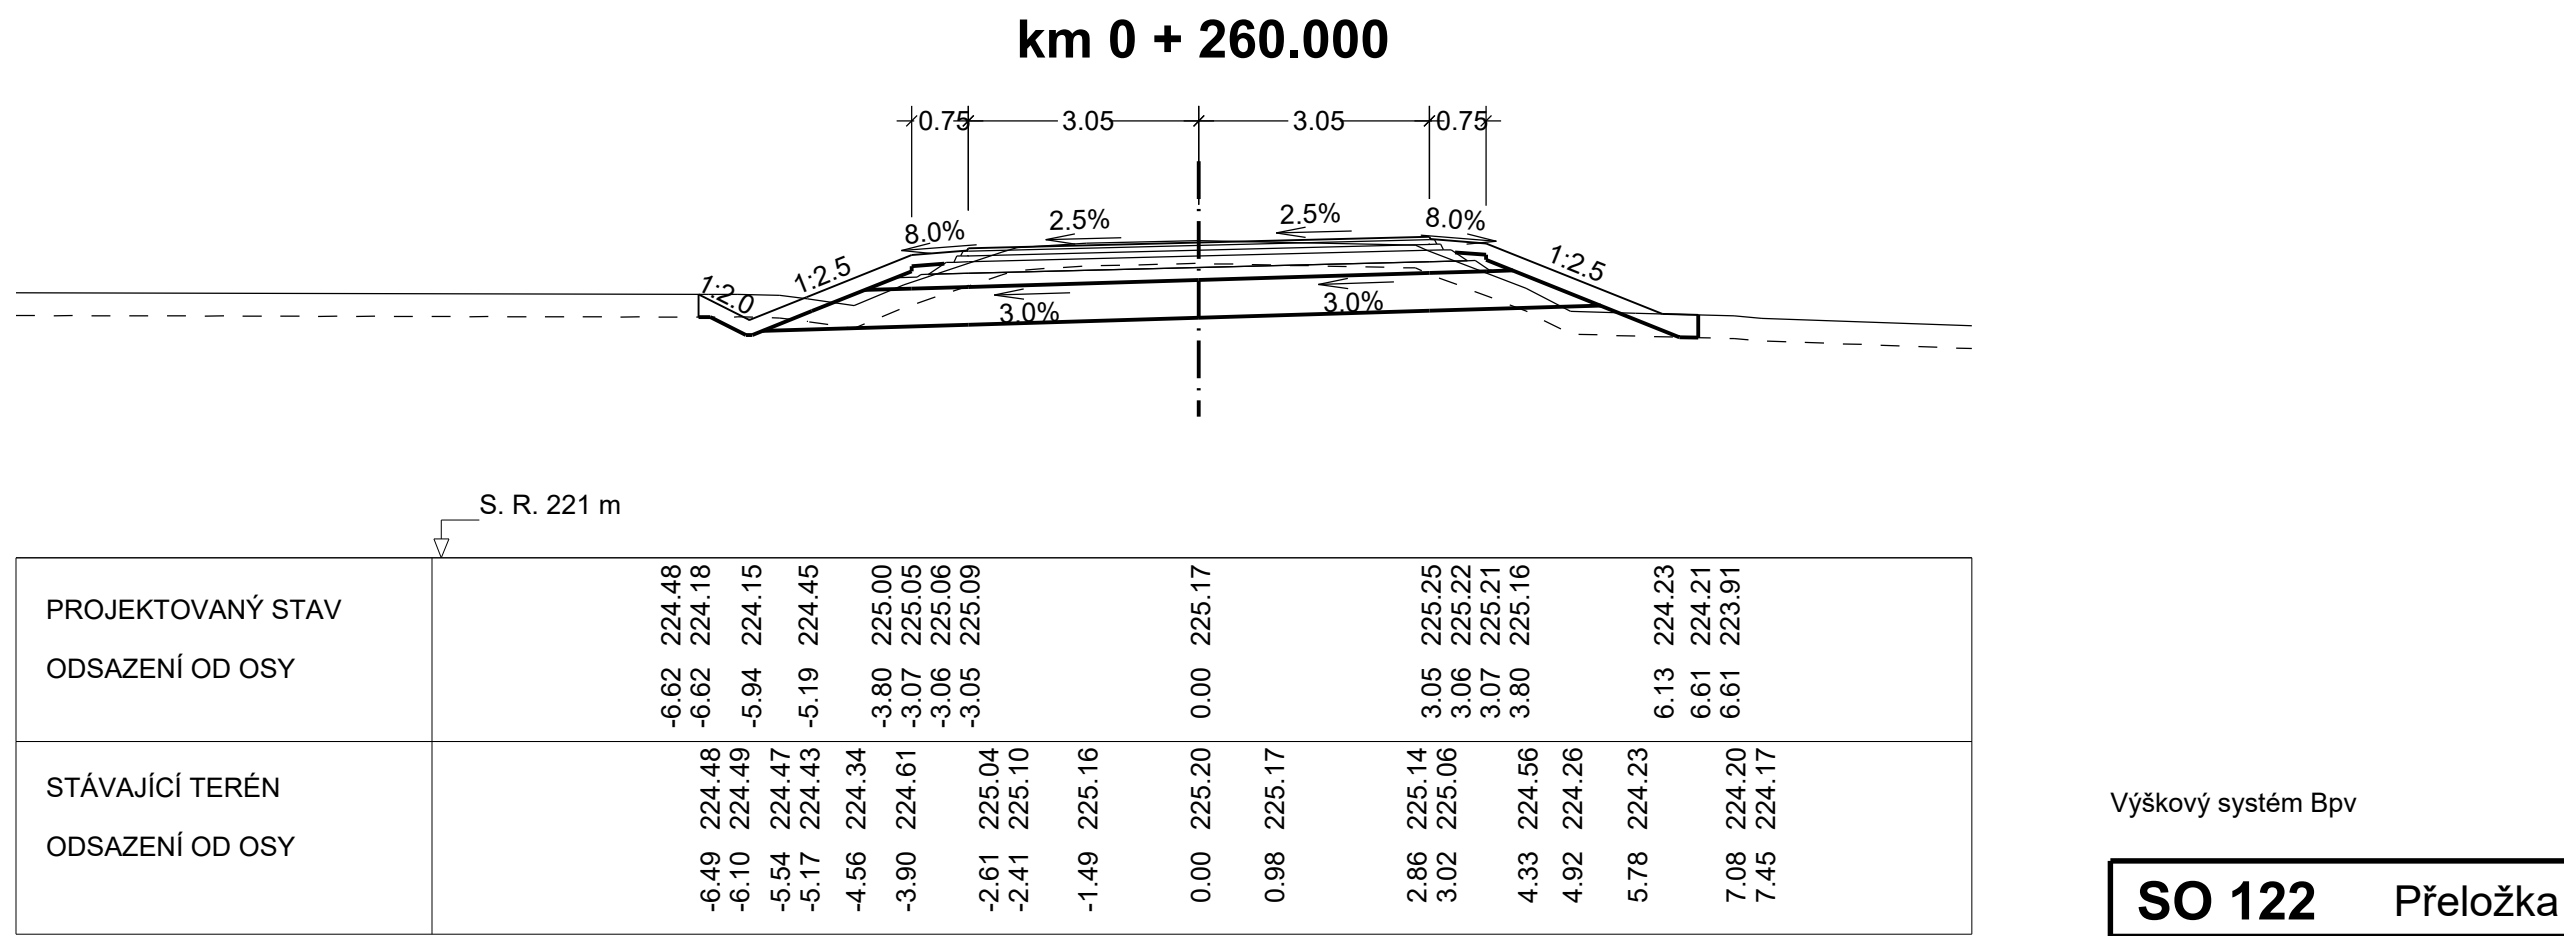
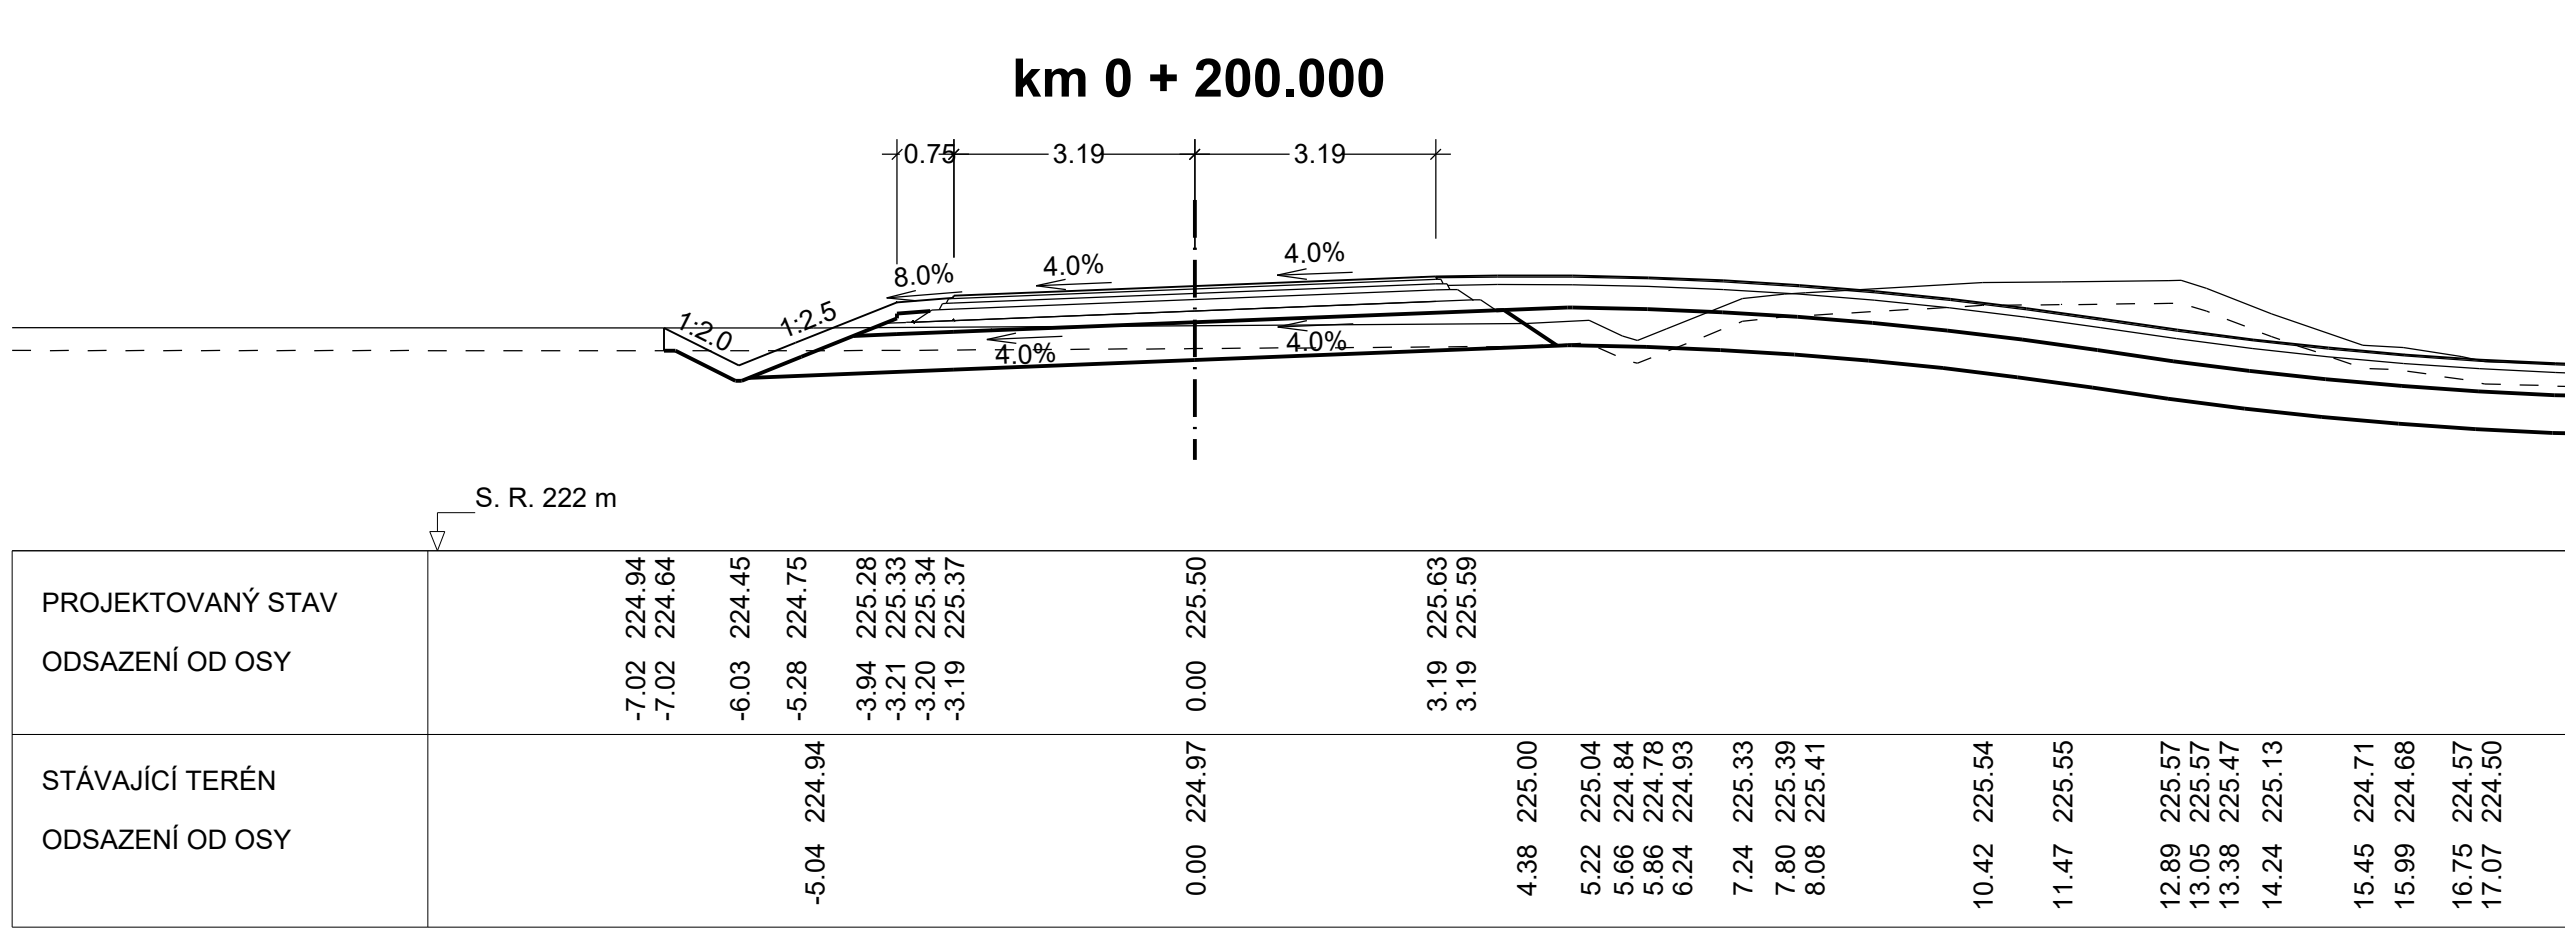
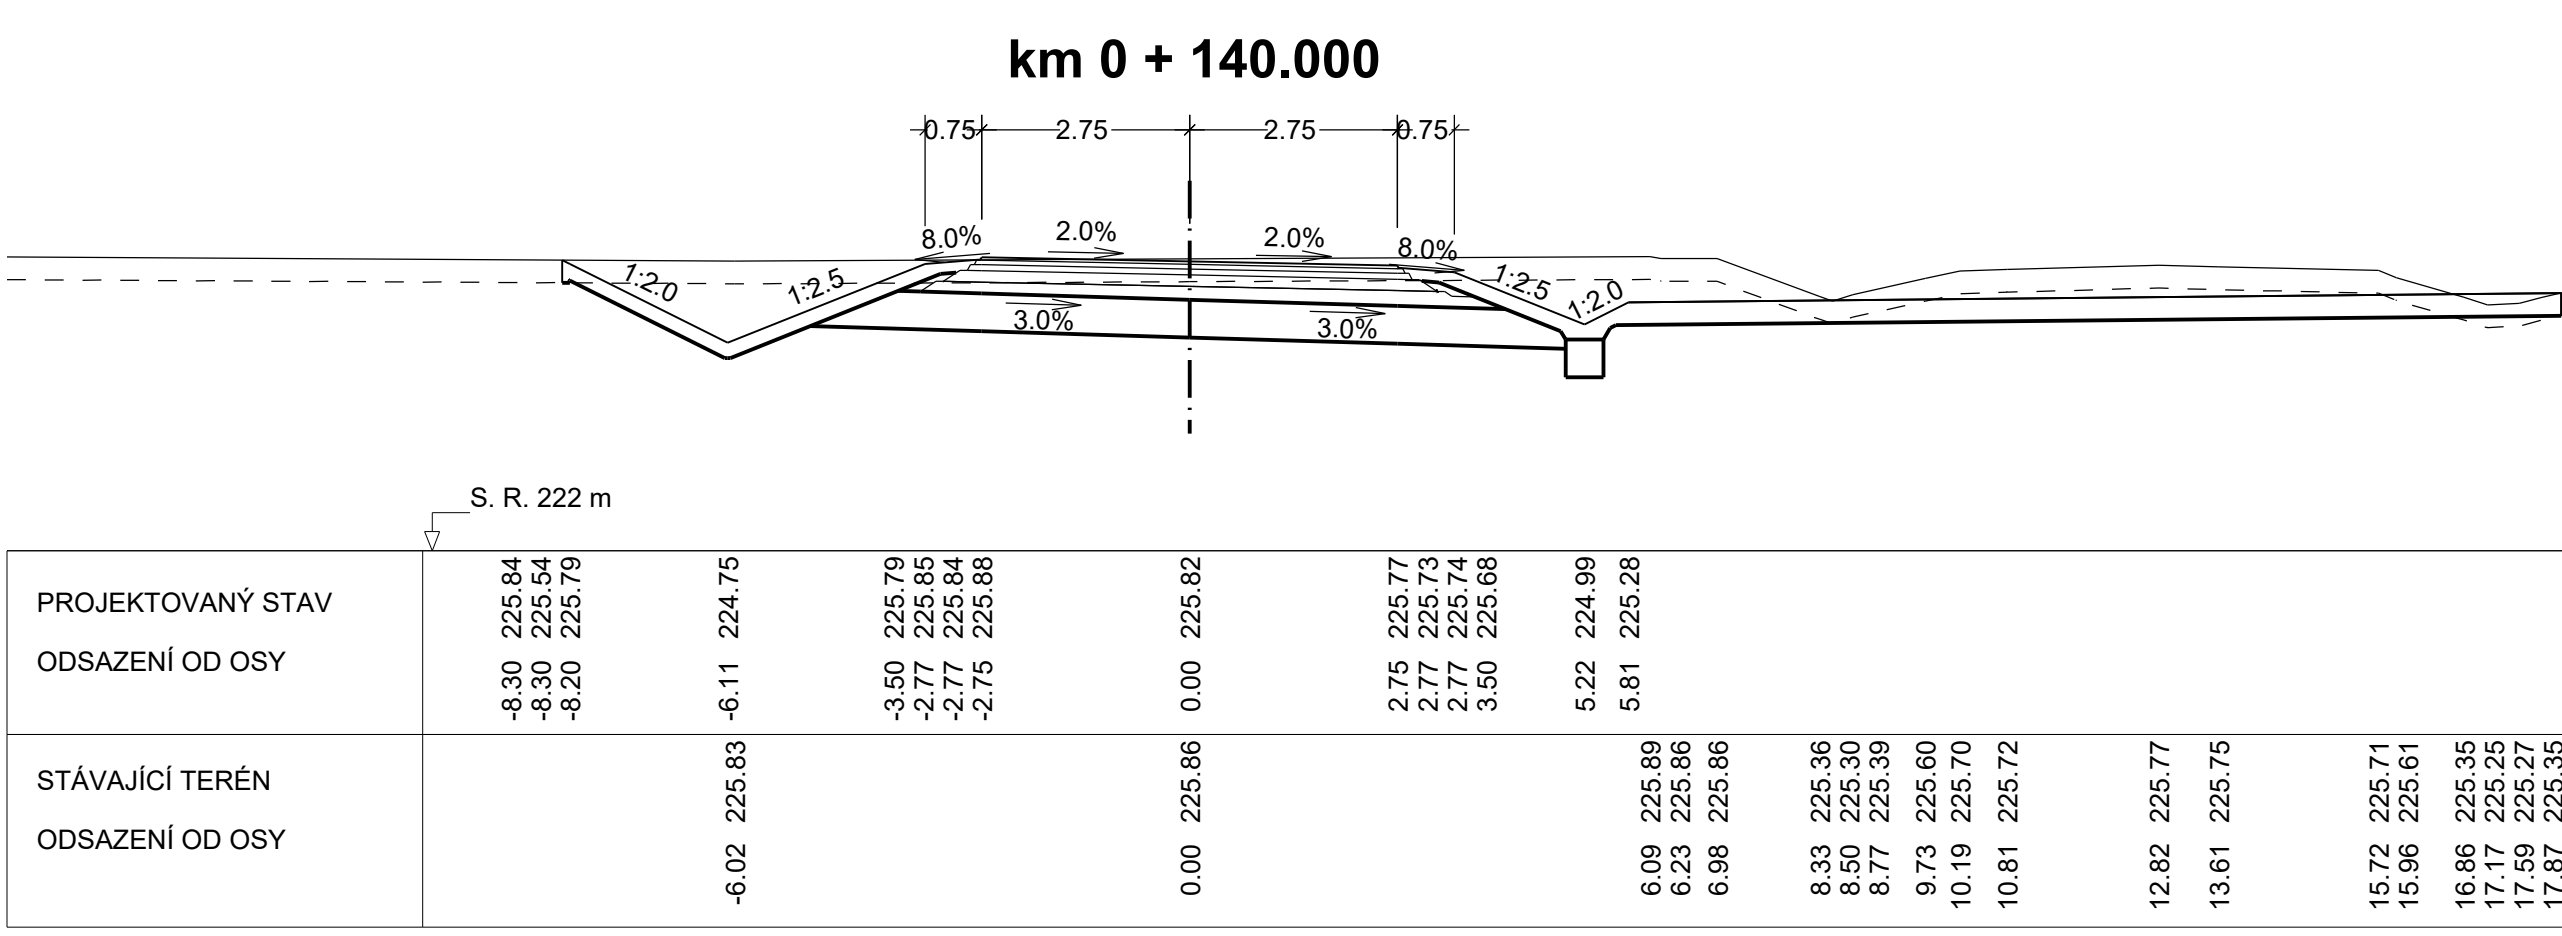
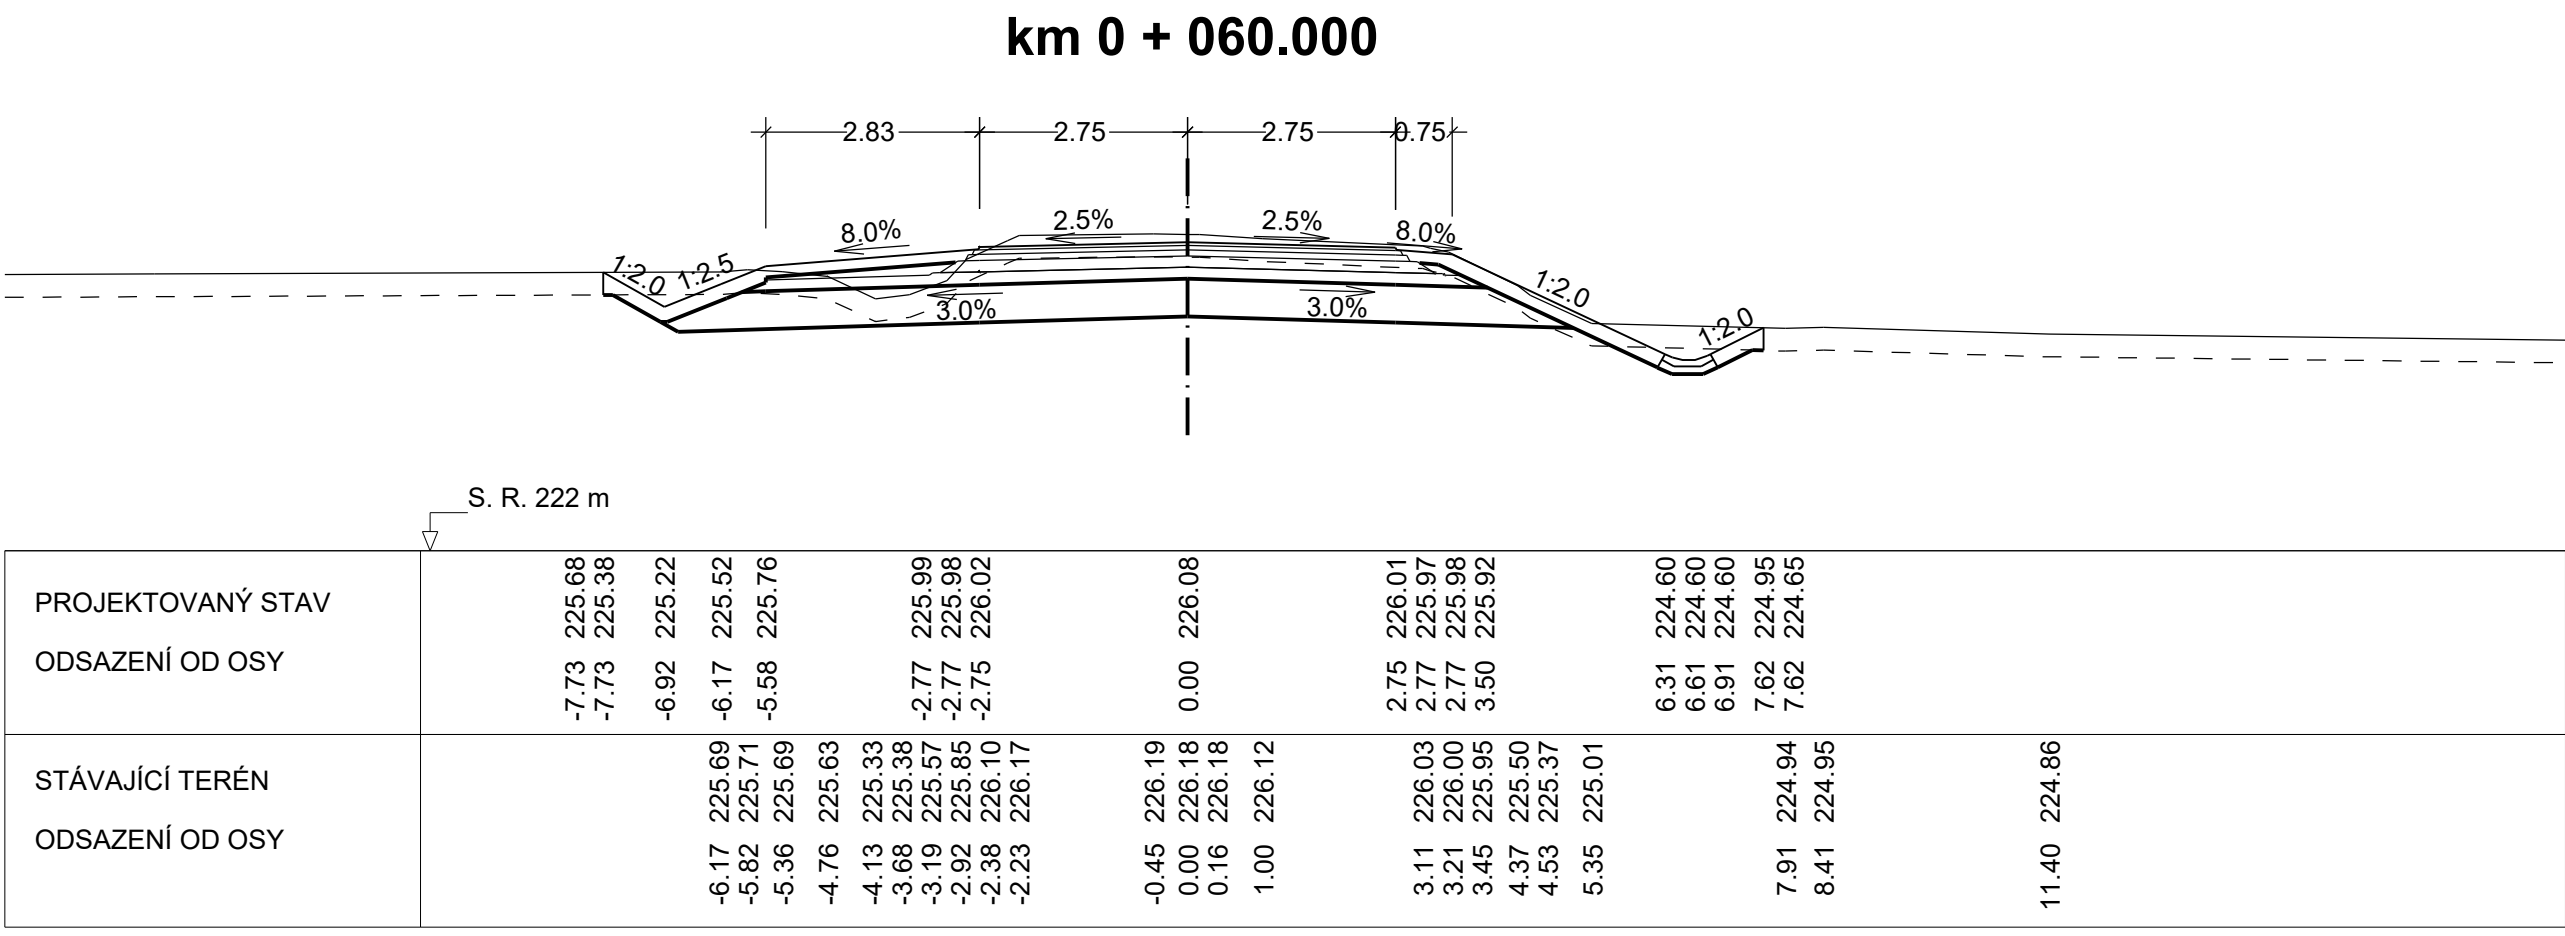
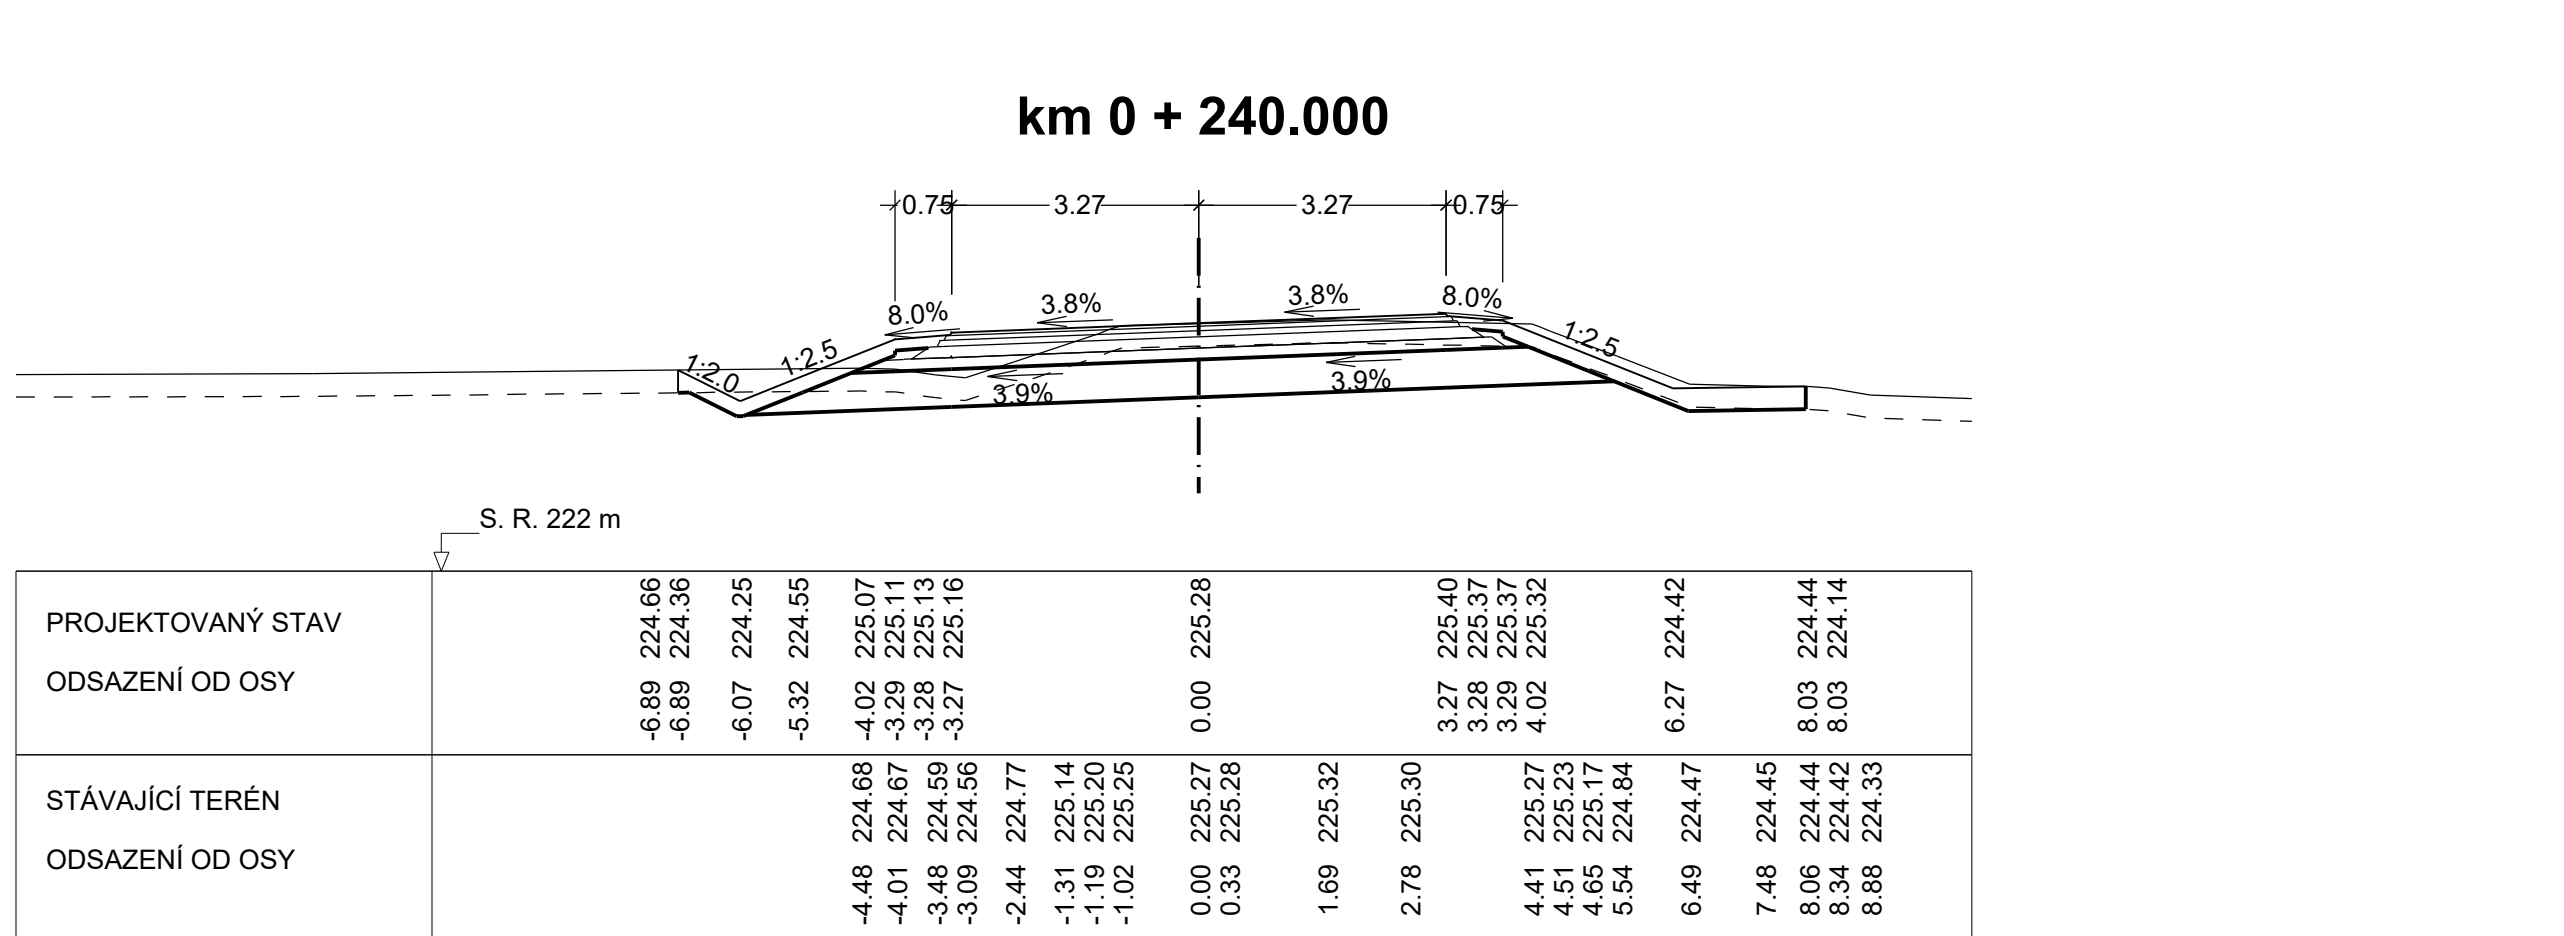
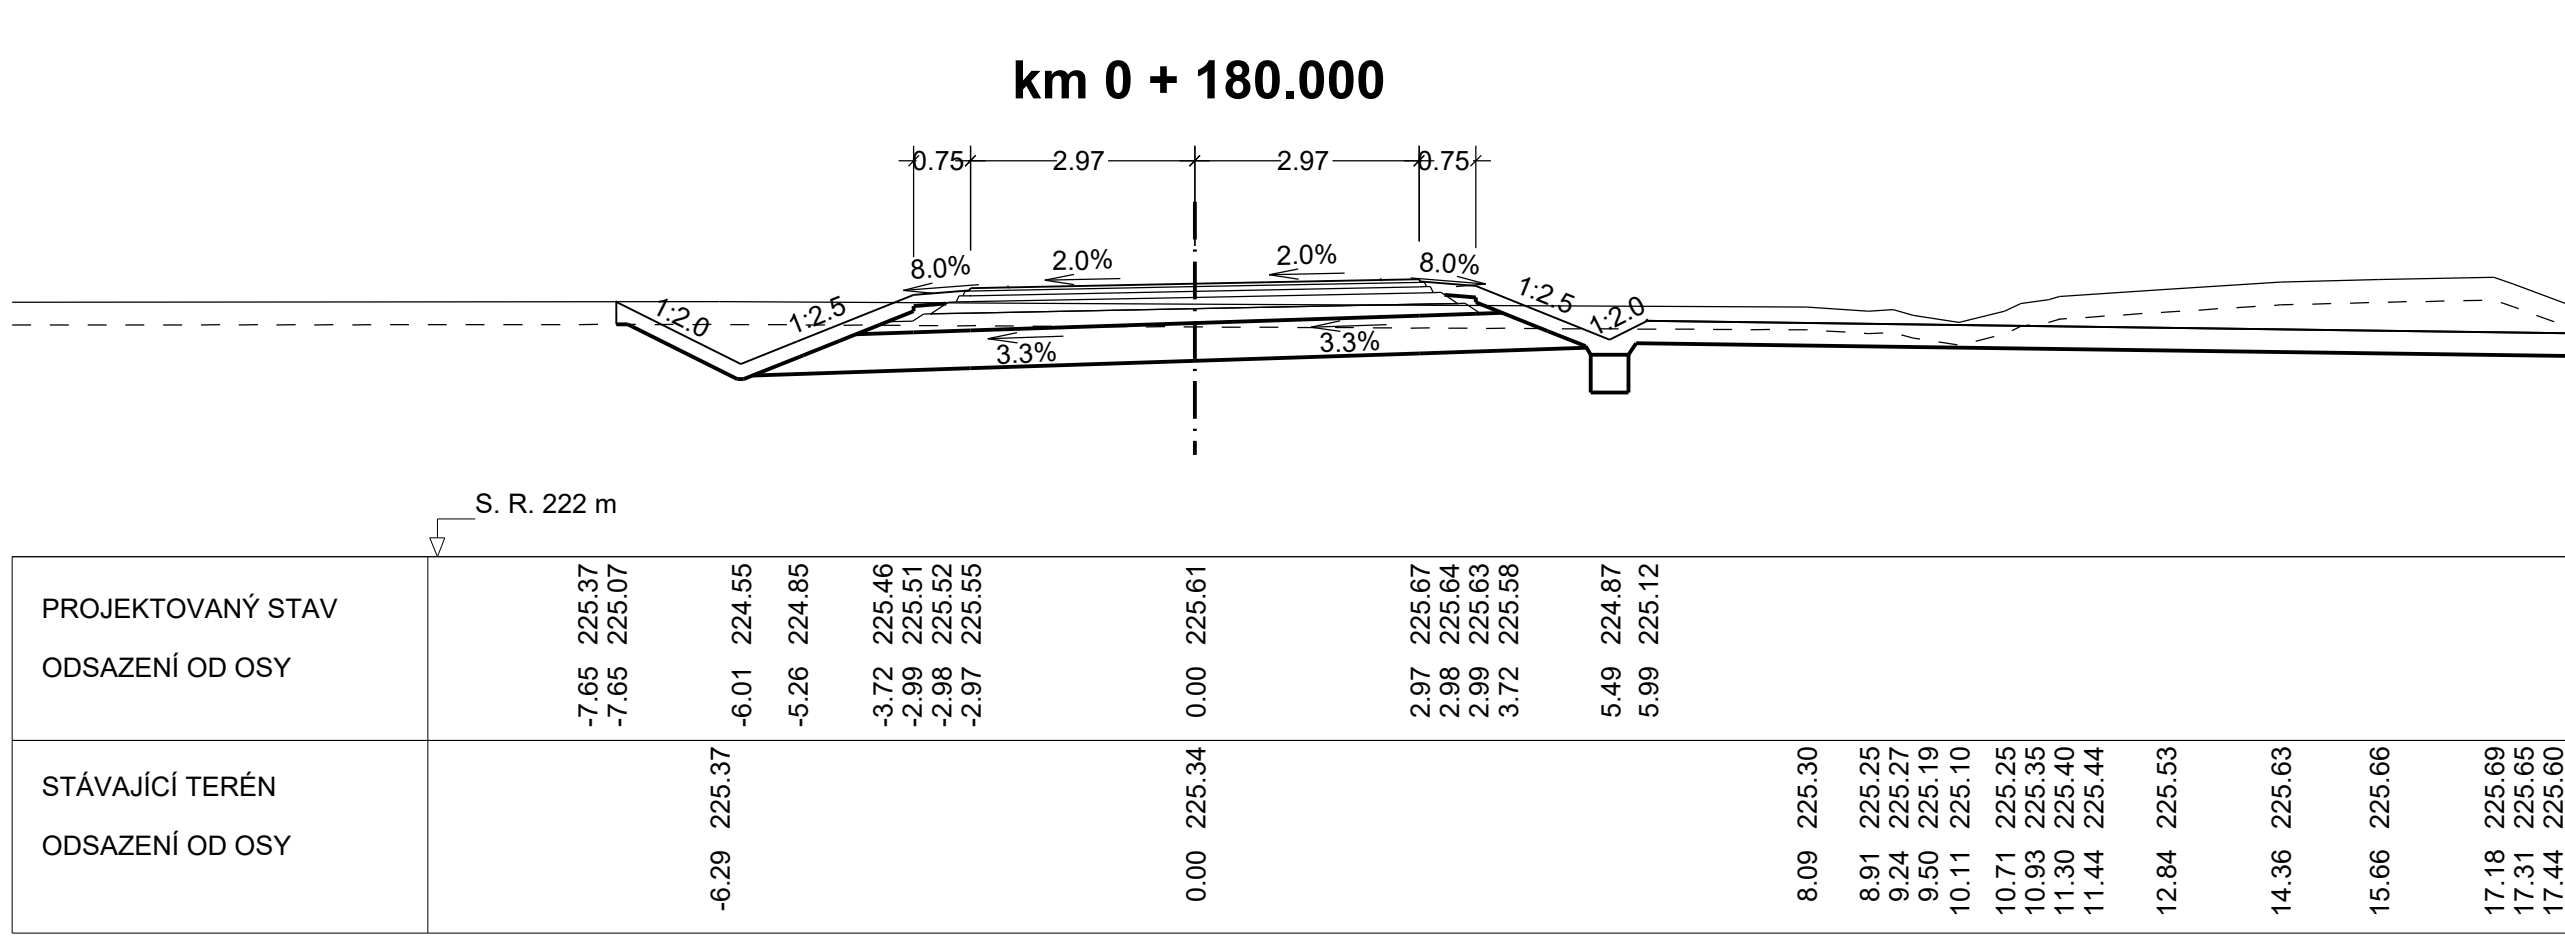
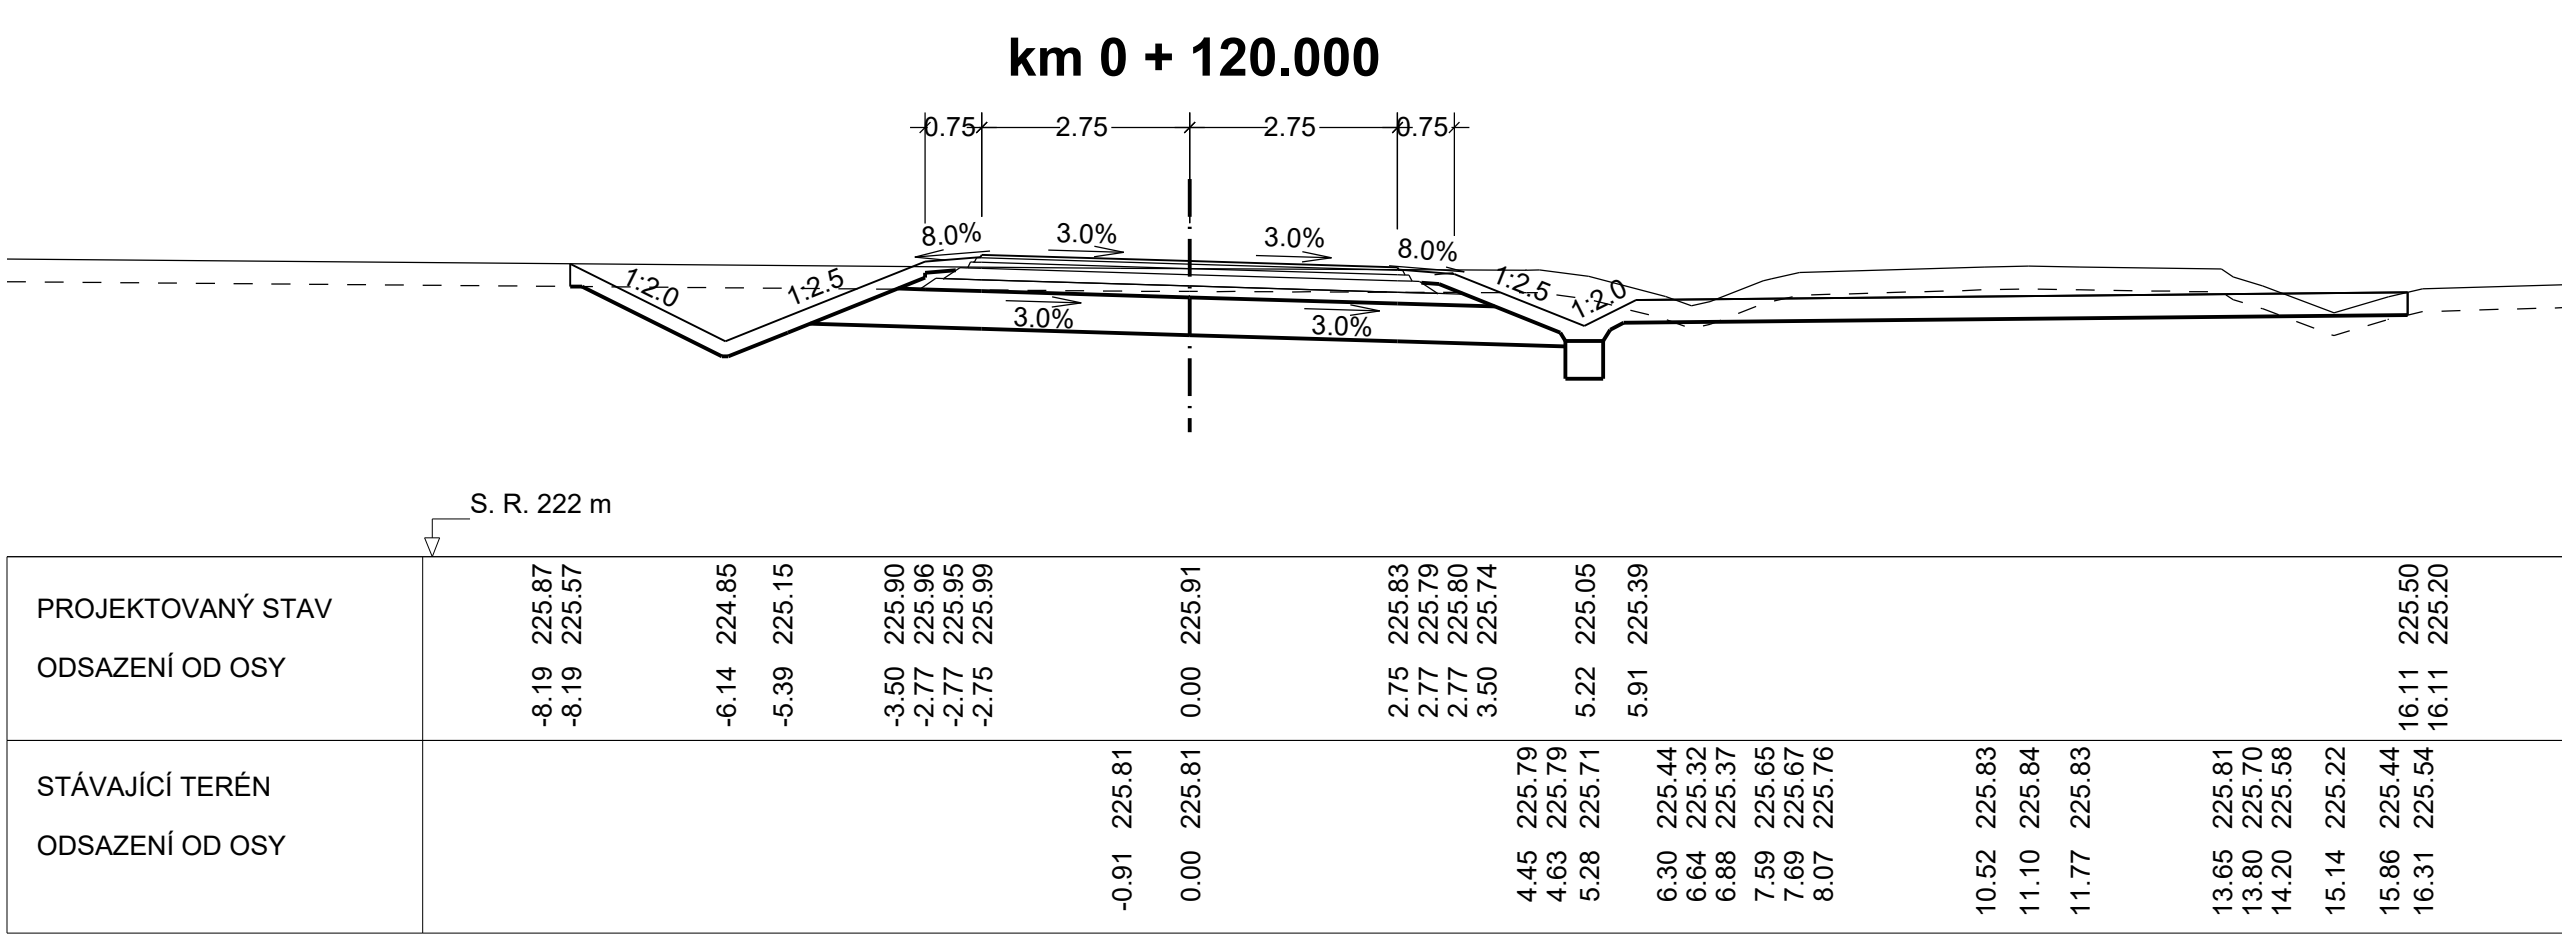


SO 122 - PŘELOŽKA SILNICE III/27612 V km 6,080
PŘÍČNÉ ŘEZY, M 1 : 100

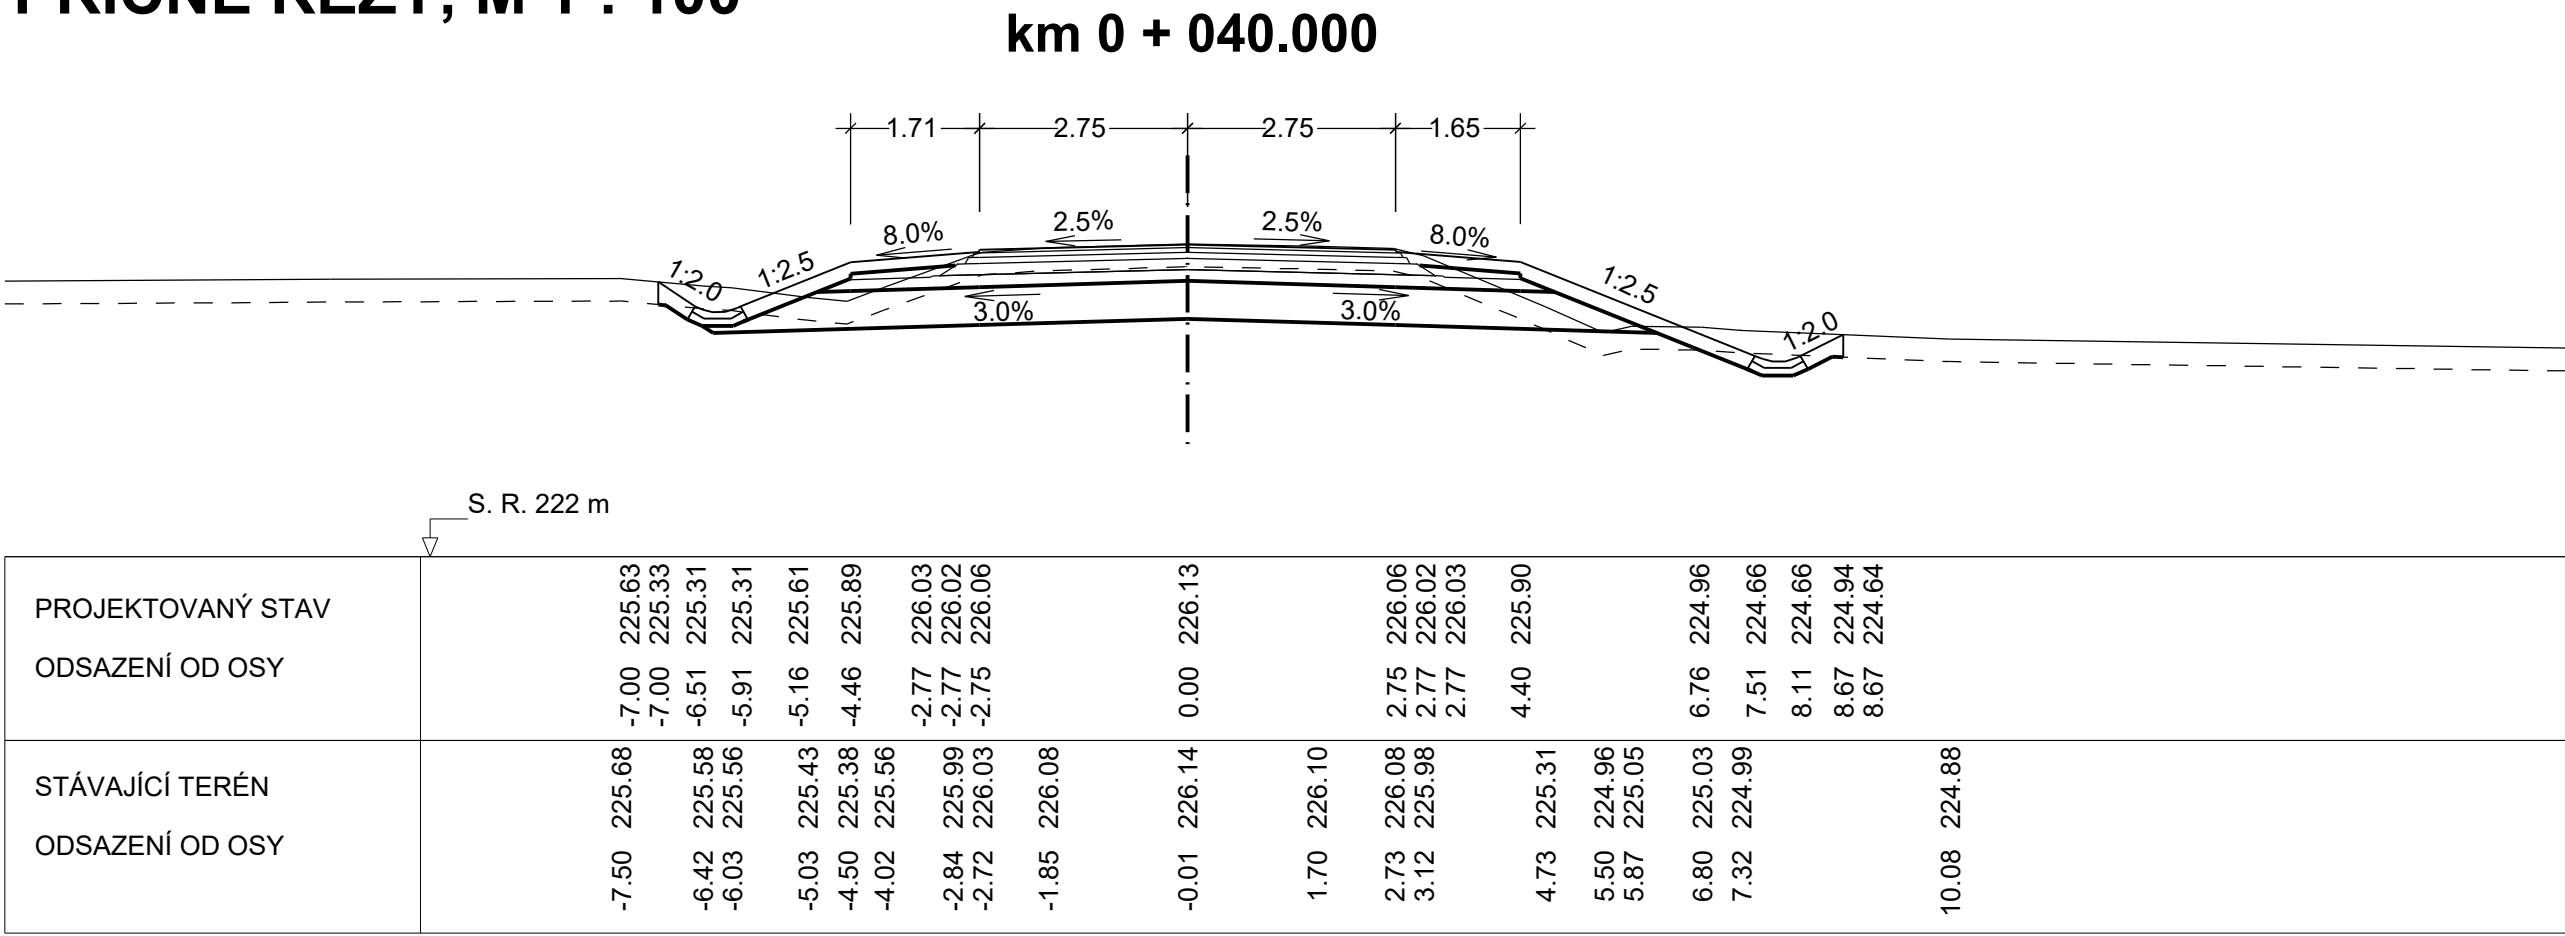

Výškový systém BpV

SO 122 Přeložka silnice III/27612 v km 6,080

Objednatel: **ŘEDITELSTVÍ SILNIC A DÁLNIC** Ředitelství silnic a dálnic s. p.
Čerčanská 2023/12, Křč, 140 00 Praha 4

Zhotovitel: **Valbek** Valbek, spol. s r.o.
Vaňurova 505/17, 460 07 Liberec 3

HIP: ING. T. KLIMENT

Valbek

Vypracoval: ING. A. DUMANSKA
Zodp. projektant: ING. T. KLIMENT
Tech. kontrola: ING. M. HANŽL
Akce: I/16 MLADÁ BOLESLAV - MARTINOVICE

Zak. číslo: 21-L113-001
Datum: 02/2025
Stupeň: POPS
Počet formátů: 8 x A4
Měřítko: 1 : 100
Č. přílohy: Paré

Zhotovitel: Valbek, spol. s r.o.
Vaňurova 505/17, 460 07 Liberec 3

Příloha: PŘÍČNÉ ŘEZY

5