
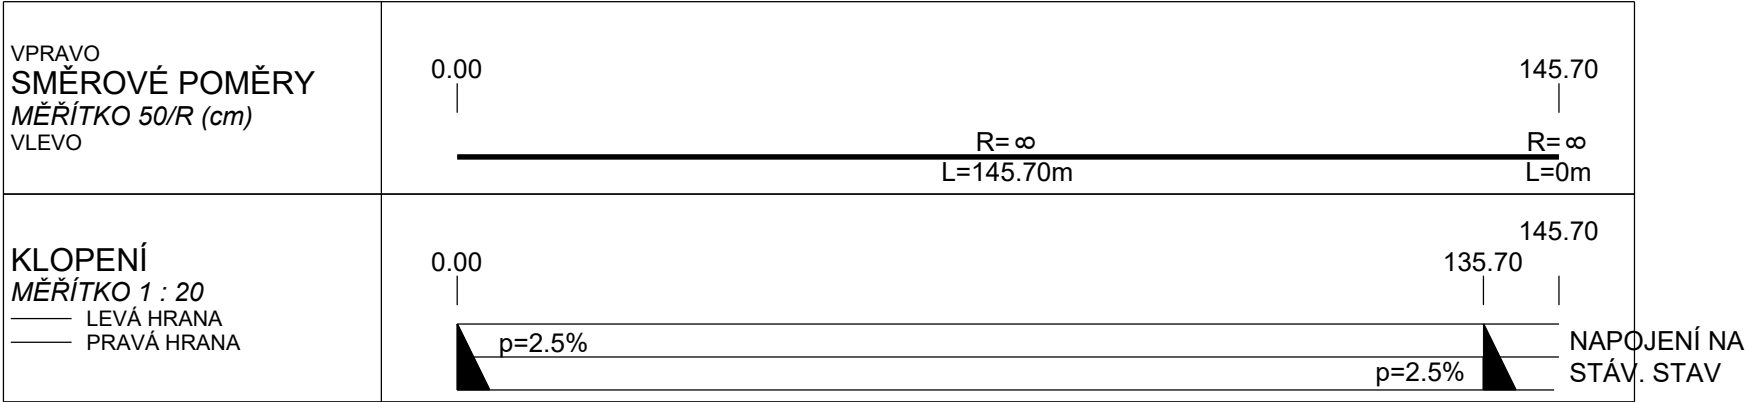


SO 123 - PŘELOŽKA MÍSTNÍ KOMUNIKACE V km 0,230  
PODÉLNÝ PROFIL, M 1 : 1 000 / 100

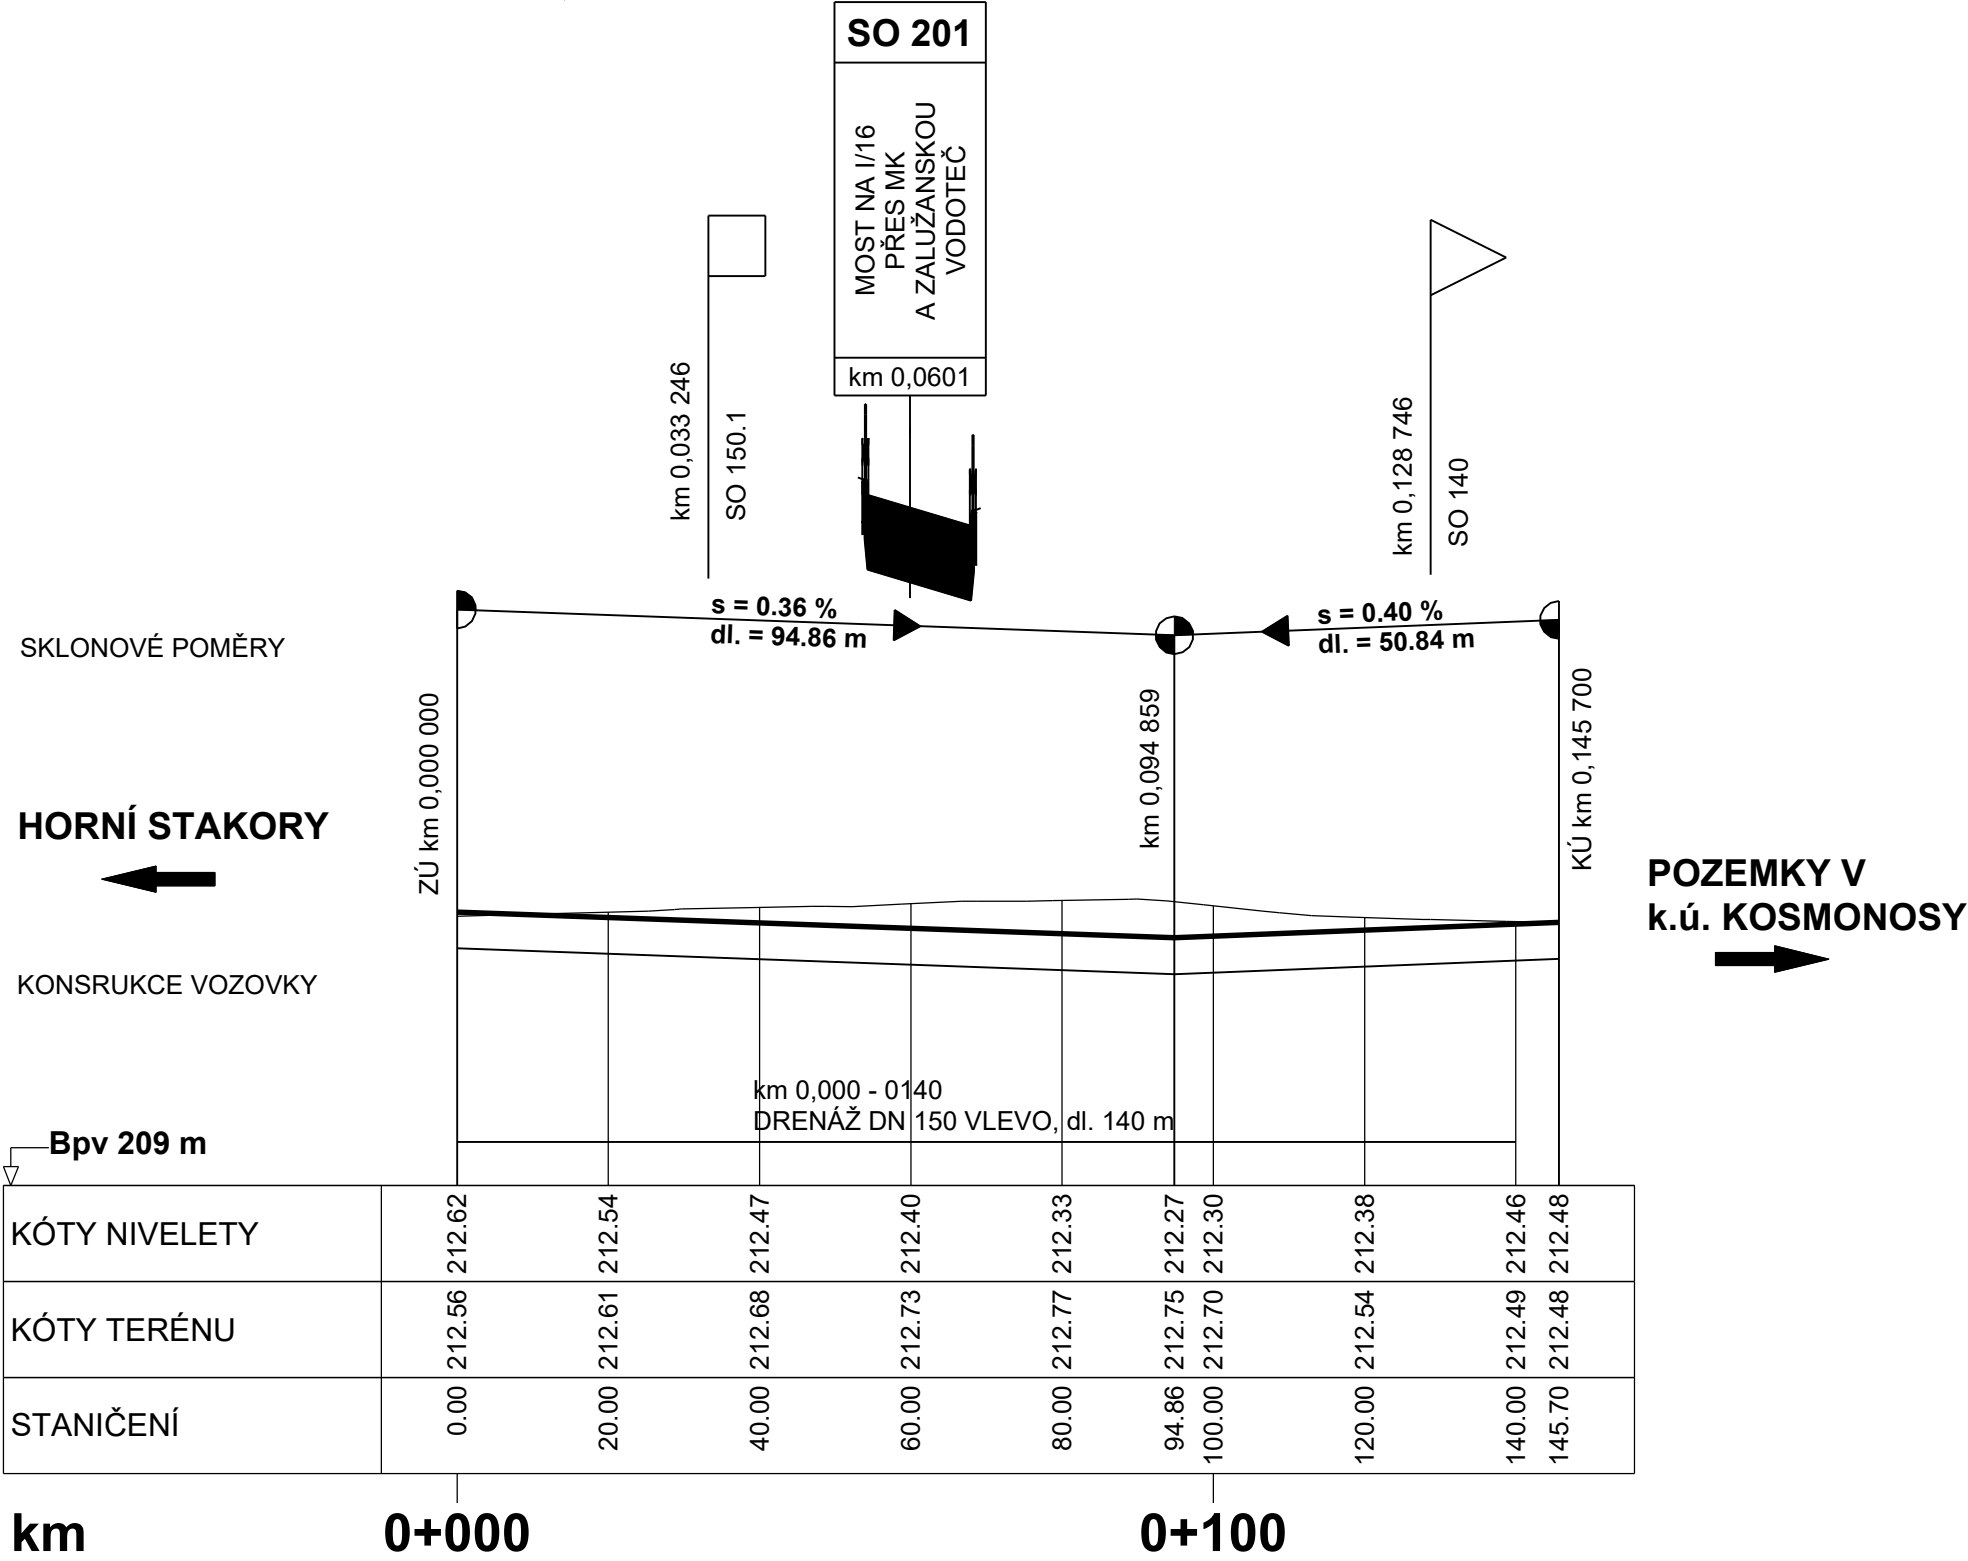

Výškový systém Bpv

SO 123

Přeložka místní komunikace v km 0,230

Objednatel:



Ředitelství  
silnic  
a dálnic

Ředitelství silnic a dálnic s. p.  
Čerčanská 2023/12, Krč, 140 00 Praha 4

Zhotovitel:



Valbek

Valbek, spol. s r.o.

Vaňurova 505/17  
460 07 Liberec 3

HIP:  
ING. T. KLIMENT



Valbek

Vypracoval

ING. A. DUMANSKA

Zodp. projektant

ING. T. KLIMENT

Tech. kontrola

ING. M. HANŽL

Akce

I/16 MLADÁ BOLESLAV - MARTINOVICE

Zhotovitel:

Valbek, spol. s r.o.  
Vaňurova 505/17  
460 07 Liberec 3

Příloha

PODÉLNÝ PROFIL

Zak. číslo

21-L113-001

Datum

02/2025

Stupeň

PDPS

Počet formátů

3 x A4

Měřítko

1 : 1000 / 100

Č. přílohy

Paré

3