


SO 123 - PŘELOŽKA MÍSTNÍ KOMUNIKACE V km 0,230
VZOROVÉ PŘÍČNÉ ŘEZY, M 1 : 50

NÁVRHOVÁ KATEGORIE MO -/7,5/40

TŘÍDA DOPRAVNÍHO ZATÍŽENÍ IV
NÁVRHOVÁ ÚROVEŇ PORUŠENÍ D1
TYP PODLOŽÍ PIII (D1-A-2)

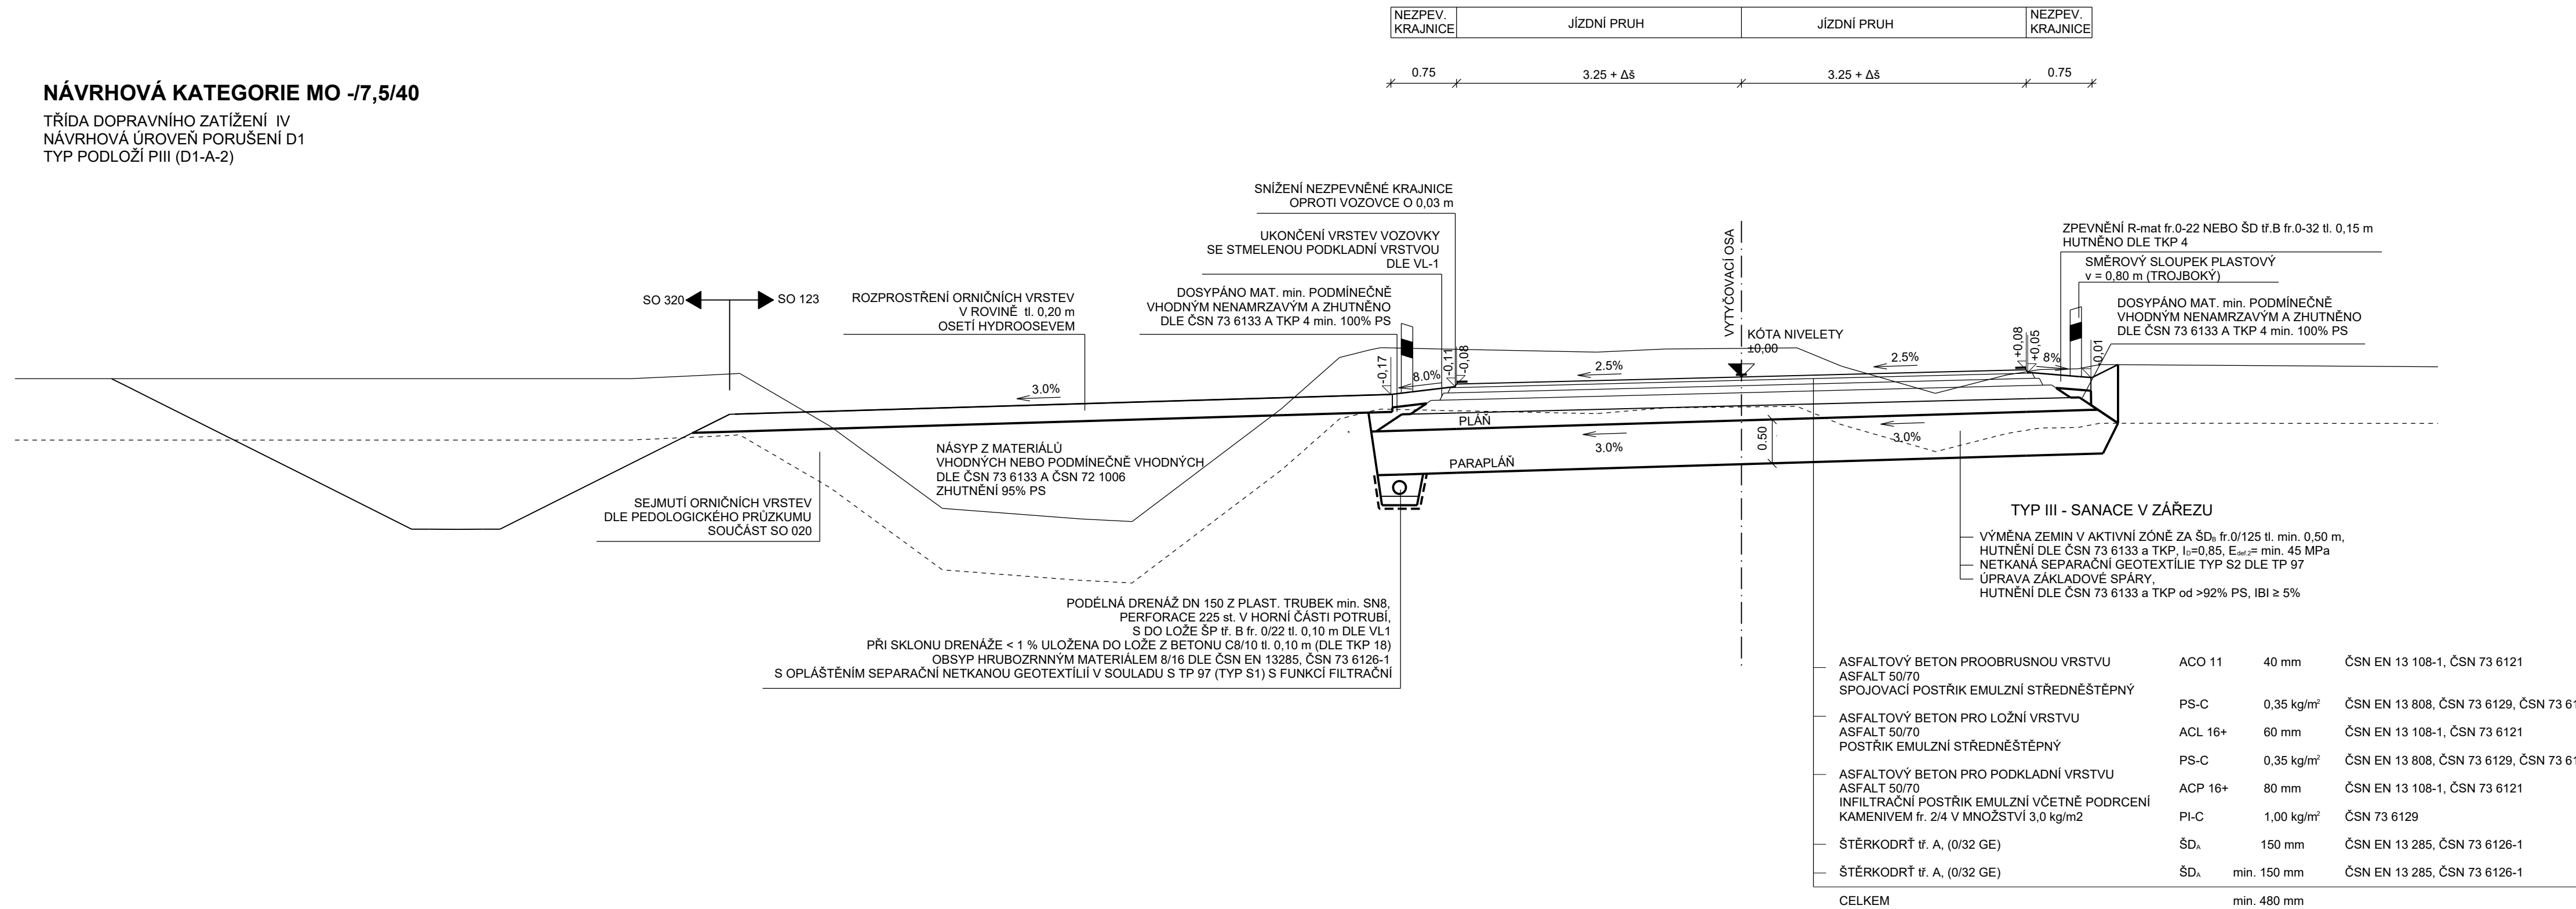

DOD.24

SO 123 Přeložka místní komunikace v km 0,230

Objednatel:



**ŘEDITELSTVÍ
SILNIC
A DÁLNIC**

Ředitelství silnic a dálnic s. p.
Čerčanská 2023/12, Krč, 140 00 Praha 4

Zhotovitel:



Valbek

Valbek, spol. s r.o.
Vaňurova 505/17
460 07 Liberec 3

HIP:

ING. T. KLIMENT

	Vypracoval	ING. A. DUMANSKA		Zak. číslo	21-LI13-001
	Zodp. projektant	ING. T. KLIMENT		Datum	02/2025
	Tech. kontrola	ING. M. HANŽL		Stupeň	PDPS
	Akce I/16 MLADÁ BOLESLAV - MARTINOVICE			Počet formátů	5 x A4
				Měřítko	1 : 50
Zhotovitel: Valbek, spol. s r.o. Vaňurova 505/17 460 07 Liberec 3	Příloha VZOROVÉ PŘÍČNÉ ŘEZY			Č. přílohy	Paré
				4	