




SO 123 - PŘELOŽKA MÍSTNÍ KOMUNIKACE V km 0,230
PŘÍČNÉ ŘEZY, M 1:100

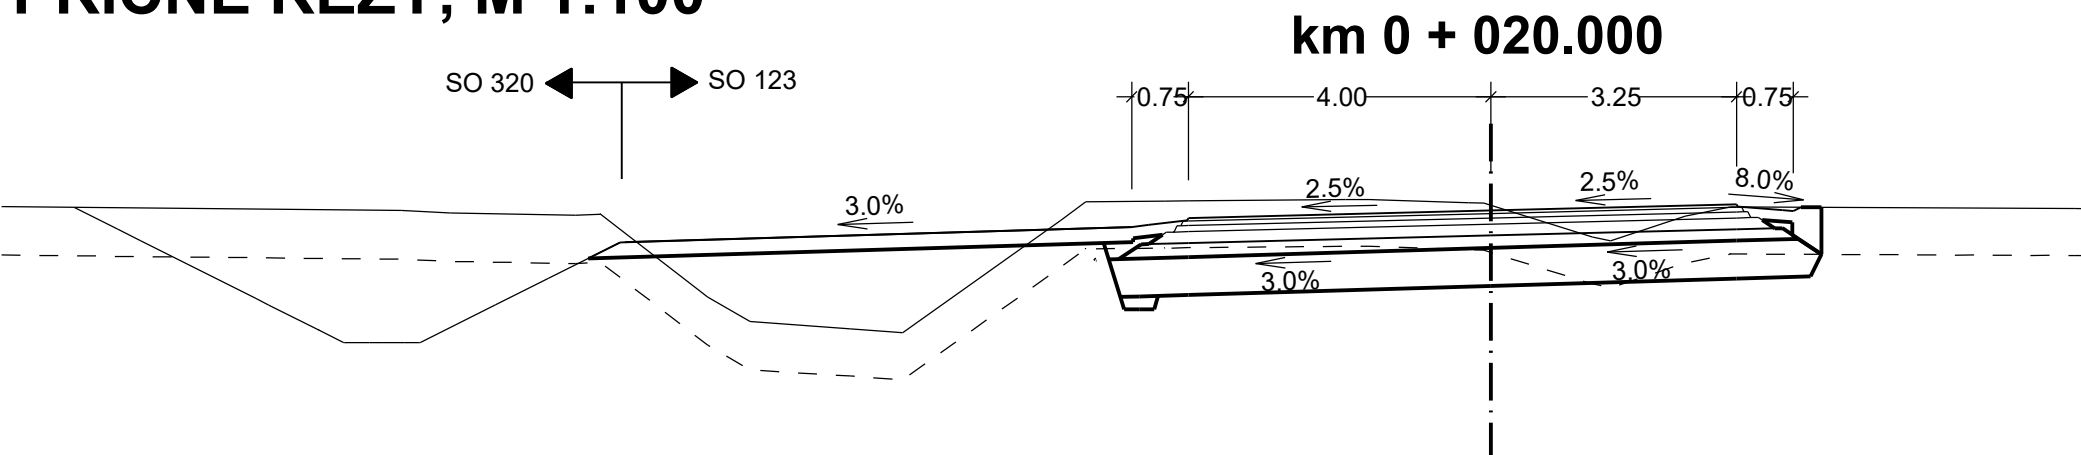


PROJEKTOVANÝ STAV	S. R. 208 m											
ODSAZENÍ OD OSY												
STÁVAJÍCÍ TERÉN	-13.76	212.51										
ODSAZENÍ OD OSY	-12.10	212.48	-11.77	212.50	-11.45	212.12						
	-10.36	211.40	-9.80	211.07	-8.47	210.98	-7.78	210.93				
	-5.69	212.41	-5.36	212.66	-4.75	212.33	-4.52	212.35	-4.02	212.41	-4.02	212.40
	-4.31	212.67	-4.00	212.67	-4.00	212.44	-0.29	212.65	-0.09	212.64	0.00	212.54
	1.34	212.19	1.59	212.14	2.57	212.47	3.17	212.59	3.25	212.62	3.27	212.59
	3.86	212.55	4.00	212.54	4.10	212.59	4.37	212.59	4.37	211.97		
	7.72	212.57										

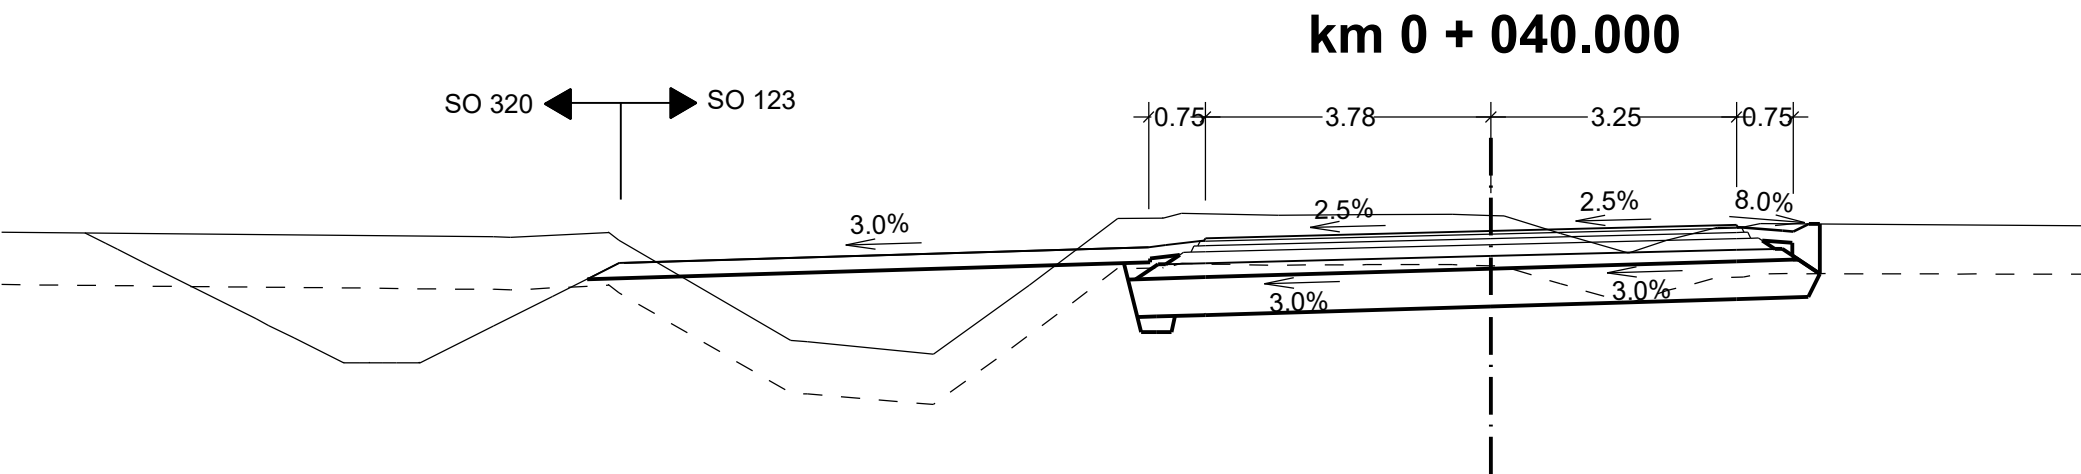


PROJEKTOVANÝ STAV	S. R. 208 m											
ODSAZENÍ OD OSY												
STÁVAJÍCÍ TERÉN	-13.19	212.40	-12.97	212.39	-11.66	212.45	-11.53	212.35	-9.26	211.03	-9.04	211.01
ODSAZENÍ OD OSY	-7.37	210.84	-6.11	211.75	-4.94	212.64	-4.33	212.64	-4.09	212.71	-3.78	212.38
	-2.81	212.68	-1.65	212.69	-0.51	212.69	0.00	212.68	0.17	212.67	0.92	212.44
	1.82	212.18	2.33	212.35	3.00	212.52	3.34	212.53	3.56	212.57	3.25	212.55
	3.27	212.51	3.27	212.52	3.86	212.48	4.00	212.46	4.21	212.57	4.35	212.57
	4.35	211.91										

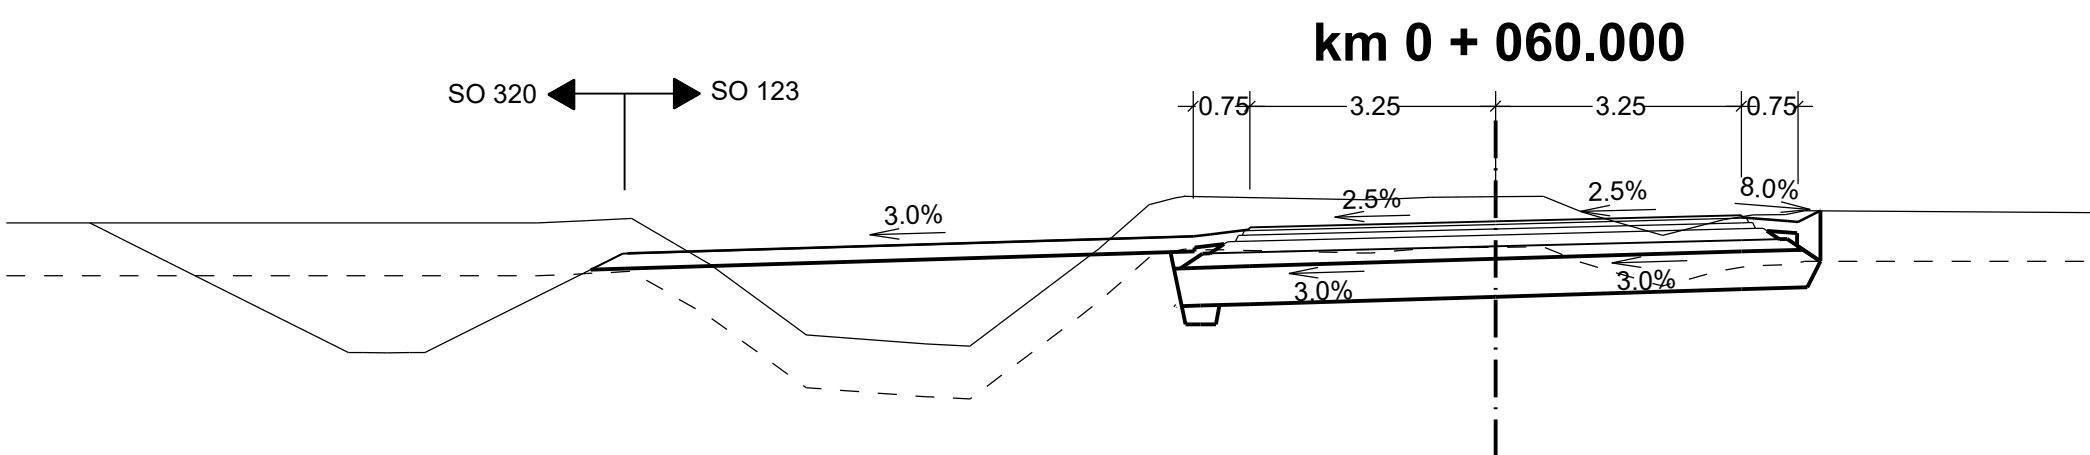


PROJEKTOVANÝ STAV	S. R. 208 m											
ODSAZENÍ OD OSY												
STÁVAJÍCÍ TERÉN	-12.67	212.38	-12.02	212.41	-11.43	212.44	-10.39	211.84	-9.12	210.90	-7.53	210.78
ODSAZENÍ OD OSY	-6.95	210.75	-5.25	212.04	-4.58	212.62	-4.24	212.71	-4.11	212.73	-3.27	212.29
	-3.45	212.72	-1.65	212.68	-0.86	212.72	0.00	212.73	0.63	212.73	1.14	212.52
	2.21	212.21	3.02	212.42	3.40	212.48	3.84	212.49	4.09	212.54	3.25	212.48
	3.27	212.44	3.27	212.45	3.86	212.40	4.00	212.39	4.29	212.54	4.30	212.54
	4.30	211.87										

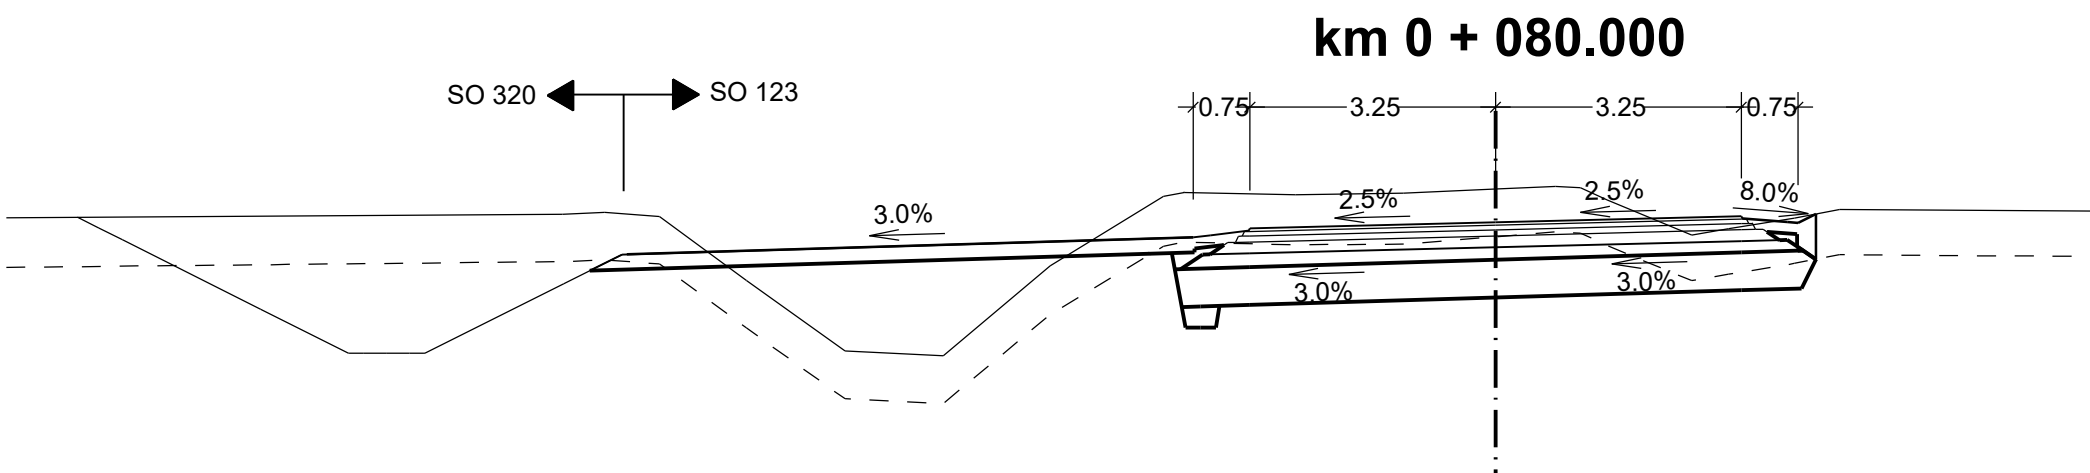

PROJEKTOVANÝ STAV	S. R. 207 m											
ODSAZENÍ OD OSY												
STÁVAJÍCÍ TERÉN	-12.34	212.43	-11.78	212.46	-11.06	212.41	-9.91	211.56	-8.60	210.63	-7.30	210.56
ODSAZENÍ OD OSY	-5.89	211.75	-4.39	212.67	-4.12	212.72	-2.64	212.69	-1.22	212.71	0.00	212.77
	0.79	212.80	1.12	212.78	1.47	212.62	2.60	212.16	3.08	212.24	3.25	212.41
	3.27	212.37	3.27	212.38	3.86	212.33	4.00	212.32	4.24	212.44	4.24	211.84
	4.24	211.84										

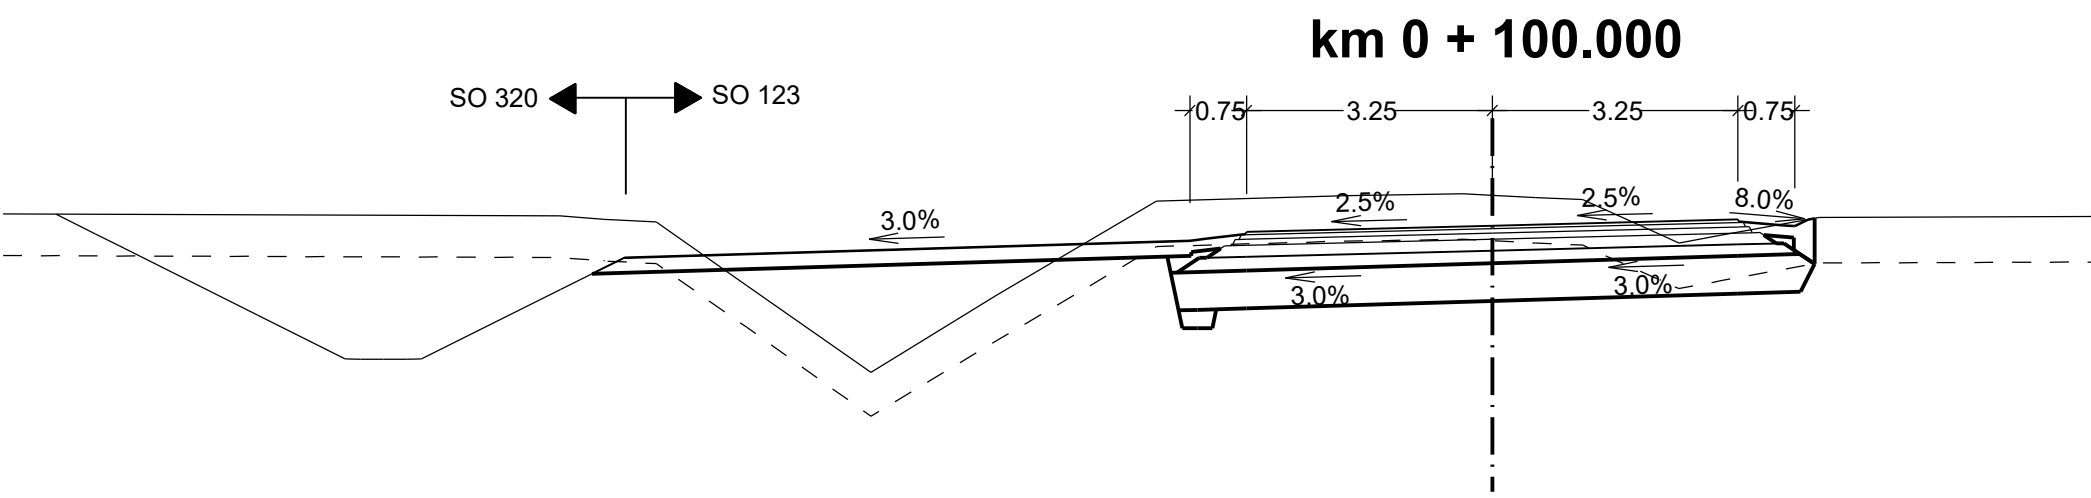

PROJEKTOVANÝ STAV	S. R. 207 m											
ODSAZENÍ OD OSY												
STÁVAJÍCÍ TERÉN	-12.33	212.42	-11.74	212.38	-11.06	212.34	-9.86	211.50	-8.22	210.35	-6.55	211.38
ODSAZENÍ OD OSY	-4.44	212.62	-4.00	212.10	-3.77	212.12	-3.27	212.17	-3.26	212.18	-3.25	212.21
	-1.94	212.69	-0.39	212.72	0.00	212.70	0.57	212.67	1.20	212.64	2.23	212.18
	2.47	212.06	3.01	212.17	4.32	212.40	3.27	212.34	3.27	212.35	3.86	212.30
	4.00	212.29	4.17	212.38	4.26	212.39	4.26	211.79				

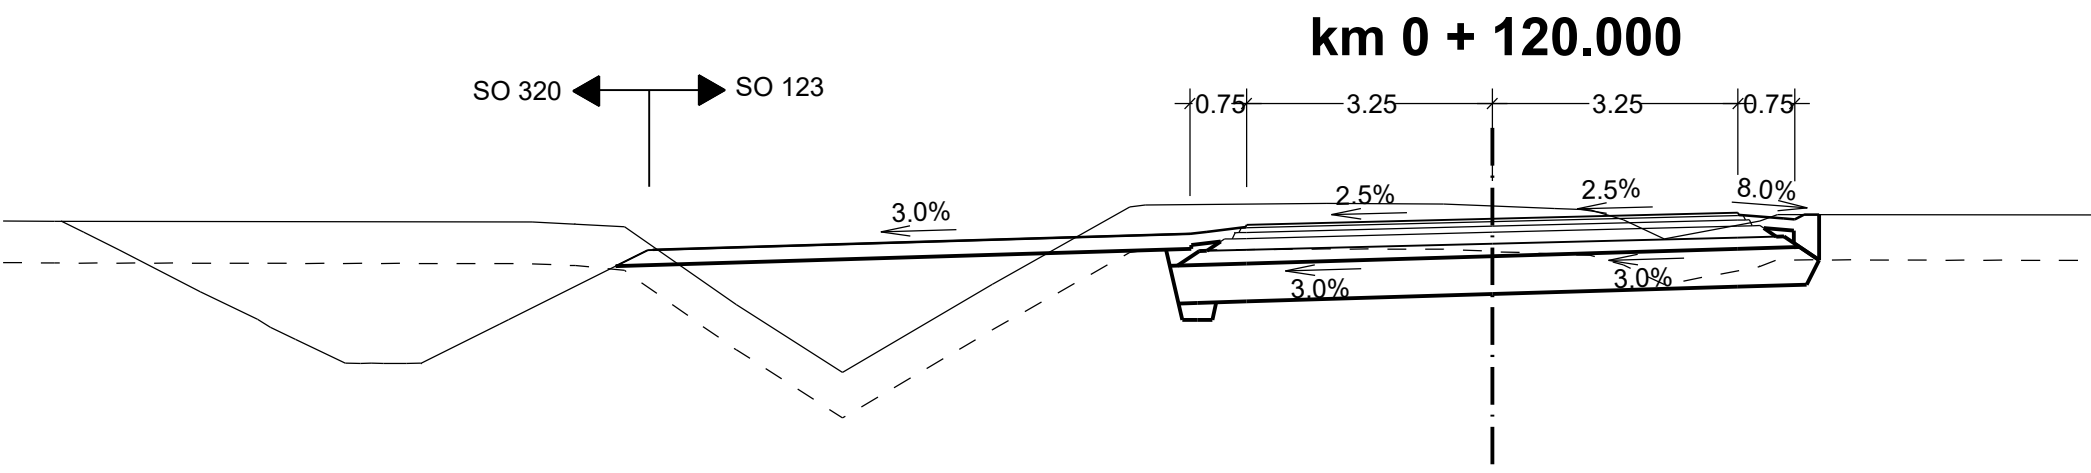

PROJEKTOVANÝ STAV	S. R. 207 m											
ODSAZENÍ OD OSY												
STÁVAJÍCÍ TERÉN	-12.70	212.33	-12.13	212.30	-11.48	212.27	-10.00	211.24	-8.60	210.34	-6.61	211.51
ODSAZENÍ OD OSY	-4.79	212.53	-4.59	212.55	-4.00	212.18	-3.77	212.20	-3.27	212.25	-3.26	212.26
	-2.19	212.58	-0.65	212.57	0.00	212.54	0.83	212.51	1.29	212.49	1.73	212.36
	2.28	212.11	3.54	212.35	3.77	212.43	3.86	212.38	4.00	212.37	4.13	212.43
	4.32	212.43	4.32	211.83								

Výškový systém Bpv

SO 123 Přeložka místní komunikace v km 0,230

Objednatel:

 **Ředitelství silnic a dálnic**

Ředitelství silnic a dálnic s. p.
Čerčanská 2023/12, Krč, 140 00 Praha 4

Zhotovitel:

 **Valbek**

Valbek, spol. s r.o.
Vaňurova 505/17
460 07 Liberec 3

HIP:

ING. T. KLIMENT

 **Valbek**

Zhotovitel:
Valbek, spol. s r.o.
Vaňurova 505/17
460 07 Liberec 3

Vypracoval	ING. A. DUMANSKA	Zak. číslo	21-L113-001
Zodp. projektant	ING. T. KLIMENT	Datum	02/2025
Tech. kontrola	ING. M. HANŽL	Stupeň	PDPS
Akce		Počet formátů	3 x A4
		Měřítko	1 : 100
		Č. přílohy	Paré

Příloha

PŘÍČNÉ ŘEZY

5