


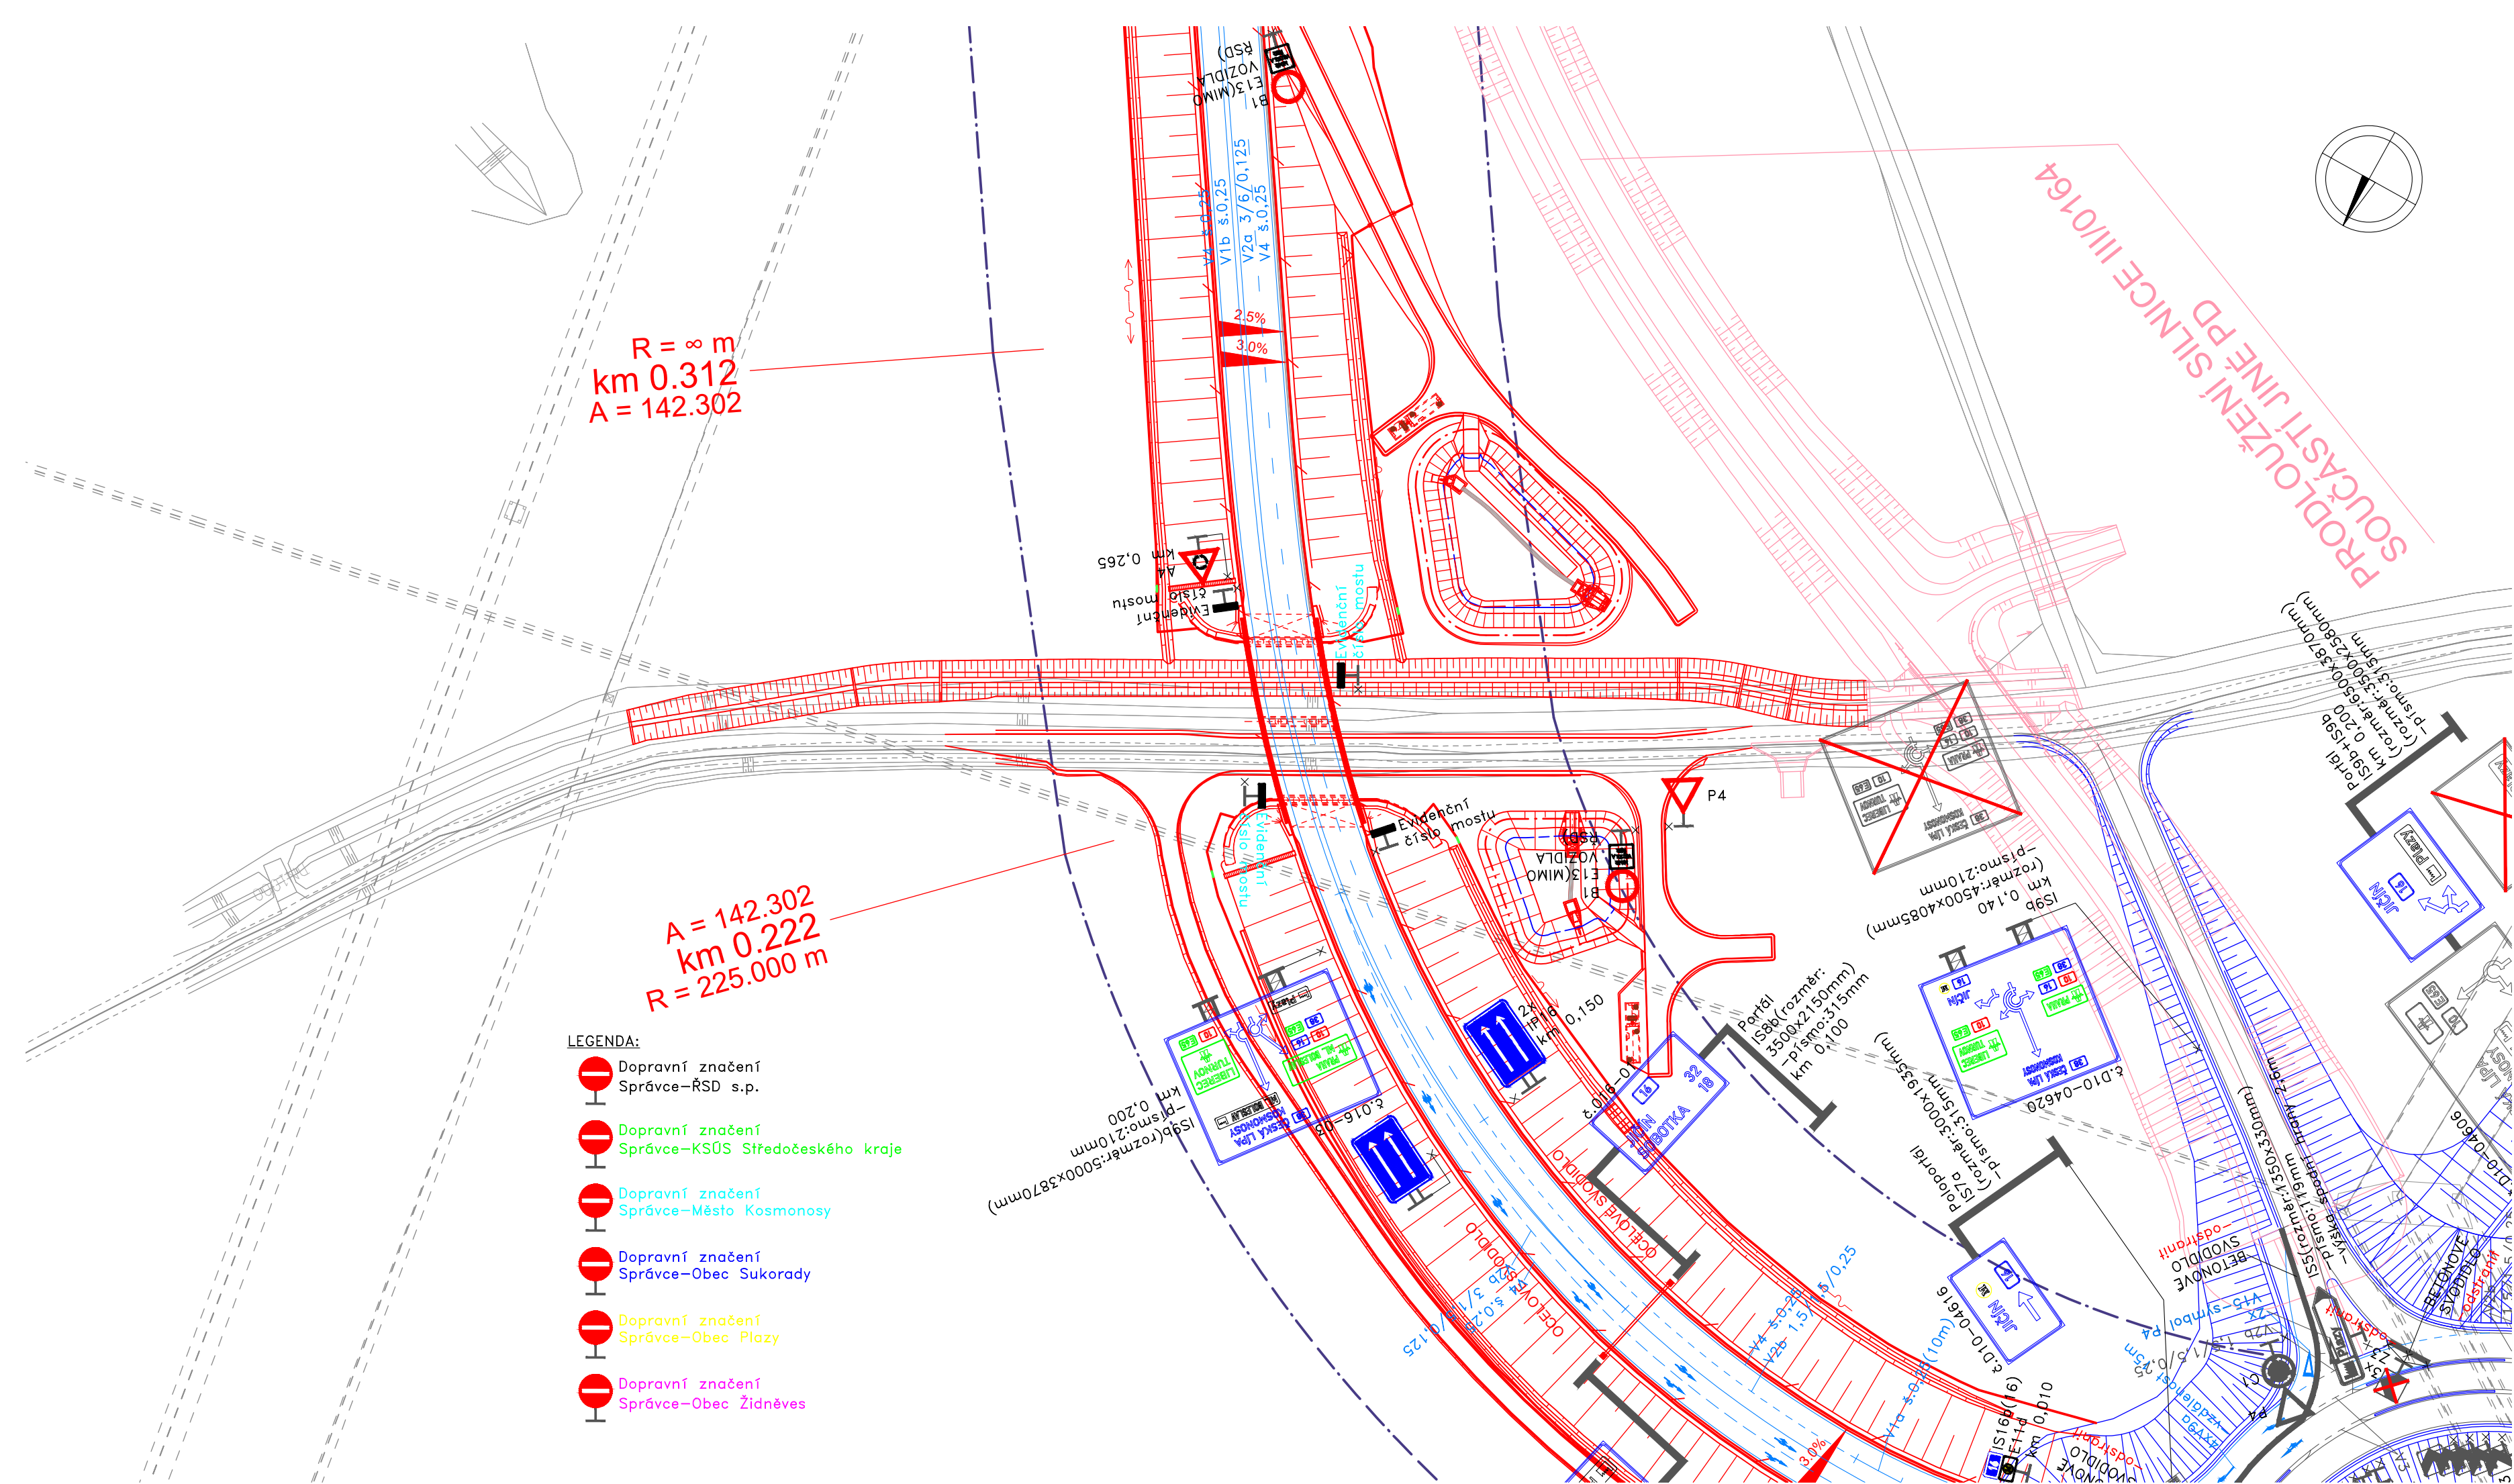

Souřadnicový systém: S-JTSK
Výškový systém: Bpv

SO 123 Přeložka místní komunikace v km 0,230

Objednatel:



**Ředitelství
silnic
a dálnic**

Ředitelství silnic a dálnic s. p.
Čerčanská 2023/12, Krč, 140 00 Praha 4

Zhotovitel:



Valbek, spol. s r.o.
Vaňurova 505/17
460 07 Liberec 3

	Vypracoval	STANISLAV KRUPÍČKA		Zak. číslo	024-24	
	Zodp. projektant	ING. PETER HAJOŠ		Datum	02/2025	
	Tech. kontrola	ANTONÍN SEIDL		Stupeň	PDPS	
	Akce			Počet formátů	3 x A4	
Zhotovitel: DISK s.r.o. Menšíkovská 1239/10 160 00 Praha 6	Příloha DOPRAVNÍ ZNAČENÍ			I/16 MLADÁ BOLESLAV - MARTINOVICE		
				Měřítko		1 : 1000
				Č. přílohy		Paré
				7		