


SO 124 - PŘELOŽKA MÍSTNÍ KOMUNIKACE km 7,340-7,700 VLEVO
PODÉLNÝ PROFIL M 1 : 1 000 / 100

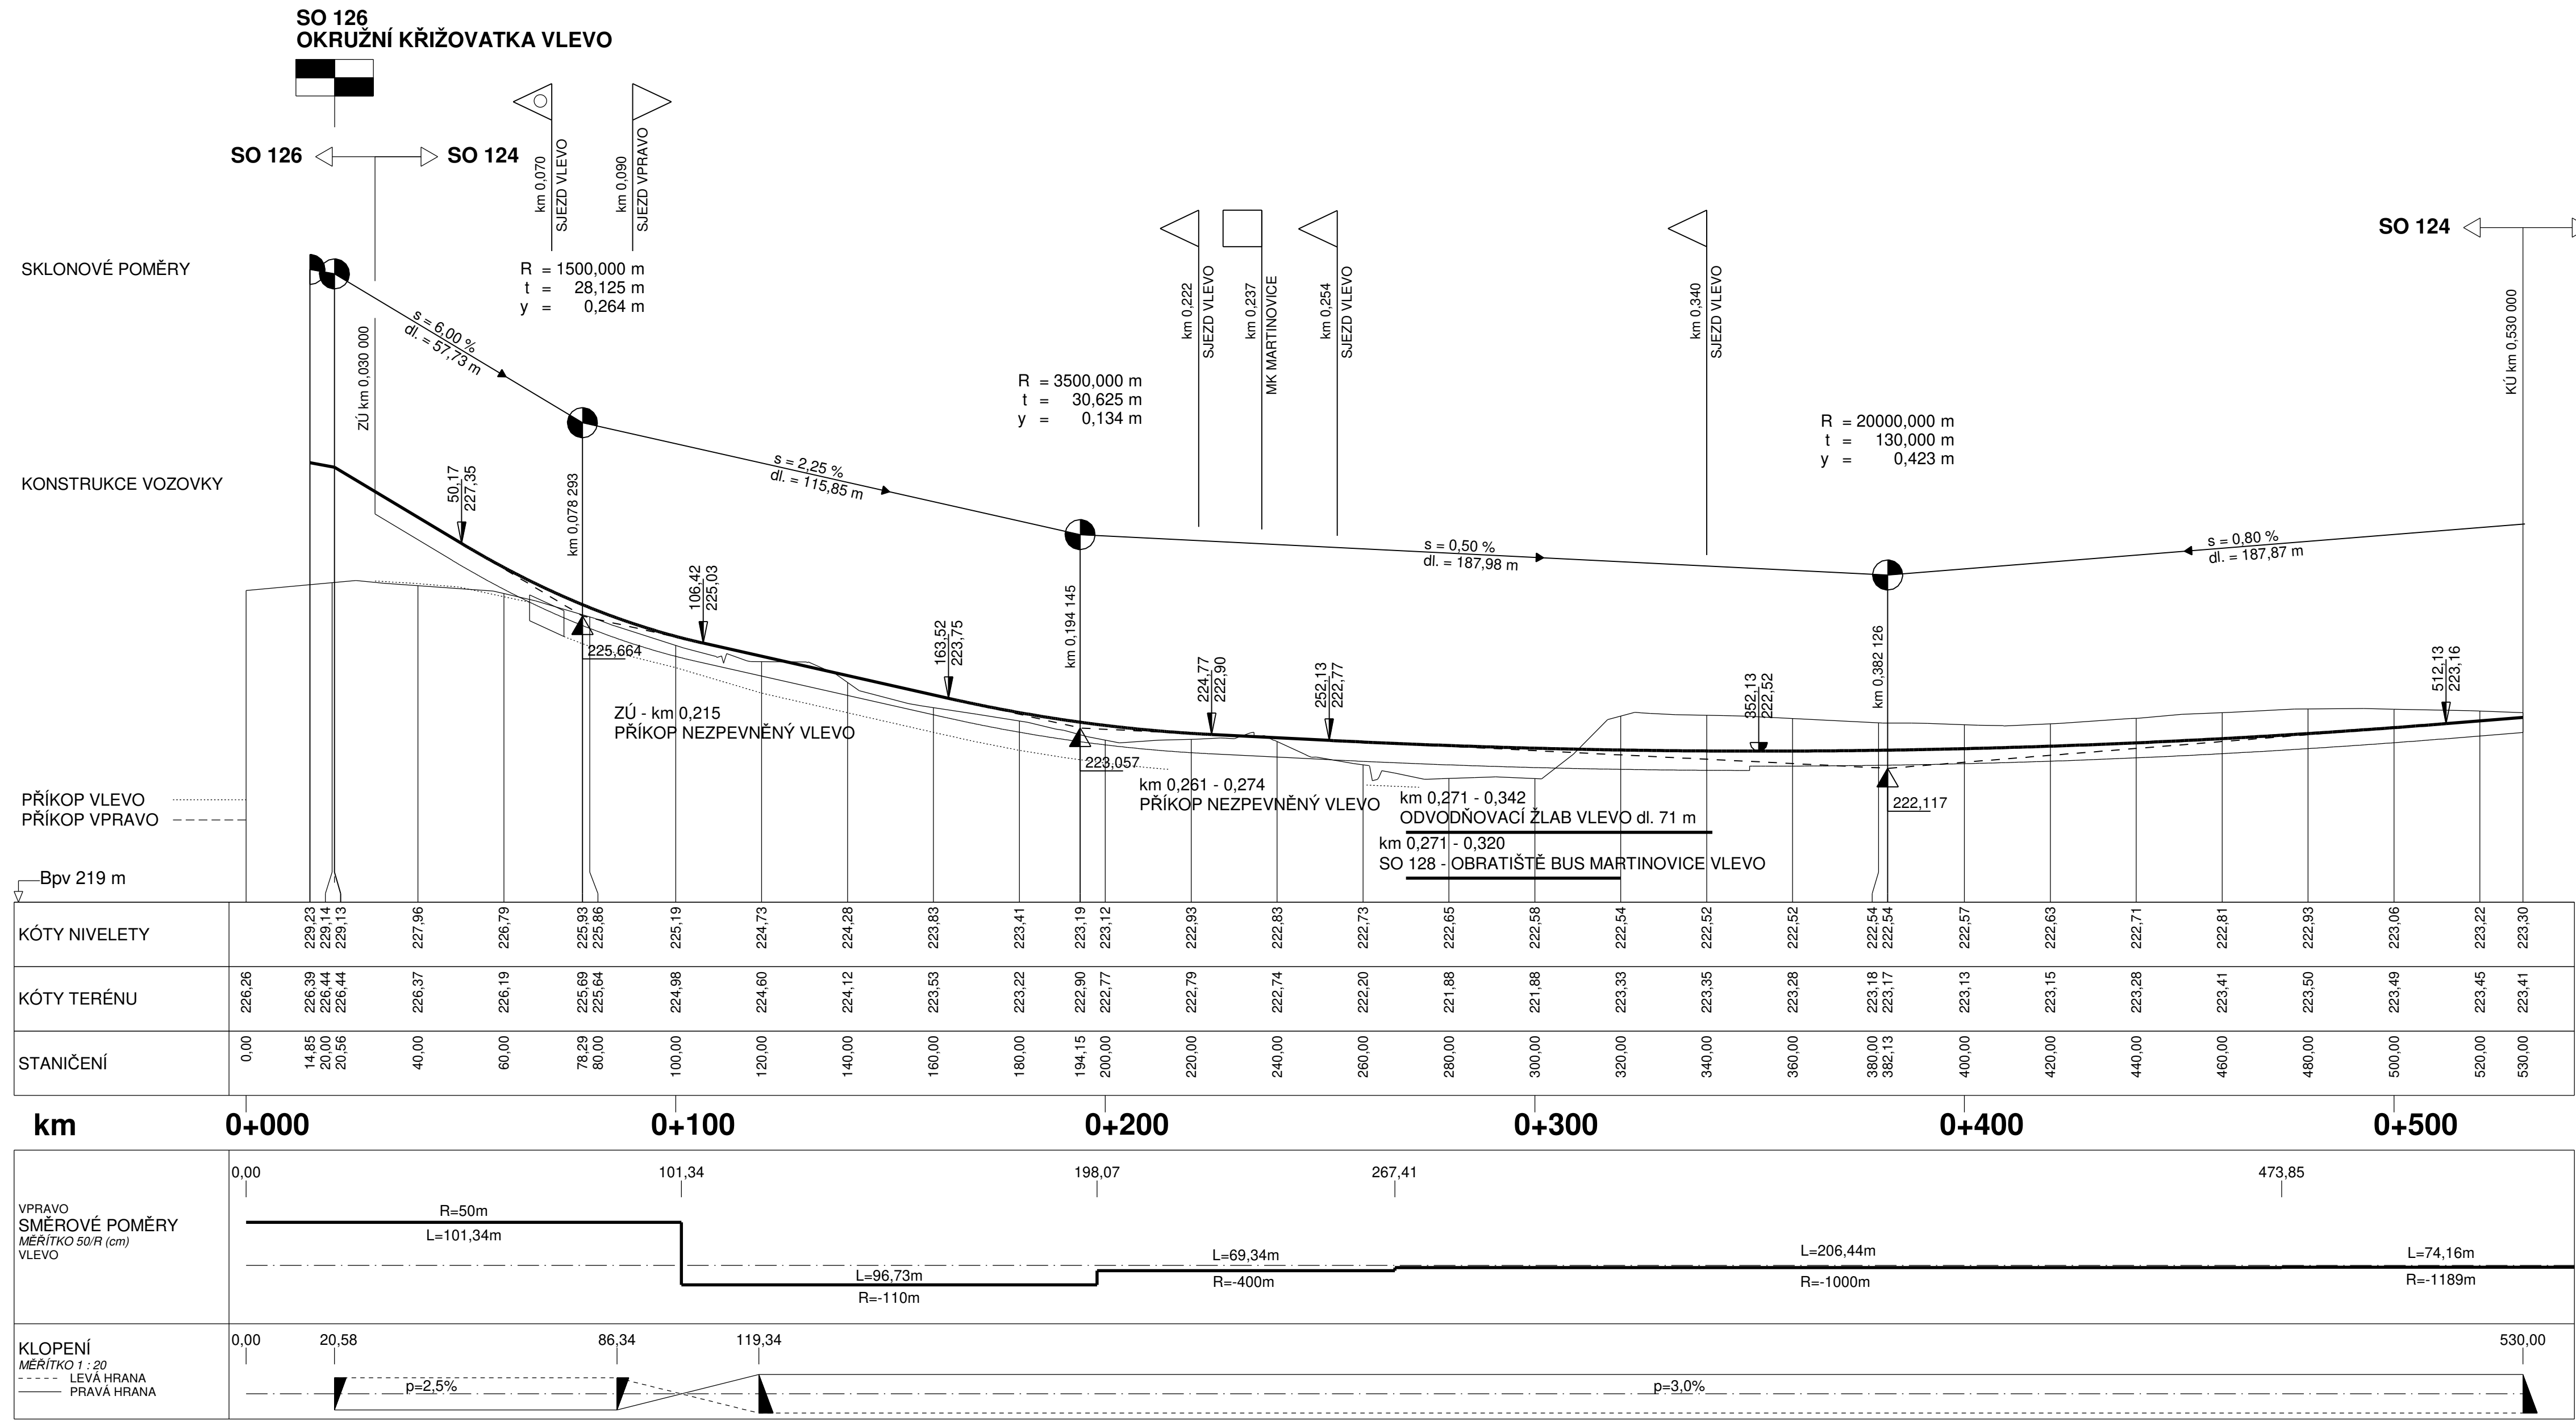

Výškový systém Bpv

SO 124 Přeložka místní komunikace km 7,340-7,700 vlevo

Objednatel:



ŘEDITELSTVÍ
SILNIC
A DÁLNIC

Ředitelství silnic a dálnic s. p.
Čerčanská 2023/12, Krč, 140 00 Praha 4

Zhotovitel:



Valbek, spol. s r.o.
Vaňurova 505/17
460 07 Liberec 3

HIP:

ING. T. KLIMENT



Vypracoval
Zodp. projektant
Tech. kontrola

M. KOŘÍNEK
ING. T. KLIMENT
ING. M. HANŽL

Zak. číslo
Datum
Stupeň

21-L113-001
02/2025
PDPS

Akce
I/16 MLADÁ BOLESLAV - MARTINOVICE

Počet formátů
Měřitko
Č. přílohy

8xA4
1 : 1000/100
Paré

Zhotovitel:

Valbek, spol. s r.o.
Vaňurova 505/17
460 07 Liberec 3

Příloha

PODÉLNÝ PROFIL

3