
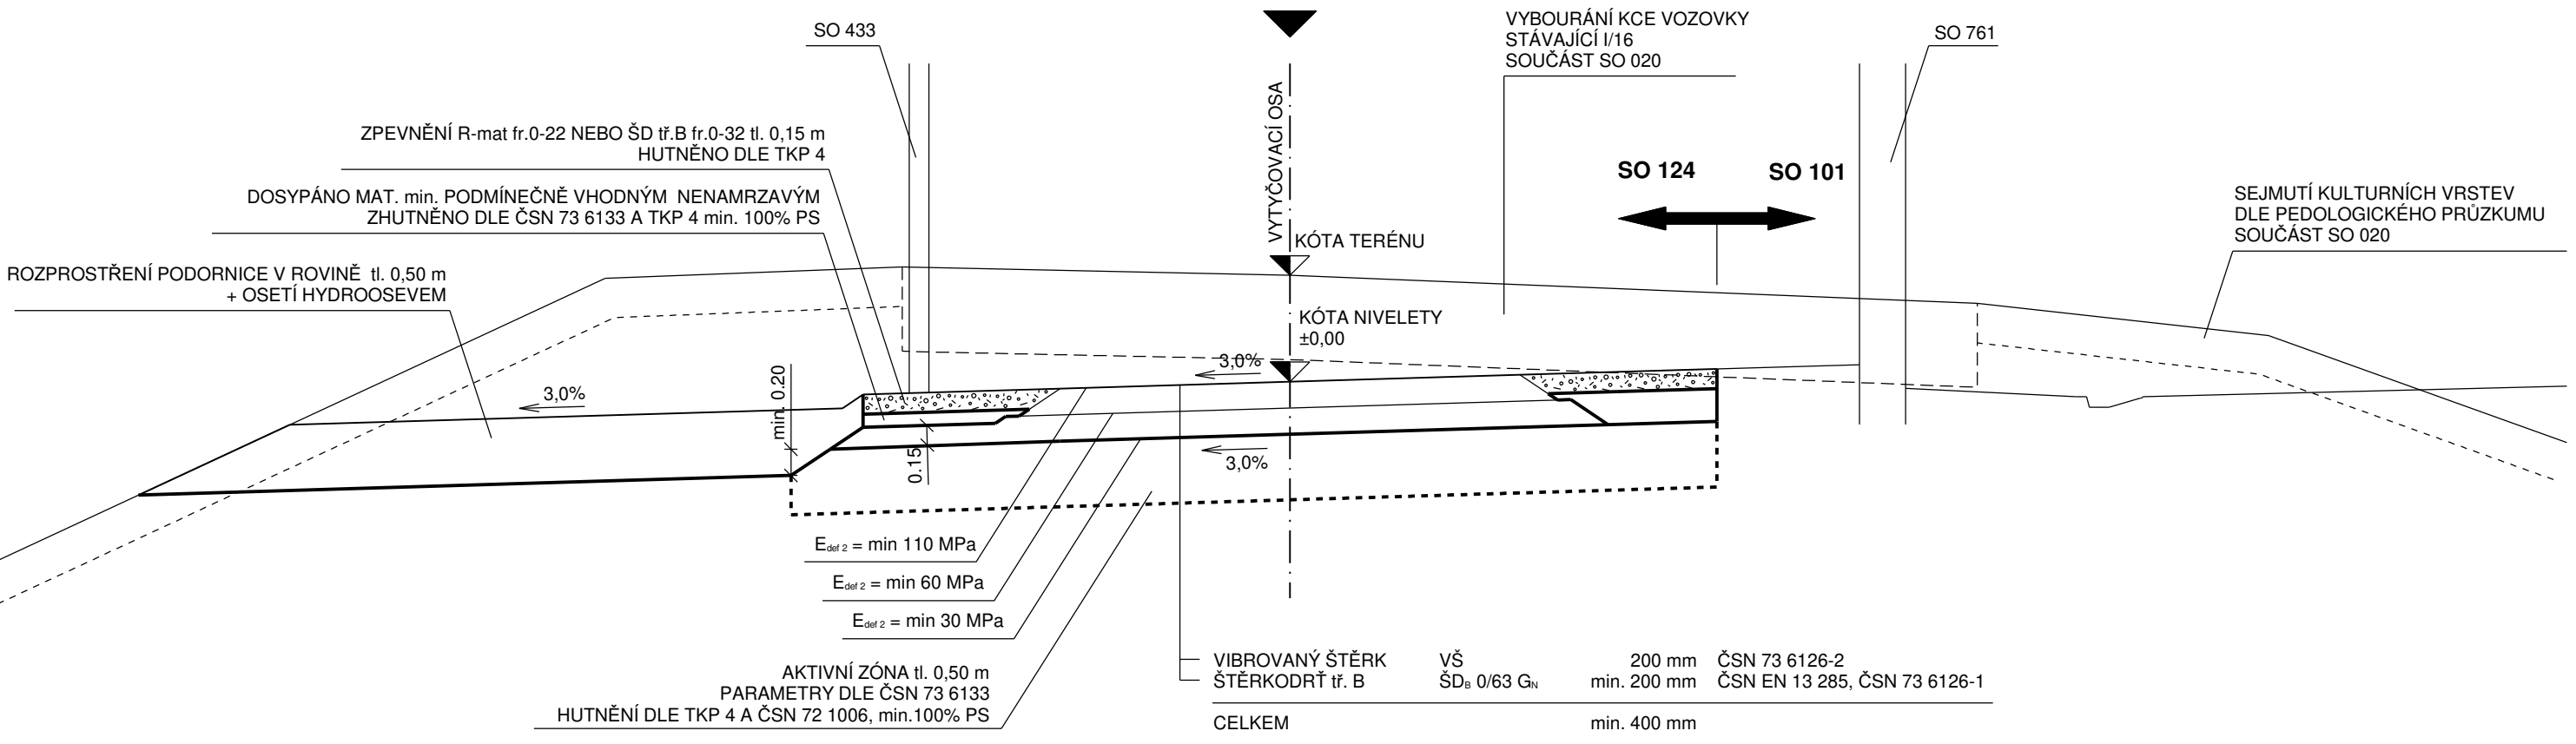
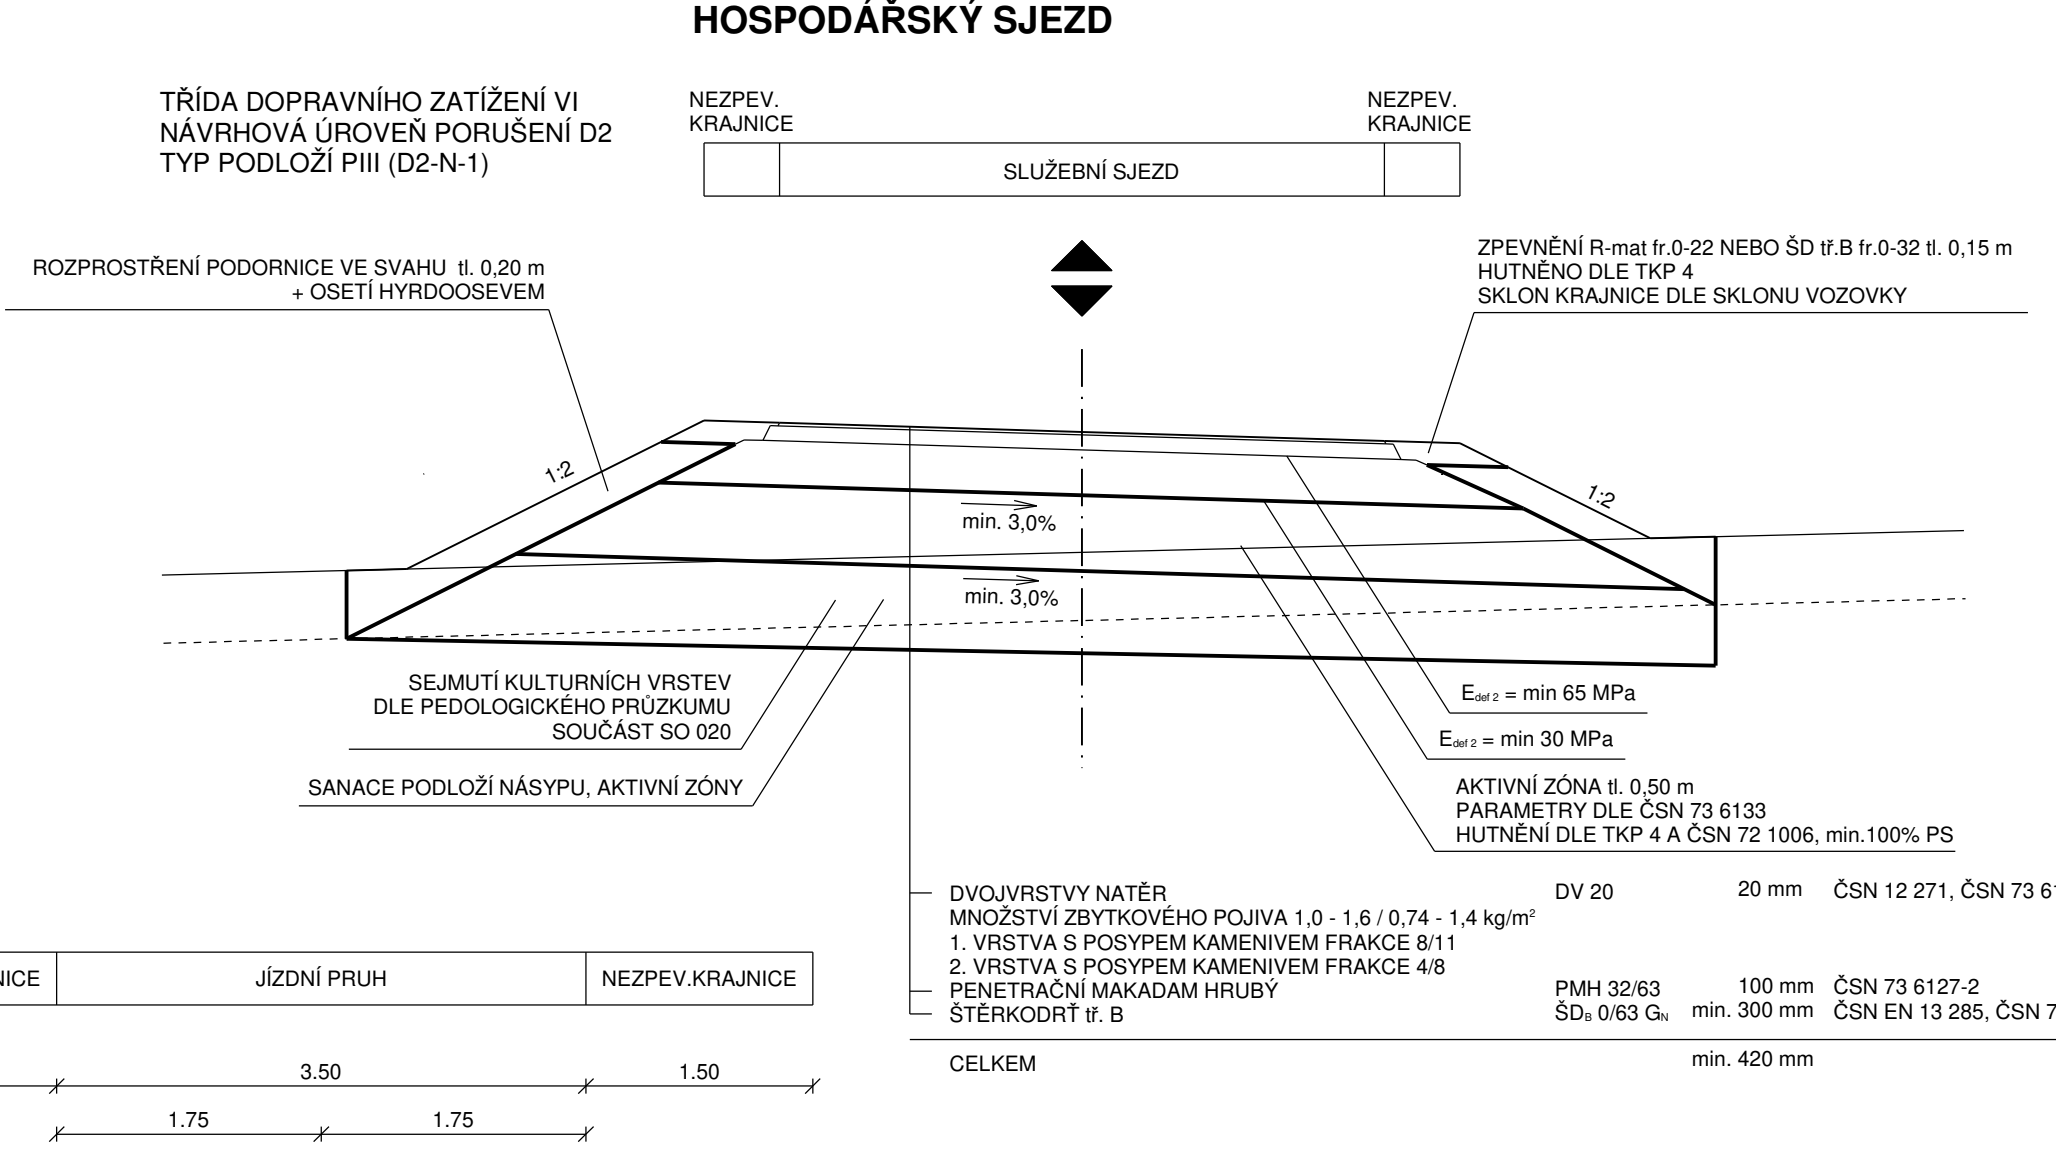
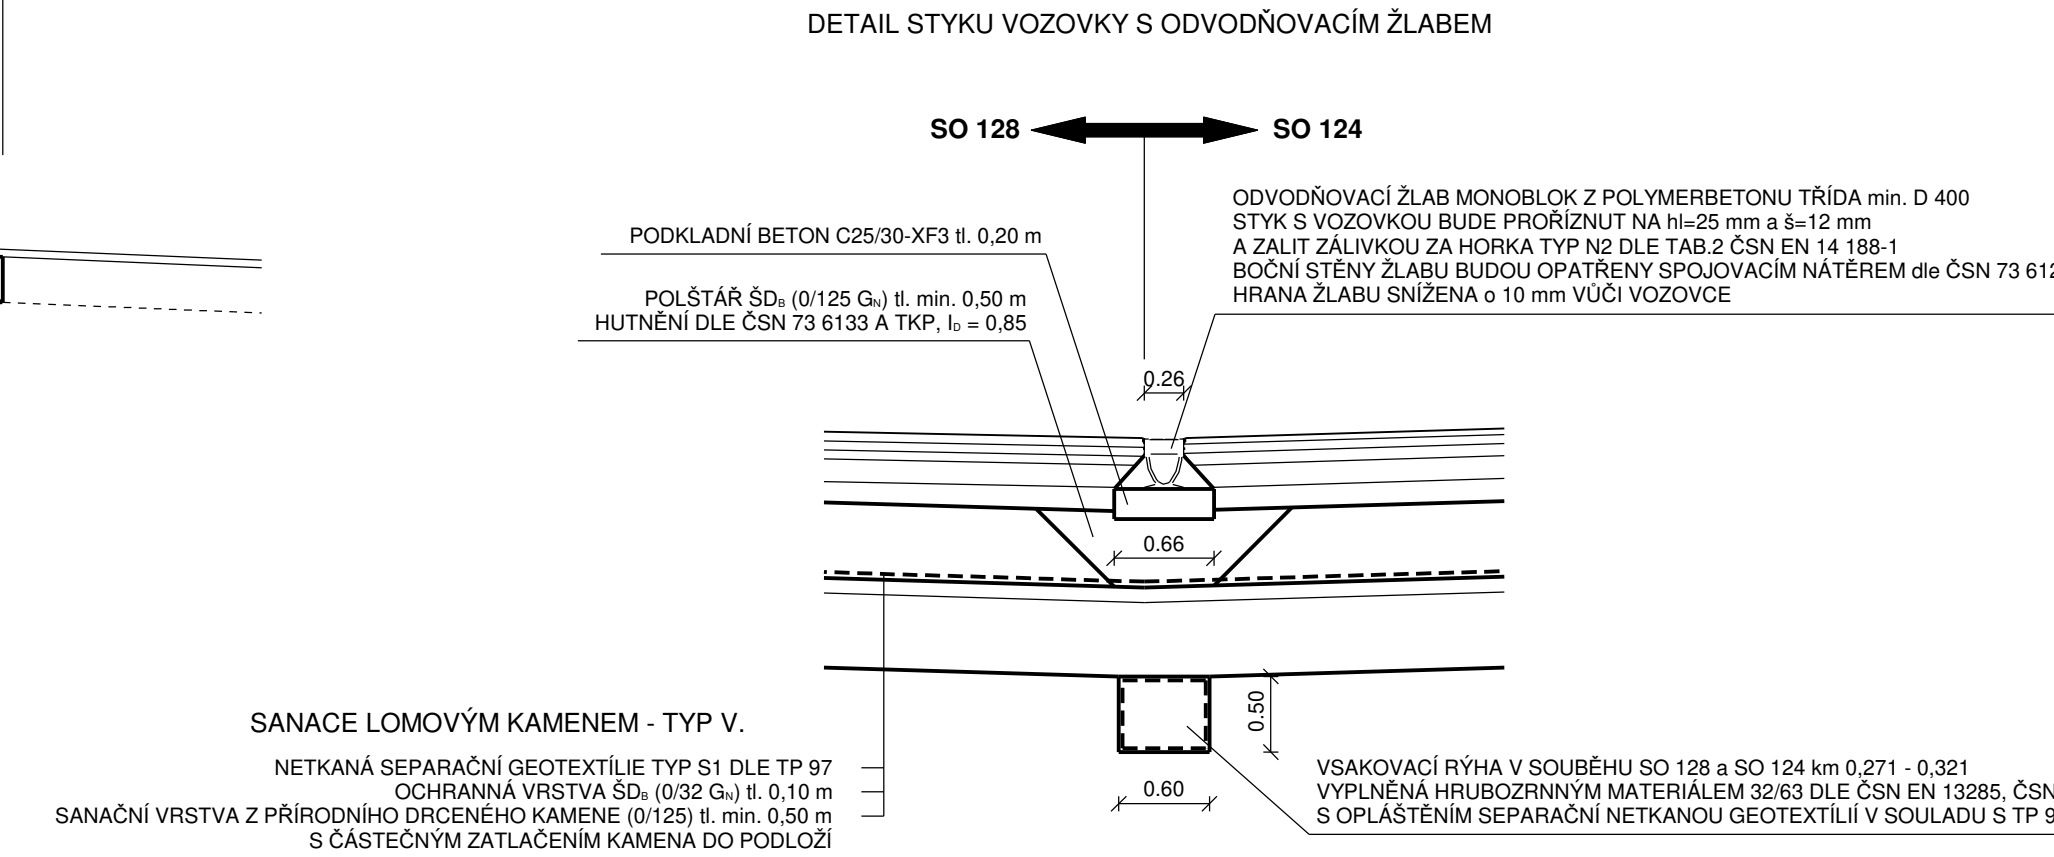
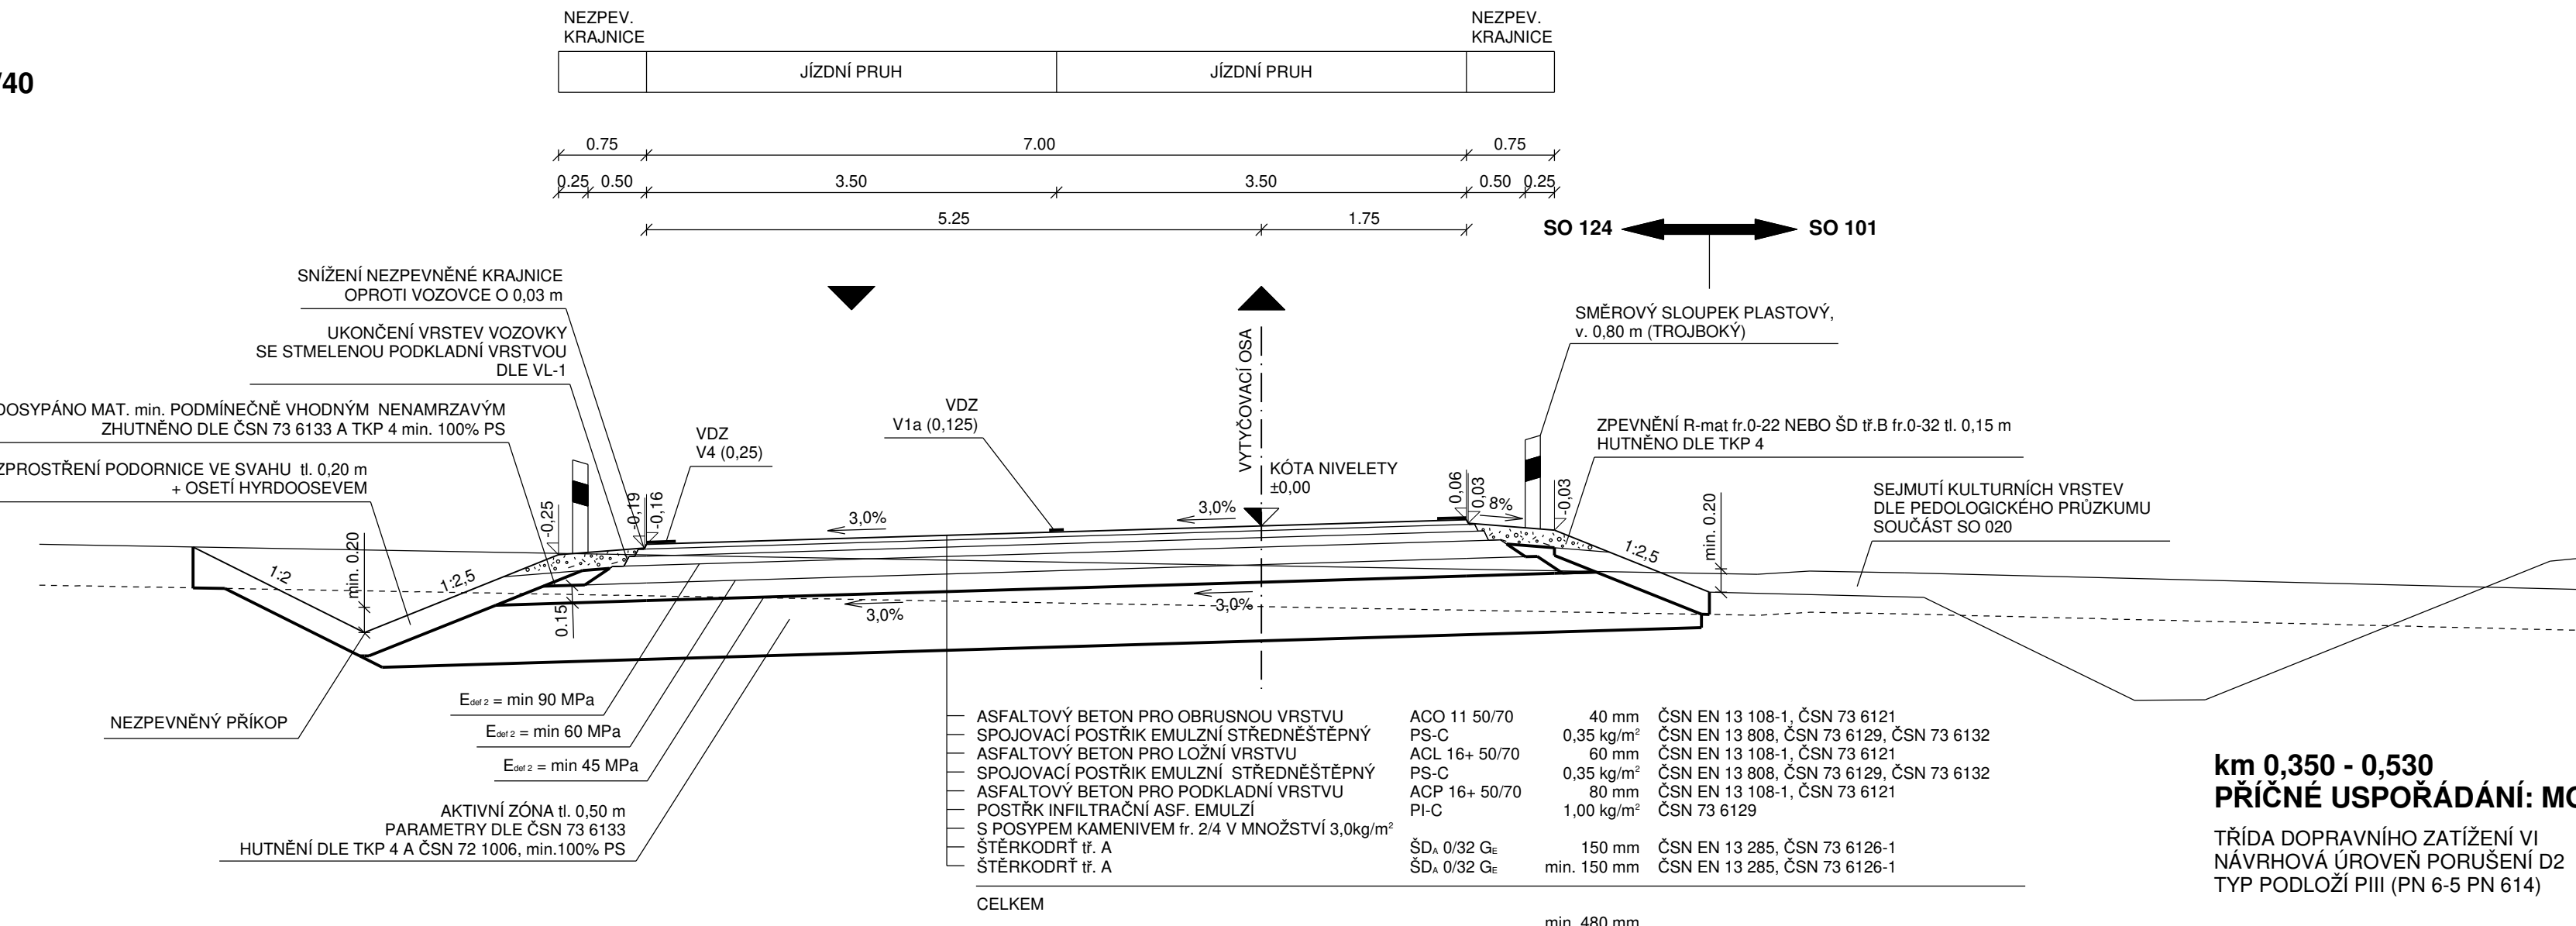


SO 124 - PŘELOŽKA MÍSTNÍ KOMUNIKACE km 7,340 - 7,700 VLEVO
VZOROVÉ PŘÍČNÉ ŘEZY, M 1 : 50

km 0,035 - 0,350
PŘÍČNÉ USPOŘÁDÁNÍ: MO2k -/8/40
TRÍDA DOPRAVNÍHO ZATÍŽENÍ IV
NÁVRHOVÁ ÚROVEŇ PORUŠENÍ D1
TYP PODLOŽÍ PIII (D1-A-2)

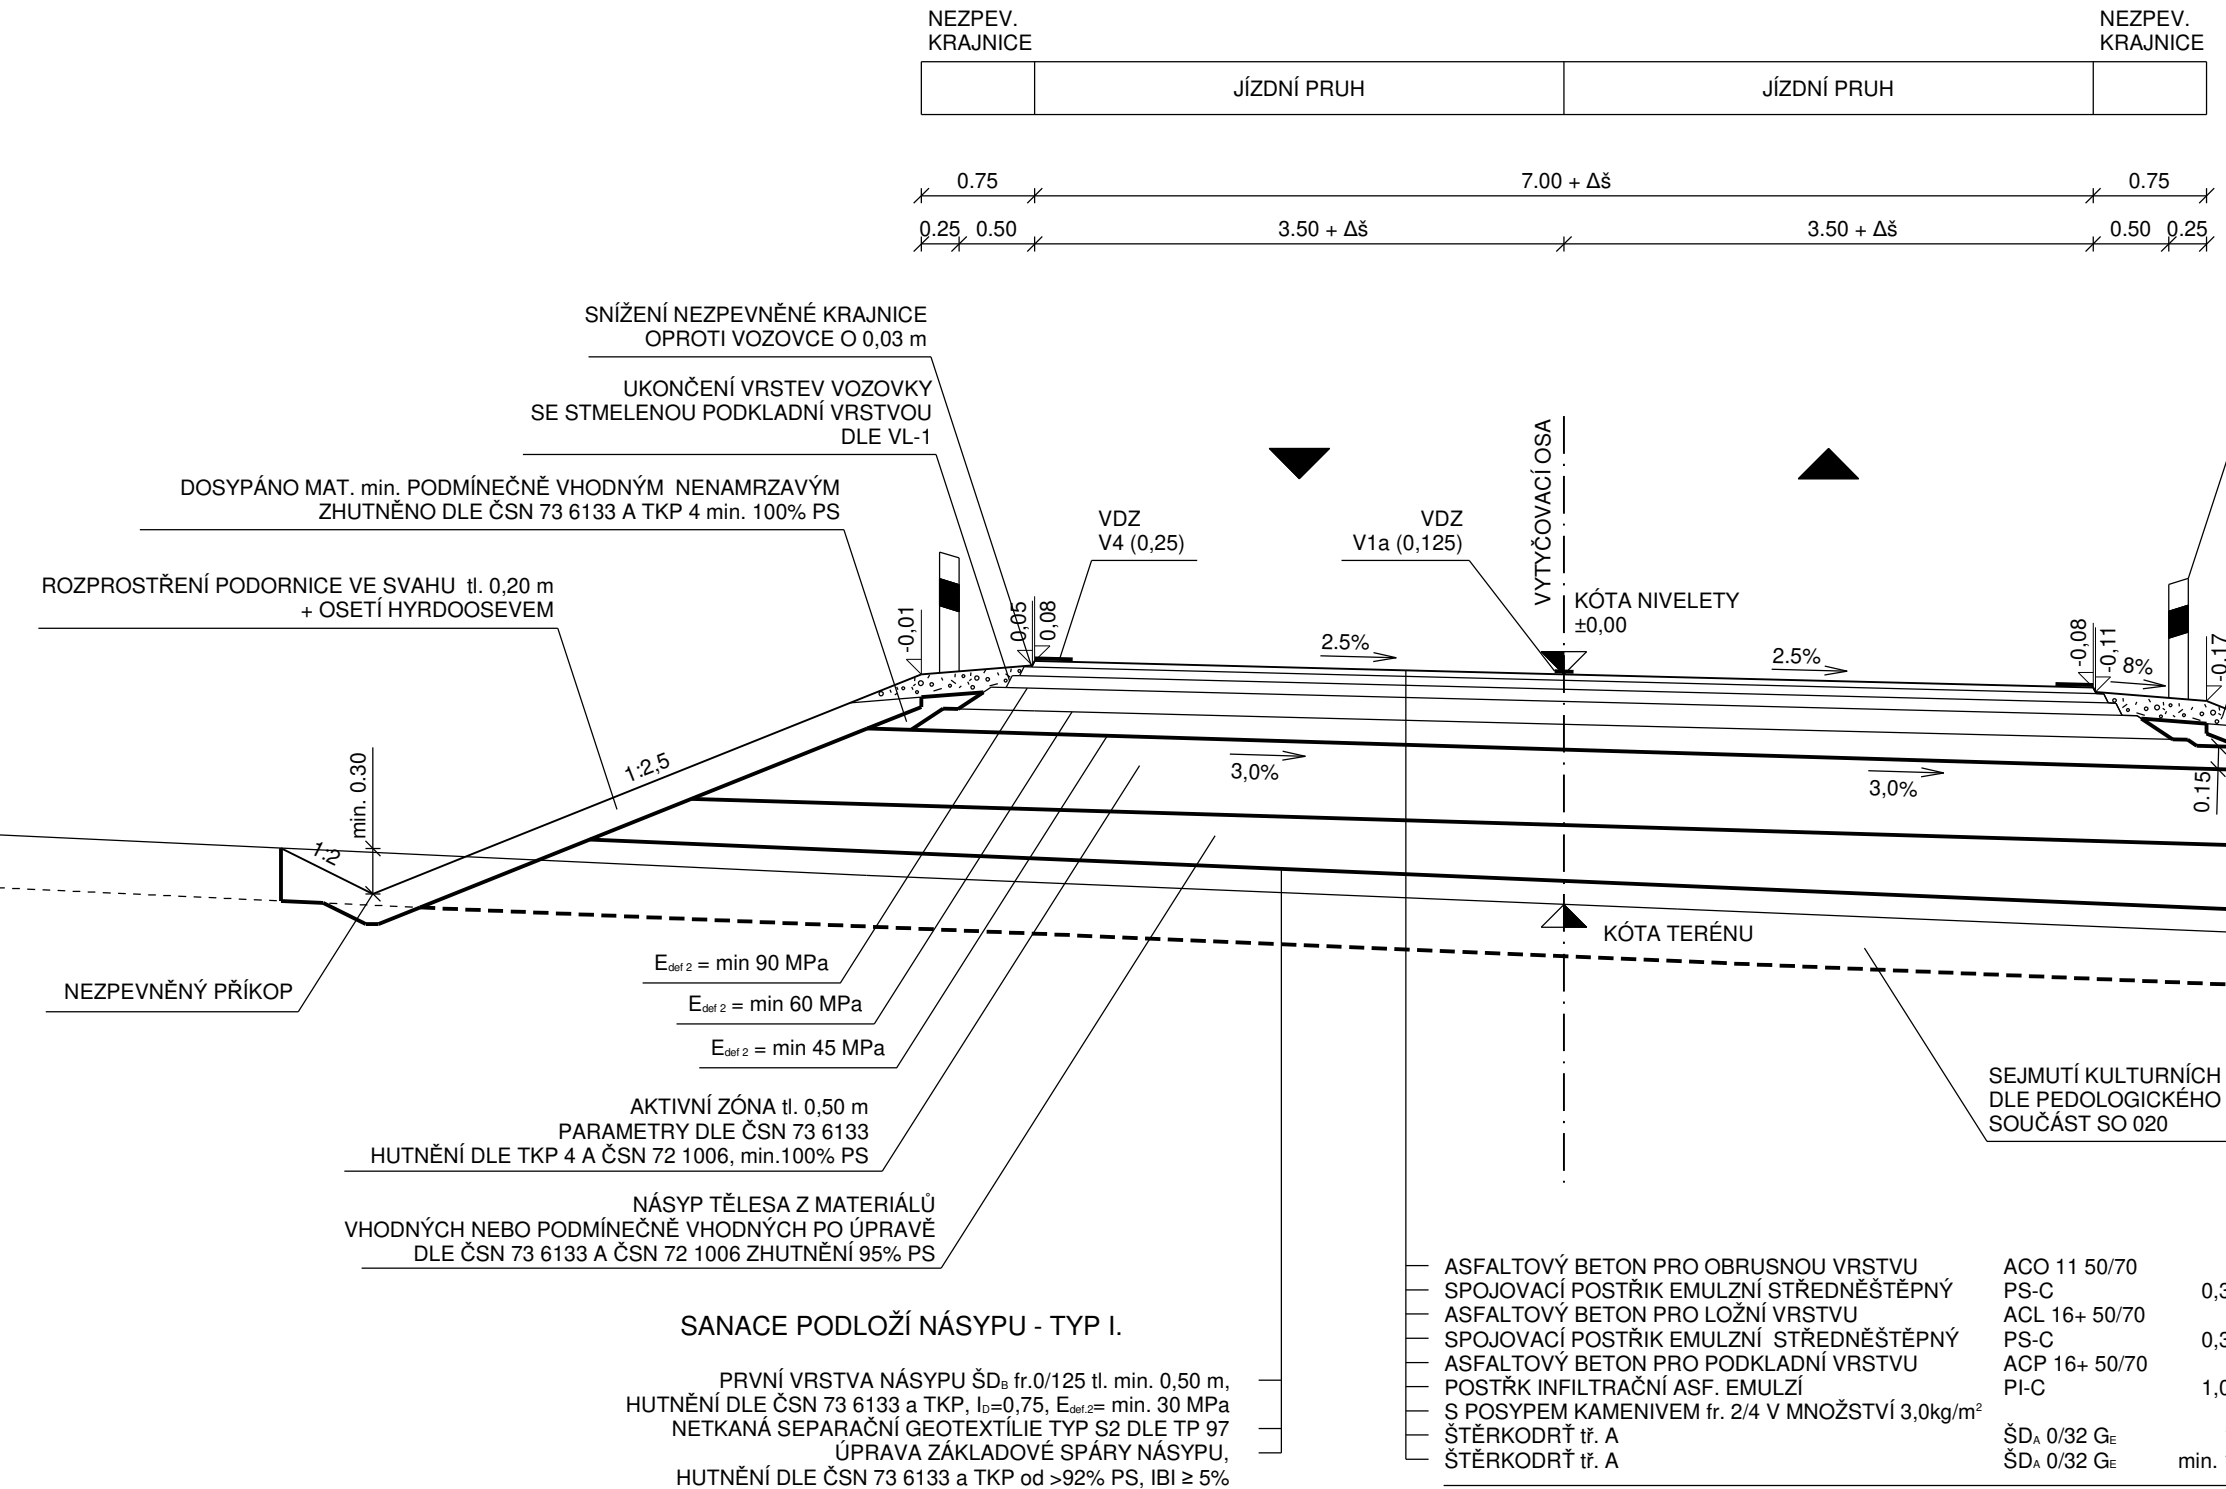

SO 124 Přeložka místní komunikace km 7,340 - 7,700 vlevo

Objednatel: Ředitelství silnic a dálnic s. p.
Čerčanská 2023/12, Krč, 140 00 Praha 4

Zhotovitel: Valbek, spol. s r.o.
Vaňurova 505/17
460 07 Liberec 3

Valbek	Vypracoval	M. KOŘÍNEK	Zak. číslo	21-L113-001
	Zodp. projektant	ING. T. KLIMENT	Datum	02/2025
	Tech. kontrola	ING. M. HANŽL	Stupeň	PDPS
	Akce	I/16 MLADÁ BOLESLAV - MARTINOVICE	Počet formátů	7 x A4
Zhotovitel: Valbek, spol. s r.o. Vaňurova 505/17 460 07 Liberec 3	Příloha	VZOROVÉ PŘÍČNÉ ŘEZY	Měřítko	1 : 50
			Č. přílohy	Paré