




**SO 124 - PŘELOŽKA MÍSTNÍ KOMUNIKACE km 7,340 - 7,700 VLEVO
PŘÍČNÉ ŘEZY km 0,040 - 0,200, M 1 : 100**

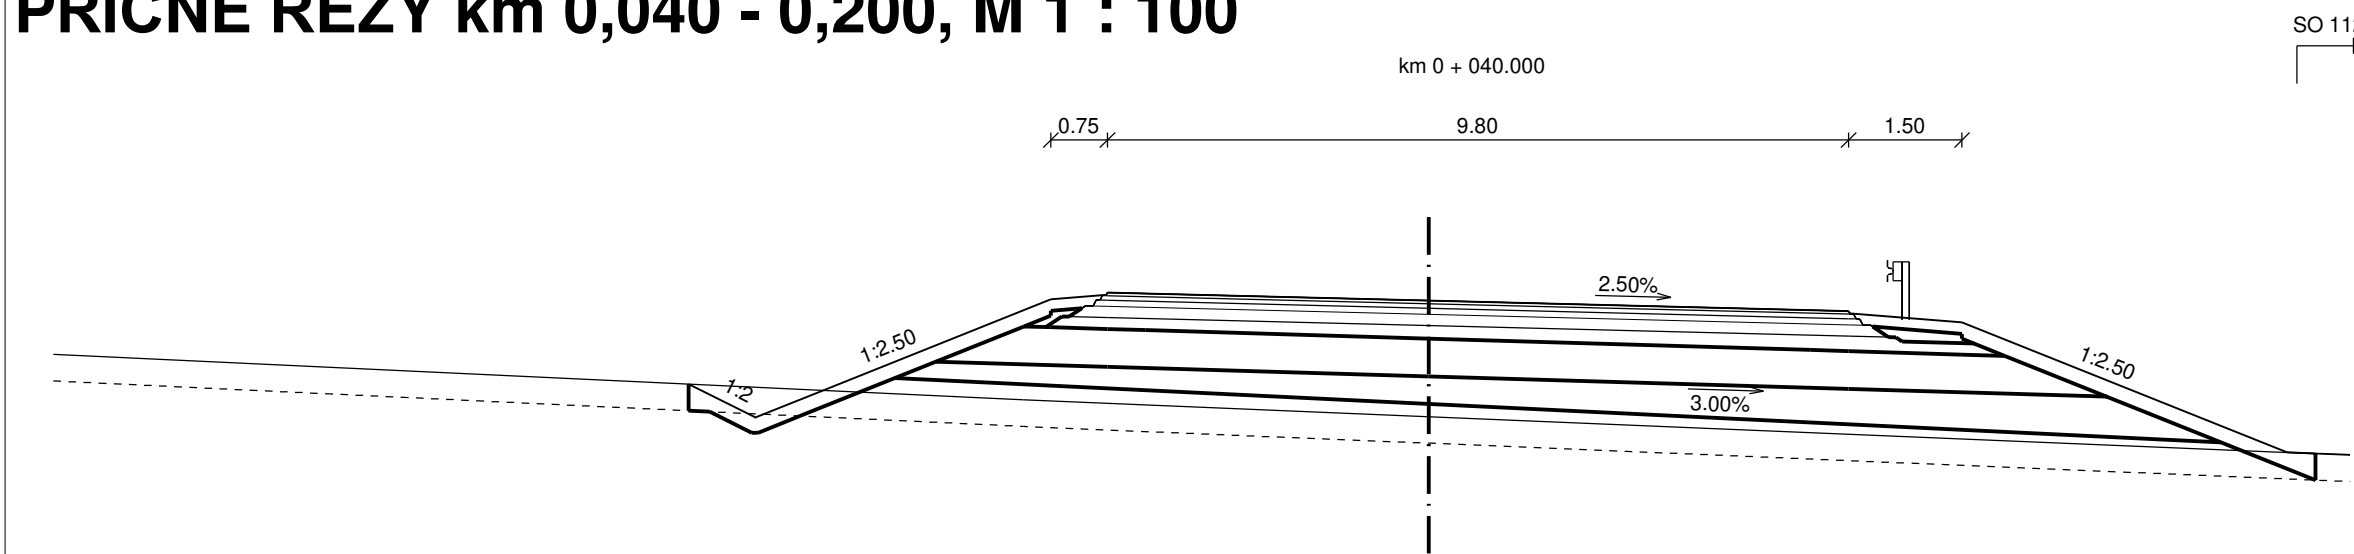



PROJEKTOVANÝ STAV	-9.79 226.86	-5.00 227.88	0.00 227.86	5.05 227.83	7.05 227.67	11.35 226.05
ODSAZENÍ OD OSY	-9.91 226.42	-4.27 228.04	0.00 227.86	5.55 227.82	7.55 227.70	11.73 225.94
STÁVAJÍCÍ TERÉN	-9.01 226.77	-4.25 228.01	-3.75 228.05	5.57 227.79		
ODSAZENÍ OD OSY		-5.36 226.85	0.00 226.43			

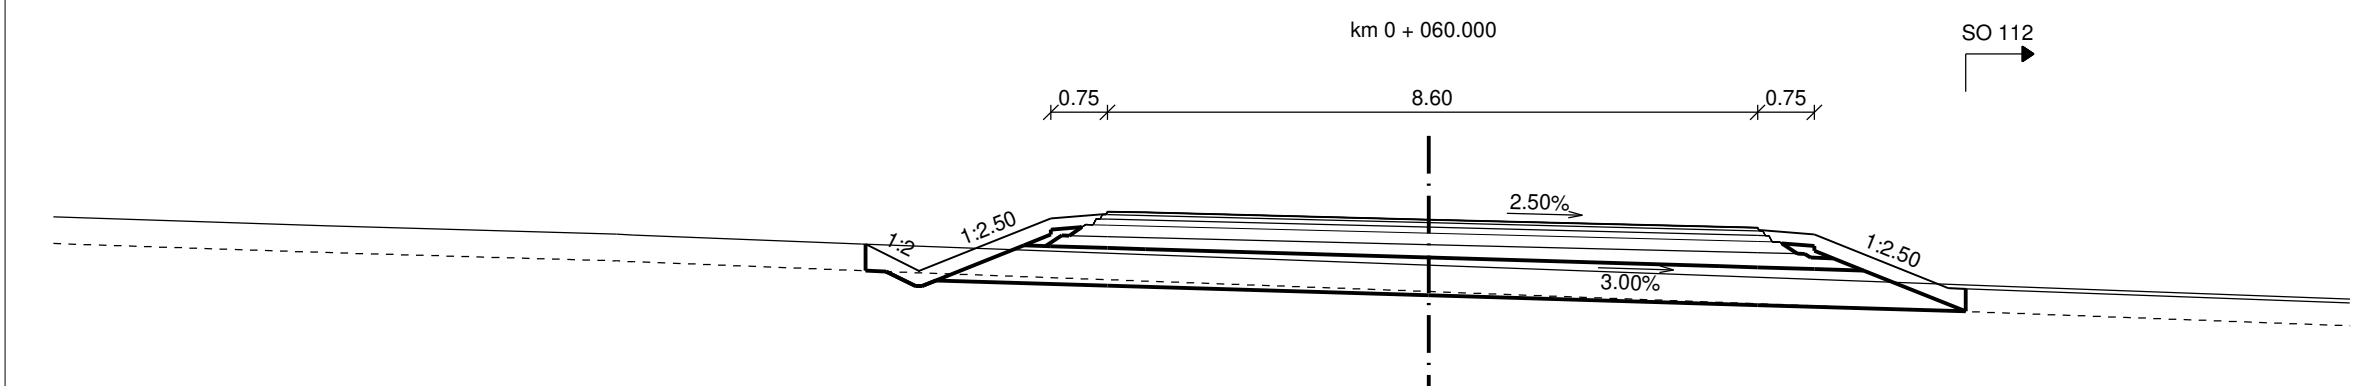


		S. R. 223 m
PROJEKTOVANÝ STAV		-7,45 226,47
ODSAZENÍ OD OSY		-6,74 226,11 -5,99 226,41 -5,00 226,81 -4,27 226,87 -4,28 226,90 -3,75 226,69
STÁVAJÍCÍ TERÉN	-10,74 226,60 -10,59 226,93	
ODSAZENÍ OD OSY		0,00 226,19 3,85 226,70 4,35 226,69 4,37 226,65 5,10 226,60 6,69 226,69 7,10 225,93

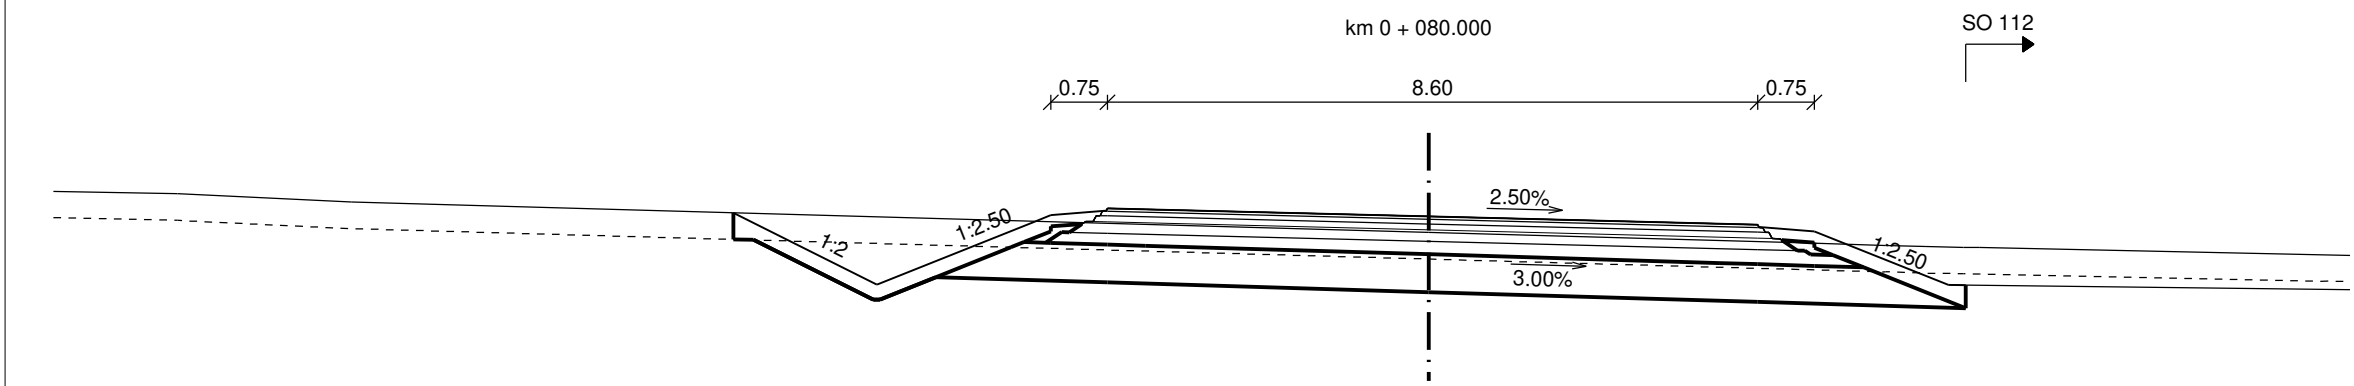


															S. R. 222 m														
PROJEKTOVANÝ STAV																													
ODSAZENÍ OD OSY																													

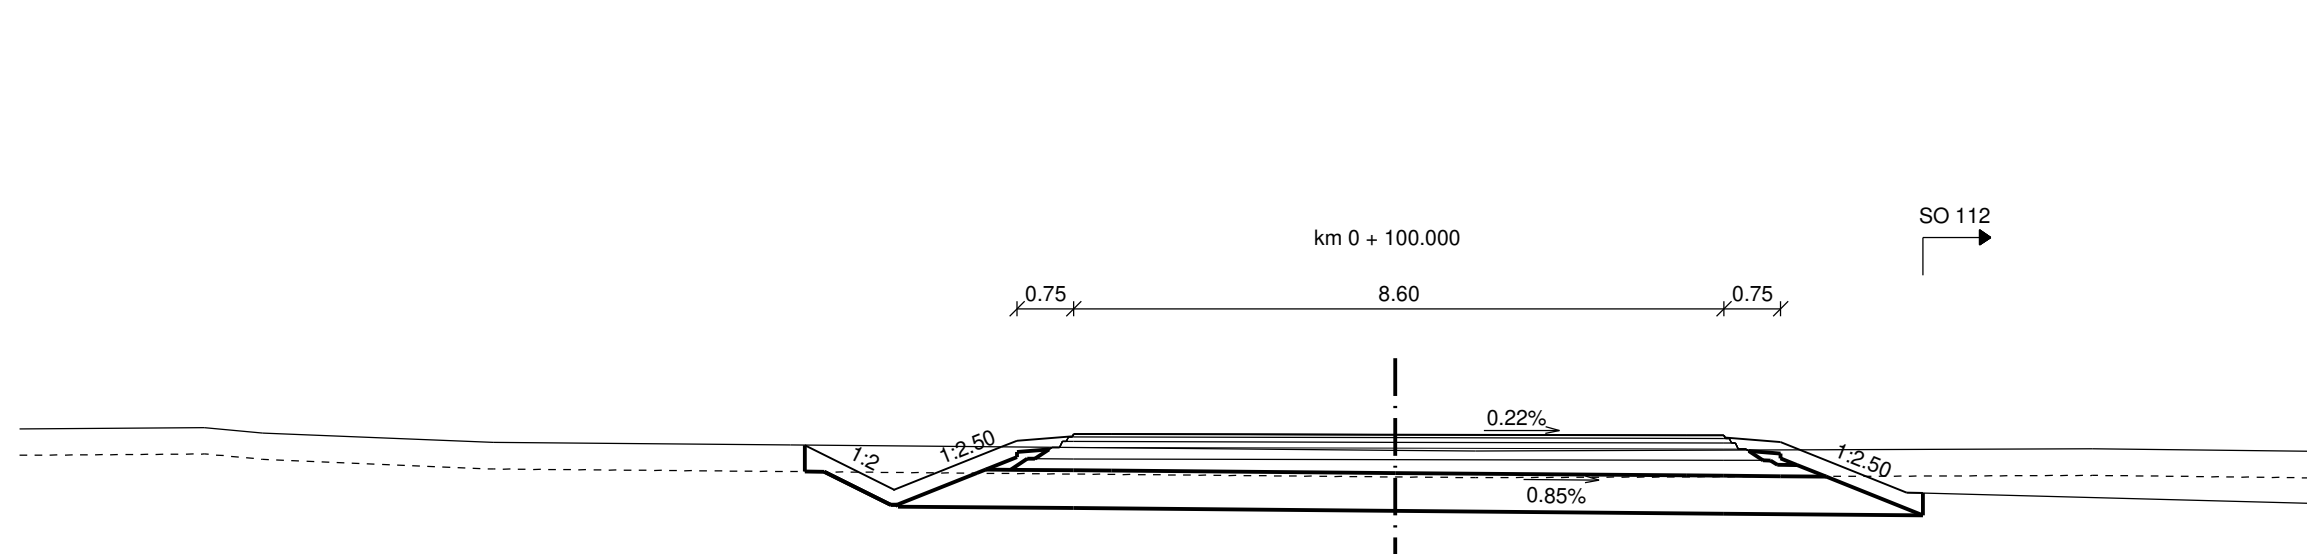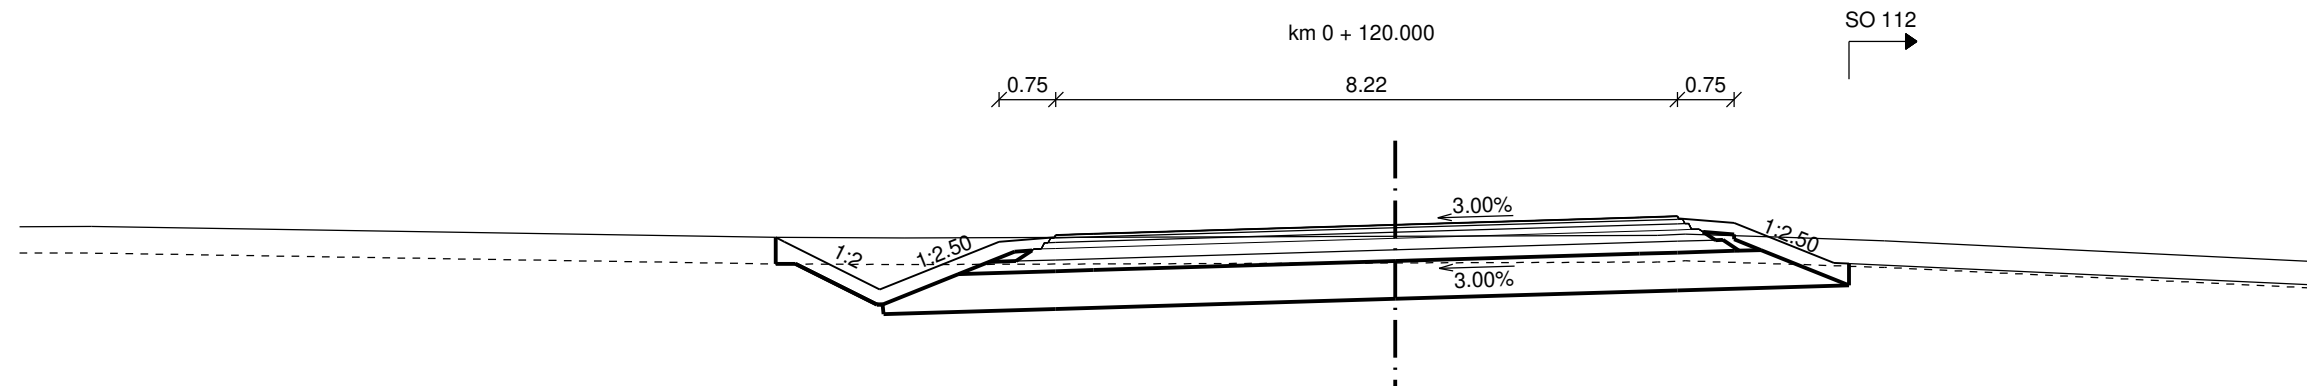[illegible]


		S. R. 221 m	
PROJEKTOVANÝ STAV		-8.19 224.56 -8.08 224.50	-5.62 223.87 -5.24 224.50 -4.50 224.56 -4.48 224.59 -3.98 224.61
ODSAZENÍ OD OSY			0.00 224.73
STÁVAJÍCÍ TERÉN		-8.19 224.56	3.23 224.82 3.73 224.84 3.75 224.81
ODSAZENÍ OD OSY		-6.48 224.55	4.48 224.75 5.17 224.56 6.48 224.51

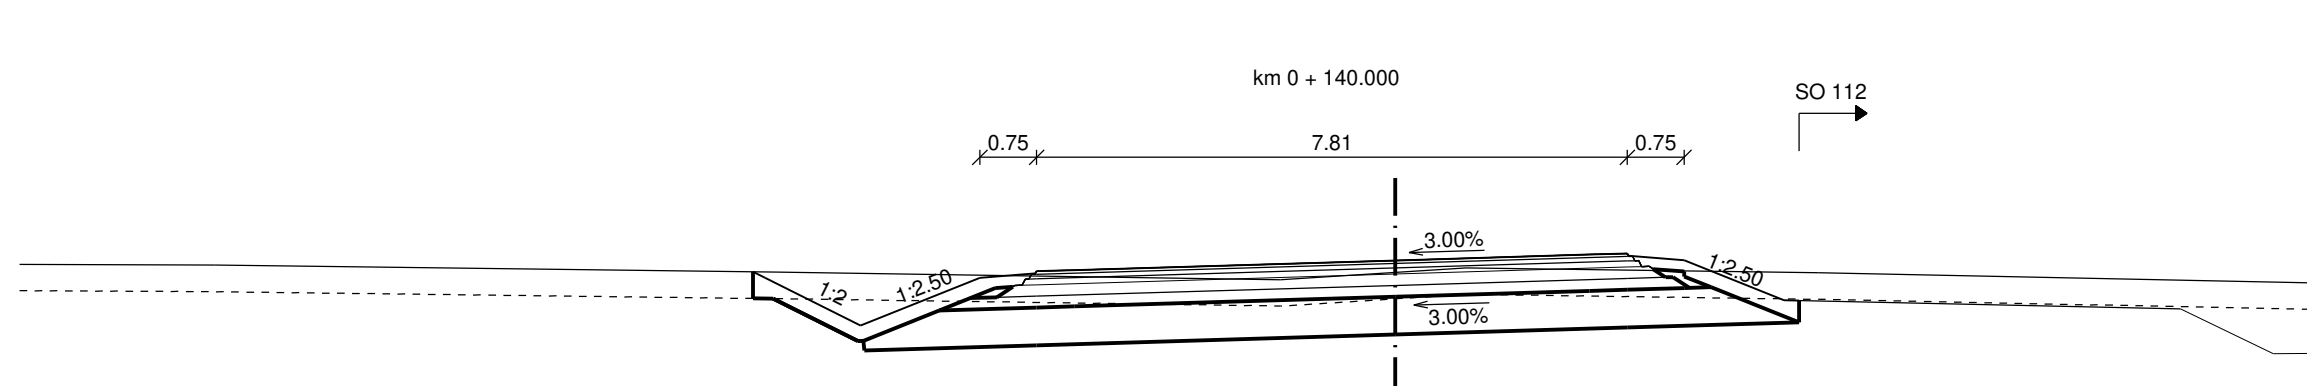


		S. R. 221 m	
PROJEKTOVANÝ STAV		-8,49 224,12 -8,33 224,04	-7,07 223,41
ODSAZENÍ OD OSY		-5,49 224,04 -4,76 224,10 -4,74 224,13 -4,24 224,15	0,00 224,28
			2,57 224,35 3,07 224,37 3,09 224,34 3,82 224,28
			5,15 223,75
STÁVAJÍCÍ TERÉN		-8,19 224,12	
ODSAZENÍ OD OSY			-1,52 224,02 0,00 224,12 0,94 224,18
			5,60 224,11

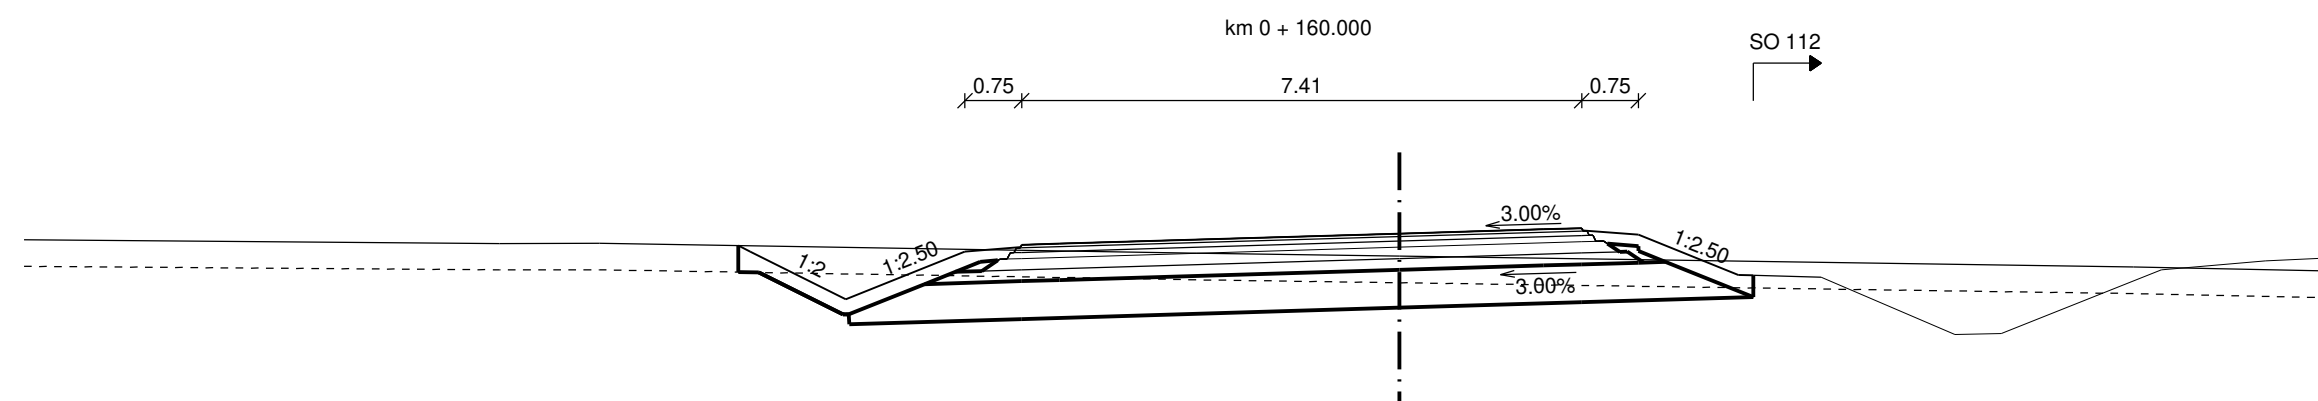

S. R. 220 m PROJEKTOVANÝ STAV ODSAZENÍ OD OSY		-8.74 223.67 -8.59 223.59 -7.32 222.96 -5.75 223.59 -5.01 223.65 -5.00 223.68 -4.50 223.69	0.00 223.63 1.91 223.98 2.41 223.90 2.43 223.97 3.16 223.91 4.48 223.28
STÁVAJÍCÍ TERÉN ODSAZENÍ OD OSY		-11.90 223.69 -10.58 223.70 -2.68 223.57 0.00 223.53 9.71 223.38	

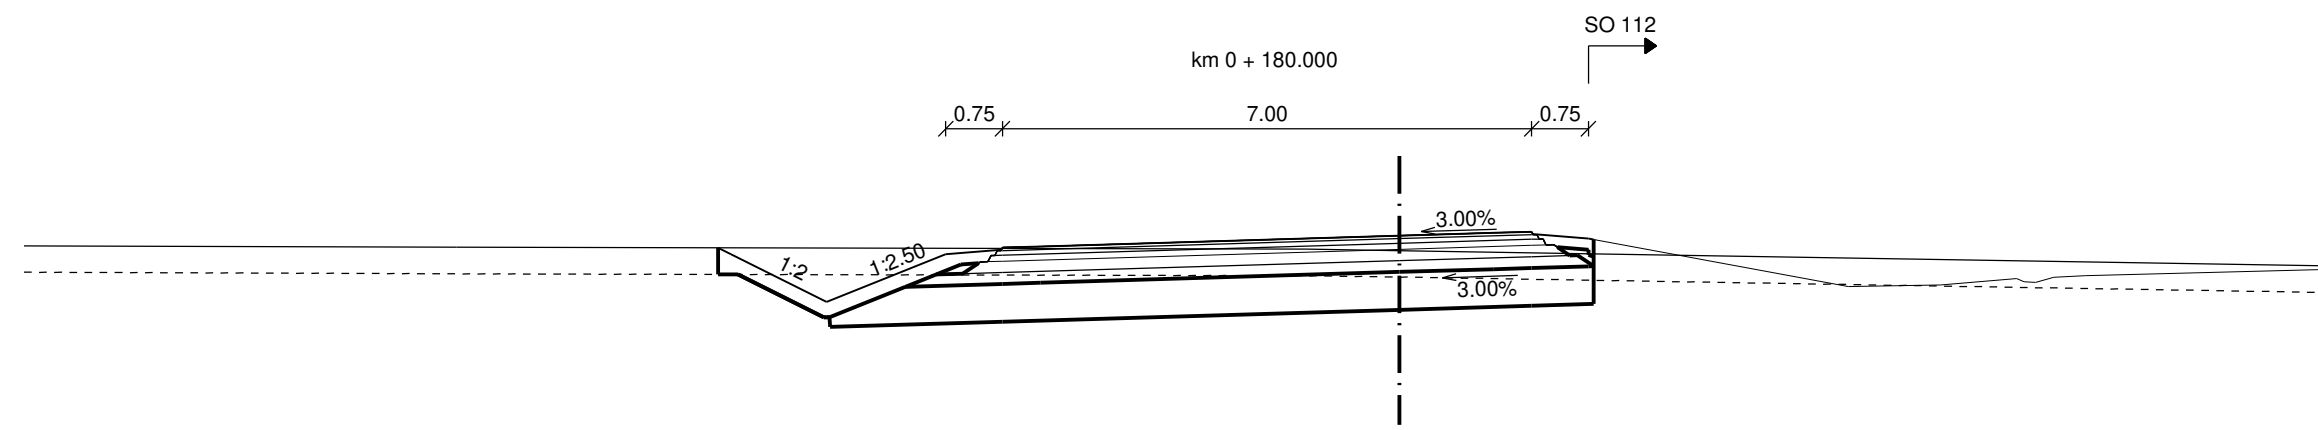

		S. R. 219 m			
PROJEKTOVANÝ STAV	-9,01 223,25 -8,84 223,17	-7,58 222,64	-6,00 223,17 -5,27 223,23 -5,25 223,26 -4,75 223,27	0,00 223,41	1,25 223,45 1,75 223,47 1,77 223,44 2,50 223,38
ODSAZENÍ OD OSY					
STÁVAJÍCÍ TERÉN	-12,47 223,26			-1,22 223,24	
ODSAZENÍ OD OSY				0,00 223,22	

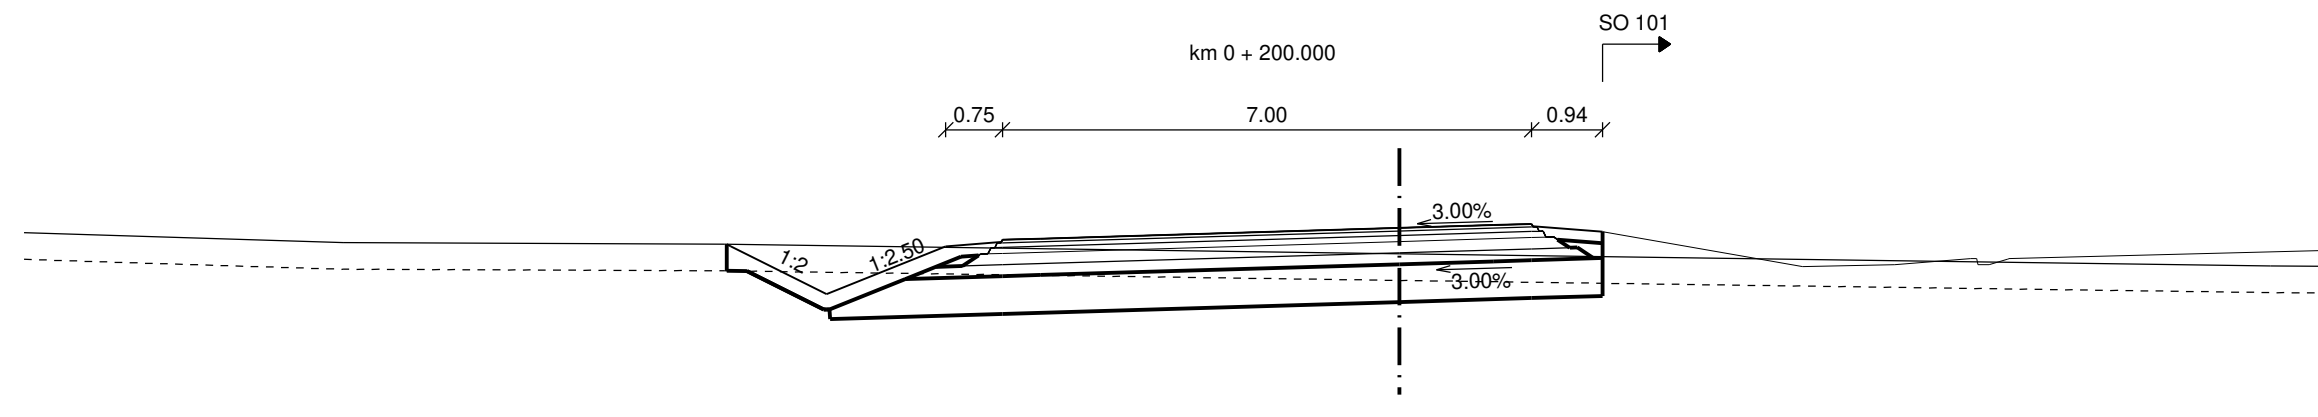

S. R. 219 m PROJEKTOVANÝ STAV ODSAZENÍ OD OSY		-8,90 222,90 -8,84 222,87 -7,58 222,24 -6,00 222,07 -5,27 222,03 -5,25 222,06 -4,75 222,97 0,00 223,12 1,25 223,15 1,75 223,17 1,77 223,14 2,69 223,06
STÁVAJÍCÍ TERÉN ODSAZENÍ OD OSY		-8,92 222,90 0,00 222,77 11,52 222,61

Výškový systém Bpv

SO 124 Přeložka místní komunikace km 7,340 - 7,700 vlevo



Ředitelství silnic a dálnic s. p.
Čerčanská 2023/12, Krč, 140 00 Praha 4

Zhotovitel:



Valbek, spol. s r.o.
Vaňurova 505/17
460 07 Liberec 3

HIP:

ING. T. KLIMENT



Valbek, spol. s r. o.

Zhotovitel:
Vaišbek, spol. s r. o.
Vaišurova 505/17
460 07 Liberec 3

Příloha

PŘÍČNÉ ŘEZY km 0,040 - 0,200

5.1

Paré