SO 124 PŘELOŽKA MÍSTNÍ KOMUNIKACE km 7,340 - 7,700 VLEVO
PŘÍČNÉ ŘEZY, km 0,220 - 0,380, M 1 : 100

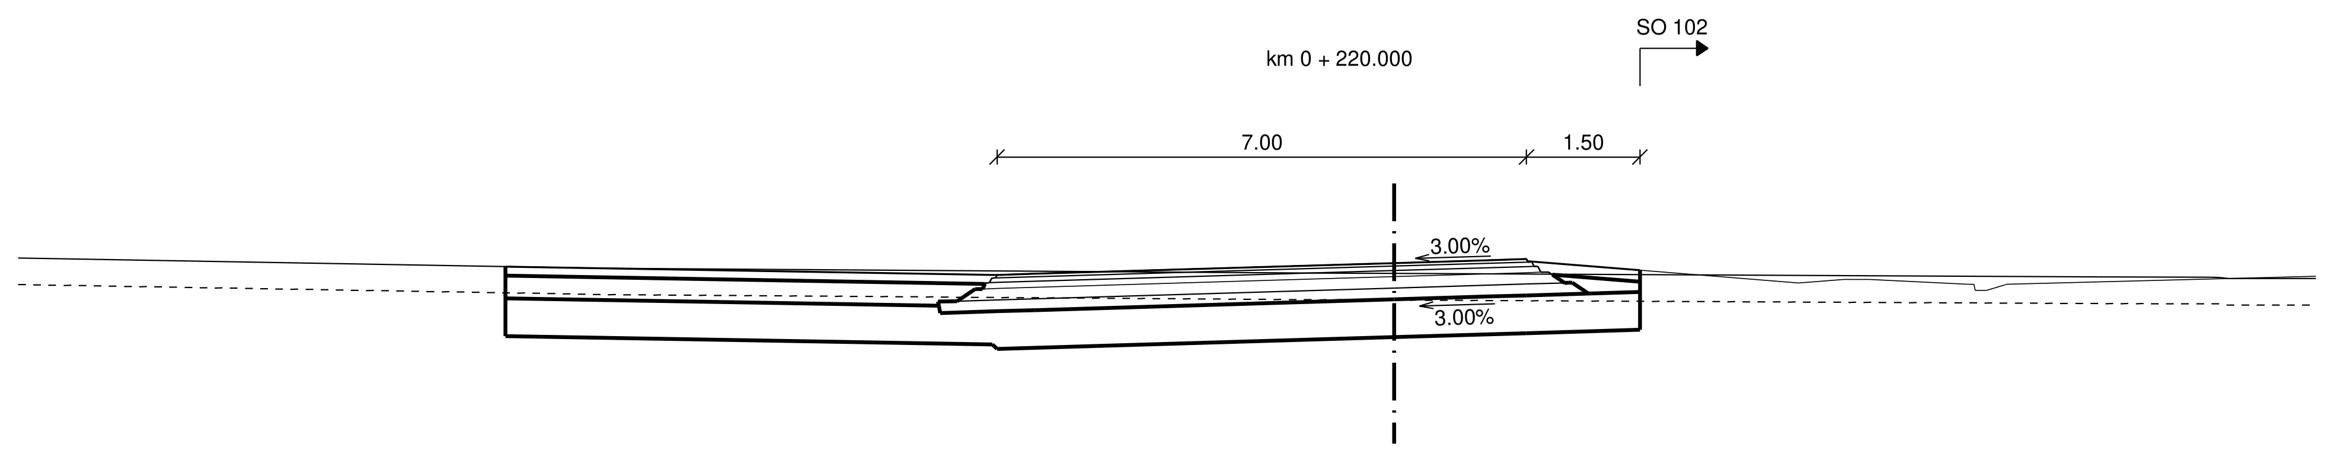

S. R. 219 m

ODSAZENÍ OD OSY	PROJEKTOVANÝ STAV
-17.75	222.88
-5.25	222.77
-4.75	222.79
0.00	222.93
1.25	222.97
1.75	222.98
1.77	222.95
3.25	222.83

ODSAZENÍ OD OSY	STÁVAJÍCÍ TERÉN
-10.47	222.86
-1.11	222.80
0.00	222.79
9.32	222.75
10.79	222.74
10.93	222.74
11.03	222.72

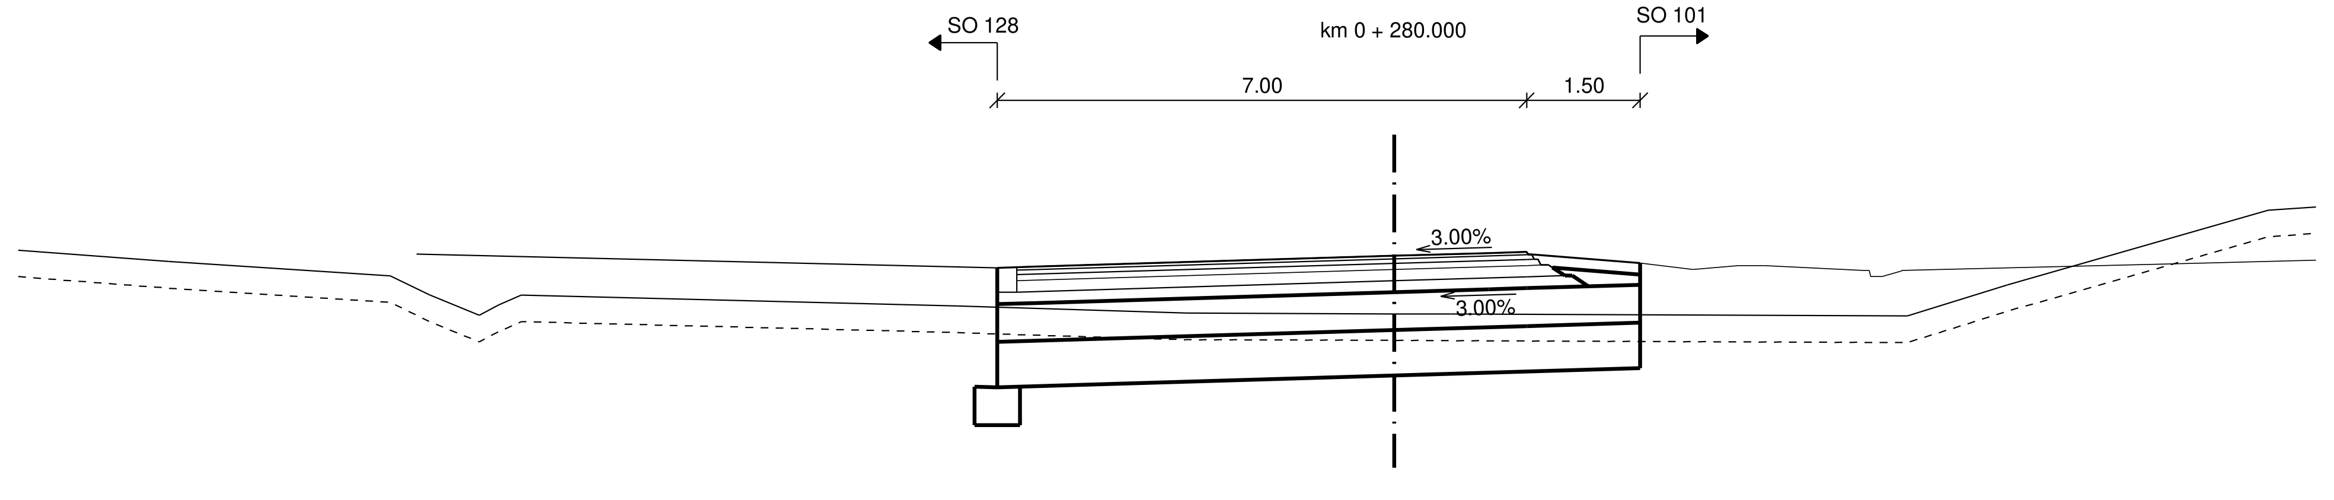

S. R. 218 m

ODSAZENÍ OD OSY	PROJEKTOVANÝ STAV
-5.25	222.49
-4.75	222.50
0.00	222.65
1.25	222.68
1.75	222.70
1.77	222.67
3.25	222.55

ODSAZENÍ OD OSY	STÁVAJÍCÍ TERÉN
-12.76	222.13
-12.10	221.86
-11.84	222.00
-11.54	222.13
-5.77	221.98
-2.75	221.89
0.00	221.88
0.75	221.88
6.78	221.85
8.11	222.26
11.56	223.25

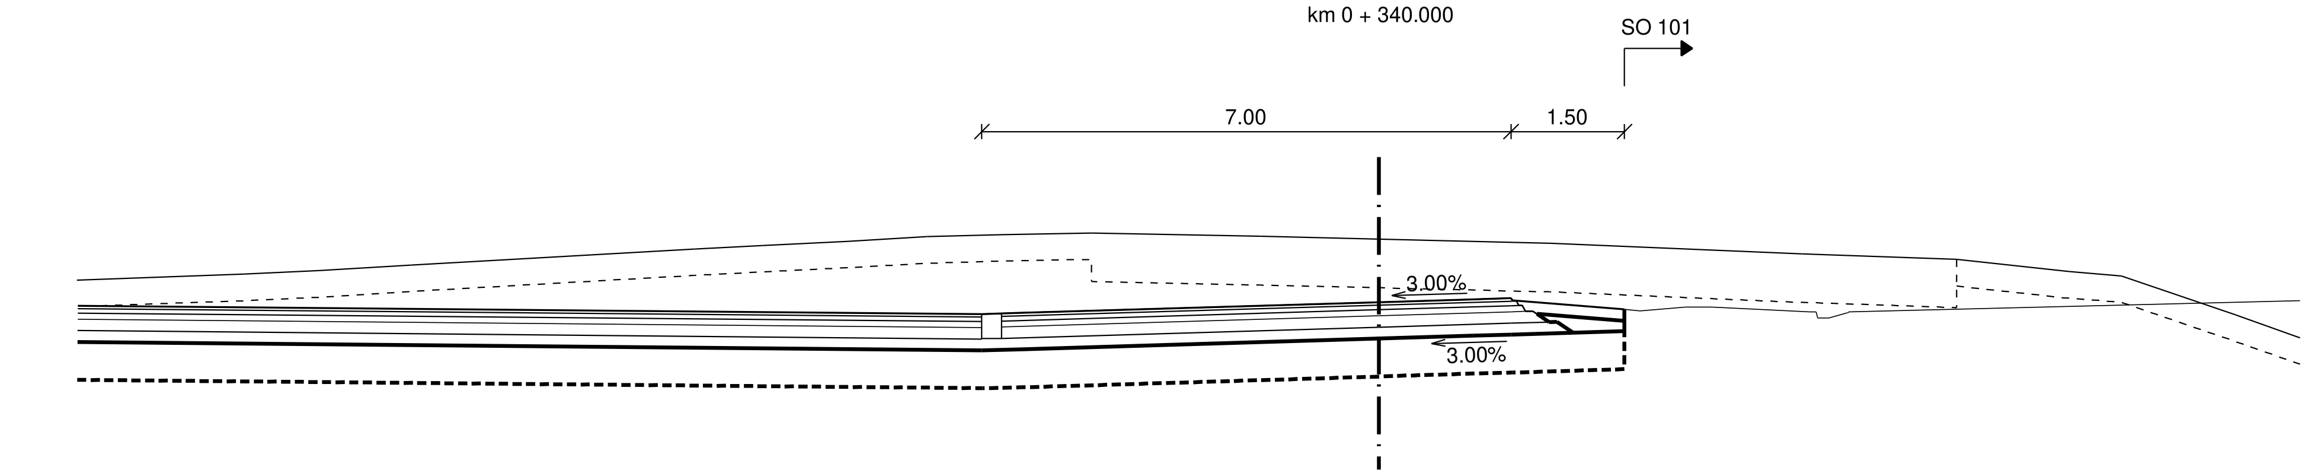

S. R. 219 m

ODSAZENÍ OD OSY	PROJEKTOVANÝ STAV
-5.25	222.36
-4.75	222.38
0.00	222.52
1.25	222.56
1.75	222.57
1.77	222.54
3.25	222.42

ODSAZENÍ OD OSY	STÁVAJÍCÍ TERÉN
-12.80	223.01
-9.05	223.22
-8.15	223.27
-7.03	223.32
-5.97	223.39
-4.96	223.41
-3.80	223.43
-1.56	223.39
0.00	223.35
2.28	223.30
5.60	223.16
7.64	223.09
9.13	222.92
9.82	222.87
11.33	222.35

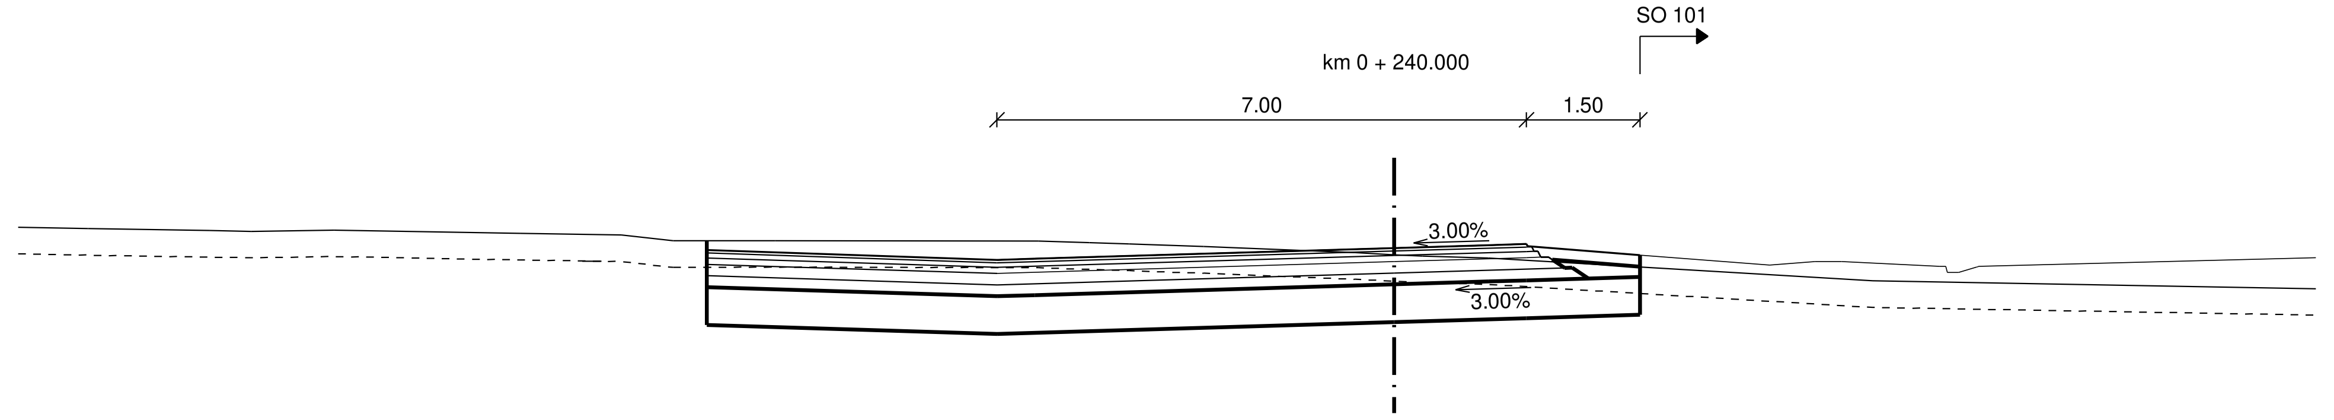

S. R. 219 m

ODSAZENÍ OD OSY	PROJEKTOVANÝ STAV
-10.74	223.01
-10.11	222.69
-9.09	222.80
-5.25	222.67
-4.75	222.69
0.00	222.83
1.25	222.87
1.75	222.88
1.77	222.85
3.25	222.73

ODSAZENÍ OD OSY	STÁVAJÍCÍ TERÉN
-11.55	223.02
-10.22	223.00
-9.53	222.92
-8.18	222.93
-4.71	222.92
-4.03	222.90
-3.51	222.88
-2.52	222.85
-0.52	222.77
0.00	222.74
0.38	222.72
1.25	222.70
6.33	222.39

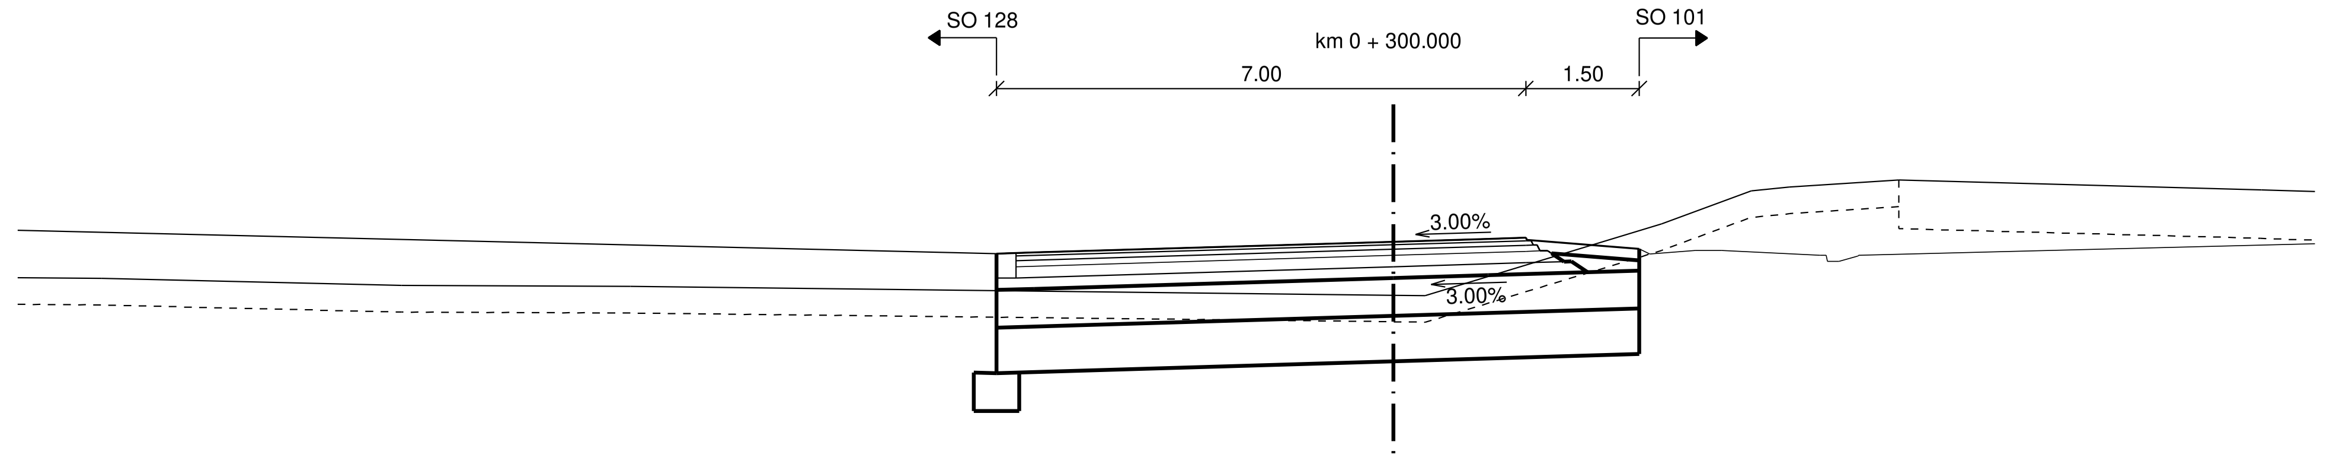

S. R. 218 m

ODSAZENÍ OD OSY	PROJEKTOVANÝ STAV
-5.25	222.43
-4.75	222.44
0.00	222.58
1.25	222.62
1.75	222.64
1.77	222.61
3.25	222.49

ODSAZENÍ OD OSY	STÁVAJÍCÍ TERÉN
-10.09	222.00
0.00	221.88
0.42	221.87
3.54	222.82
4.73	223.26
5.24	223.31
6.68	223.40
11.48	223.27

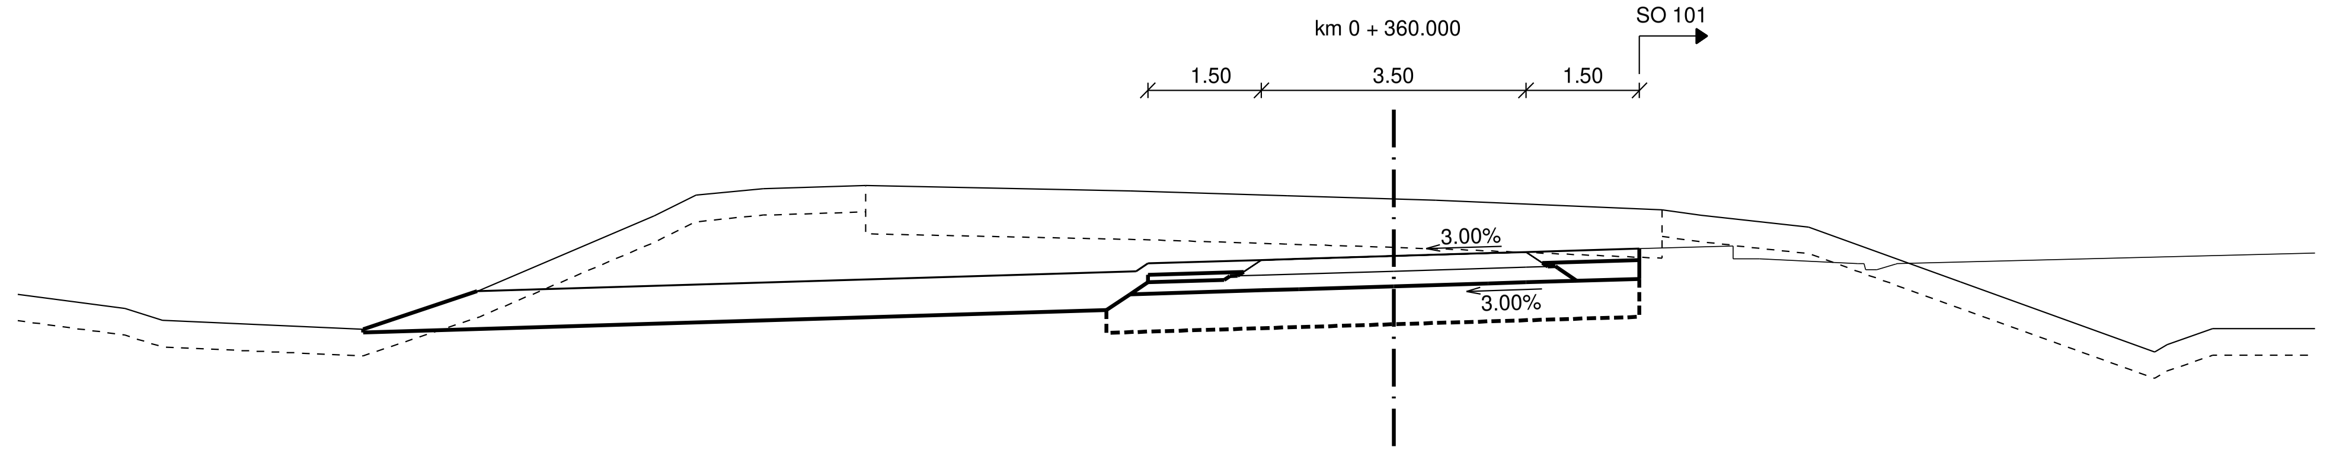

S. R. 218 m

ODSAZENÍ OD OSY	PROJEKTOVANÝ STAV
-12.12	222.06
-3.41	222.32
-3.25	222.42
-1.75	222.47
-1.25	222.48
0.00	222.52
1.25	222.56
1.75	222.57
3.25	222.62

ODSAZENÍ OD OSY	STÁVAJÍCÍ TERÉN
-12.08	222.07
-9.78	223.05
-9.23	223.32
-8.34	223.41
-6.98	223.45
-3.48	223.38
-1.41	223.32
0.00	223.27
0.55	223.26
3.55	223.13
4.06	223.06
5.49	222.90
7.49	222.18
10.06	221.25
10.23	221.35
10.83	221.56

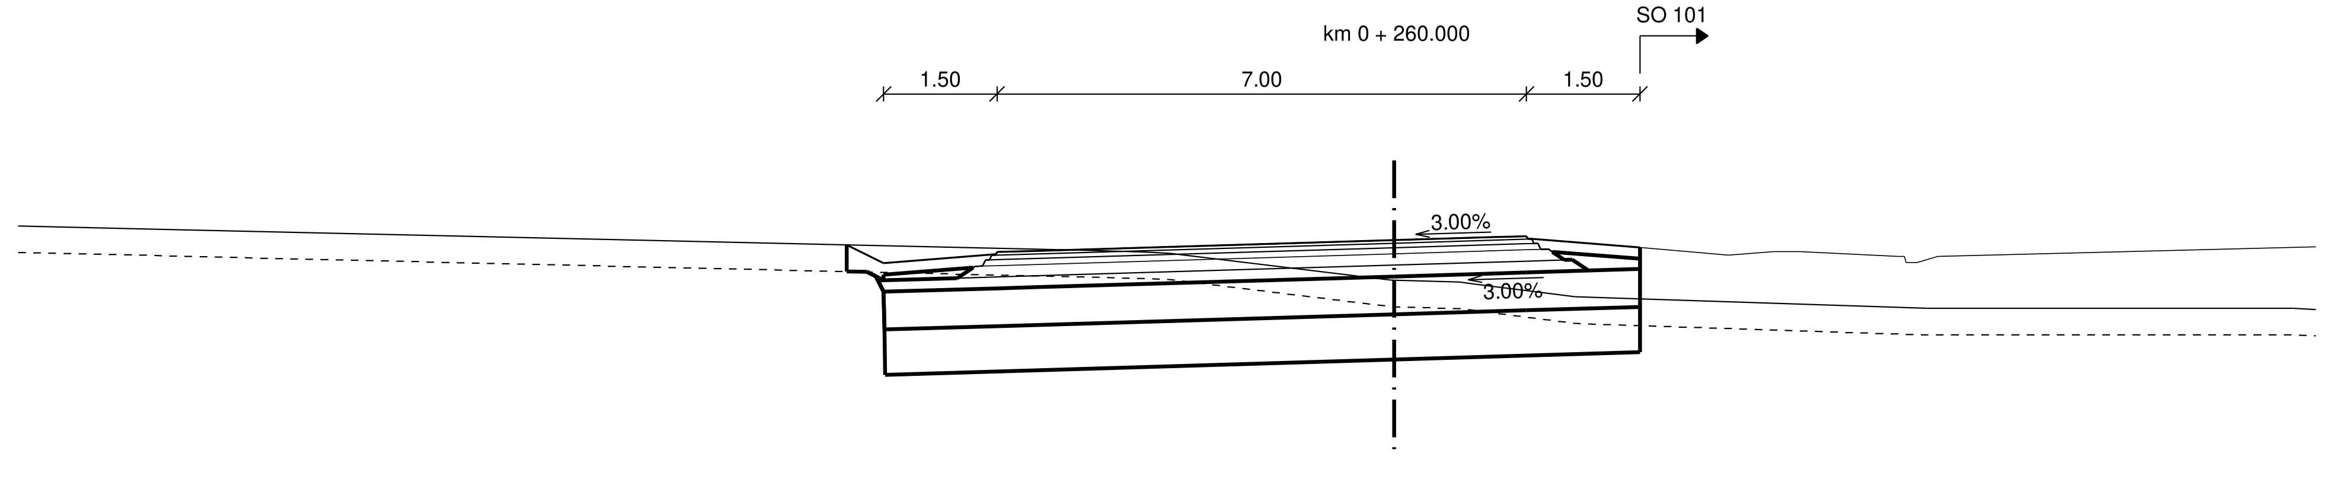

S. R. 218 m

ODSAZENÍ OD OSY	PROJEKTOVANÝ STAV
-7.24	222.67
-6.75	222.42
-5.27	222.54
-5.25	222.57
-4.75	222.59
0.00	222.73
1.25	222.77
1.75	222.78
1.77	222.75
3.25	222.63

ODSAZENÍ OD OSY	STÁVAJÍCÍ TERÉN
-4.05	222.59
-3.34	222.57
-2.98	222.56
-0.04	222.20
0.87	222.17
1.08	222.15
2.39	221.98
7.05	221.83
11.89	221.83

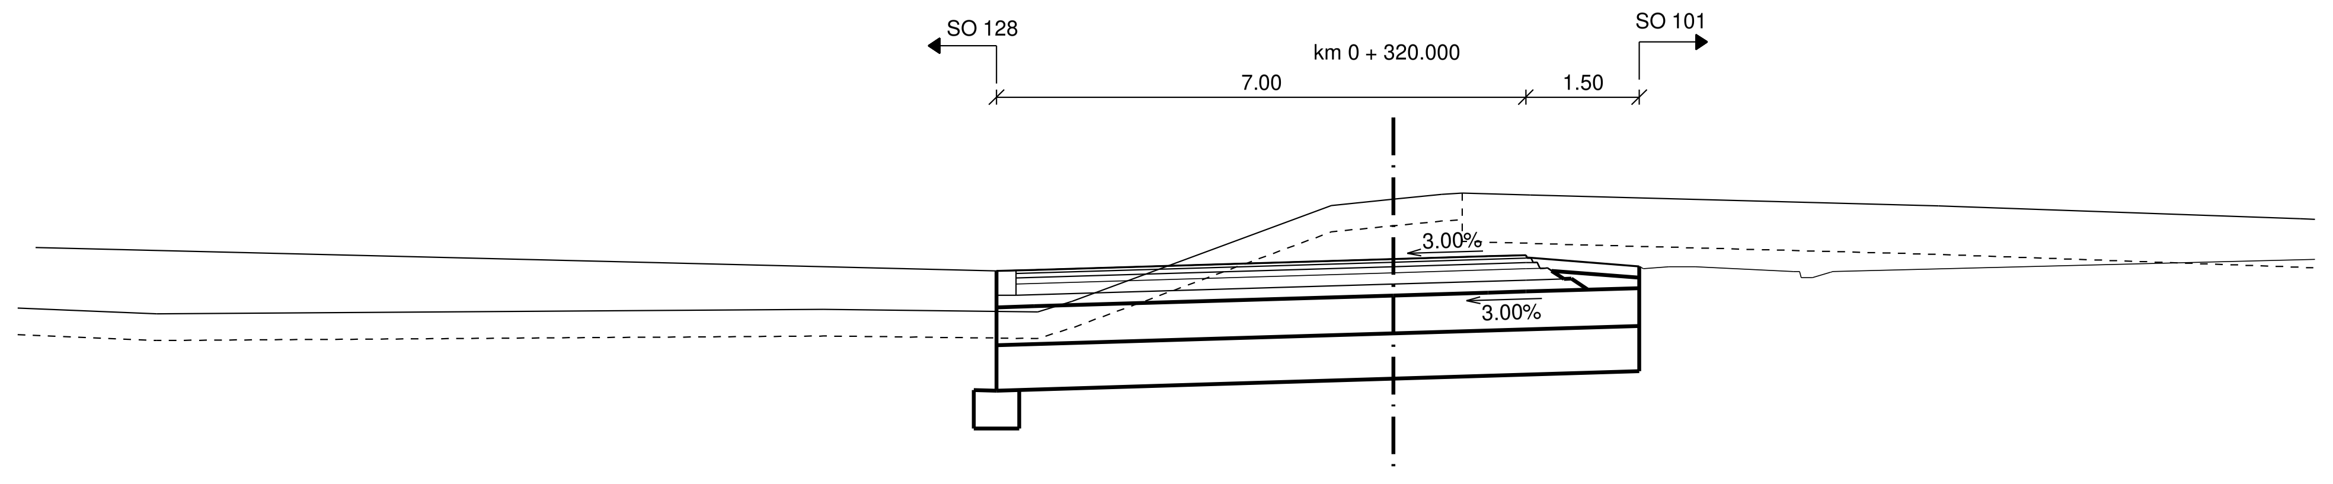

S. R. 218 m

ODSAZENÍ OD OSY	PROJEKTOVANÝ STAV
-5.25	222.39
-4.75	222.40
0.00	222.54
1.25	222.58
1.75	222.60
1.77	222.57
3.25	222.45

ODSAZENÍ OD OSY	STÁVAJÍCÍ TERÉN
-7.54	221.88
-4.70	221.84
-4.25	221.98
-0.82	223.25
0.00	223.33
0.64	223.40
0.91	223.42
1.81	223.39
7.21	223.24
11.99	223.08

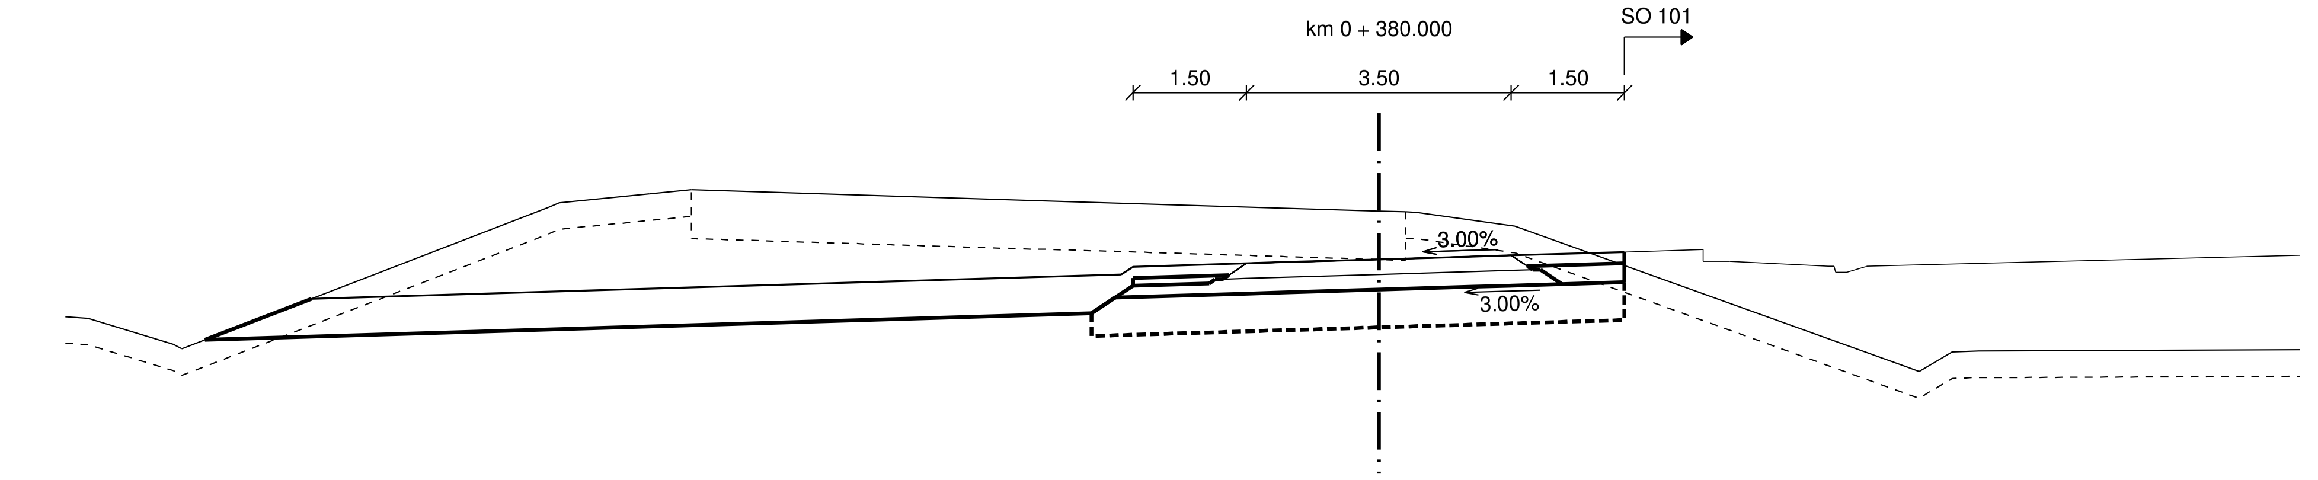

S. R. 218 m

ODSAZENÍ OD OSY	PROJEKTOVANÝ STAV
-14.11	222.01
-3.41	222.33
-3.25	222.44
-1.75	222.48
-1.25	222.50
0.00	222.54
1.25	222.57
1.75	222.59
3.25	222.63

ODSAZENÍ OD OSY	STÁVAJÍCÍ TERÉN
-11.80	223.20
-11.66	223.26
-10.47	223.38
-9.52	223.47
-4.43	223.31
0.00	223.18
0.36	223.16
0.50	223.16
1.80	222.97
6.99	221.11
7.15	221.05
7.58	221.31
7.93	221.32

Výškový systém Bpv

SO 124 Přeložka místní komuniakce km 7,340 - 7,700 vlevo

Objednatel:

ŘEDITELSTVÍ SILNIC A DÁLNIC

Ředitelství silnic a dálnic s. p.
Čerčanská 2023/12, Krč, 140 00 Praha 4

Zhotovitel:

Valbek

Valbek, spol. s r.o.
Vaňurova 505/17
460 07 Liberec 3

HIP:
ING. T. KLIMENT

Vypracoval	M. KOŘÍNEK	**Zak. číslo**	21-LI13-001
Zodp. projektant	ING. T. KLIMENT	**Datum**	02/2025
Tech. kontrola	ING. M. HANŽL	**Stupeň**	PDPS
Akce	**I/16 MLADÁ BOLESLAV - MARTINOVICE**	**Počet formátů**	10xA4
		Měřítko	1 : 100
		Č. přílohy	**Paré**
Příloha	PŘÍČNÉ ŘEZY V km 0,220 - 0,380	**5.2**	

Zhotovitel:
Valbek, spol. s r.o.
Vaňurova 505/17
460 07 Liberec 3