SO 124 - PŘELOŽKA MÍSTNÍ KOMUNIKACE km 7,340 - 7,700 VLEVO
PŘÍČNÉ ŘEZY, km 0,400 - 0,520, M 1 : 100

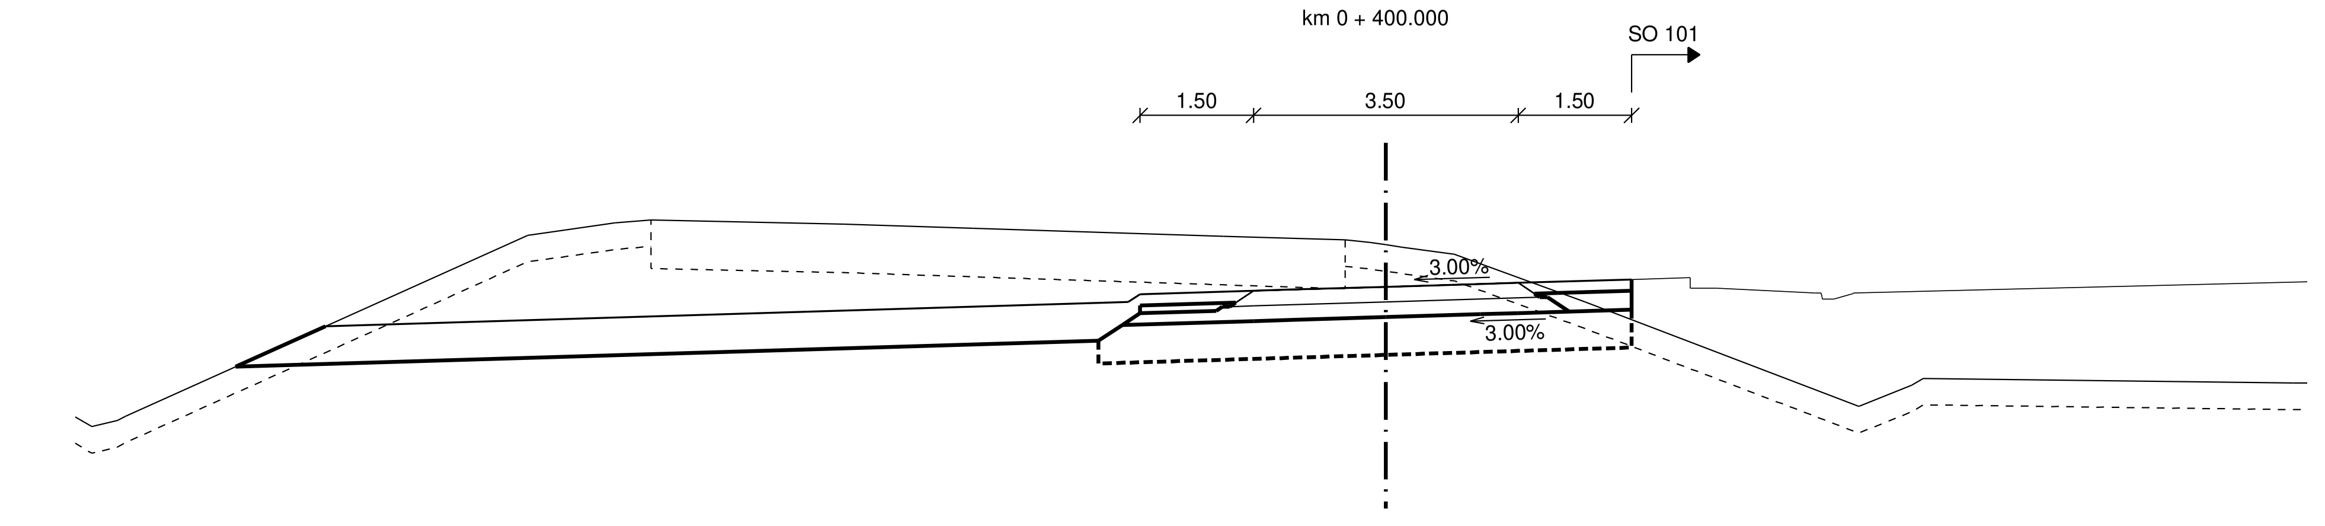

S. R. 218 m

PROJEKTOVANÝ STAV	222.05	222.37	222.48	222.52	222.54	222.57	222.61	222.63	222.67
ODSAZENÍ OD OSY	-14.02	-3.41	-3.25	-1.75	-1.25	0.00	1.25	1.75	3.25

STÁVAJÍCÍ TERÉN	223.27	223.34	223.44	223.48	223.40	223.35	223.24	223.19	223.16	223.13	223.10	223.00	222.37	220.99	221.27	221.36
ODSAZENÍ OD OSY	-12.21	-11.70	-11.06	-10.58	-7.17	-5.45	-2.15	-0.54	-0.21	0.00	0.21	0.91	2.64	6.25	6.95	7.11

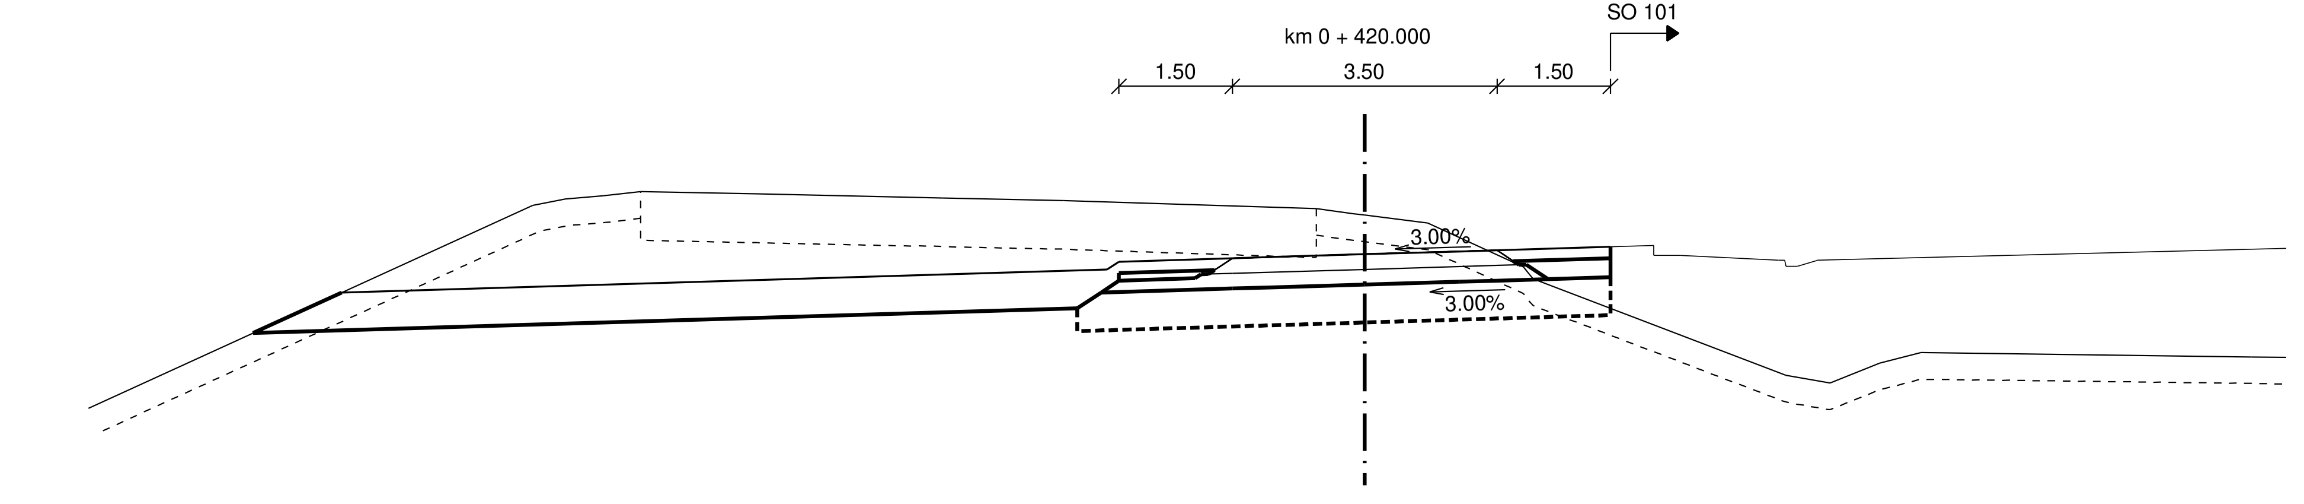

PROJEKTOVANÝ STAV	222.13	222.43	222.53	222.58	222.59	222.63	222.67	222.68	222.73	221.14
ODSAZENÍ OD OSY	-13.73	-3.41	-3.25	-1.75	-1.25	0.00	1.25	1.75	3.25	6.68

STÁVAJÍCÍ TERÉN	223.28	223.36	223.40	223.46	223.42	223.38	223.34	223.23	223.17	223.15	223.04	222.46	222.31	221.03	220.93	221.19	221.33	221.28
ODSAZENÍ OD OSY	-11.00	-10.57	-10.07	-9.57	-8.02	-5.58	-3.99	-0.64	-0.15	0.00	0.83	2.10	2.23	5.57	6.15	6.81	7.35	11.73

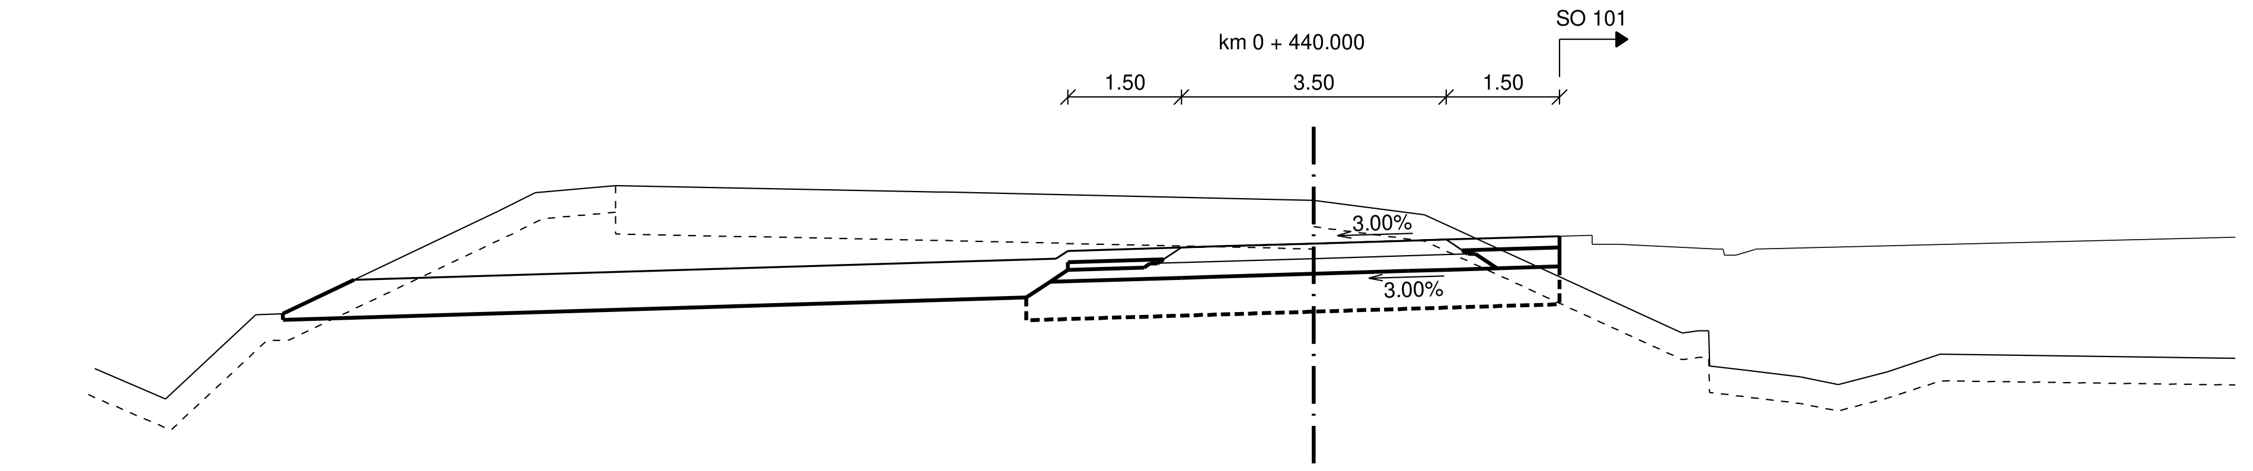

S. R. 218 m

PROJEKTOVANÝ STAV	222.23	222.51	222.61	222.66	222.67	222.71	222.75	222.76	222.81	220.93
ODSAZENÍ OD OSY	-12.69	-3.41	-3.25	-1.75	-1.25	0.00	1.25	1.75	3.25	7.26

STÁVAJÍCÍ TERÉN	223.14	223.38	223.47	223.39	223.39	223.28	223.09	221.53	221.56	221.56	221.25	221.09	221.04	221.25	220.95	220.85	221.02	221.25
ODSAZENÍ OD OSY	-10.78	-10.30	-9.23	-4.96	-4.85	0.00	1.46	4.87	5.09	5.22	5.23	5.23	5.71	5.73	6.44	6.94	7.59	8.28

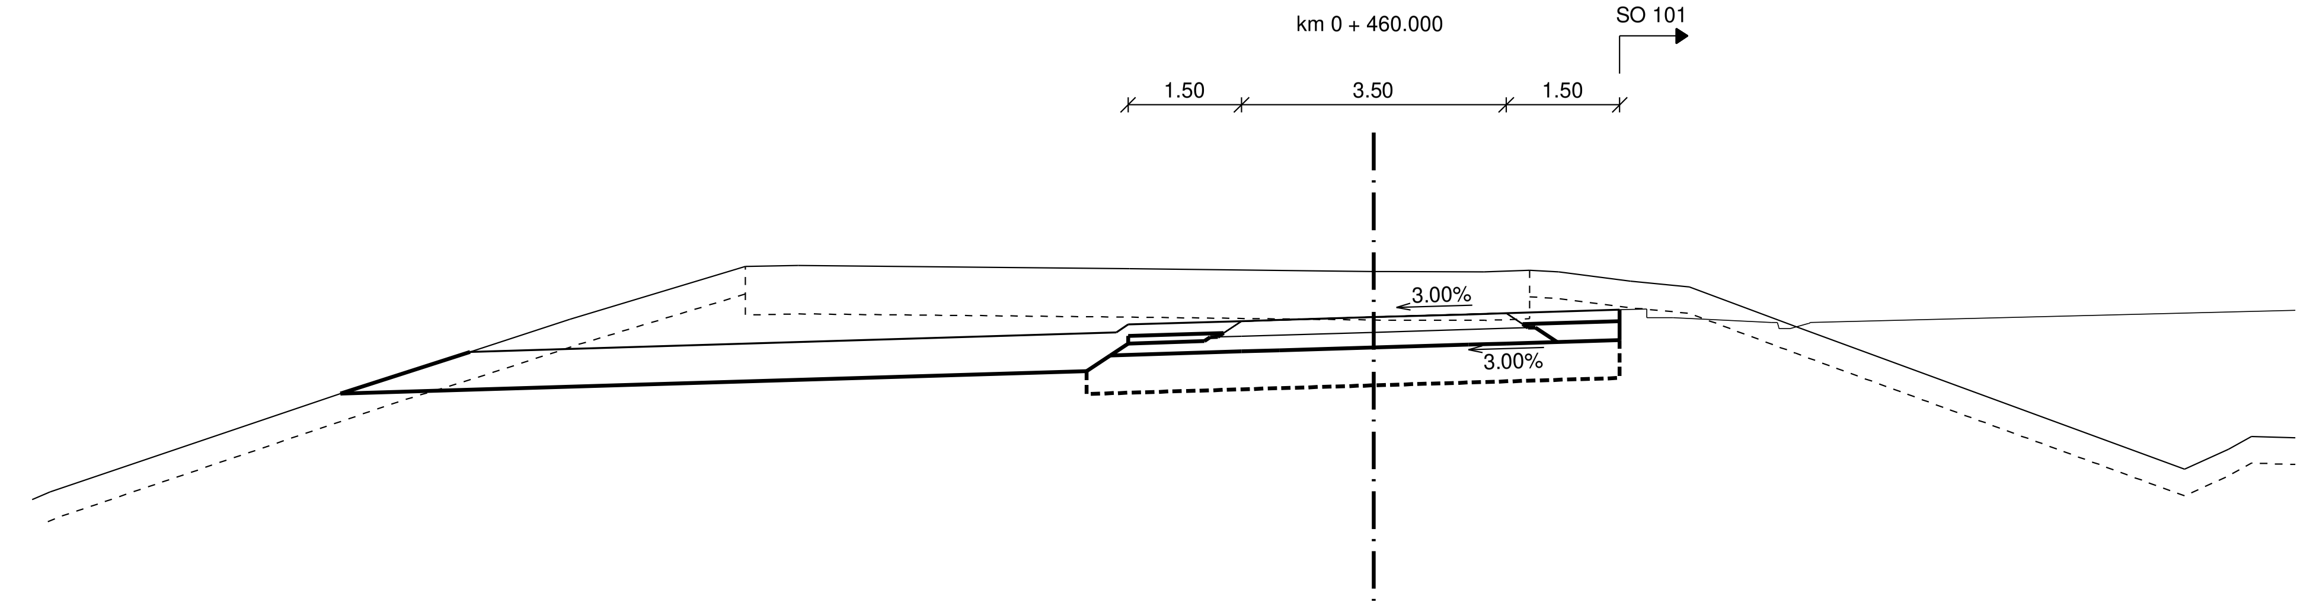

S. R. 218 m

PROJEKTOVANÝ STAV	222.35	222.61	222.71	222.76	222.77	222.81	222.85	222.86	222.91
ODSAZENÍ OD OSY	-11.95	-3.41	-3.25	-1.75	-1.25	0.00	1.25	1.75	3.25

STÁVAJÍCÍ TERÉN	222.35	222.78	223.48	223.49	223.45	223.41	223.41	223.41	223.43	223.41	223.28	223.21	222.68	220.80	221.06	221.23
ODSAZENÍ OD OSY	-11.95	-10.71	-8.31	-7.61	-3.23	0.00	0.21	1.46	2.06	2.44	3.39	4.17	5.58	10.72	11.30	11.60

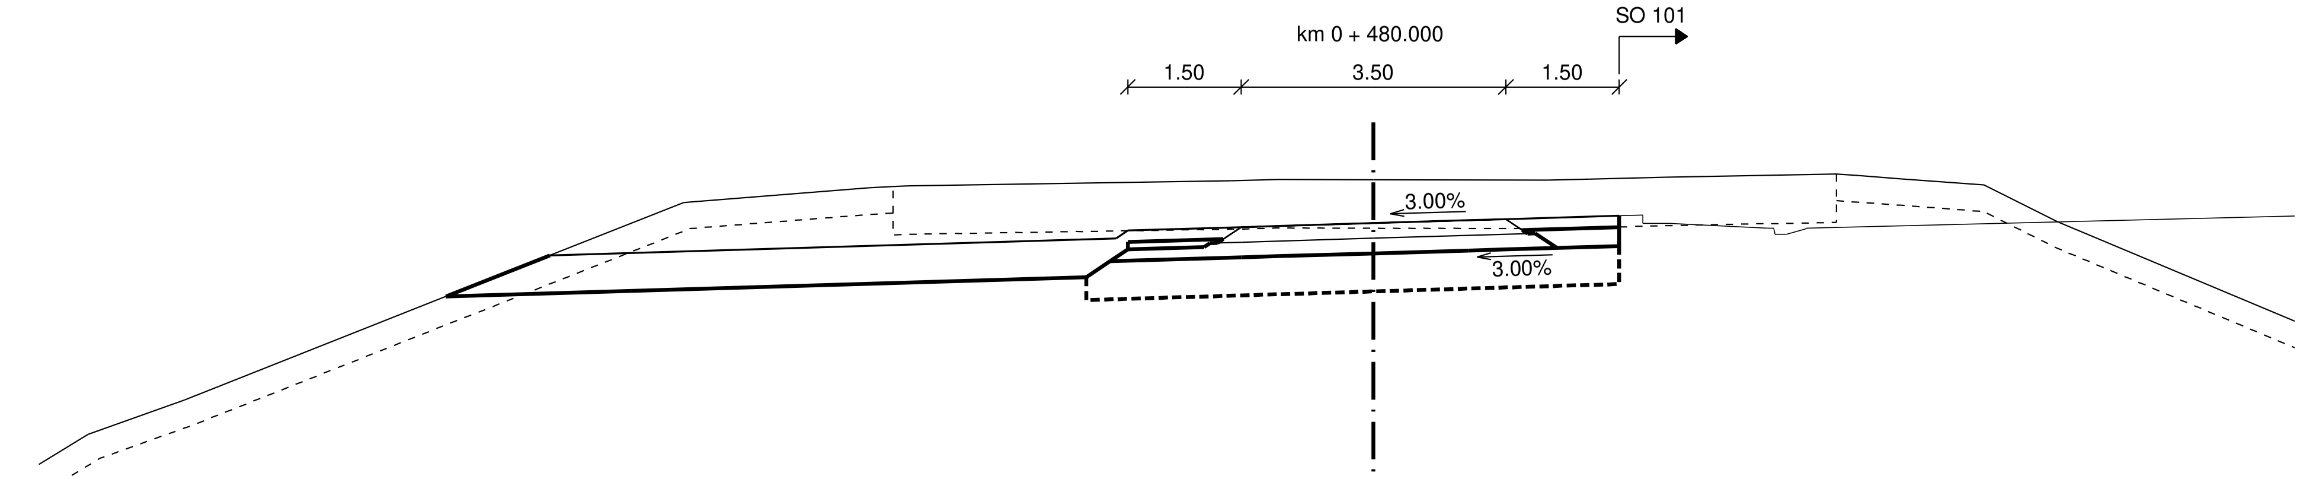

PROJEKTOVANÝ STAV	222.50	222.72	222.83	222.87	222.89	222.93	222.96	222.98	223.02
ODSAZENÍ OD OSY	-10.90	-3.41	-3.25	-1.75	-1.25	0.00	1.25	1.75	3.25

STÁVAJÍCÍ TERÉN	222.17	223.19	223.39	223.41	223.42	223.49	223.50	223.50	223.49	223.51	223.53	223.57	223.55	223.51	223.43	222.94
ODSAZENÍ OD OSY	-12.05	-9.13	-6.68	-6.35	-6.16	-1.88	-1.26	0.00	2.30	2.85	3.85	6.12	6.43	6.97	8.08	9.05

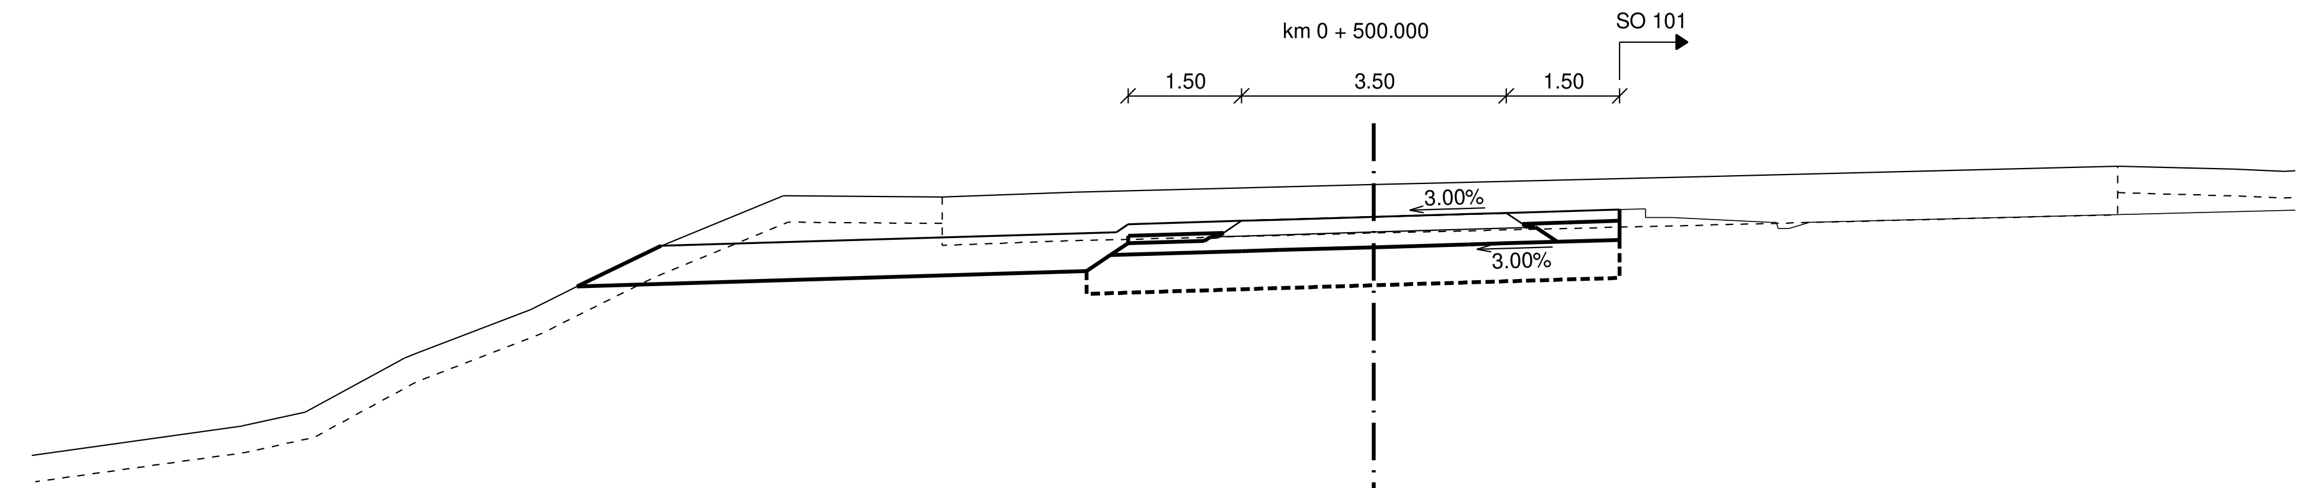

S. R. 218 m

PROJEKTOVANÝ STAV	222.68	222.86	222.97	223.01	223.03	223.06	223.10	223.12	223.16
ODSAZENÍ OD OSY	-9.42	-3.41	-3.25	-1.75	-1.25	0.00	1.25	1.75	3.25

STÁVAJÍCÍ TERÉN	221.27	221.84	222.58	223.34	223.33	223.39	223.45	223.49	223.51	223.60	223.61	223.73	223.69
ODSAZENÍ OD OSY	-12.64	-11.15	-9.67	-7.81	-5.71	-3.97	-1.80	0.00	0.74	4.61	4.77	9.84	11.38

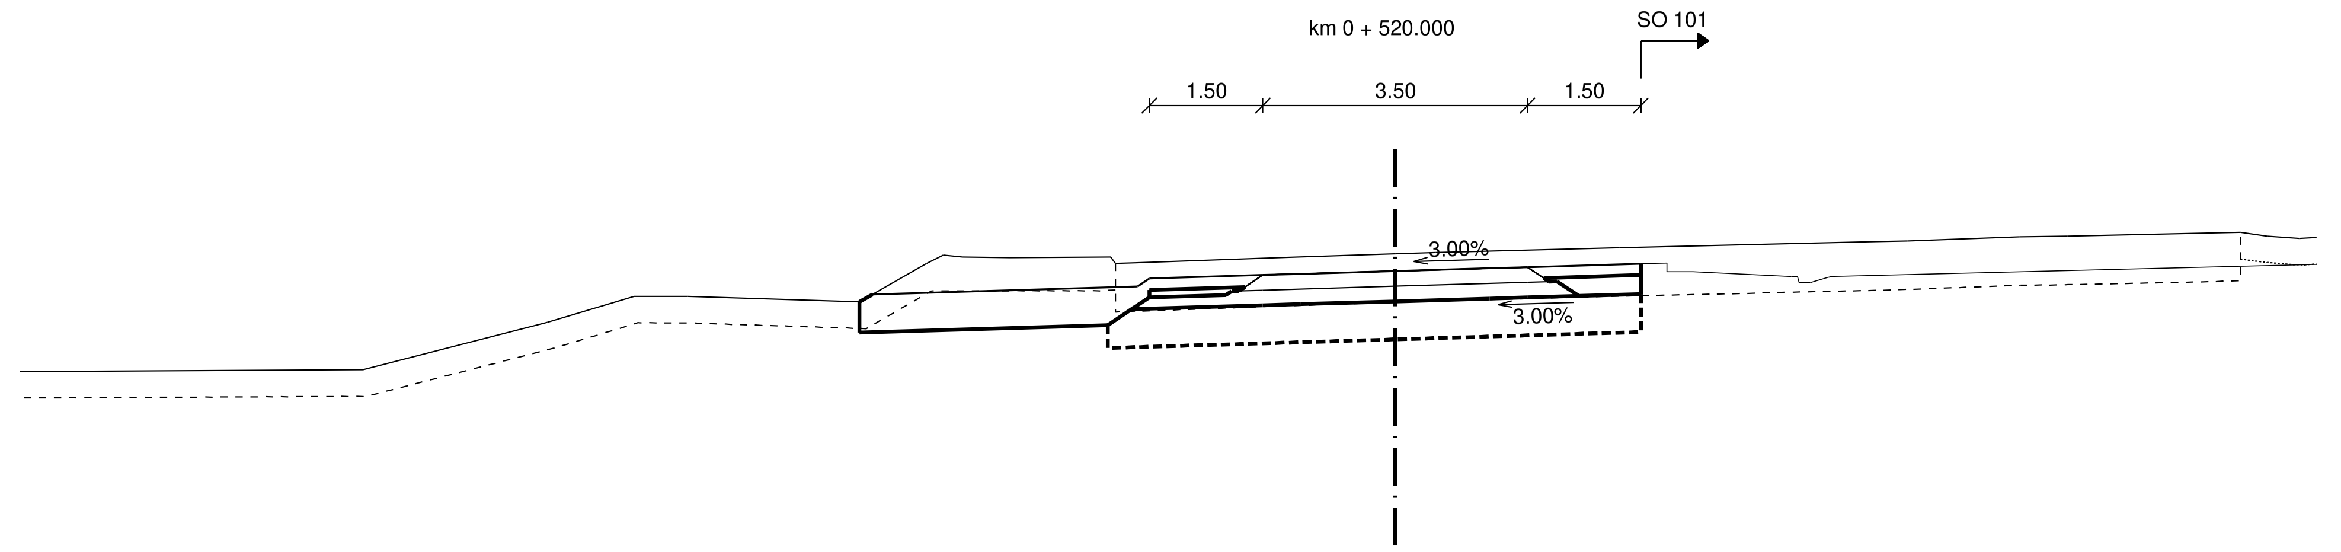

S. R. 218 m

PROJEKTOVANÝ STAV	222.91	223.02	223.12	223.17	223.18	223.22	223.26	223.27	223.32
ODSAZENÍ OD OSY	-6.91	-3.41	-3.25	-1.75	-1.25	0.00	1.25	1.75	3.25

STÁVAJÍCÍ TERÉN	222.54	222.89	222.89	222.81	223.32	223.43	223.41	223.40	223.41	223.32	223.33	223.40	223.45	223.47	223.53	223.61	223.62	223.67	223.68	223.73	223.68	223.65
ODSAZENÍ OD OSY	-11.08	-9.94	-9.22	-7.08	-6.20	-5.98	-5.72	-5.09	-3.76	-3.70	-3.43	-1.41	0.00	0.53	2.96	6.34	6.78	8.26	8.89	11.18	11.53	11.96

Výškový systém Bpv

SO 124 Přeložka místní komunikace km 7,340 - 7,700 vlevo

Objednatel:

ŘEDITELSTVÍ SILNIC A DÁLNIC

Ředitelství silnic a dálnic s. p.
Čerčanská 2023/12, Krč, 140 00 Praha 4

Zhotovitel:

Valbek

Valbek, spol. s r.o.
Vaňurova 505/17
460 07 Liberec 3

HIP:
ING. T. KLIMENT

Vypracoval	M. KOŘÍNEK	**Zak. číslo**	21-LI13-001
Zodp. projektant	ING. T. KLIMENT	**Datum**	02/2025
Tech. kontrola	ING. M. HANŽL	**Stupeň**	PDPS
Akce		**Počet formátů**	10xA4
	I/16 MLADÁ BOLESLAV - MARTINOVICE	**Měřítko**	1 : 100
		Č. přílohy	**Paré**
Příloha	PŘÍČNÉ ŘEZY V km 0,400 - 0,520	**5.3**	

Valbek

Zhotovitel:
Valbek, spol. s r.o.
Vaňurova 505/17
460 07 Liberec 3