
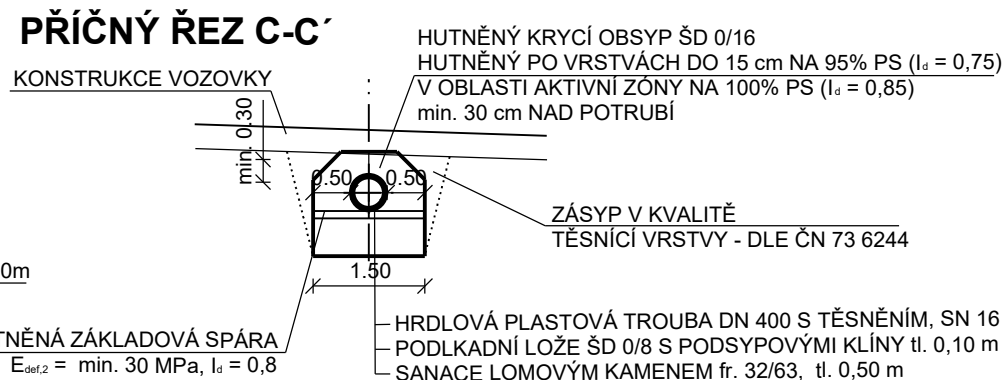
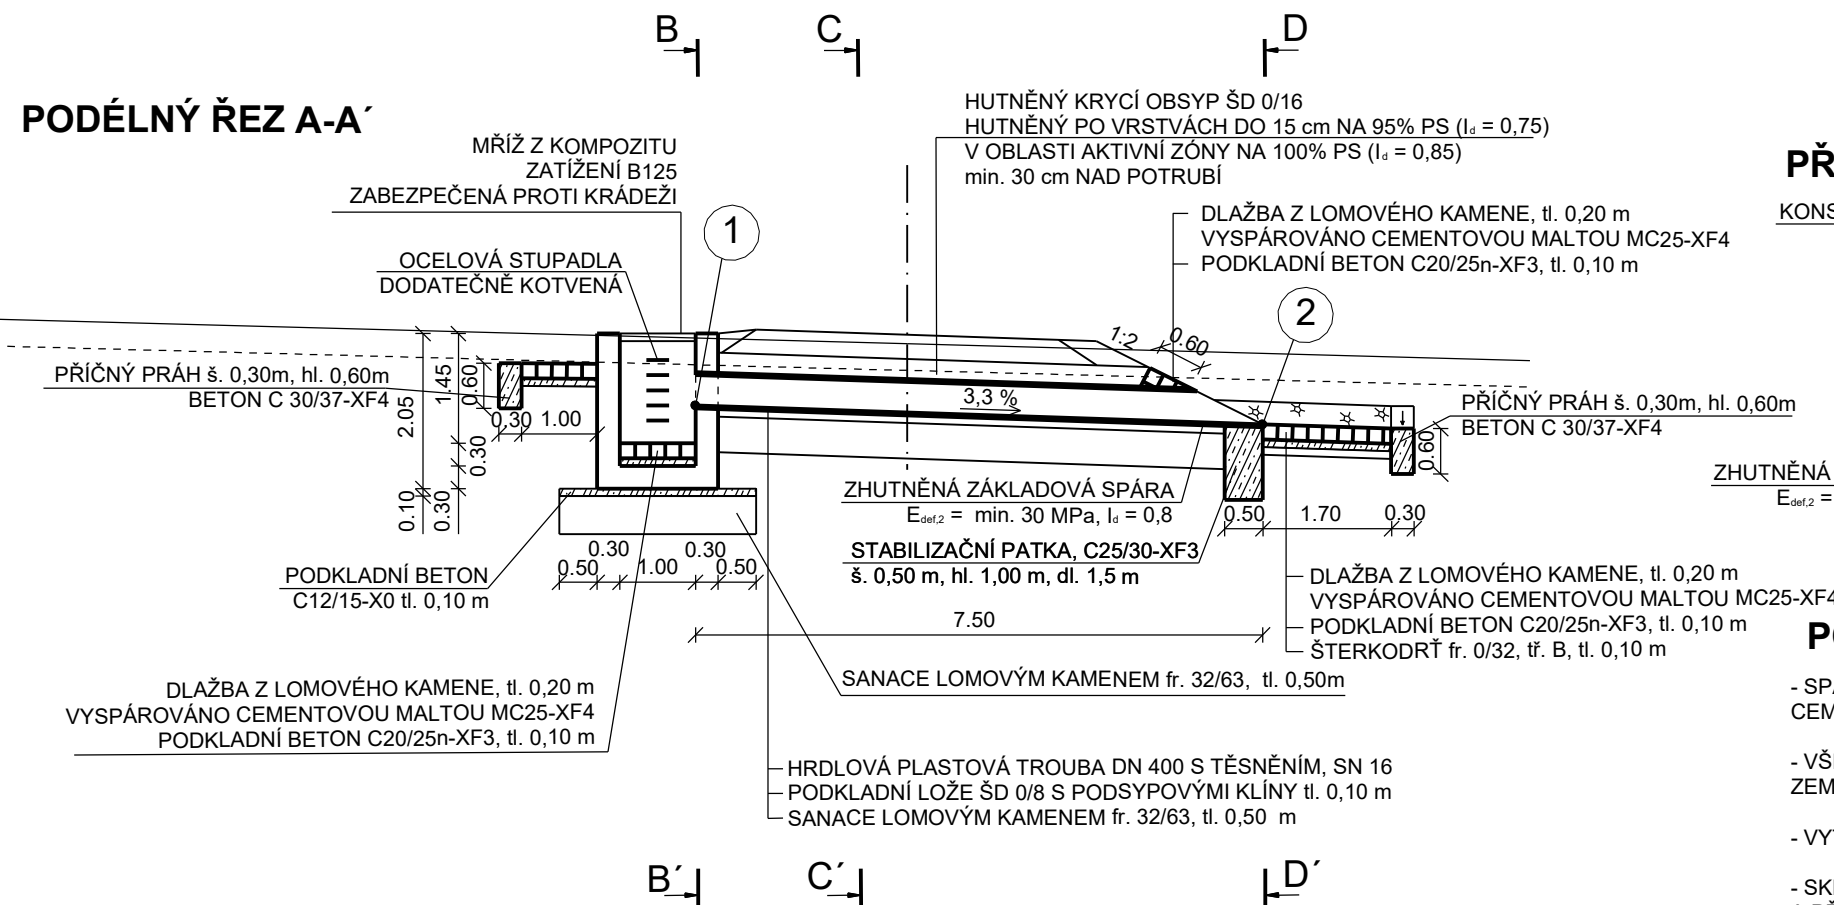
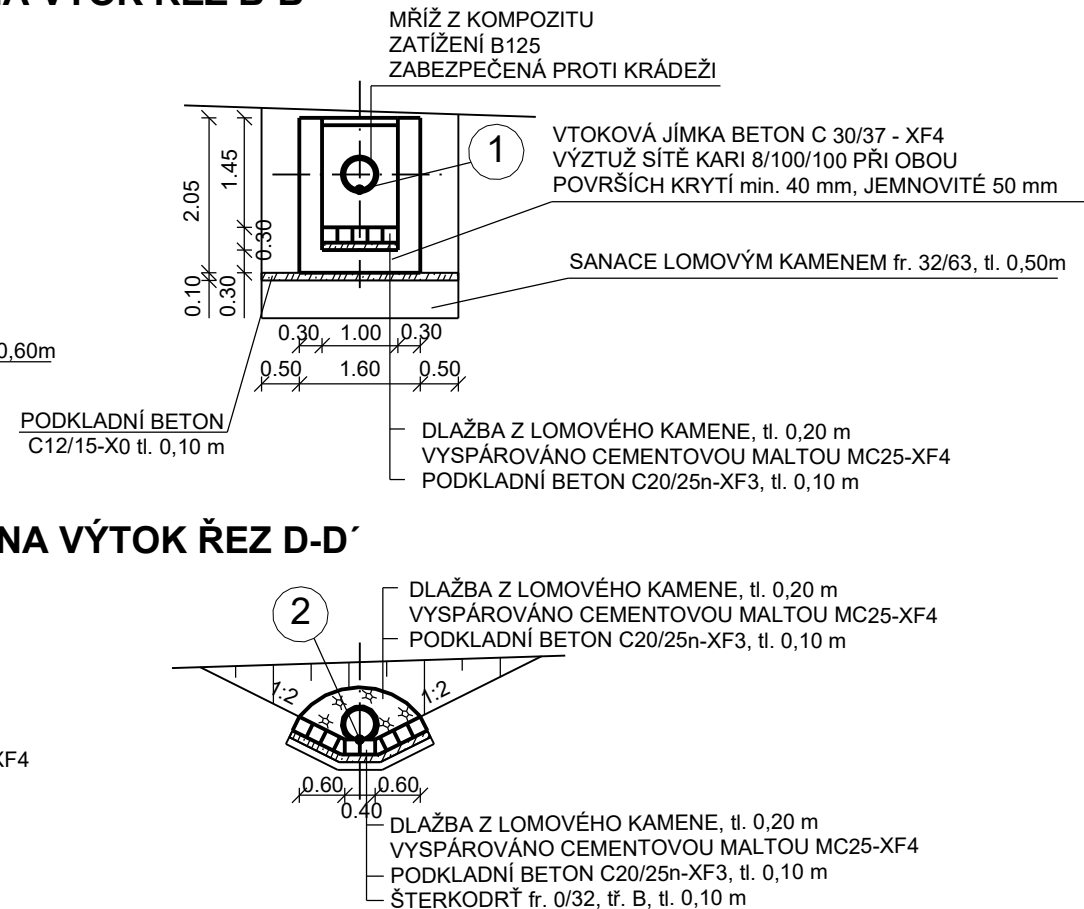


SO 124 - PŘELOŽKA MÍSTNÍ KOMUNIKACE km 7,340 - 7,700 VLEVO
PROPUSTEK DN 400 km 0,070 SJEZD VLEVO
M 1 : 100

HUTNĚNÝ KRYCÍ OBSYP ŠD 0/16
HUTNĚNÝ PO VRSTVÁCH DO 15 cm NA 95% PS ($I_L = 0,75$)

POHLED NA VTO

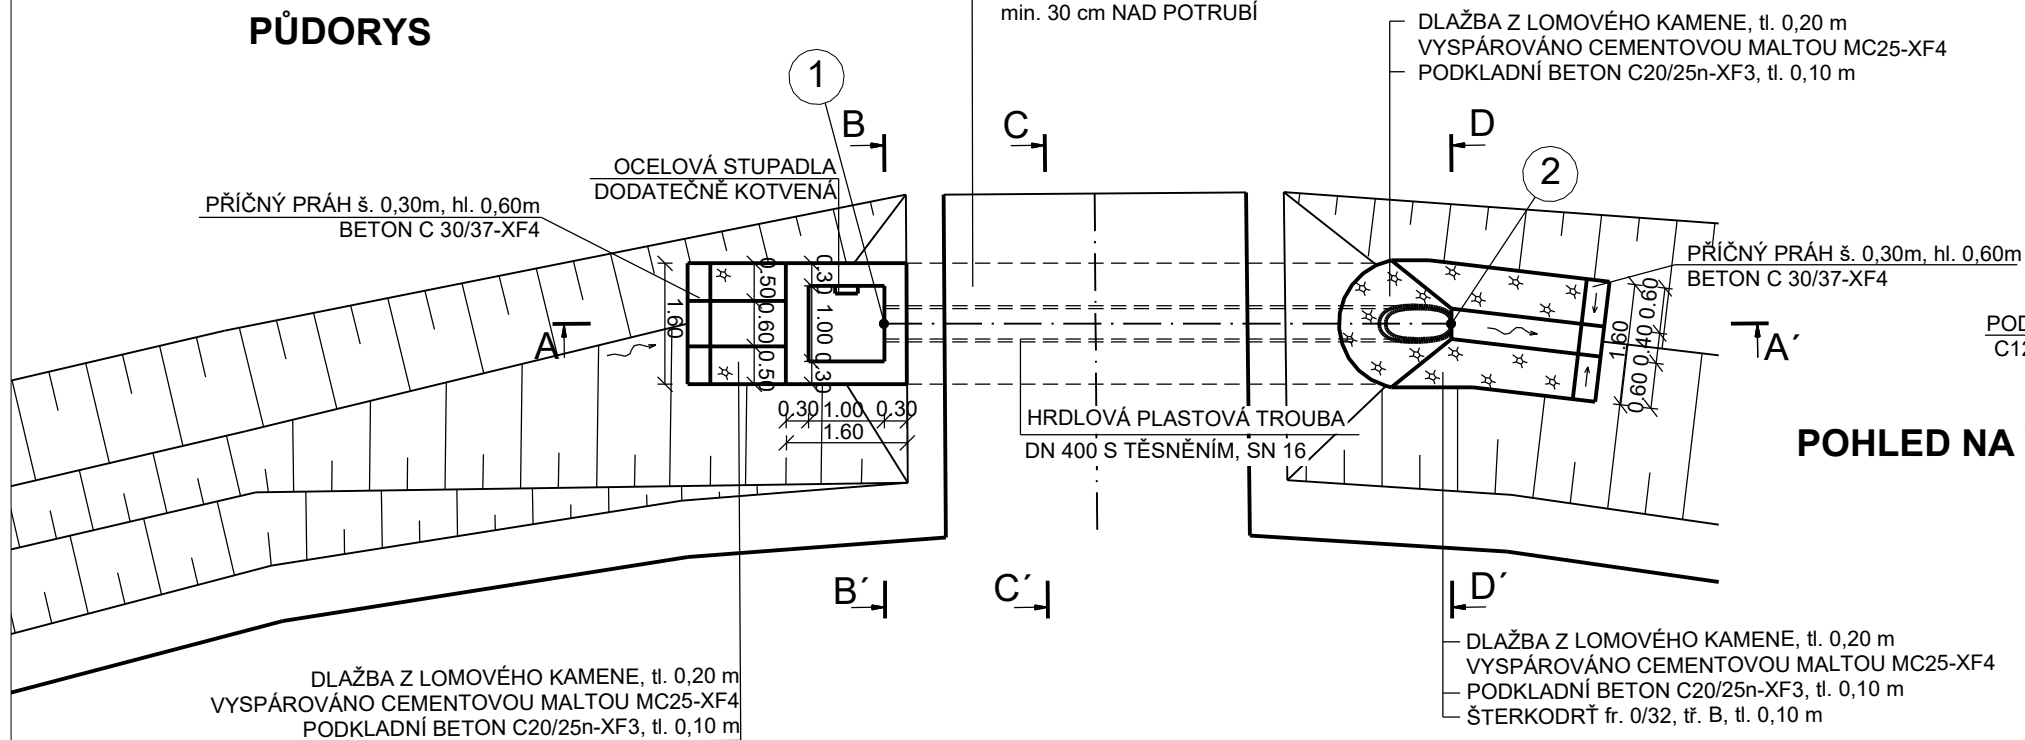

POZNÁMKY:

- SPÁRY DLAŽBY Z LOMOVÉHO KAMENE VYPLNĚNÉ
CEMENTOVOU MALTOU M25 - XF4 tl. 0,20 m

- VŠECHNY BETONOVÉ PRVKY, KTERÉ PŘIJDOU DO STYKU SE ZEMINOU MUSÍ BÝT OPATŘENY NÁTĚRY: 1x NPe A 2x NA

- VYTYČENÍ BUDE PROVEDENO DLE TKP1 A SOUVISEJÍCÍCH PŘEDPISŮ

- SKLONY SVAHŮ JSOU URČENY SKLONEM SILNIČNÍHO TĚLESA
A PŘÍLEHLÝCH PŘÍKOPŮ

- VÝZTUŽ JÍMKY KARI SÍŤ 8/100/100, KRYTÍ min. 40 mm, JMENOVITÉ 50 mm

- OCELOVÁ STUPADLA DODATEČNĚ KOTVENÁ

-POTRUBÍ MUSÍ BÝT UV STABILNÍ

PARAMETRY PROPUSTKŮ					VYTYČOVANÉ BODY	
STANIČENÍ [km]	TROUBA DN [mm]	DÉLKA DL [m]	SKLON S _i [%]	ÚHEL α [°]	VTOK - 01 Y / X [S-JTSK] / Z [Bpv]	VÝTOK - 02 Y / X [S-JTSK] / Z [Bpv]
0,070	400	7,50	3,30	90	694168,460/1010771,666/225,37	694161,404/1010774,209/225,12

Souřadnicový sysrém: S-JTSK

Výškový systém: Bpv

SO 124 Přeložka místní komunikace km 7,340 - 7,700 vlevo

Objednatel:

ŘEDITELSTVÍ SILNIC A DÁLNIC

Ředitelství silnic a dálnic s. p.

Čerčanská 2023/12, Krč, 140 00 Praha 4

Zhotovitel:

**Valbek, spol. s r.o.**

Vaňurova 505/17

460 07 Liberec 3

	Vypracoval A. BARTONIČKOVÁ		Zak. číslo 21-LI13-001
	Zodp. projektant ING. T. KLIMENT		Datum 02/2025
	Tech. kontrola ING. M. HANŽL		Stupeň PDPS
	Akce I/16 MLADÁ BOLESLAV - MARTINOVICE		Počet formátů 3 x A4
			Měřítko 1 : 100
			Č. přílohy Paré
Zhotovitel: Valbek, spol. s r.o. Vaňurova 505/17 460 07 Liberec 3	Příloha PROPUSTEK DN 400 km 0,070 SJEZD VLEVO		6