


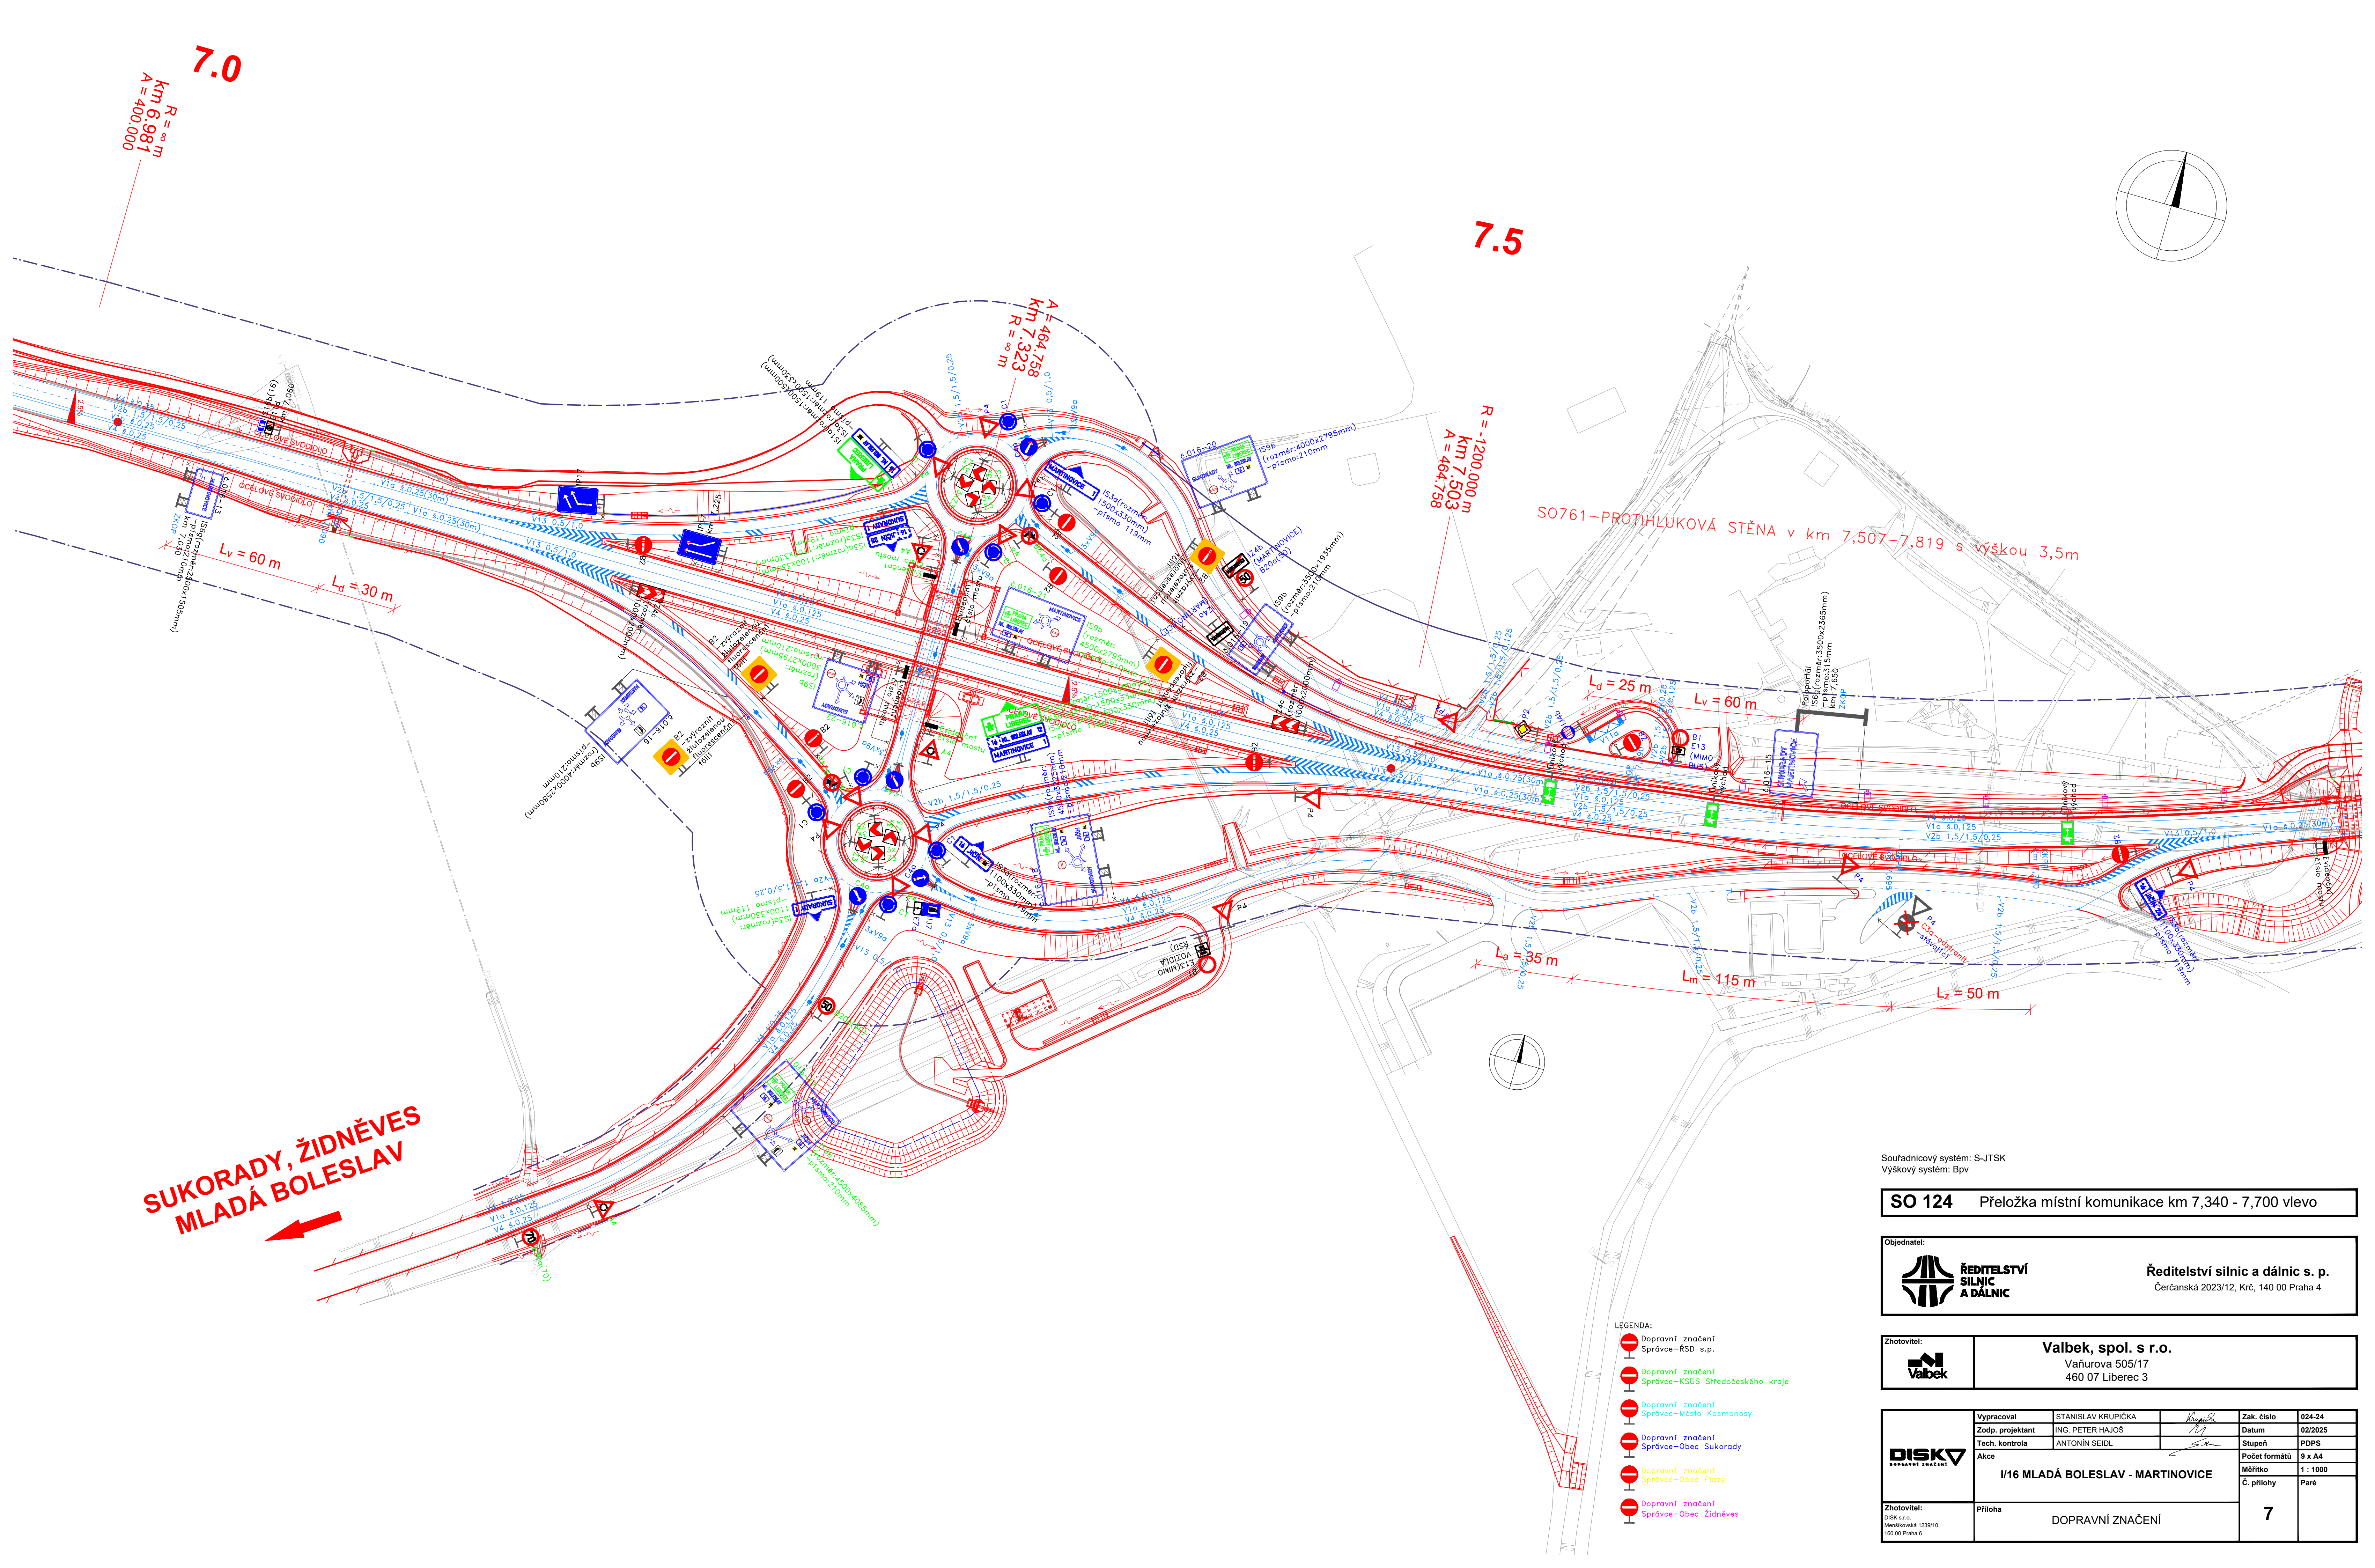

Souřadnicový systém: S-JTSK
Výškový systém: Bpv

SO 124 Přeložka místní komunikace km 7,340 - 7,700 vlevo

Objednatel:
**ŘEDITELSTVÍ
SILNIC
A DÁLNIC**
Ředitelství silnic a dálnic s. p.
Čerčanská 2023/12, Krč, 140 00 Praha 4

Zhotovitel:
**Valbek**
Valbek, spol. s r.o.
Vaňurova 505/17
460 07 Liberec 3

	Vypracoval	STANISLAV KRUPÍČKA		Zak. číslo	024-24	
	Zodp. projektant	ING. PETER HAJOŠ		Datum	02/2025	
	Tech. kontrola	ANTONÍN SEIDL		Stupeň	PDPs	
	Akce	I/16 MLADÁ BOLESLAV - MARTINOVICE			Počet formátů	9 x A4
Zhotovitel: DISK s.r.o. Mentšikovská 1239/10 160 00 Praha 6	Příloha	DOPRAVNÍ ZNAČENÍ			Měřítko	1 : 1000
					Č. přílohy	Paré
					7	