
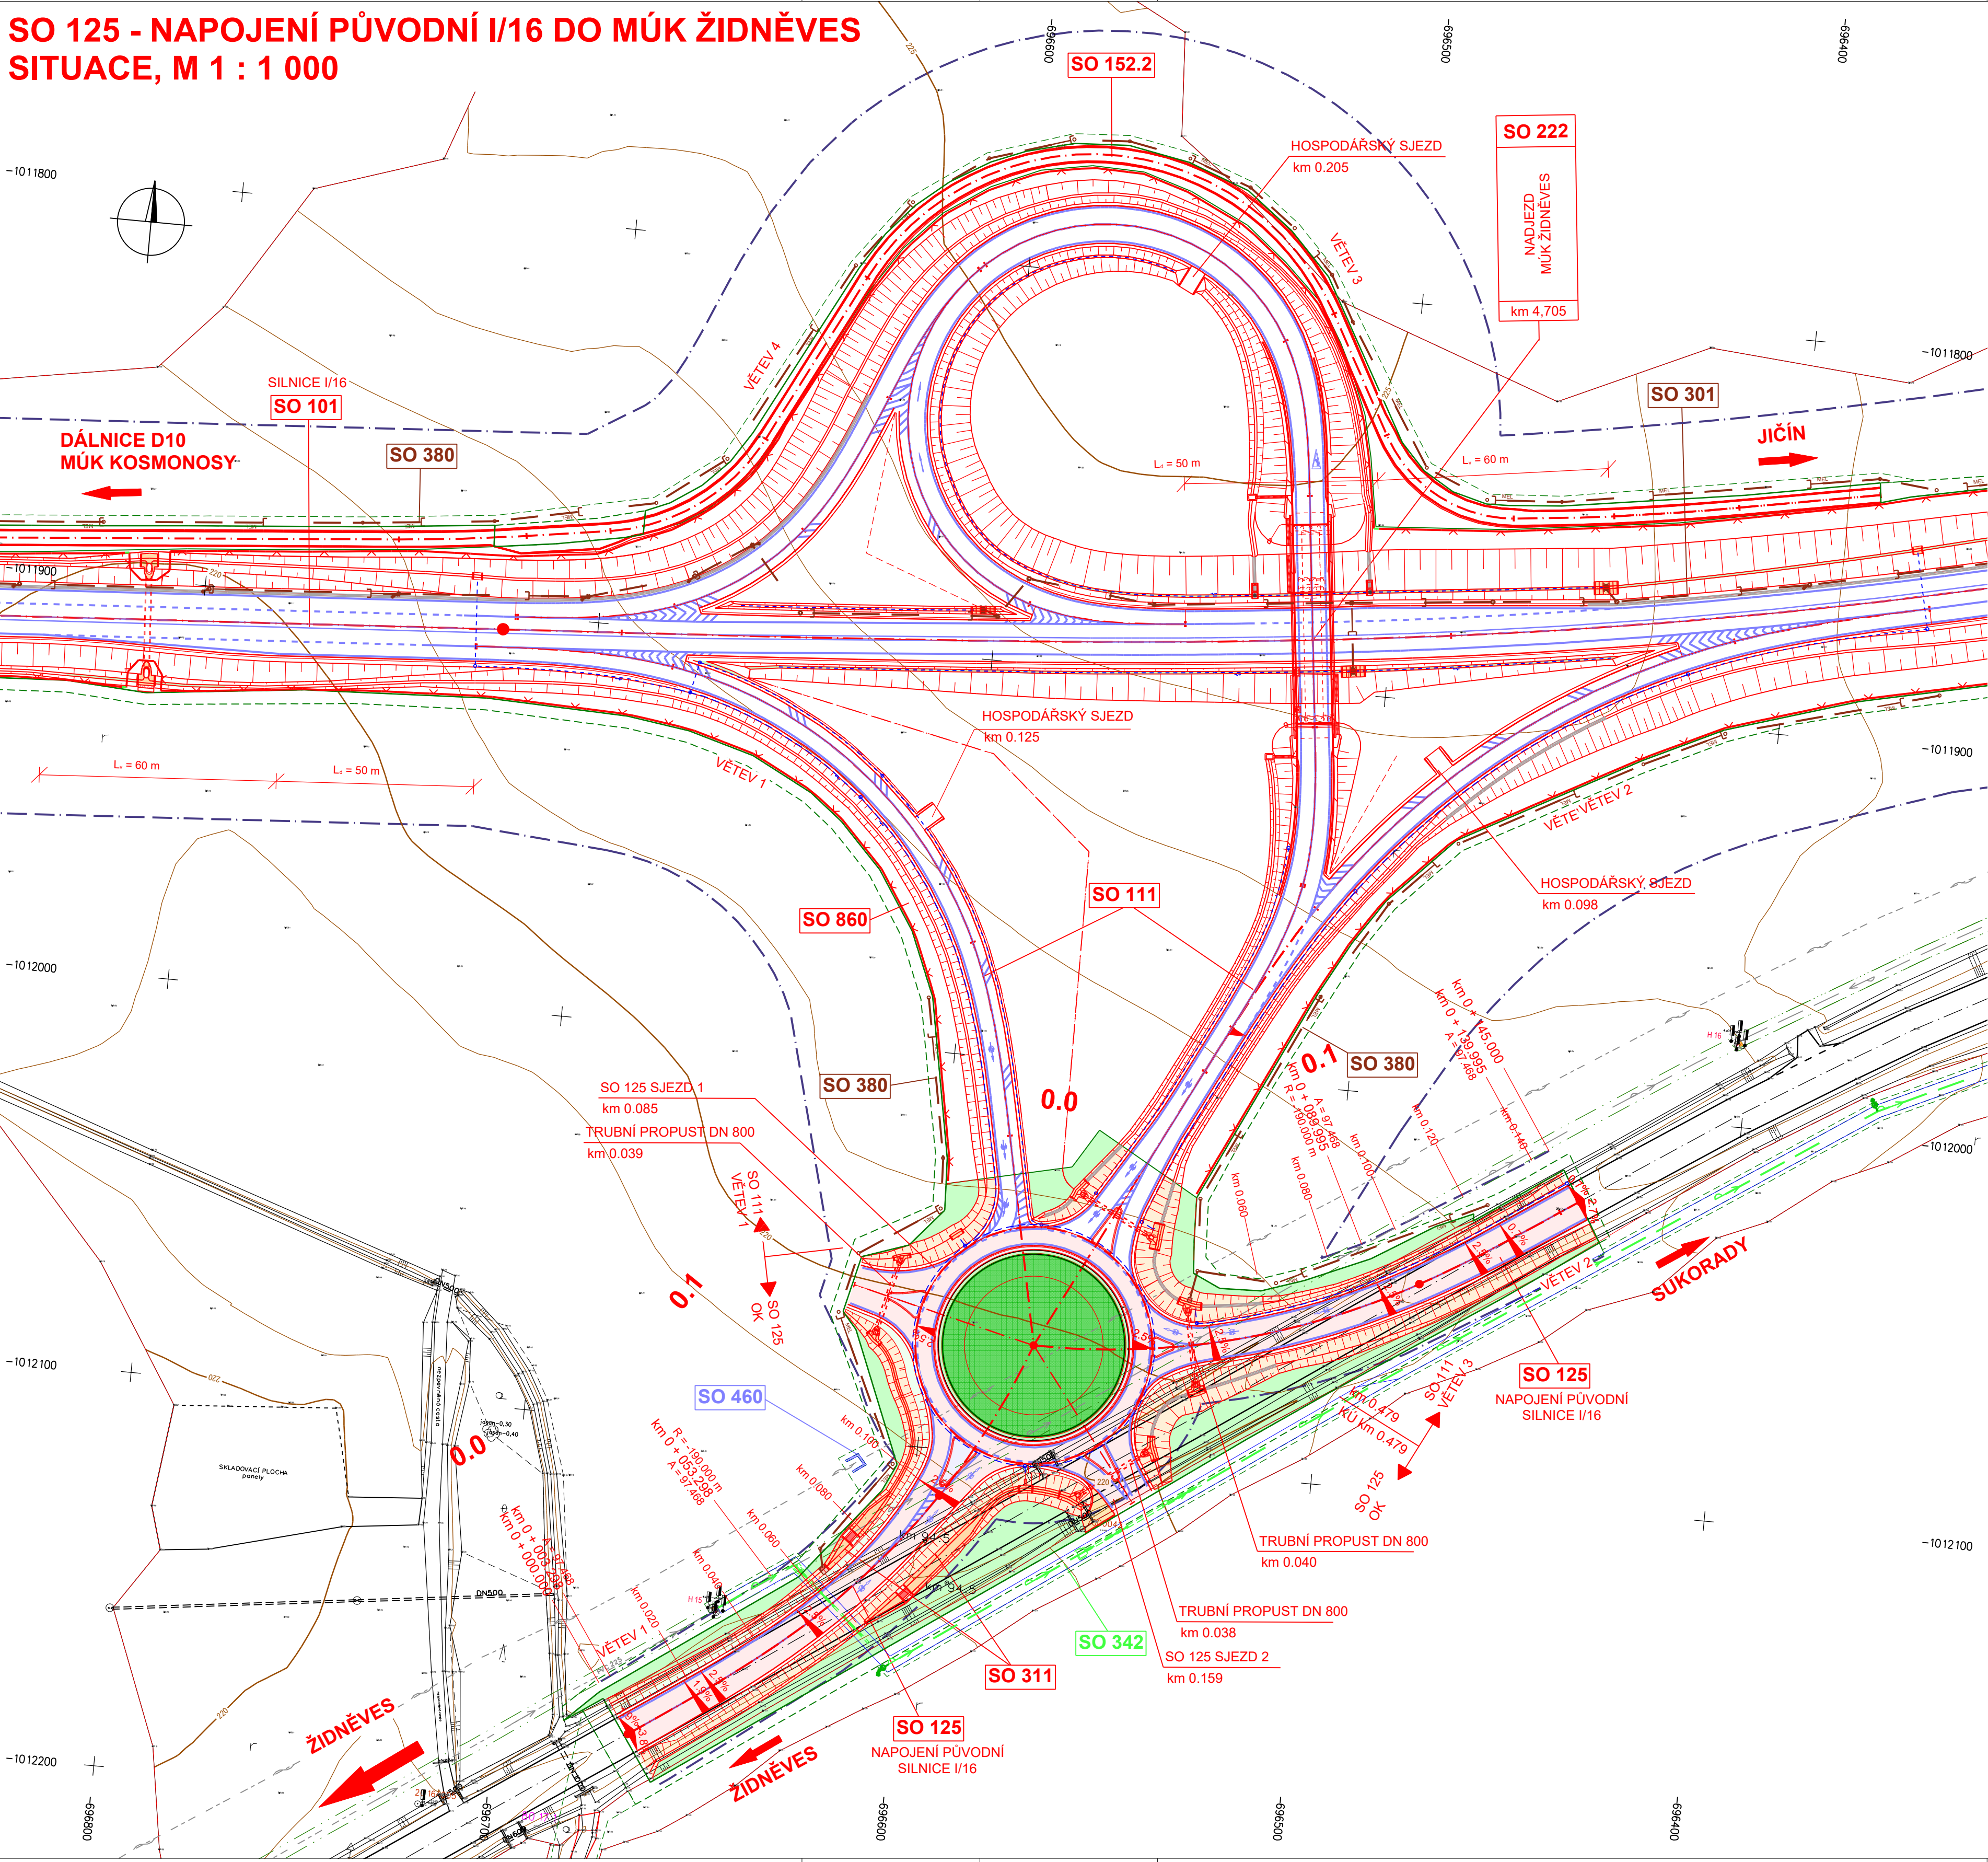
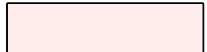
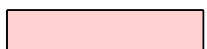
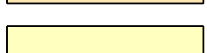
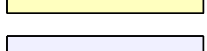


SO 125 - NAPOJENÍ PŮVODNÍ I/16 DO MÚK ŽIDNĚVES
SITUACE, M 1 : 1 000

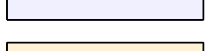

LEGENDA:		NOVÉ IS	
PLOCHY		VOZOVKA - ASFALTOVÝ KRYT	 DEŠŤOVÁ KANALIZACE
		VOZOVKA - FRÉZOVANÁ	 MELIORACE
		VOZOVKA - POLNÍ CESTY	 VÝTLAK
		CHODNÍK	 VODOVOD
		DLAŽBA VOZOVKY	 NADZEMNÍ VEDENÍ NN
		SVAHY VÝKOPU	 NADZEMNÍ VEDENÍ VN
OBVOD STAVBY		SVAHY NÁSYPU	 PODZEMNÍ VEDENÍ NN
		VEGETAČNÍ ÚPRAVY	 PODZEMNÍ VEDENÍ VN
		TRVALÝ ZÁBOR	 PLYNOVOD - SDĚLOVACÍ VEDENÍ
		DOČASNÝ ZÁBOR	 PLYNOVOD - STL
		STÁVAJÍCÍ IS - INFORMATIVNÍ ZÁKRES	
			PODZEMNÍ VEDENÍ NN
			PODZEMNÍ VEDENÍ VN
			NADZEMNÍ VEDENÍ NN
			NADZEMNÍ VEDENÍ VN
			NADZEMNÍ VEDENÍ VVN
			DEŠŤOVÁ KANALIZACE
			PLYNOVOD - STL
			PODZEMNÍ SDĚLOVACÍ VEDENÍ
			VODOVOD

Souřadnicový systém: S-JSTK
Výškový systém Bpv

SO 125 Napojení původní I/16 do MUK Židněves

Ředitelství silnic a dálnic s. p.
Čerčanská 2023/12, Krč, 140 00 Praha 4

Valbek, spol. s r.o.
Vaňurova 505/17
460 07 Liberec 3

HIP:
ING. T. KLIMENT

	Vypracoval	ING. A. DUMANSKA	Zak. číslo	21-LI13-001
	Zodp. projektant	ING. T. KLIMENT	Datum	02/2025
	Tech. kontrola	ING. M. HANŽL	Stupeň	PDPS
	Akce	I/16 MLADÁ BOLESLAV - MARTINOVICE		Počet formátů 8 x A4
Zhotovitel: Valbek, spol. s r.o. Vaňurova 505/17 460 07 Liberec 3	Příloha SITUACE		Měřítka	1 : 1 000
			Č. přílohy	Paré