


**SO 125 - NAPOJENÍ PŮVODNÍ I/16 DO MÚK ŽIDNĚVES
VZOROVÉ PŘÍČNÉ ŘEZY, M 1:50**



OKRUŽNÍ KŘIŽOVATKA D = 60 m

TŘÍDA DOPRAVNÍHO ZATÍŽENÍ I
NÁVRHOVÁ ÚROVEŇ PORUŠENÍ
TYP PODLOŽÍ PIII (D0-A-3)

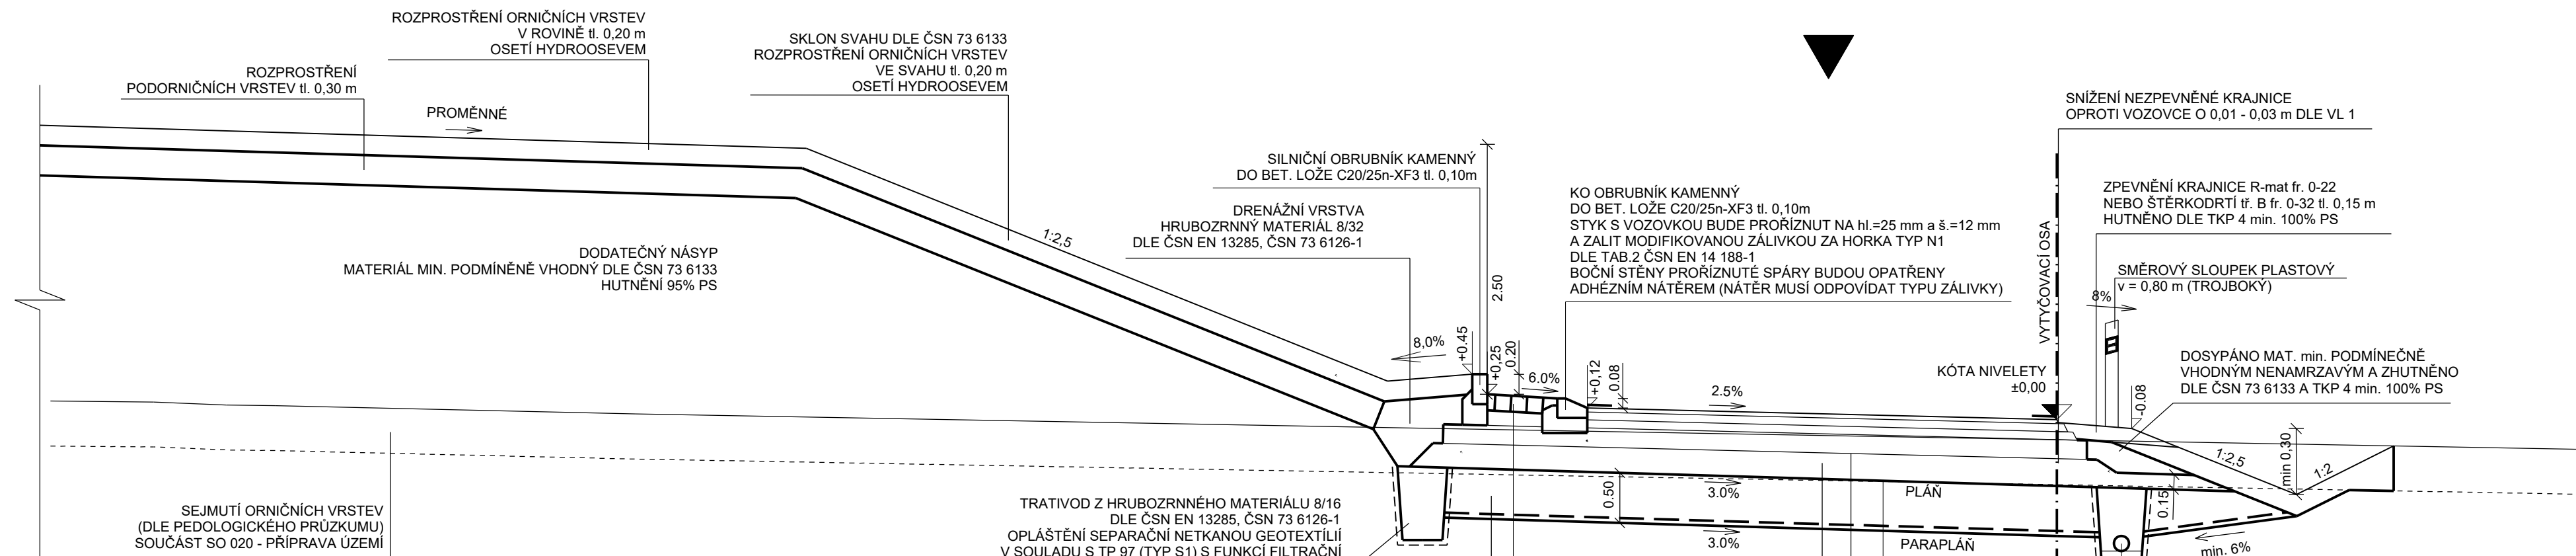

SANACE V ZÁŘEZU - TYP III

PEMÍN V AKTIVNÍ ZÓNĚ ZA ŠD₀ fr.0/125 tl. min. 0,50 m,
NÍ DLE ČSN 73 6133 a TKP, I_c=0,85, E_{od}= min. 45 MPa
TKANÁ SEPARAČNÍ GEOTEXTILIE TYP S2 DLE TP 97
ÚPRAVA ZÁKLADOVÉ SPÁRY
VTNĚNÍ DLE ČSN 73 6133 a TKP od >92% PS, IBI ≥ 5%

KAMENNÁ DLÁŽBA 160 x 160 mm	DL 160	160 mm	ČSN 73 6131, TP 192
LOŽNÍ VRSTVA Z BETONU C20/25n - XF3.	L	min. 100 mm	ČSN EN 206
VYSPAROVANO CEMENTOVOU MALTOU M25-XF4			
VRSTVA ZE SMĚSI STĚLELENÉ CEMENTEM	SC 0/32 C ₁₀	190 mm	ČSN EN 14 227-1, ČSN 73 6124
ŠTĚRKODRŮT tř. A ₁ (0/32 G ₅)	ŠD _A	min. 250 mm	ČSN EN 13 285, ČSN 73 6126-1
CELKEM		min. 700 mm	



ASFALTOVÝ KOBEREC MASTIKOVÝ ASFALETOVÝ PODKLAD S PODCENÍM PVRCHU KAMENIVO fr. 2/4 v MNOŽSTVÍ 1,5 kg/2	SMA 11 S	40 mm	ČSN EN 13 108-5, ČSN 73 6121
PMB 45/80-65			
SPJOVACÍ POSTŘIK EMULZNÍ STŘEDNĚŠTĚPNÝ S MODIFIKOVANÝM ASFALEM	PS-CP	0,35 kg/m ²	ČSN EN 13 808, ČSN 73 6129, ČSN 73 6121
ASFALTOVÝ BETON MODIFIKOVANÝ PRO LOŽNÍ VRSTVU	ACL 22S	80 mm	ČSN EN 13 108-1, ČSN 73 6121
PMB 25/55-60			
SPJOVACÍ POSTŘIK EMULZNÍ STŘEDNĚŠTĚPNÝ S MODIFIKOVANÝM ASFALEM	PS-CP	0,35 kg/m ²	ČSN EN 13 808, ČSN 73 6129, ČSN 73 6121
ASFALTOVÝ BETON PRO PODKLADNÍ VRSTVY	ACP 22 S	80 mm	ČSN EN 13 108-1, ČSN 73 6121
ASFALT 50/70			
SMĚS Z KAMENIVA STMELENA CEMENTEM (0/32)	SC 0/32 C _{50/60}	190 mm	ČSN EN 13 108-1, ČSN 73 6121
ŠTERKODŘť. A. (0/63 GE)	ŠD,	min. 250 mm	ČSN EN 13 285, ČSN 73 6126-1

CELKEM min. 640 mm

POZN. NA PODKLADNÍCH VRSTVÁCH Z SC PROVÉST OPATŘENÍ K VÝVOJI REFLEXNÍCH TRHLIN DLE TP 170, ČSN 73 6124-1

NÁVRHOVÁ KATEGORIE S 9,5/60

TŘÍDA DOPRAVNÍHO ZATÍŽENÍ
NÁVRHOVÁ ÚROVEŇ PORUŠENÍ
TYP PODLOŽÍ PIII (D1-A-2)

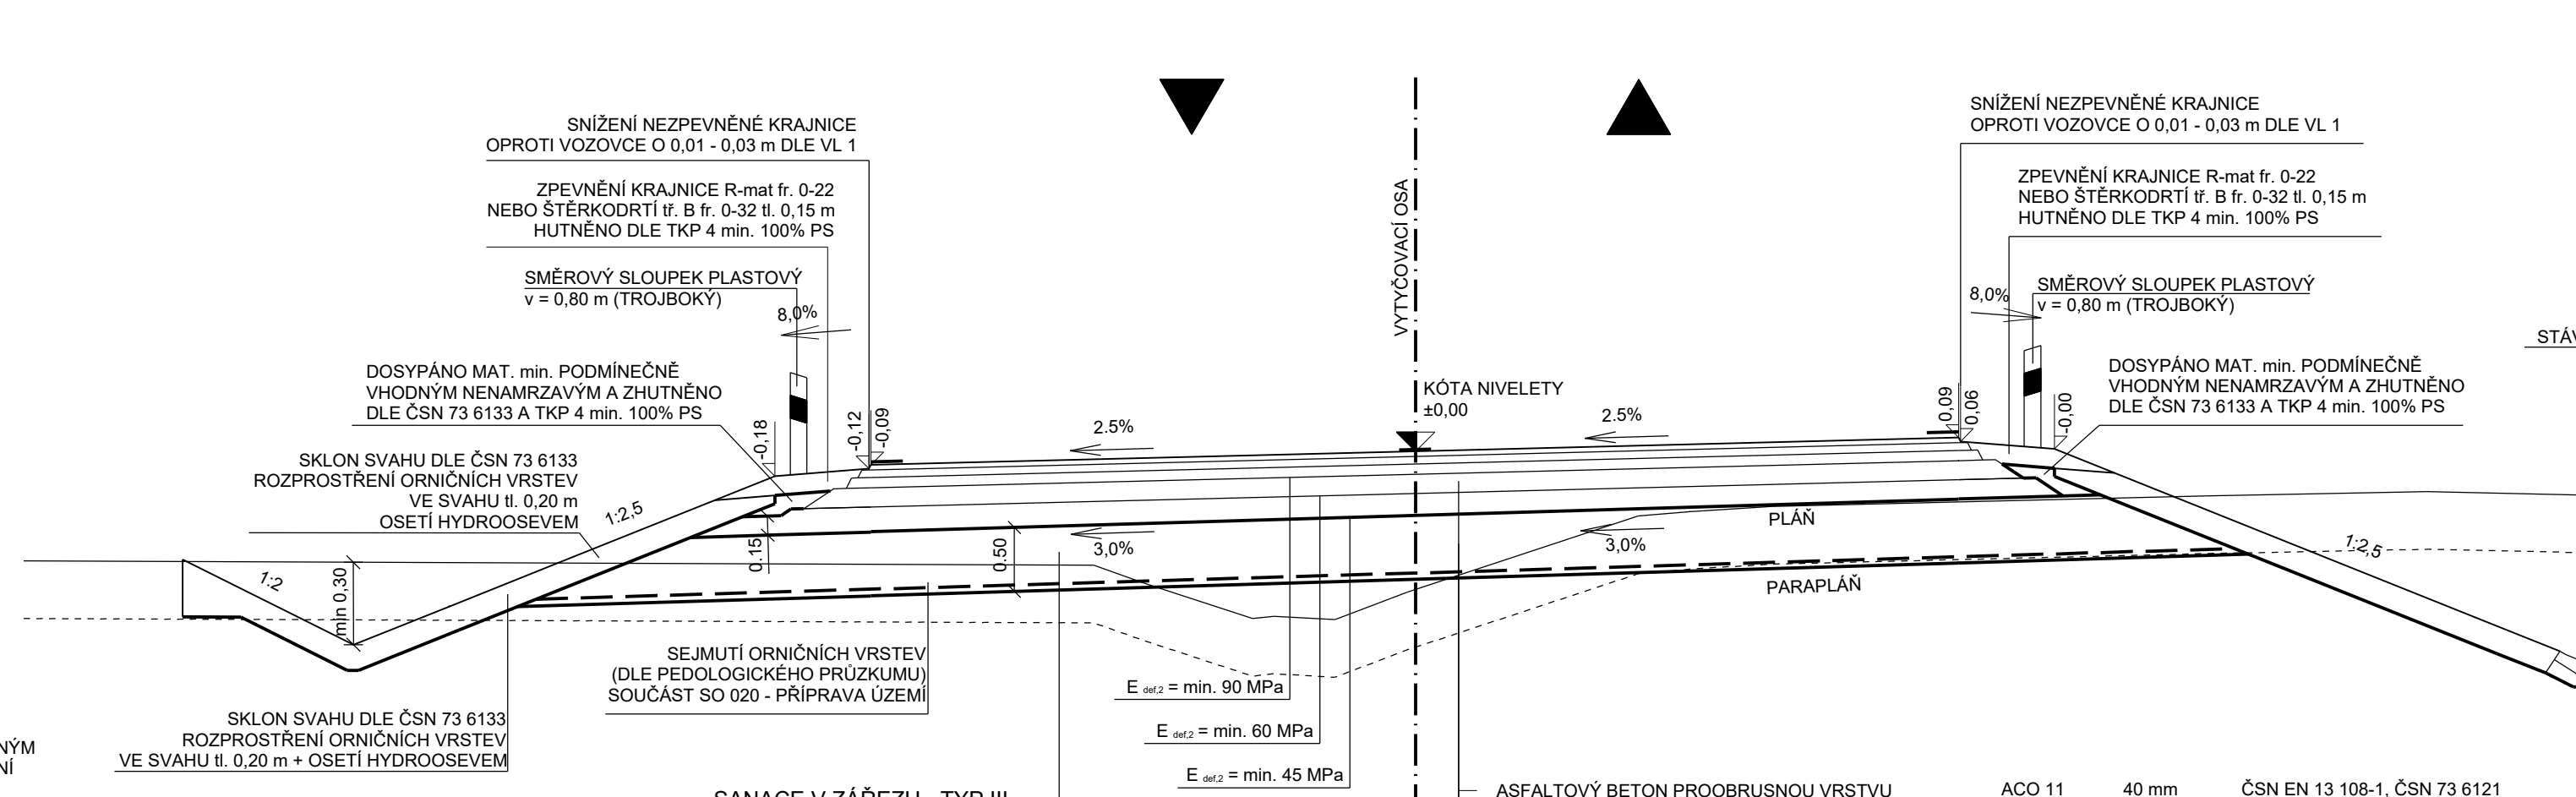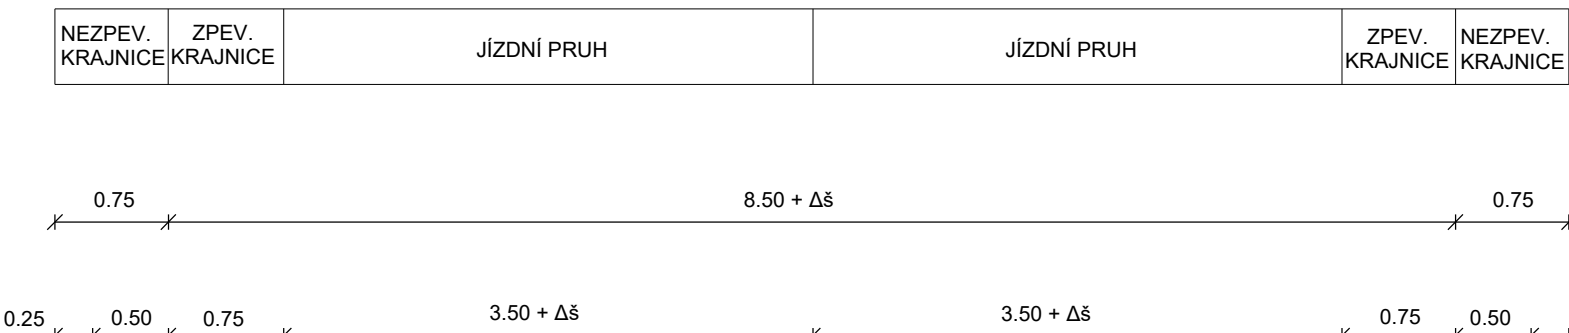


SANACE V ZÁŘEZU - TYP III

VÝMĚNA ZEMIN V AKTIVNÍ ZÓNE ZA ŠD₆ fr.0/125 tl. min. 0,50 m,
HUTNĚNÍ DLE ČSN 73 6133 a TKP, $i_0=0,85$, $e_{cr,0.95}$ min. 45 MPa
NETKANÁ SEPARAČNÍ GEOTEXTILIE TYP S2 DLE TP 97
ÚPRAVA ZÁKLADOVÉ SPÁRY,
HUTNĚNÍ DLE ČSN 73 6133 a TKP od >92% PS, I_{BI} ≥ 5%


ASFALTOVÝ BETON PROOBRUSNOU VRSTVU ASFALT 50/70	ACO 11	40 mm	ČSN EN 13 108-1, ČSN 73 6121
SPOJOVACÍ POŠTRK EMULZNÍ STŘEDNĚSTĚPNÝ	PS-C	0,35 kg/m ²	ČSN EN 13 808, ČSN 73 6129, ČSN 73 6126-1
ASFALTOVÝ BETON PRO LOŽNÍ VRSTVU ASFALT 50/70	ACL 16+	60 mm	ČSN EN 13 108-1, ČSN 73 6121
POŠTRK EMULZNÍ STŘEDNĚSTĚPNÝ	PS-C	0,35 kg/m ²	ČSN EN 13 808, ČSN 73 6129, ČSN 73 6126-1
ASFALTOVÝ BETON PRO PODKLADNÍ VRSTVU ASFALT 50/70	ACP 16+	80 mm	ČSN EN 13 108-1, ČSN 73 6121
INFILTRAČNÍ POŠTRK EMULZNÍ VČETNĚ PODPORCENÍ KAMENIVÝ PR. 214 V MNOŽSTVÍ 3,0 kg/m ²	PI-C	1,00 kg/m ²	ČSN 73 6129
ŠTĚRKODRŮT A. (0/32 GE)	ŠD.	150 mm	ČSN EN 13 285, ČSN 73 6126-1
	ŠD.	min. 150 mm	ČSN EN 13 285, ČSN 73 6126-1

CELKEM	min. 480 m
--------	------------


DETAIL NAPOJENÍ NOVÉ KONSTRUKCE NA STÁVAJÍCÍ V PŘÍČNÉM SMĚRU

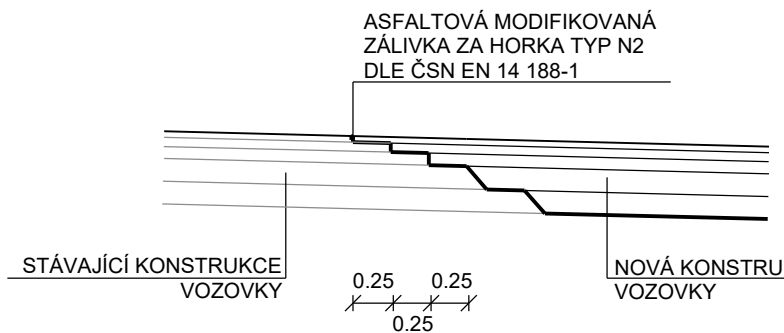

DETAIL NAPOJENÍ NOVÉ KONSTRUKCE NA STÁVAJÍCÍ V PODÉLNÉM SMĚRU

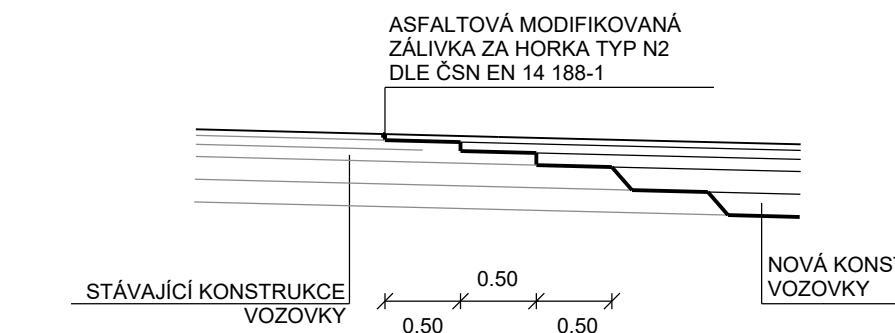


DETAIL DĚLÍČÍHO OSTRŮVKU

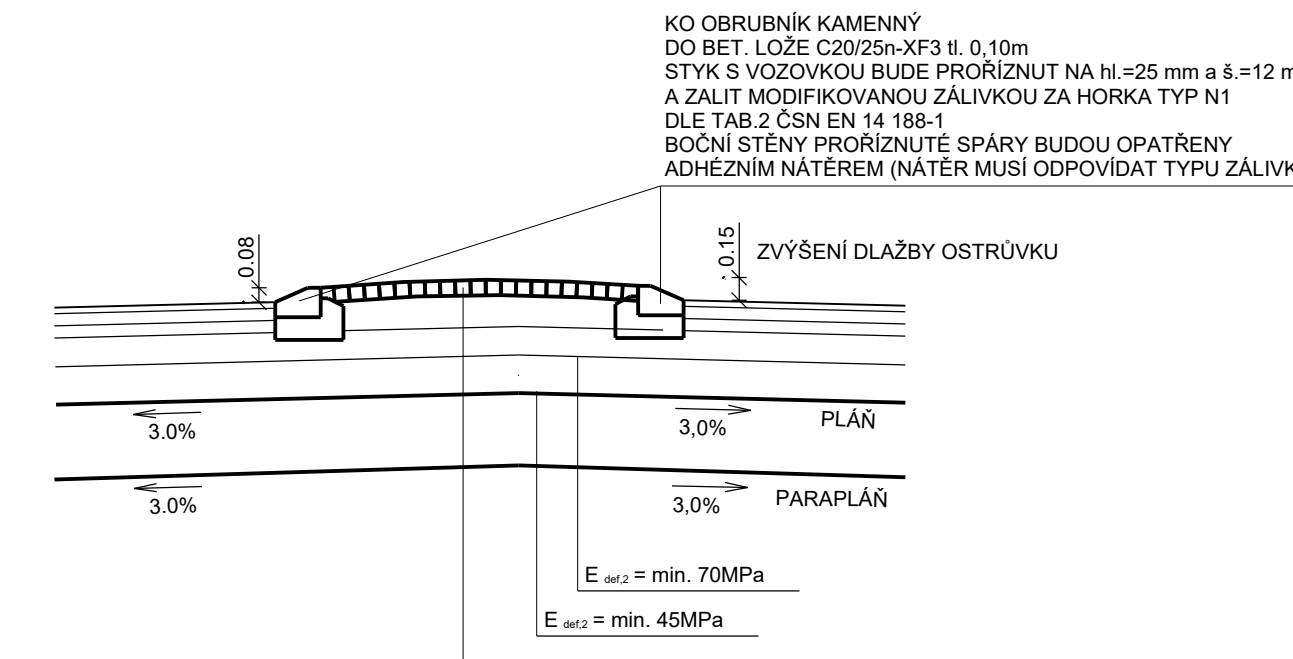


KAMENNÁ DLÁŽBA 100 x 100 mm VYSPAROVANÁ CEMENTOVOU MALTOU M25-XF4 LOŽNÍ VRSTVA Z BETONU C20/25n - XF3, VRSTVA ZE SMĚSI STIHLNÉHO CEMENTEM ŠTERKODU II. A, (0/32 G ₅)	DL 100 L SC 0/32 C ₅₀ SD _A	100 mm min. 180 mm 190 mm min. 250 mm	ČSN 73 6131, TP 192 ČSN EN 206 ČSN EN 14 227-1, ČSN 73 6124- ČSN EN 13 285, ČSN 73 6126-1
CEMENT		720 mm	

DETAILY ZPEVNĚNÍ PŘÍKOPŮ

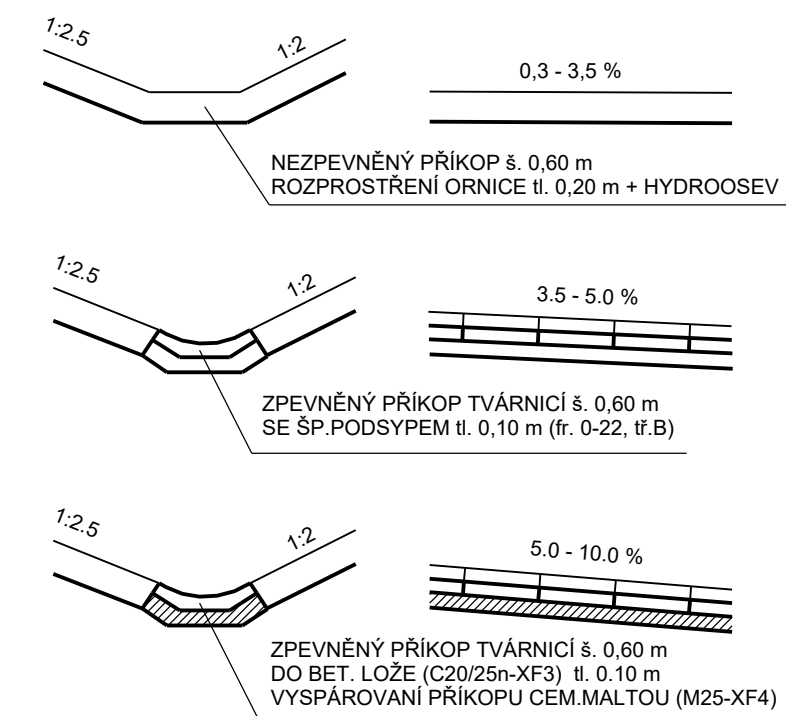

SO 125 Napojení původní I/16 do MUK Židněves

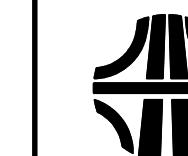Objednatel:

**ŘEDITELSTVÍ
SILNIC
A DÁLNIC**

Ředitelství silnic a dálnic s. p.
Čerčanská 2023/12, Krč, 140 00 Praha 4

Zhotovitel:



Valbek, spol. s r.o.
Vaňurova 505/17
460 07 Liberec 3

	HIP:
--	------

ING. T. KLIMENT

	Vypracoval	ING. A. DUMANSKA		Zak. číslo	21-LI13-001	
	Zodp. projektant	ING. T. KLIMENT		Datum	02/2025	
	Tech. kontrola	ING. M. HANŽL		Stupeň	PDPS	
	Akce	I/16 MLADÁ BOLESLAV - MARTINOVICE			Počet formátů	5 x A4
Zhotovitel: Valbek, spol. s r.o. Vaňurova 505/17 460 07 Liberec 3	Příloha	VZOROVÉ PŘÍČNÉ ŘEZY			Mřížkito	1 : 50
					Č. přílohy	Paré
					4	