




SO 125 - NÁPOJENÍ PŮVODNÍ I/16 DO MÚK ŽIDNĚVES
PŘÍČNÉ ŘEZY, OKRUŽNÍ KŘÍŽOVATKA
M 1:100

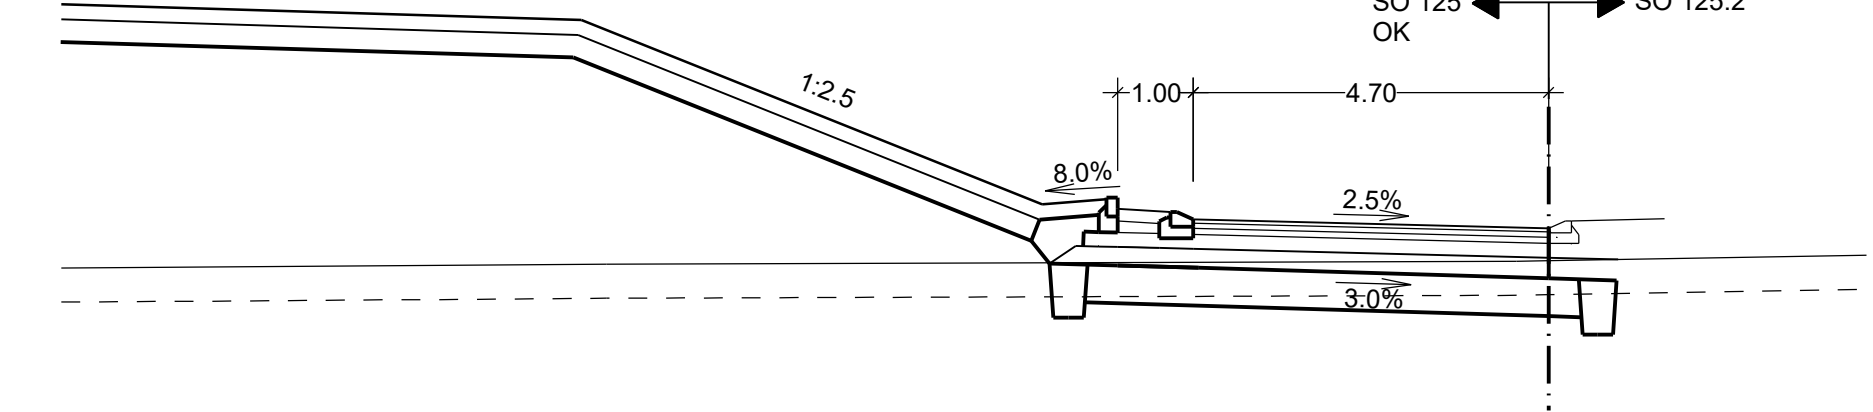


PROJEKTOVANÝ STAV	S. R. 217 m	-12.80	223.29	-6.70	220.85	-5.85	220.92	-5.70	220.79	-5.00	220.93	-5.00	220.94	-4.70	220.65	-4.70	220.61	0.00	220.53
ODSAZENÍ OD OSY		-12.80	223.29	-6.70	220.85	-5.85	220.92	-5.70	220.79	-5.00	220.93	-5.00	220.94	-4.70	220.65	-4.70	220.61	0.00	220.53
STÁVAJÍCÍ TERÉN		-12.46	220.06															-0.43	220.10
ODSAZENÍ OD OSY		-12.46	220.06															0.00	220.10

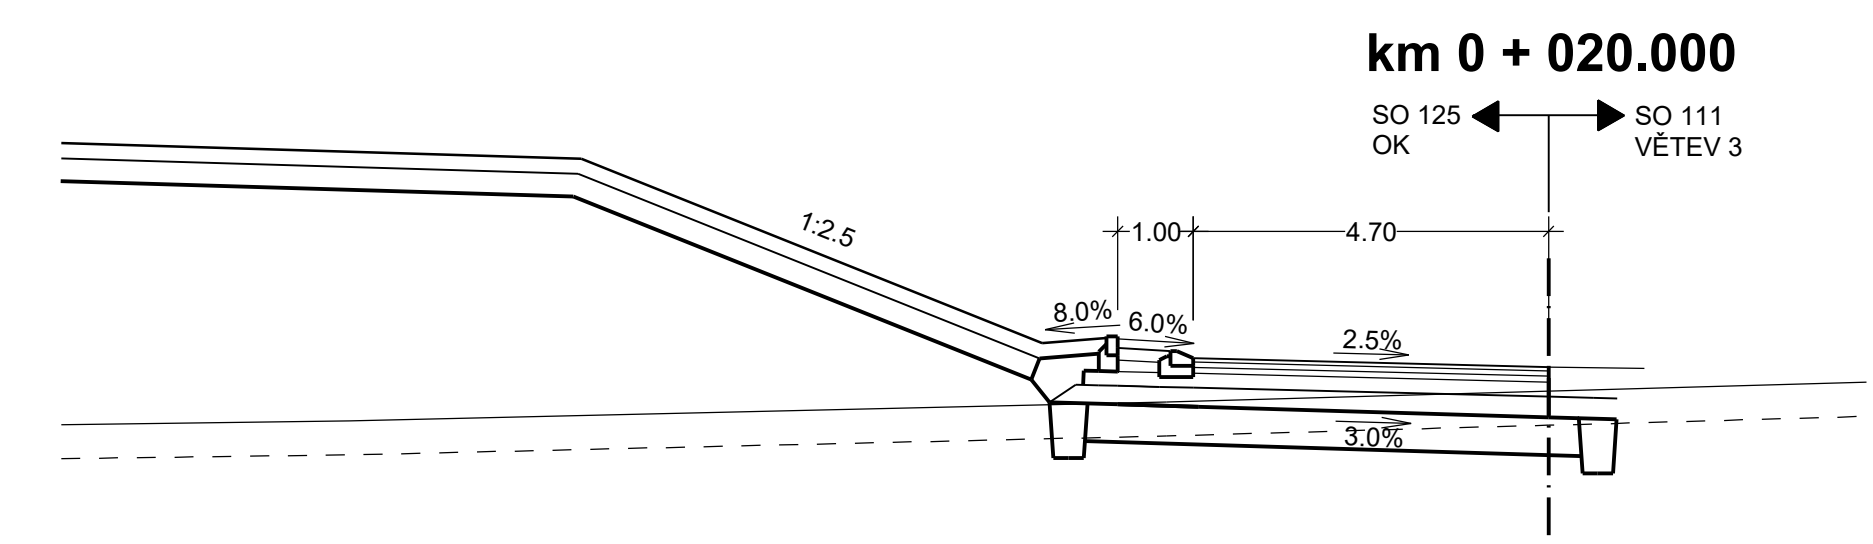


PROJEKTOVANÝ STAV	S. R. 217 m	-12.80	223.59	-6.70	221.15	-5.85	221.22	-5.70	221.09	-5.00	220.93	-5.00	221.04	-4.70	220.95	-4.70	220.91	0.00	220.83
ODSAZENÍ OD OSY		-12.80	223.59	-6.70	221.15	-5.85	221.22	-5.70	221.09	-5.00	220.93	-5.00	221.04	-4.70	220.95	-4.70	220.91	0.00	220.83
STÁVAJÍCÍ TERÉN															-5.05	220.37		0.00	220.51
ODSAZENÍ OD OSY															-5.05	220.37		0.00	220.51

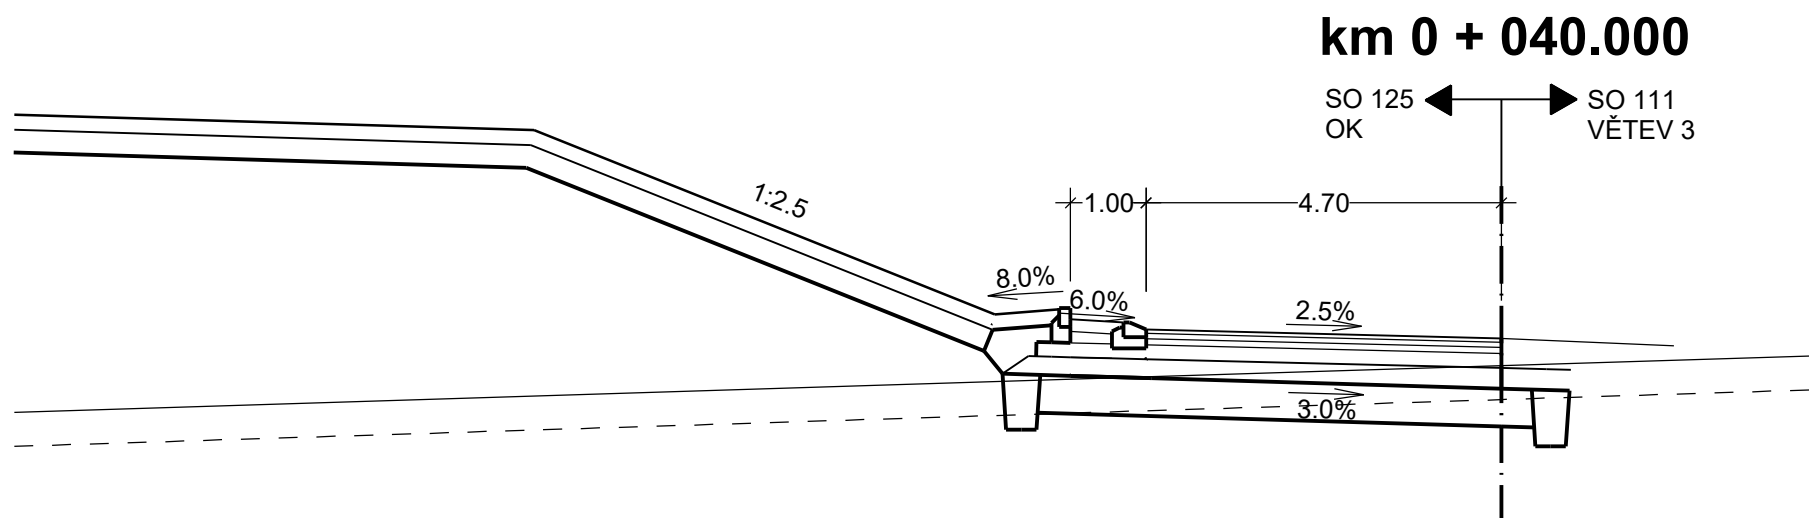


PROJEKTOVANÝ STAV	S. R. 217 m	-12.80	223.85	-6.70	221.41	-5.85	221.48	-5.70	221.35	-5.00	221.19	-5.00	221.31	-4.70	221.17	-4.70	221.17	0.00	221.10
ODSAZENÍ OD OSY		-12.80	223.85	-6.70	221.41	-5.85	221.48	-5.70	221.35	-5.00	221.19	-5.00	221.31	-4.70	221.17	-4.70	221.17	0.00	221.10
STÁVAJÍCÍ TERÉN																		0.00	220.74
ODSAZENÍ OD OSY																		0.00	220.74

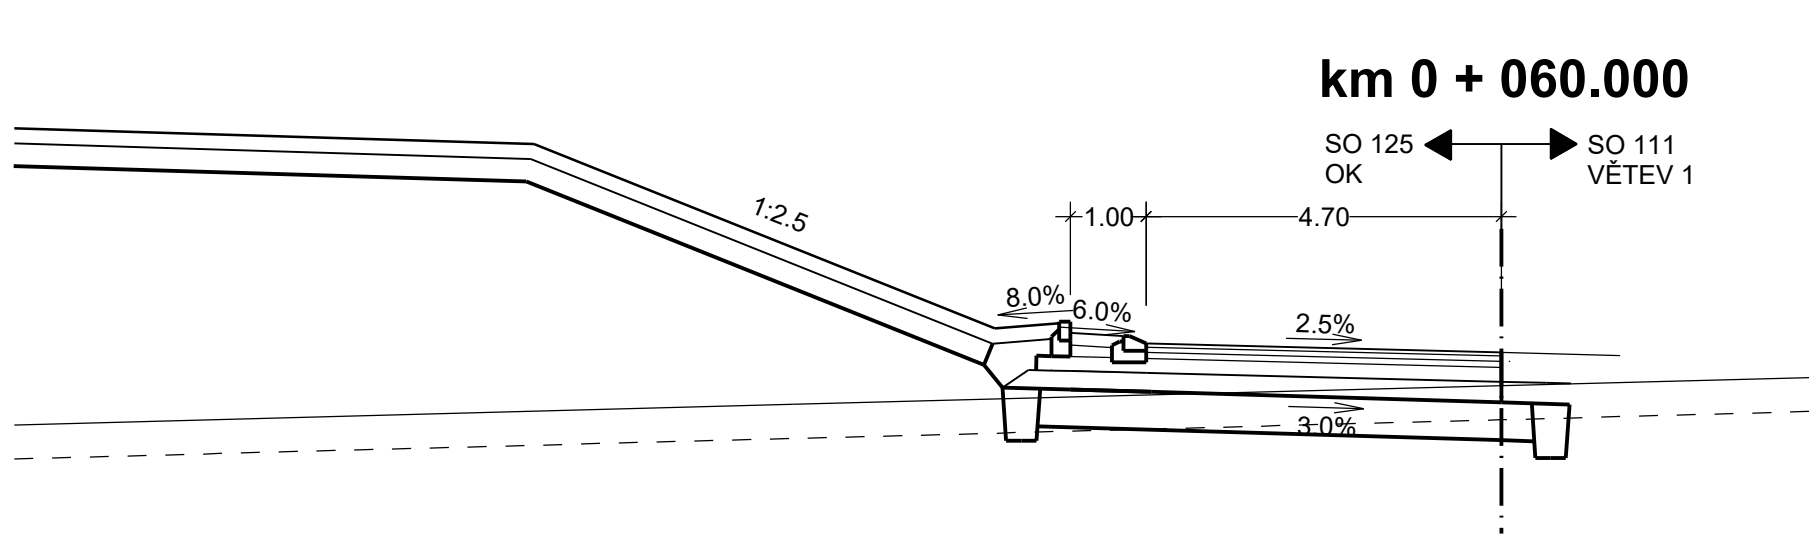


PROJEKTOVANÝ STAV	S. R. 217 m	-12.80	223.78	-6.70	221.35	-5.85	221.41	-5.70	221.28	-5.00	221.12	-5.00	221.24	-4.70	221.15	-4.70	221.11	0.00	221.03
ODSAZENÍ OD OSY		-12.80	223.78	-6.70	221.35	-5.85	221.41	-5.70	221.28	-5.00	221.12	-5.00	221.24	-4.70	221.15	-4.70	221.11	0.00	221.03
STÁVAJÍCÍ TERÉN																		0.00	220.58
ODSAZENÍ OD OSY																		0.00	220.58

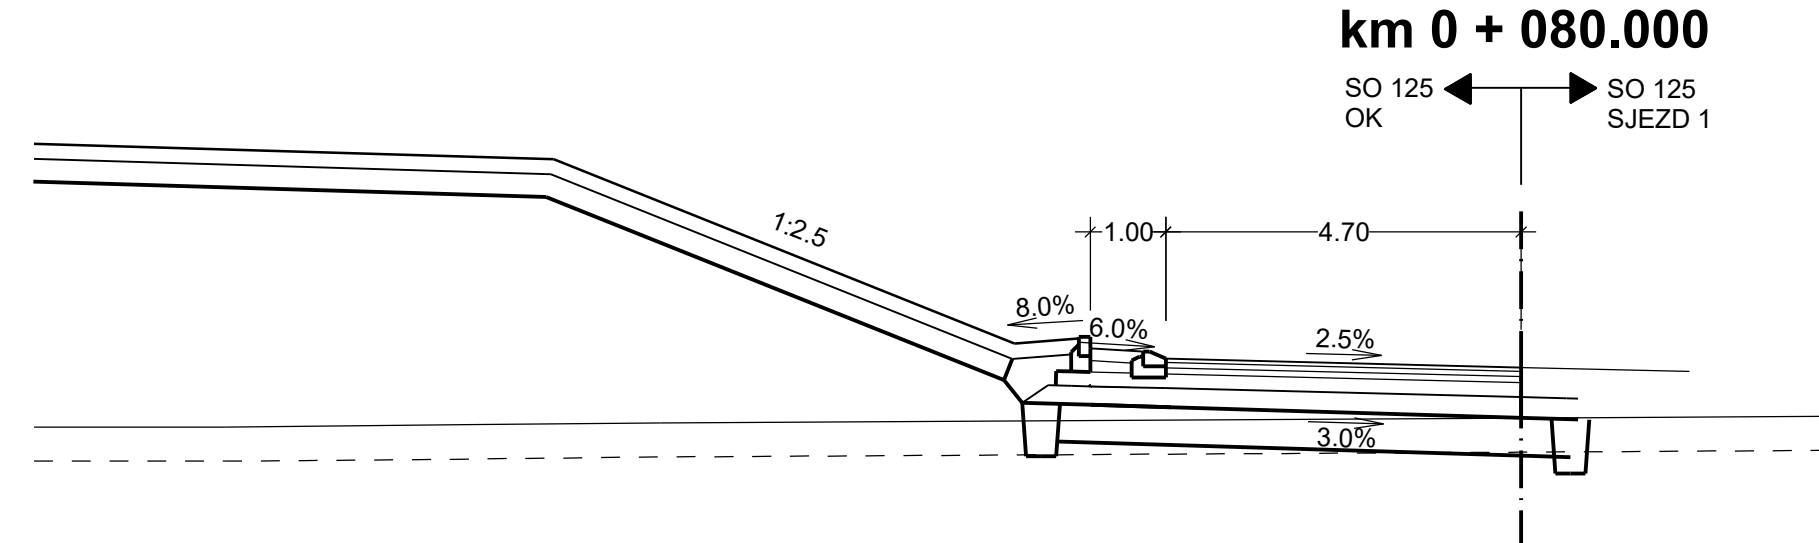


PROJEKTOVANÝ STAV	S. R. 217 m	-12.80	223.47	-6.70	221.03	-5.85	221.10	-5.70	220.97	-5.00	220.81	-5.00	220.92	-4.70	220.83	-4.70	220.79	0.00	220.71
ODSAZENÍ OD OSY		-12.80	223.47	-6.70	221.03	-5.85	221.10	-5.70	220.97	-5.00	220.81	-5.00	220.92	-4.70	220.83	-4.70	220.79	0.00	220.71
STÁVAJÍCÍ TERÉN		-13.85	219.96															0.00	220.04
ODSAZENÍ OD OSY		-13.85	219.96															0.00	220.04

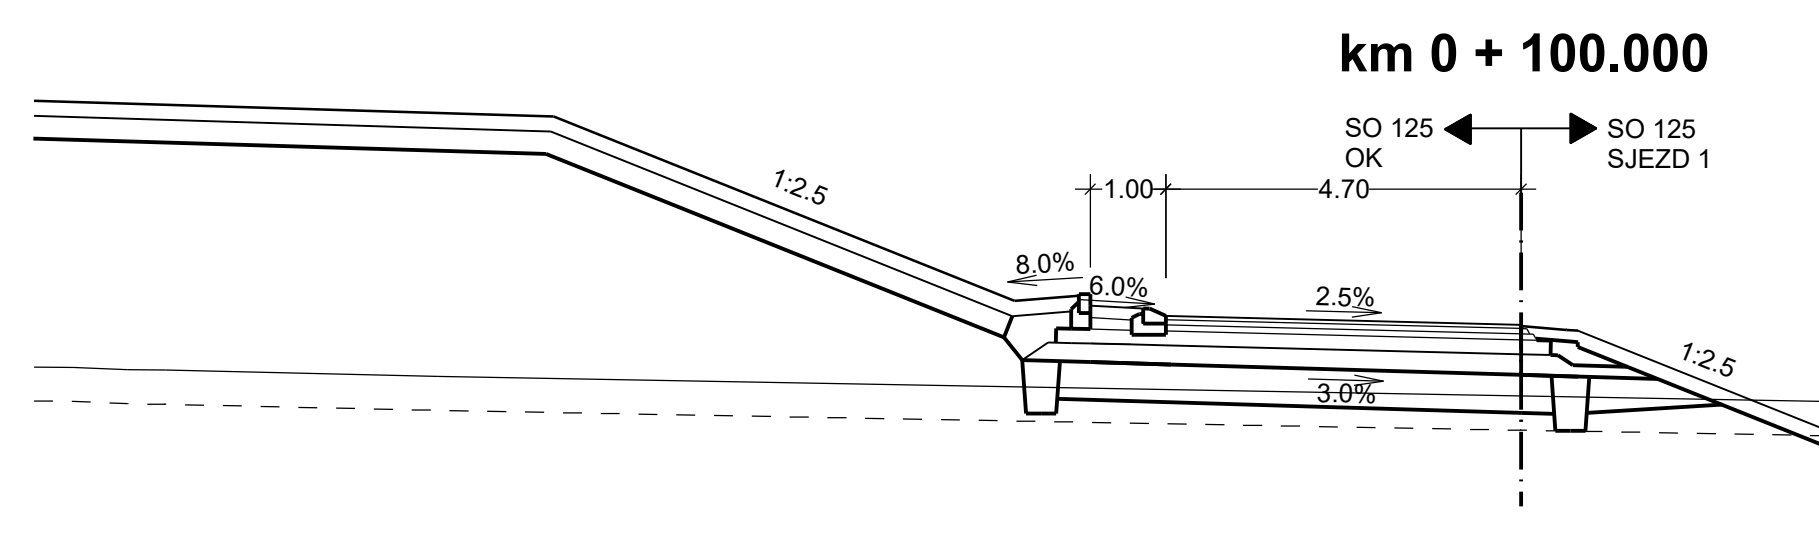


PROJEKTOVANÝ STAV	S. R. 216 m	-12.80	223.15	-6.70	220.71	-5.85	220.78	-5.70	220.65	-5.00	220.49	-5.00	220.61	-4.70	220.51	-4.70	220.47	0.00	220.39
ODSAZENÍ OD OSY		-12.80	223.15	-6.70	220.71	-5.85	220.78	-5.70	220.65	-5.00	220.49	-5.00	220.61	-4.70	220.51	-4.70	220.47	0.00	220.39
STÁVAJÍCÍ TERÉN																		0.00	219.45
ODSAZENÍ OD OSY																		0.00	219.45

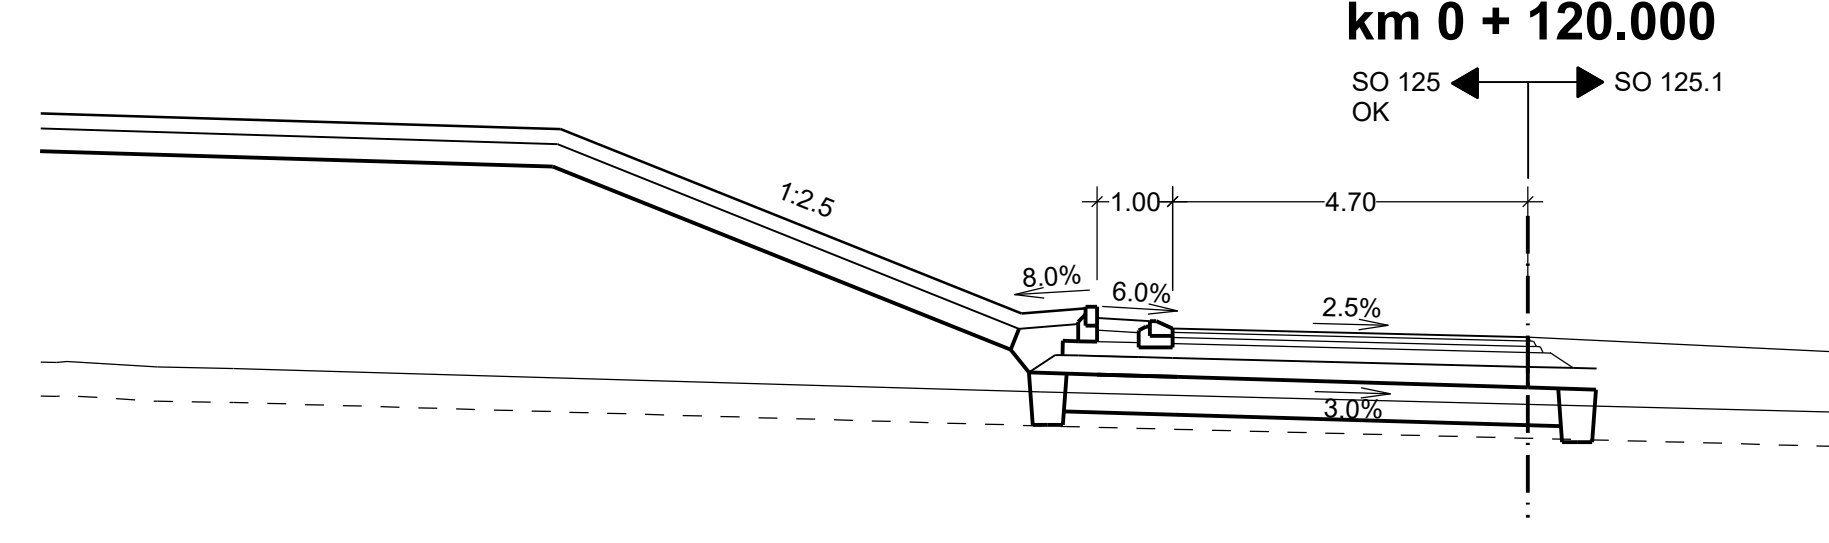


PROJEKTOVANÝ STAV	S. R. 216 m	-12.80	222.87	-6.70	220.43	-5.85	220.50	-5.70	220.37	-5.00	220.21	-5.00	220.33	-4.70	220.19	-4.70	220.19	0.00	220.11
ODSAZENÍ OD OSY		-12.80	222.87	-6.70	220.43	-5.85	220.50	-5.70	220.37	-5.00	220.21	-5.00	220.33	-4.70	220.19	-4.70	220.19	0.00	220.11
STÁVAJÍCÍ TERÉN																		-6.45	219.39
ODSAZENÍ OD OSY																		-6.45	219.39

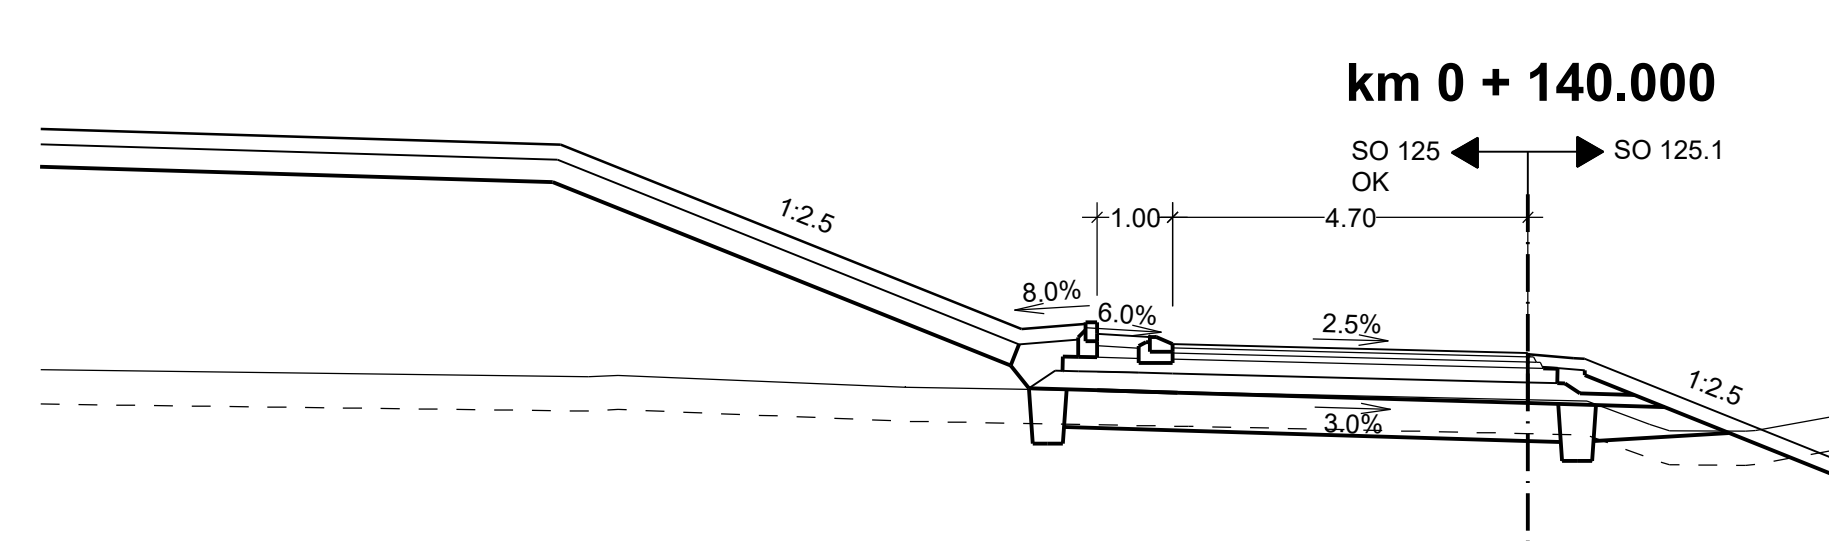

PROJEKTOVANÝ STAV	S. R. 216 m	-12.80	222.77	-6.70	220.34	-5.85	220.40	-5.70	220.27	-5.00	220.11	-5.00	220.23	-4.70	220.14	-4.70	220.10	0.00	220.02
ODSAZENÍ OD OSY		-12.80	222.77	-6.70	220.34	-5.85	220.40	-5.70	220.27	-5.00	220.11	-5.00	220.23	-4.70	220.14	-4.70	220.10	0.00	220.02
STÁVAJÍCÍ TERÉN		-12.43	219.70															0.78	219.38
ODSAZENÍ OD OSY		-12.43	219.70															0.78	219.38

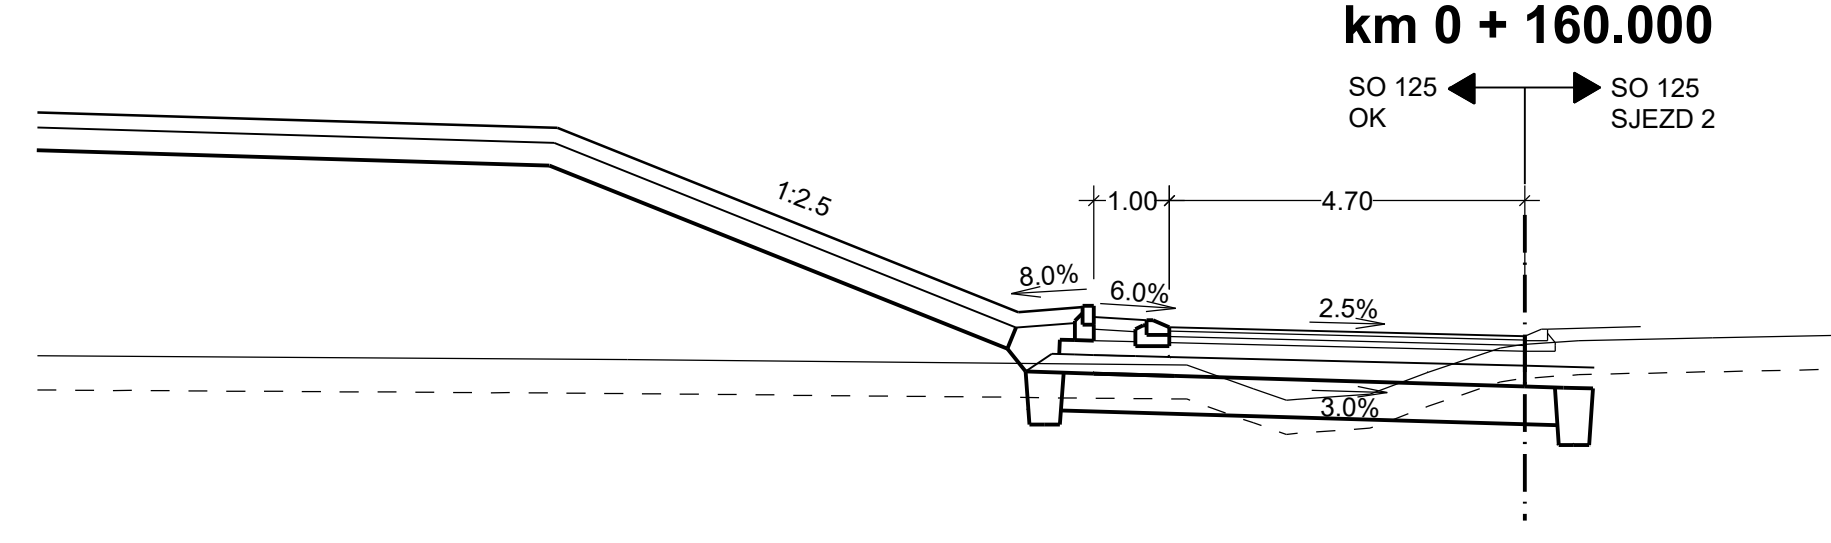

PROJEKTOVANÝ STAV	S. R. 216 m	-12.80	222.88	-6.70	220.44	-5.85	220.51	-5.70	220.38	-5.00	220.22	-5.00	220.34	-4.70	220.24	-4.70	220.20	0.00	220.13
ODSAZENÍ OD OSY		-12.80	222.88	-6.70	220.44	-5.85	220.51	-5.70	220.38	-5.00	220.22	-5.00	220.34	-4.70	220.24	-4.70	220.20	0.00	220.13
STÁVAJÍCÍ TERÉN		-11.87	219.82															-4.47	219.75
ODSAZENÍ OD OSY		-11.87	219.82															-4.47	219.75

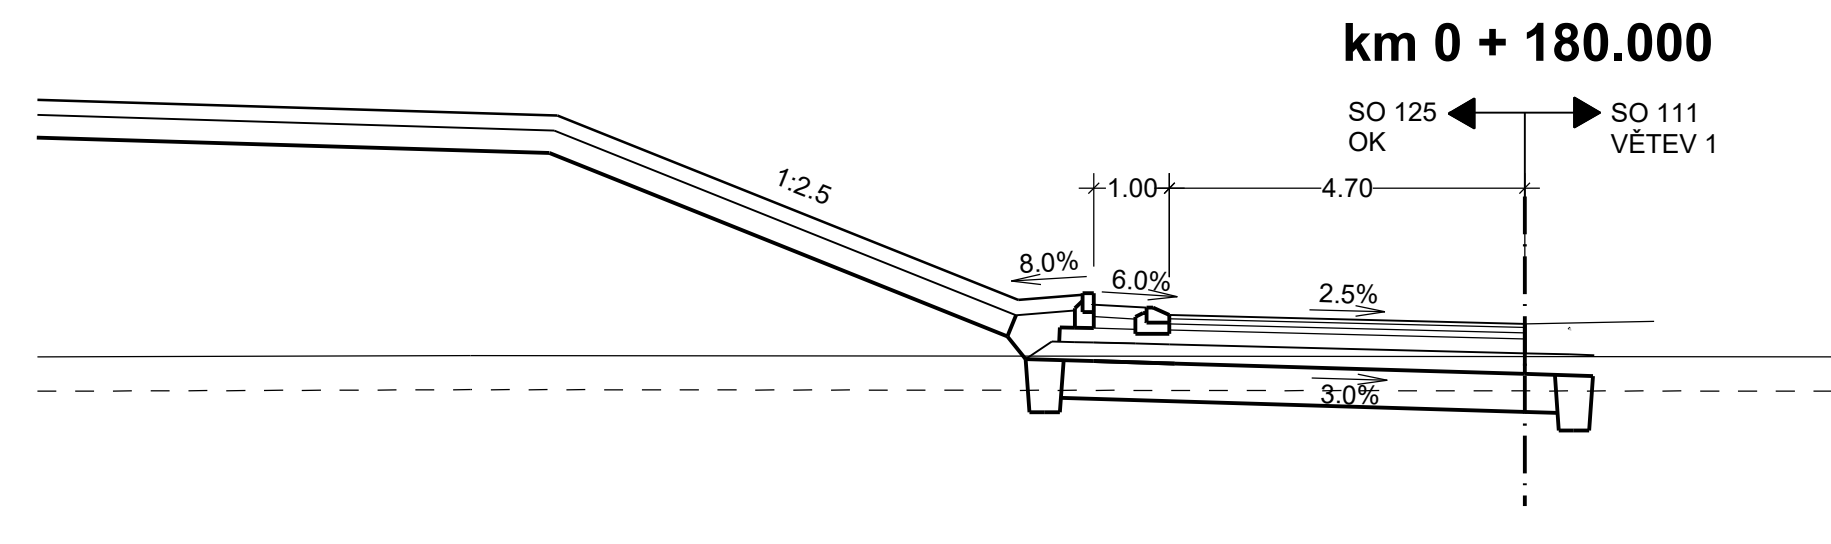

PROJEKTOVANÝ STAV	S. R. 216 m	-12.80	223.16	-6.70	220.72	-5.85	220.79	-5.70	220.66	-5.00	220.50	-5.00	220.62	-4.70	220.52	-4.70	220.48	0.00	220.41
ODSAZENÍ OD OSY		-12.80	223.16	-6.70	220.72	-5.85	220.79	-5.70	220.66	-5.00	220.50	-5.00	220.62	-4.70	220.52	-4.70	220.48	0.00	220.41
STÁVAJÍCÍ TERÉN		-13.95	219.98															0.00	219.97
ODSAZENÍ OD OSY		-13.95	219.98															0.00	219.97

Výškový systém: Bpv

SO 125 Napojení původní I/16 do MUK Židněves

Objednatel:



Ředitelství silnic a dálnic s. p.
Čerčanská 2023/12, Krč, 140 00 Praha 4

Zhotovitel:



Valbek, spol. s r.o.
Vaňurova 505/17
460 07 Liberec 3

HIP:

ING. T. KLIMENT



Vypracoval	ING. A. DUMANSKA	Zak. číslo	21-L113-001	
Zodp. projektant	ING. T. KLIMENT	Datum	02/2025	
Tech. kontrola	ING. M. HANŽL	Stupeň	PDPs	
Akce	I/16 MLADÁ BOLESLAV - MARTINOVICE		Počet formátů	7 x A4
Měřítka			1 : 100	
Č. přílohy			Paré	
5.1				
Příloha	PŘÍČNÉ ŘEZY, OKRUŽNÍ KŘÍŽOVATKA			

Zhotovitel:
Valbek, spol. s r.o.
Vaňurova 505/17
460 07 Liberec 3

Příloha
PŘÍČNÉ ŘEZY, OKRUŽNÍ KŘÍŽOVATKA