
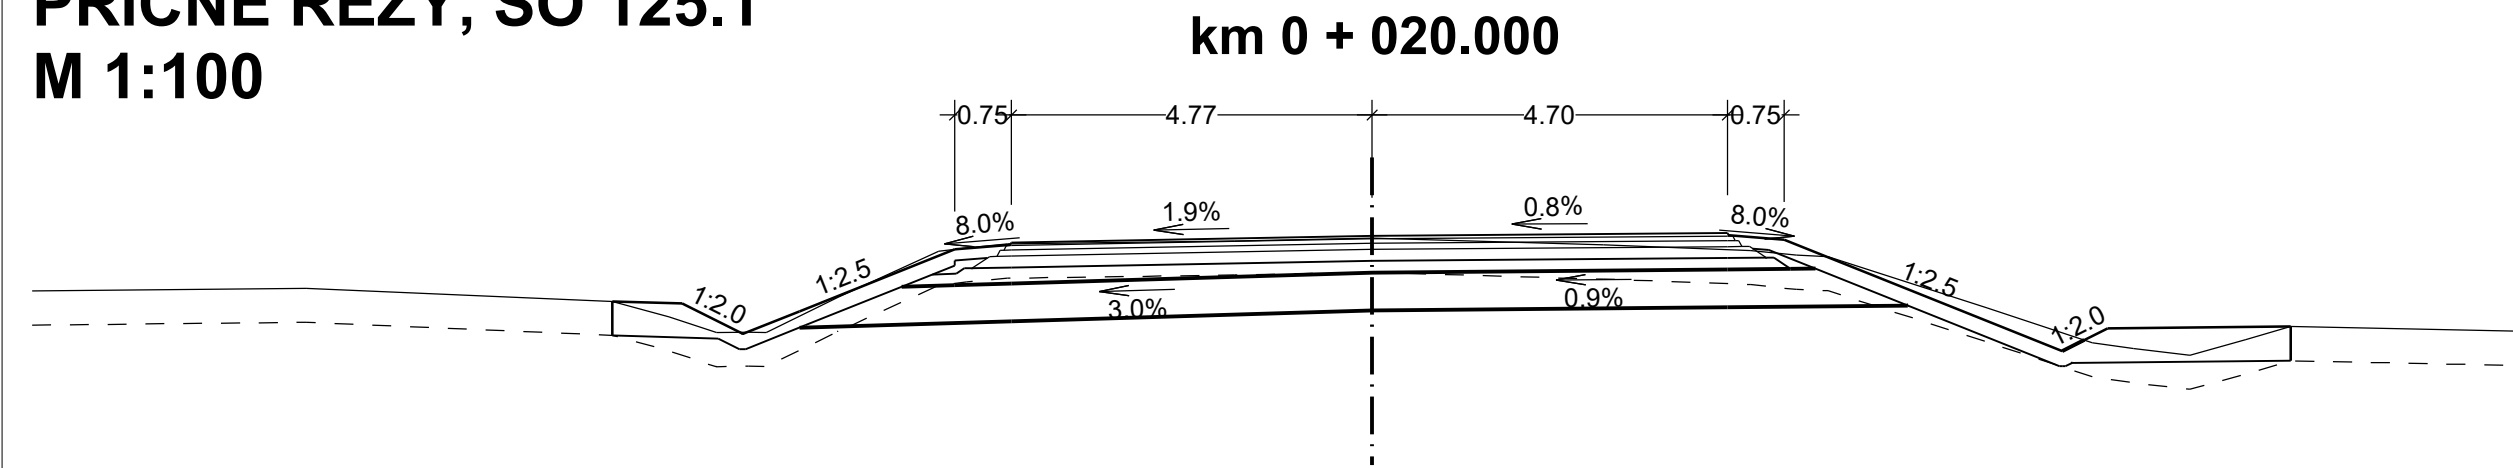
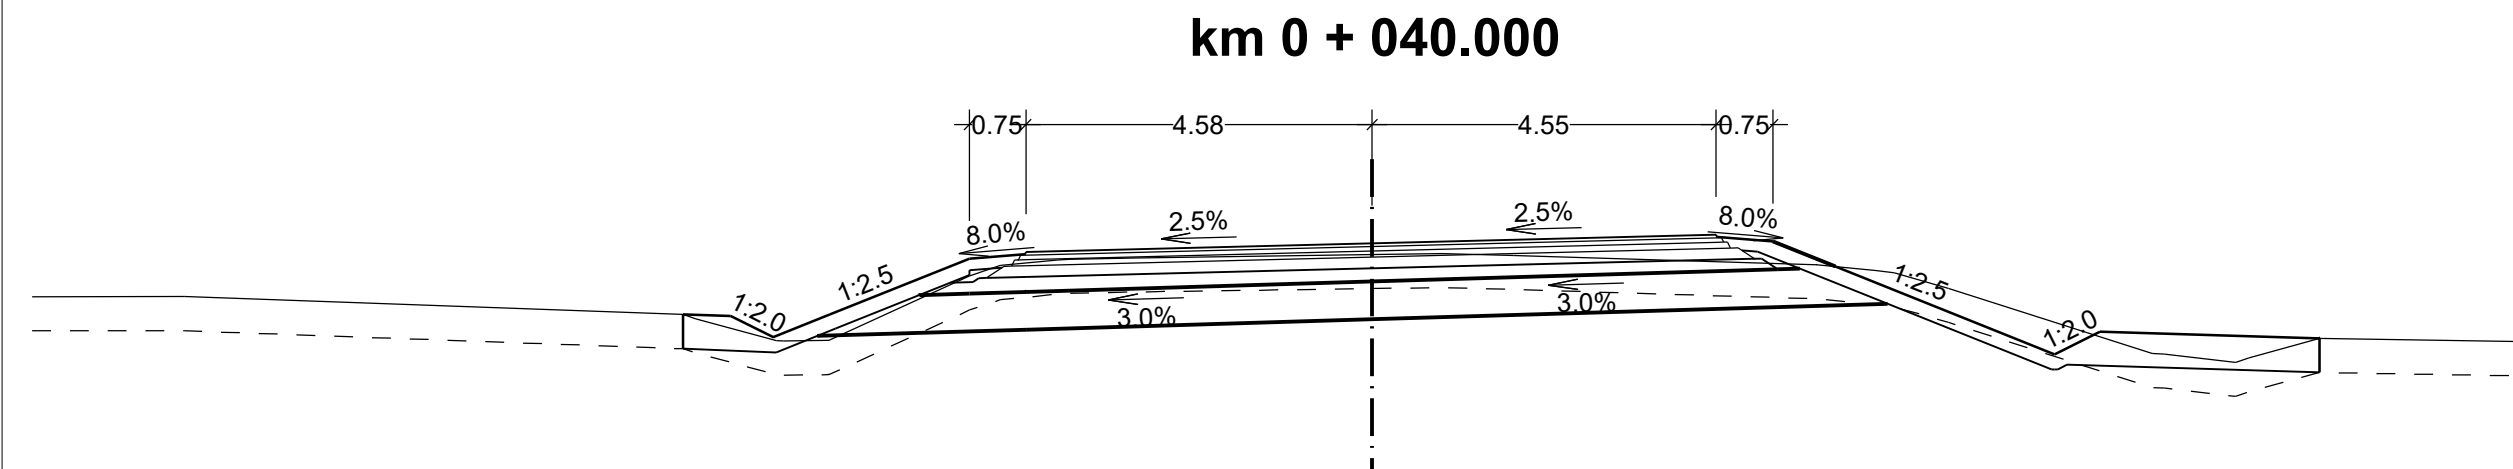




SO 125 - NAPOJENÍ PŮVODNÍ I/16 DO MÚK ŽIDNĚVES
PŘÍČNÉ ŘEZY, SO 125.1
M 1:100 **km 0 + 020.000**

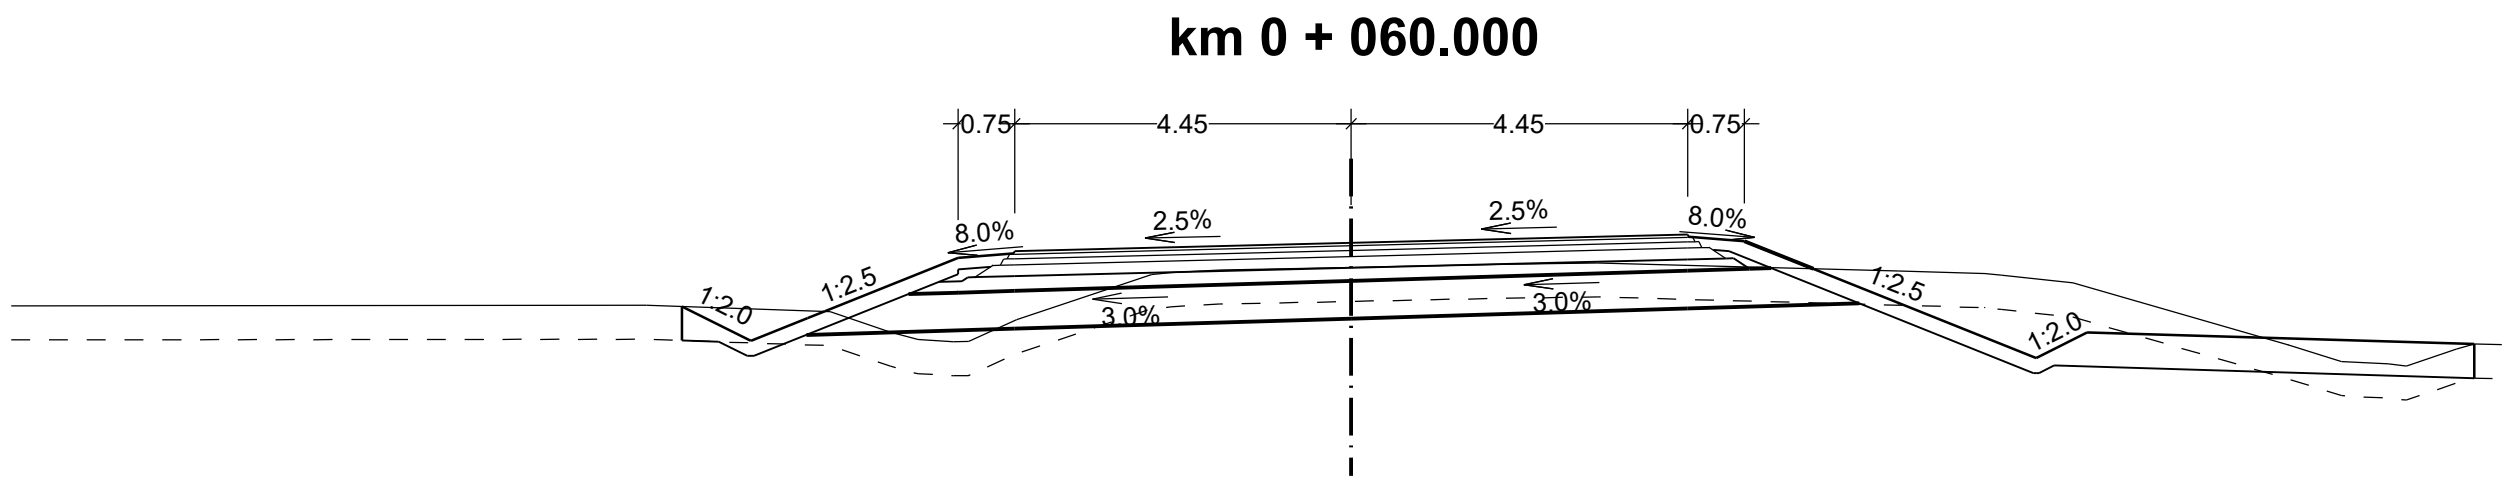

		S. R. 214 m	
PROJEKTOVANÝ STAV	ODSAZENÍ OD OSY	-10,05 217,98 -10,05 217,53	-9,11 217,95 -8,31 217,55 -7,56 217,85
STÁVAJÍCÍ TERÉN	ODSAZENÍ OD OSY	-10,05 217,98 -9,30 217,78 -8,67 217,57 -8,25 217,57 -8,01 217,57 -7,07 218,03	-5,52 218,66 -4,79 218,72 -4,79 218,71 -4,77 218,75
		-1,82 218,78	0,00 218,85
		3,06 218,73	4,70 218,94 4,72 218,90 4,72 218,91 5,45 218,85
		8,13 217,90	9,28 217,32 9,88 217,63
		10,82 217,27	12,15 217,65 12,15 217,20

[illegible]

		S. R. 214 m	
PROJEKTOVANÝ STAV		-8.85	218.20
ODSAZENÍ OD OSY		-8.85	217.75
		-7.94	217.75
		-7.19	218.05
		-6.97	218.14
		-5.20	218.85
		-4.47	218.91
		-4.47	218.89
		-4.45	218.94
		0.00	219.05
		4.45	219.16
		4.47	219.12
		4.47	219.13
		5.20	219.07
		9.06	217.52
		9.73	217.86
STÁVAJÍCÍ TERÉN		-9.32	218.22
ODSAZENÍ OD OSY		-6.89	218.14
		-6.10	217.86
		-5.73	217.77
		-5.26	217.74
		-5.06	217.74
		-4.42	218.03
		-2.64	218.63
		-2.38	218.65
		-1.74	218.69
		0.00	218.72
		1.98	218.76
		3.25	218.78
		7.24	218.67
		8.38	218.64
		8.60	218.62
		9.55	218.52
		12.39	217.70
		13.10	217.48
		13.72	217.44
		13.96	217.42
		14.62	217.64
		14.85	217.71

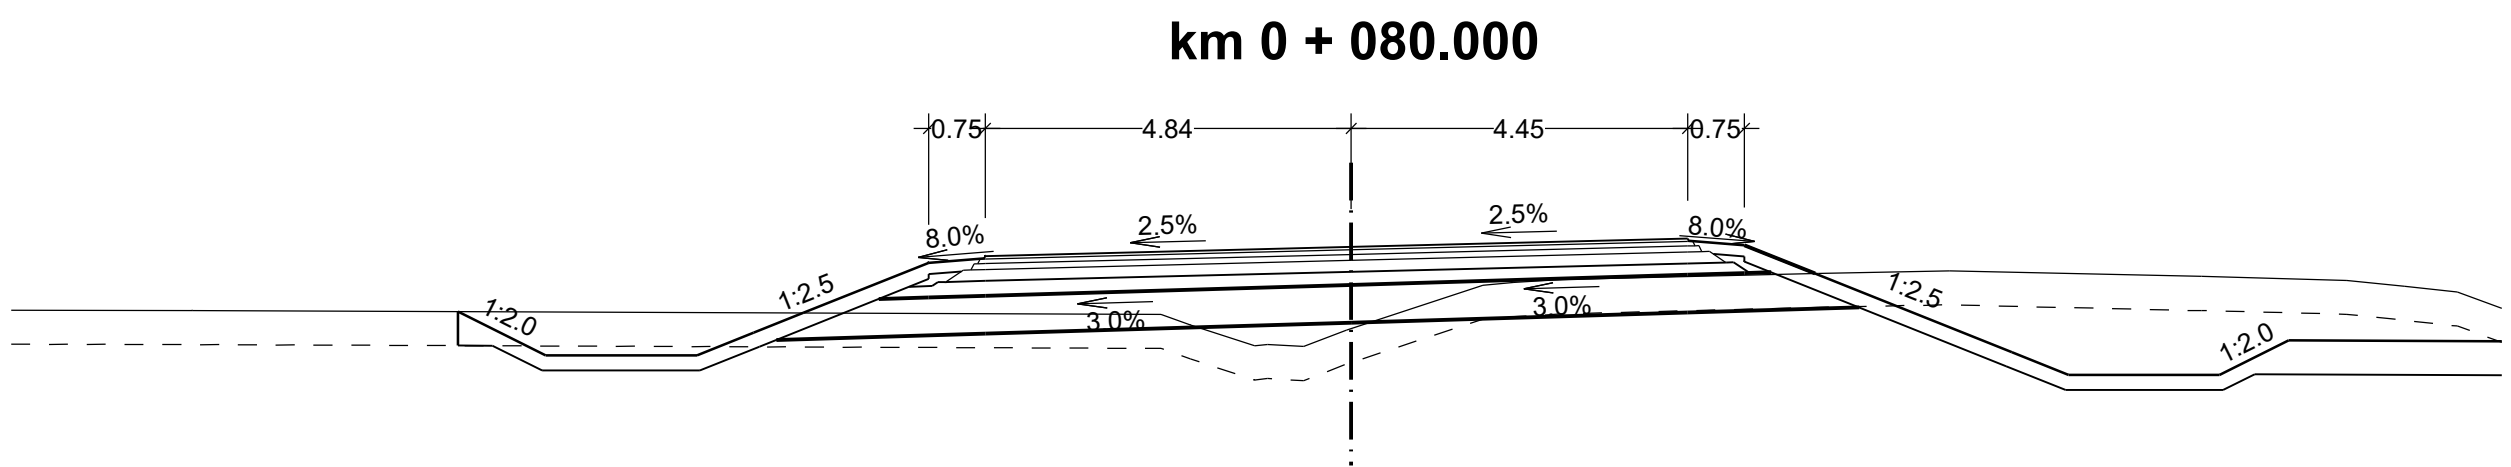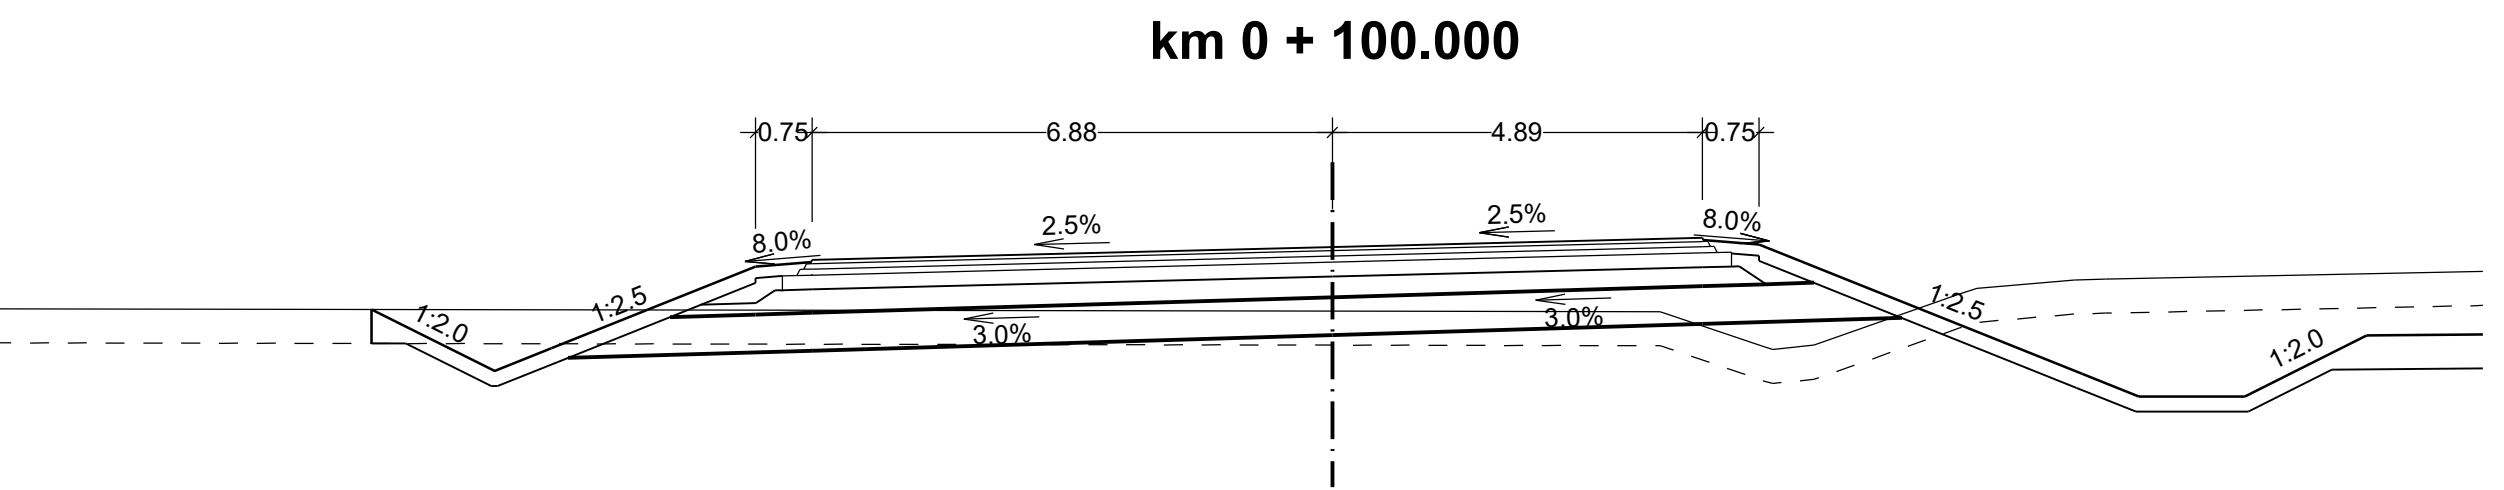[illegible][illegible]

/ýškový systém: Bpv

SO 125 Napojení původní I/16 do MUK Židněves

Objednatel:



**ŘEDITELSTVÍ
SILNIC
A DÁLNIC**

Ředitelství silnic a dálnic s. p.
Čerčanská 2023/12, Krč, 140 00 Praha 4

Zhotoviteľ: 	Valbek, spol. s r.o. Vaňurova 505/17 460 07 Liberec 3	HIP: ING. T. KLIMENT
--	--	-----------------------------

	Vypracoval	ING. A. DUMANSKA	Zak. číslo	21-LJ13-001
	Zodp. projektant	ING. T. KLIMENT	Datum	02/2025
	Tech. kontrola	ING. M. HANŽL	Stupeň	PDPS
	Akce		Počet formátů	6 x A4
I/16 MLADÁ BOLESLAV - MARTINOVICE			Měřítko	1 : 100
			Č. přílohy	Paré
Zhotovitel: Valbek, spol. s r.o. Vafuřova 505/17 460 07 Liberec 3	Příloha PŘÍČNÉ ŘEZY, SO125.1	5.2		