
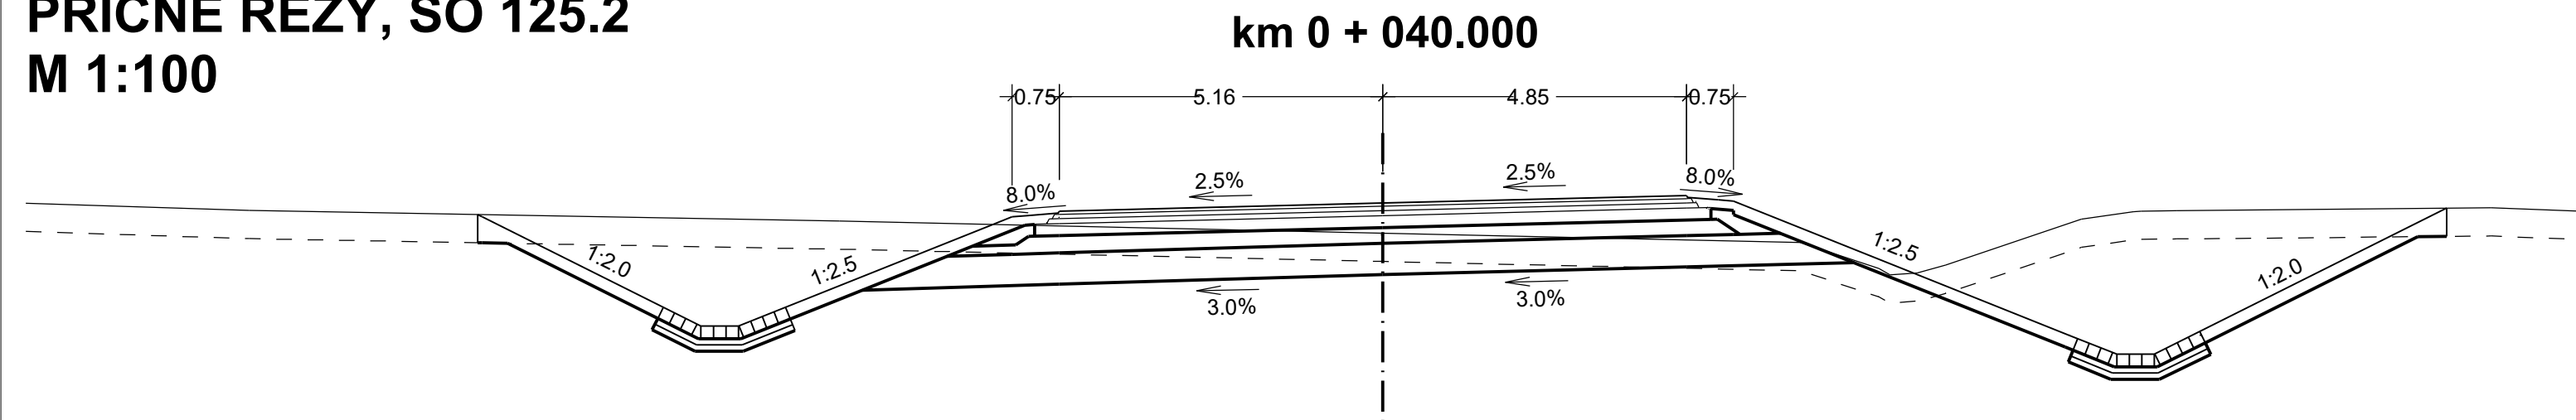
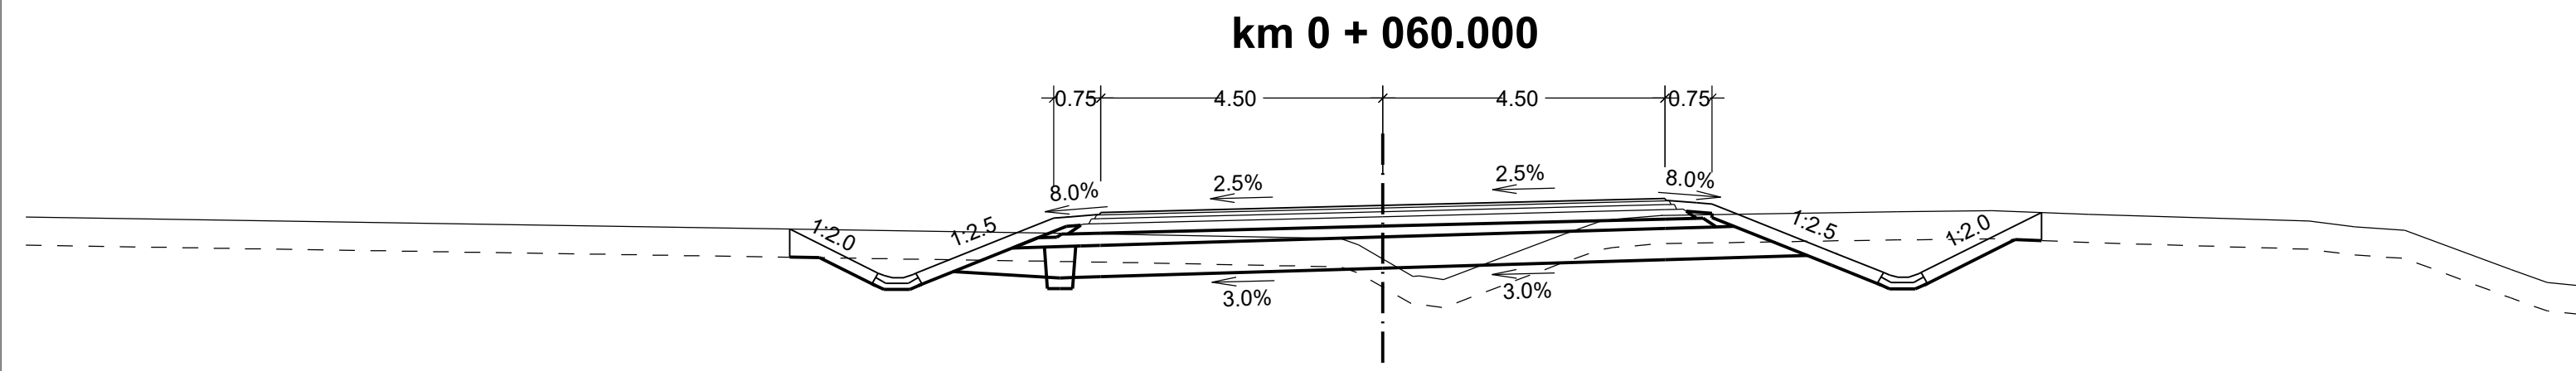
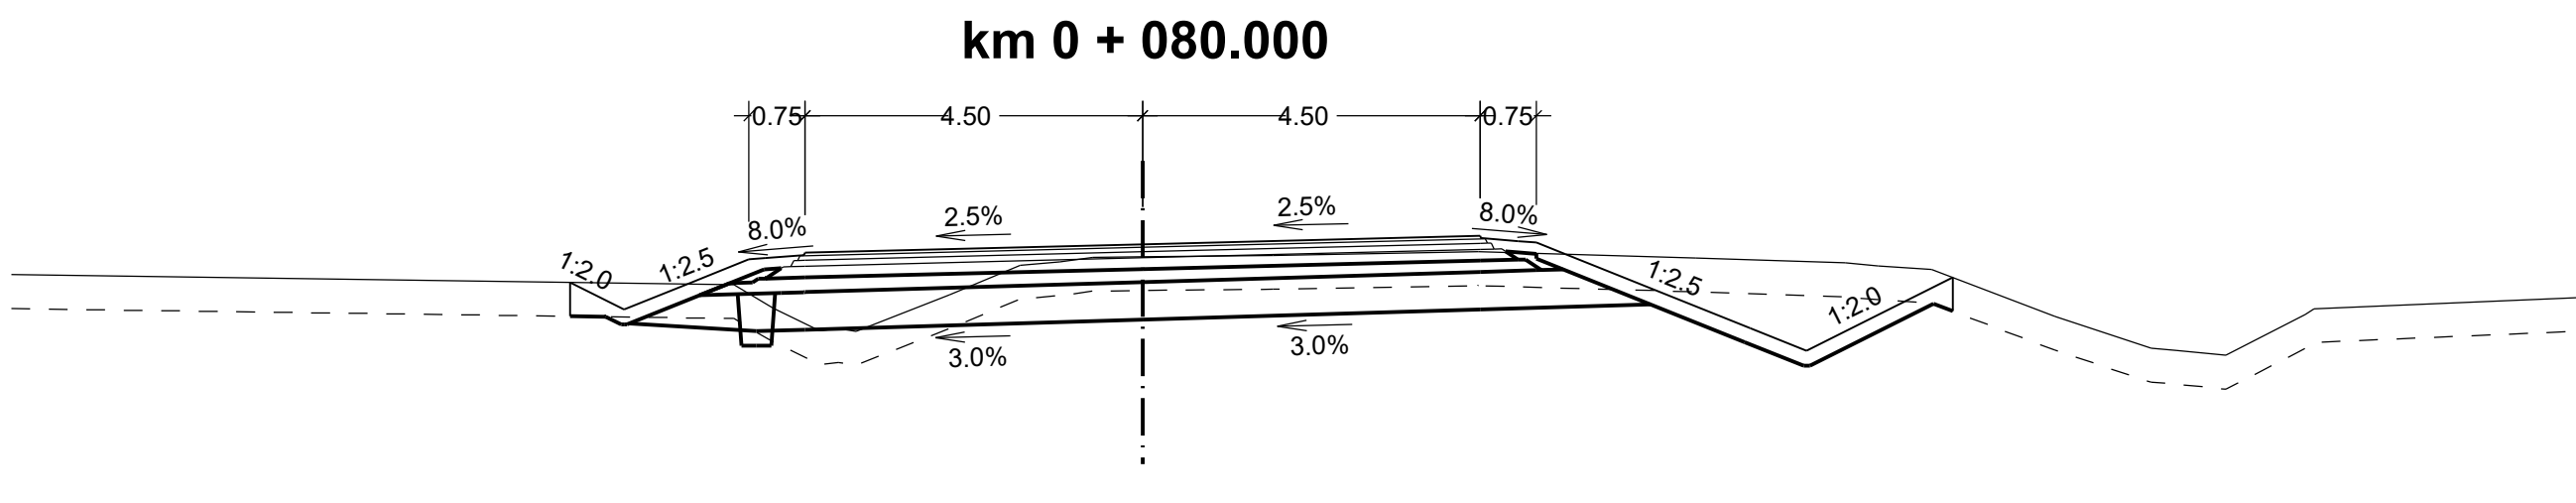
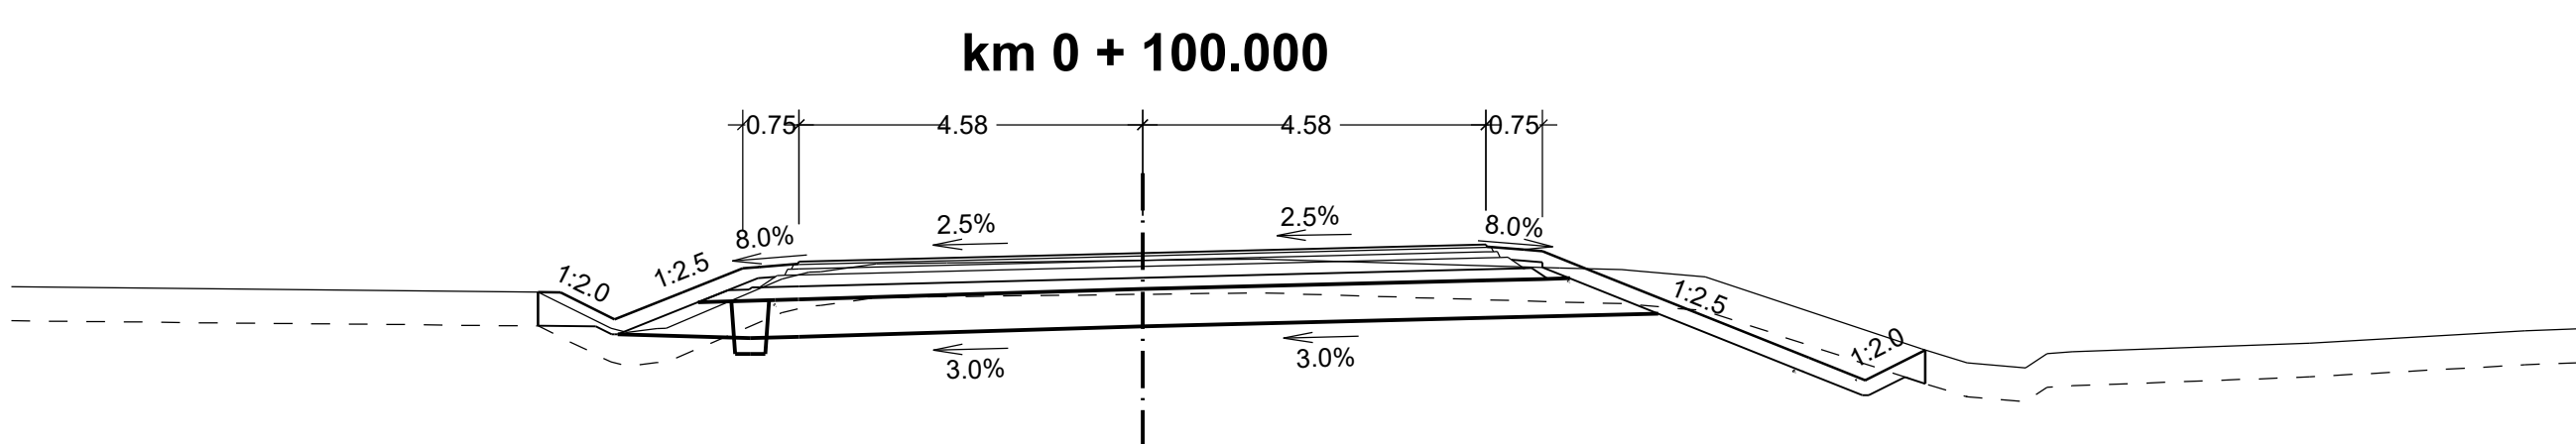



SO 125 - NAPOJENÍ PŮVODNÍ I/16 DO MÚK ŽIDNĚVES
PŘÍČNÉ ŘEZY, SO 125.2
M 1:100 km 0 + 0

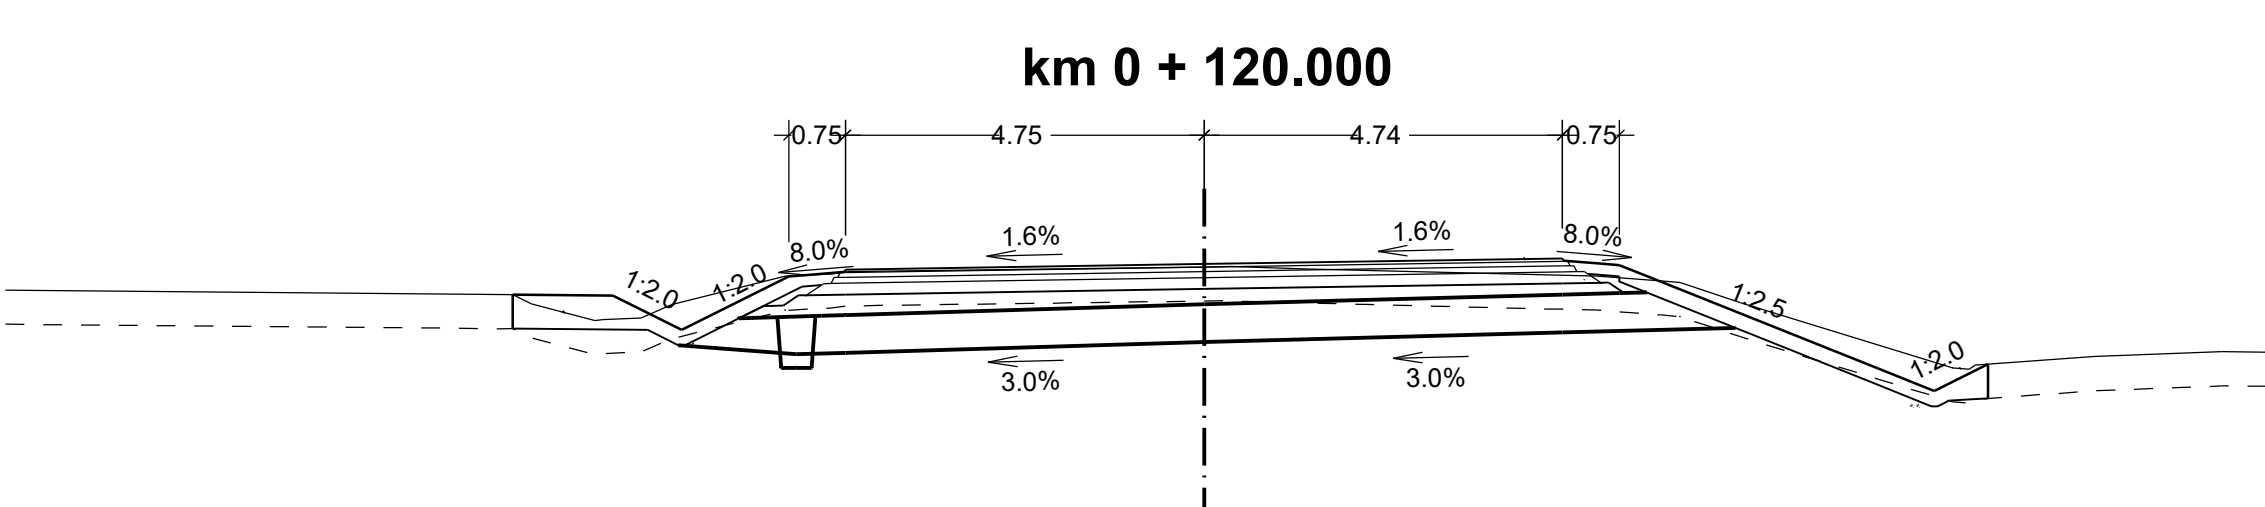

		S. R. 216 m	
PROJEKTOVANÝ STAV		-14.44 220.60 -14.44 220.15 -14.37 220.56	
ODSAZENÍ OD OSY		-10.88 218.82 -10.58 218.82 -10.28 218.82	
		-6.22 220.44 -5.91 220.56 -5.69 220.58 -5.18 220.62 -5.18 220.61 -5.16 220.65	
		-8.67 220.50	
STÁVAJÍCÍ TERÉN		0.00 220.30	
ODSAZENÍ OD OSY		4.85 220.90 4.86 220.87 4.87 220.86 5.35 220.83 5.60 220.81	
		6.66 220.15	
		7.91 219.74 8.09 219.64 8.52 219.67 8.98 219.79	
		8.47 219.66	
		10.96 218.67	
		11.71 218.37	
		12.31 218.37	
		11.14 220.53 11.97 220.64 12.10 220.65 12.67 220.66	
		17.68 220.71	
		16.97 220.70 16.97 220.25	

[illegible][illegible][illegible]

		S ₁ R 218 m			
PROJEKTOVANÝ STAV		-9.15	221.68		
ODSAZENÍ OD OSY		-9.15	222.13		
		-7.82	222.12		
		-6.91	221.66		
		-5.50	222.37		
		-5.27	222.39		
		-4.77	222.42		
		-4.76	222.43		
		-4.75	222.46		
				4.74	222.61
				4.75	222.58
				4.76	222.57
				5.25	222.54
				5.49	222.52
				6.00	222.31
				8.90	221.15
				9.65	220.85
				10.36	221.21
				10.36	220.76
				11.78	221.31
				13.46	221.37
STÁVAJÍCÍ TERÉN		-9.15	222.13		
ODSAZENÍ OD OSY		-8.90	222.01		
		-8.06	221.79		
		-7.96	221.80		
		-7.45	221.82		
		-7.04	221.99		
		-5.54	222.37		
		-4.91	222.40		
		-4.71	222.43		
				-0.77	222.48
				0.00	222.49
				0.34	222.50
				1.39	222.47
				5.19	222.37
				6.04	222.31
				6.29	222.29
				7.09	222.02
				9.90	221.16
				10.11	221.14
				10.19	221.19
				11.78	221.31
				13.46	221.37

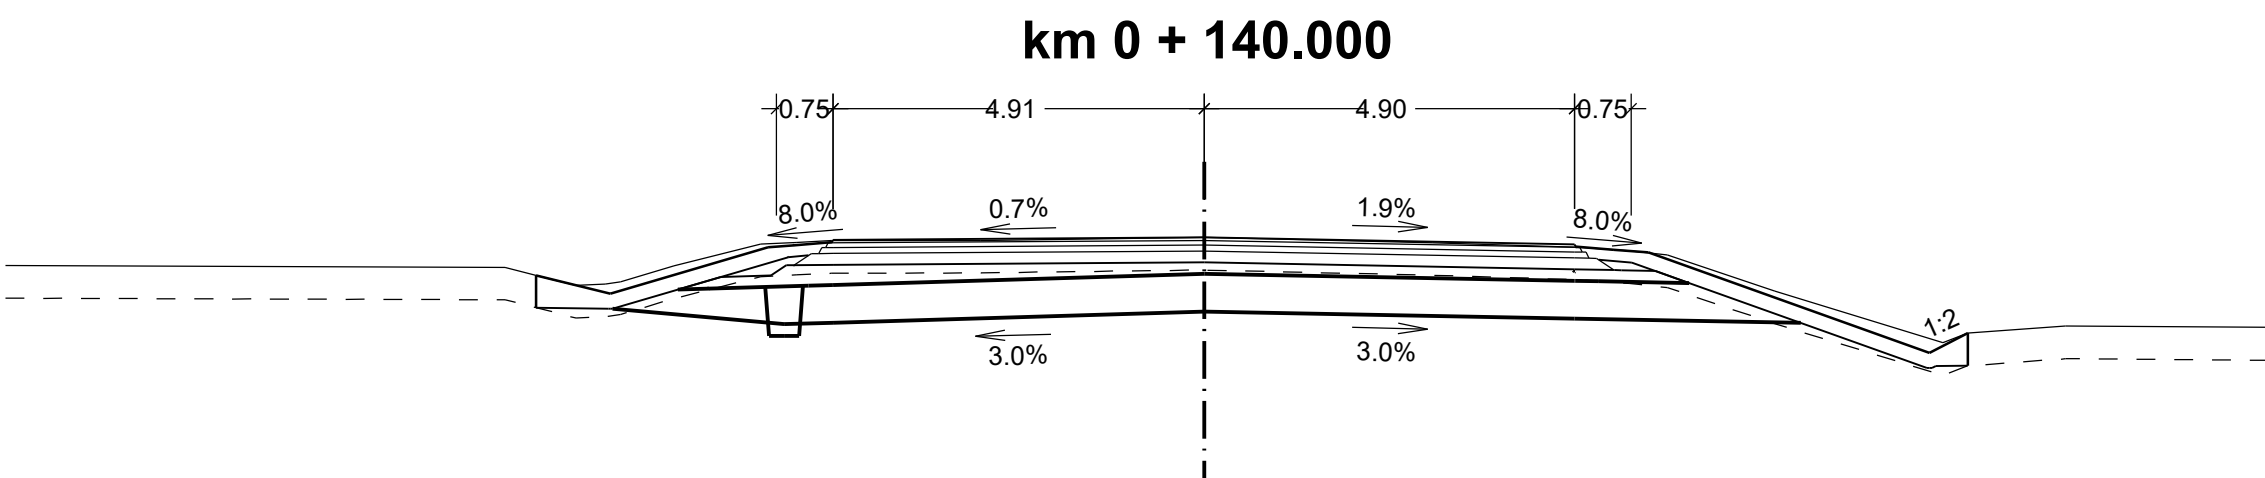[illegible]

Výškový systém: Bpv

SO 125 Napojení původní I/16 do MUK Židněves

Objednatel:

 **ŘEDITELSTVÍ
SILNIC
A DÁLNIC**

Ředitelství silnic a dálnic s. p.
Čerčanská 2023/12, Krč, 140 00 Praha 4

Zhotovitel:  Valbek	Valbek, spol. s r.o. Vaňurova 505/17 460 07 Liberec 3	HIP: ING. T. KLIMENT
---	---	---

	Vypracoval	ING. A. DUMANSKA	Zak. číslo	21-L113-001
	Zodp. projektant	ING. T. KLIMENT	Datum	02/2025
	Tech. kontrola	ING. M. HANŽL	Stupeň	PDPŠ
	Akce	I/16 MLADÁ BOLES LAV - MARTINOVICE		Počet formátů
	Měřítko			1 : 100
			Č. přílohy	Paré
Zhotovitel: Valbek, spol. s r.o. Valburská 505/17 460 07 Liberec 3	Přiloha PŘÍČNÉ ŘEZY, SO125.2	5.3		