



SO 125 - NAPOJENÍ PŮVODNÍ I/16 DO MÚK ŽIDNĚVES
PROPUSTEK DN 800 V km 0,039, Sjezd 1, M 1 : 100


PŮDORYS

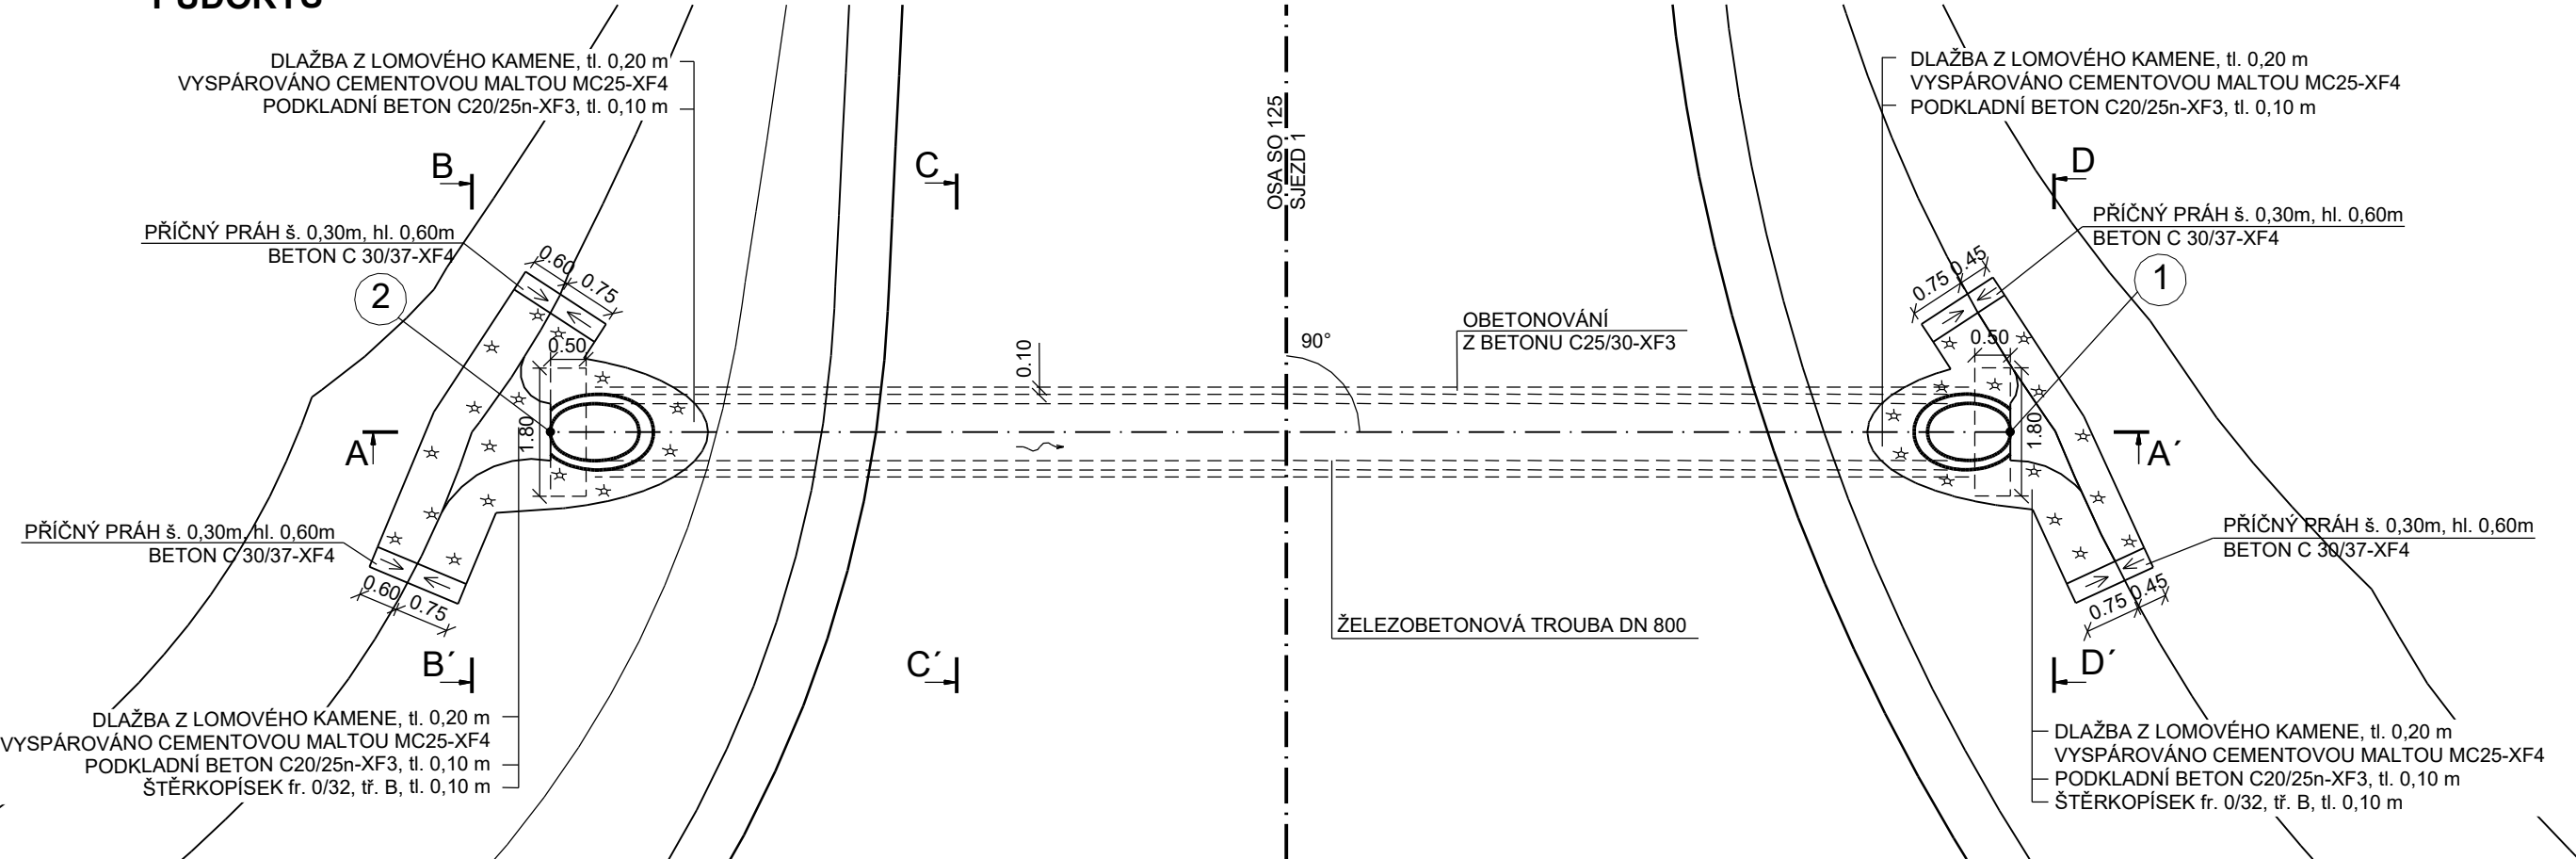


PODÉLNÝ ŘEZ A-A'

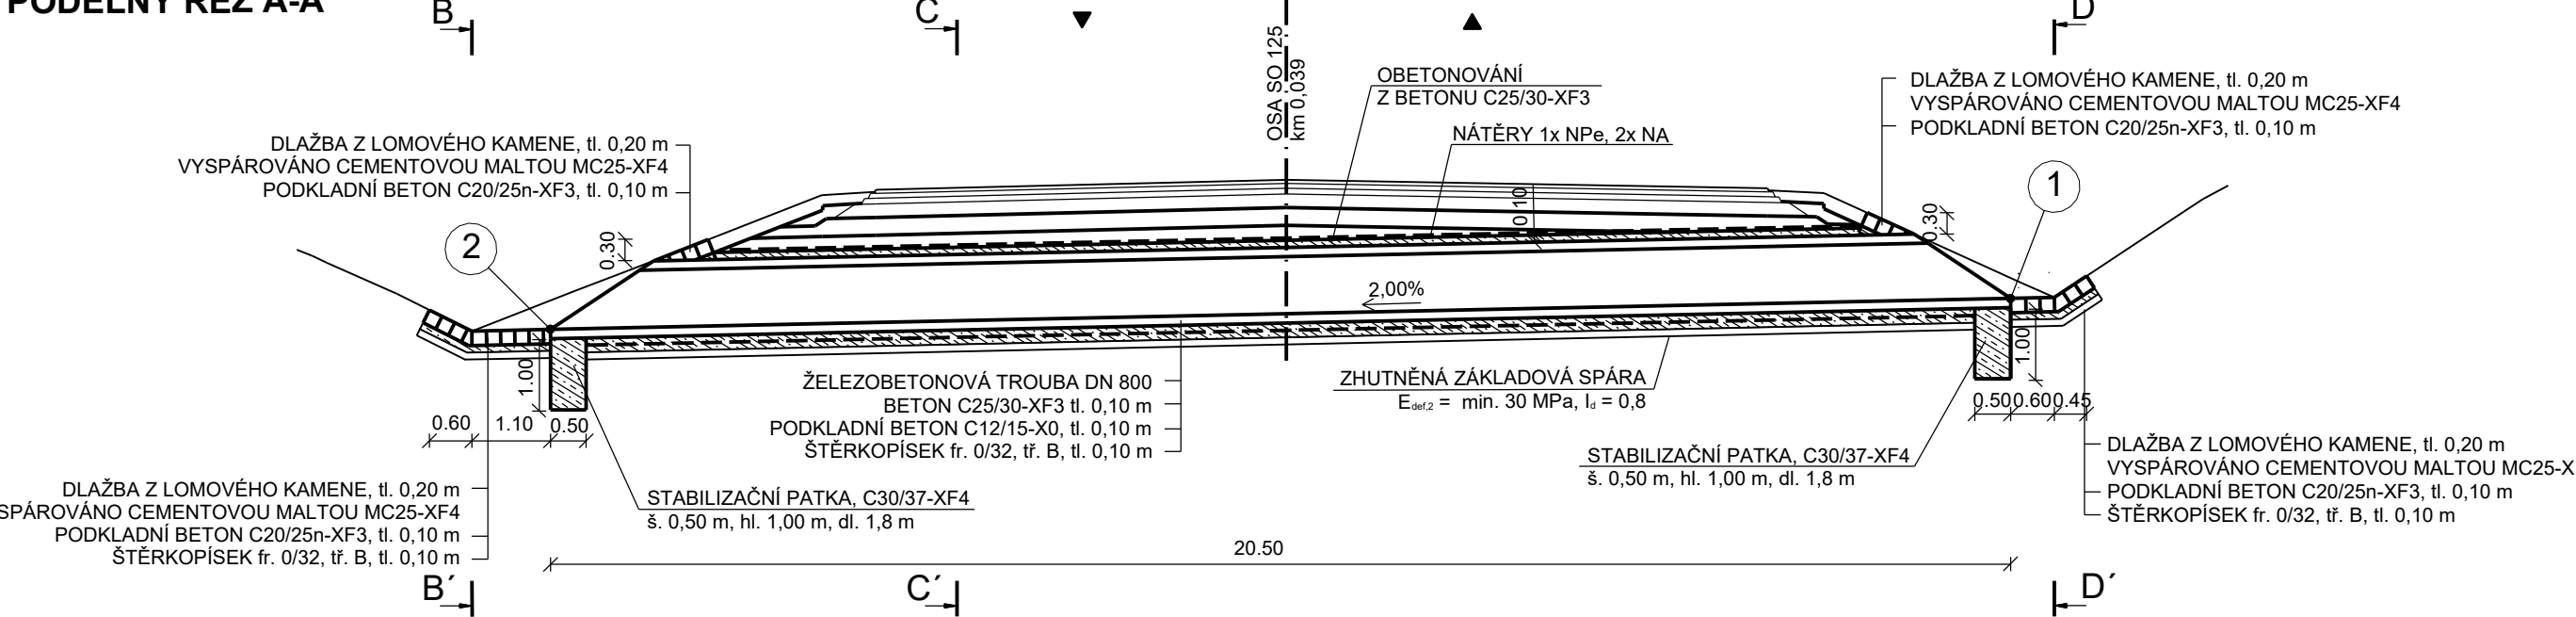


POHLED NA VTOK ŘEZ D-D'

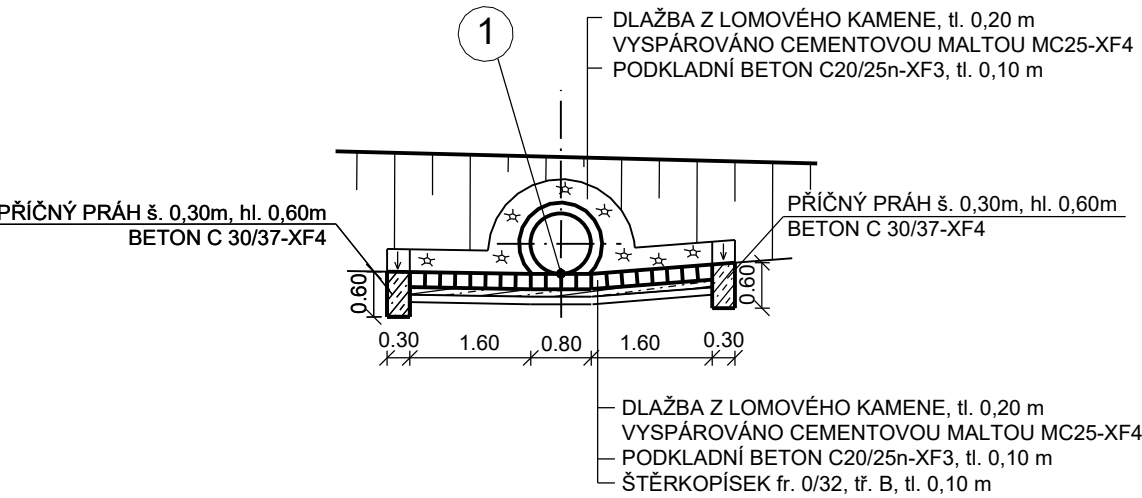

POHLED NA VÝTOK ŘEZ B-B'

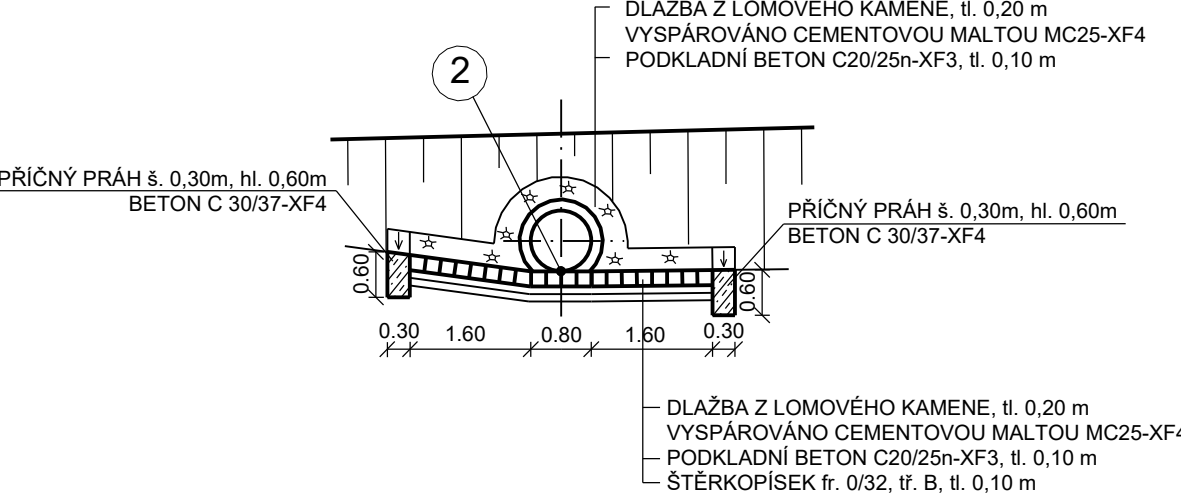

PŘÍČNÝ ŘEZ C-C'

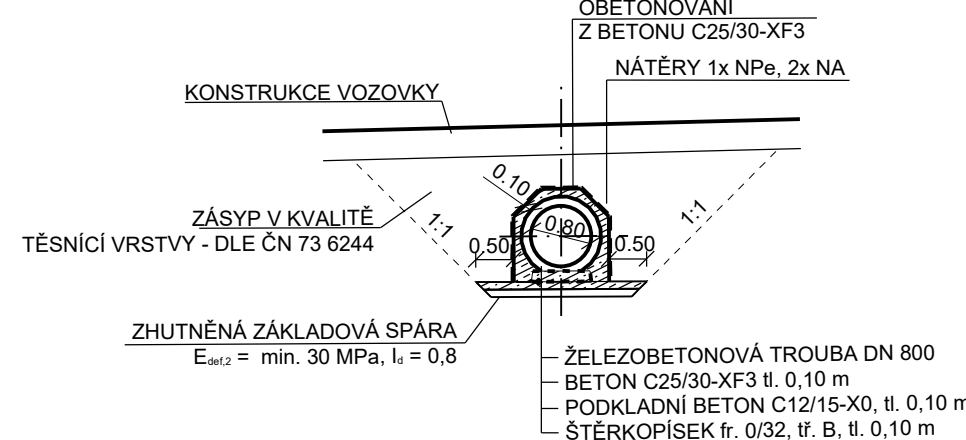

POZNÁMKY:

- SPÁROVÁNÍ DLAŽBY Z LOMOVÉHO KAMENE BUDE VYPLNĚNÉ CEMENTOVOU MALTOU MC25-XF4, tl. min. 0,20 m
- OBETONOVÁNÍ V MÍSTĚ HRDLA MINIMÁLNĚ 0,10 m
- VŠECHNY BETONOVÉ PRVKY, KTERÉ PŘIJÍDOU DO STYKU SE ZEMINOU MUSÍ BÝT OPATŘENY NÁTĚRY: 1x NPe A 2x NA
- POČET PRAHŮ ZÁVISÍ NA TYPU ZVOLENÉ TROUBY A JEJÍHO ULOŽENÍ
- VYTÝČENÍ BUDE PROVEDENO DLE TKP 1 A SOUVISEJÍCÍCH PŘEDPISŮ
- SKLONY SVAHŮ JSOU URČENY SKLONEM SILNIČNÍHO TĚLESA A PŘÍLEHLÝCH PŘÍKOPŮ
- POKUD NEBUDOU NA KRAJÍCH OSAZENY ŠIKMÉ PREFABRIKÁTY, BUDOU PRO SERÍZNUTÍ POUŽITY BETONOVÉ TROUBY (Z DŮVODU KORODUJÍCÍ VÝTUŽE)
- ŠÍŘE PODKLADNÍHO PRAHU JE 0,50 m NA KAŽDOU STRANU OD VNĚJŠÍHO OBRYSU TROUBY
- BETONOVÉ VÝROBKY VYSTAVENÉ PŘÍMÉMU OSTRÍKU ROZMRAZOVACÍCH PROSTŘEDKŮ A MRAZU A UMÍSTĚNÉ VE ZVZDÁLENOSTI MOŽNÉHO OSTRÍKU (OD HRANY VOZOVKY 10 m VČETNĚ SOLNÉ MLHY) MUSÍ SPLŇOVAT POŽADAVKY NA STUPEŇ VLIVU PROSTŘEDÍ XF4.

PARAMETRY PROPUSTKŮ					VYTÝČOVANÉ BODY	
STANIČENÍ [km]	TROUBA DN [mm]	DÉLKA DL [m]	SKLON S, [%]	ÚHEL α [°]	VTOK - 01 Y / X [S-JTSK] / Z [Bpv]	VÝTOK - 02 Y / X [S-JTSK] / Z [Bpv]
0,039	800	20,50	2,00	90	696608,686/1012052,829/218,74	696613,426/1012072,783/218,30

Souřadnicový systém: S-JTSK
Výškový systém: Bpv

SO 125 Napojení na původní I/16 do MÚK Židněves

Objednatel:



**ŘEDITELSTVÍ
SILNIC
A DÁLNIC**

Ředitelství silnic a dálnic s. p.
Čerčanská 2023/12, Krč, 140 00 Praha 4

Zhotovitel:



Valbek

Valbek, spol. s r.o.
Vaňurova 505/17
460 07 Liberec 3

	Vypracoval	A. BARTONIČKOVÁ	Zak. číslo	21-L113-001
	Zodp. projektant	ING. T. KLIMENT	Datum	02/2025
	Tech. kontrola	ING. M. HANŽL	Stupeň	PDPS
	Akce		Počet formátů	5 x A4
Zhotovitel: Valbek, spol. s r.o. Vaňurova 505/17 460 07 Liberec 3	I/16 MLADÁ BOLESLAV - MARTINOVICE		Měřítko	1 : 100
			Č. přílohy	Paré
			6.2	
	Příloha	PROPUSTEK DN 800 V km 0,039, Sjezd 1		