


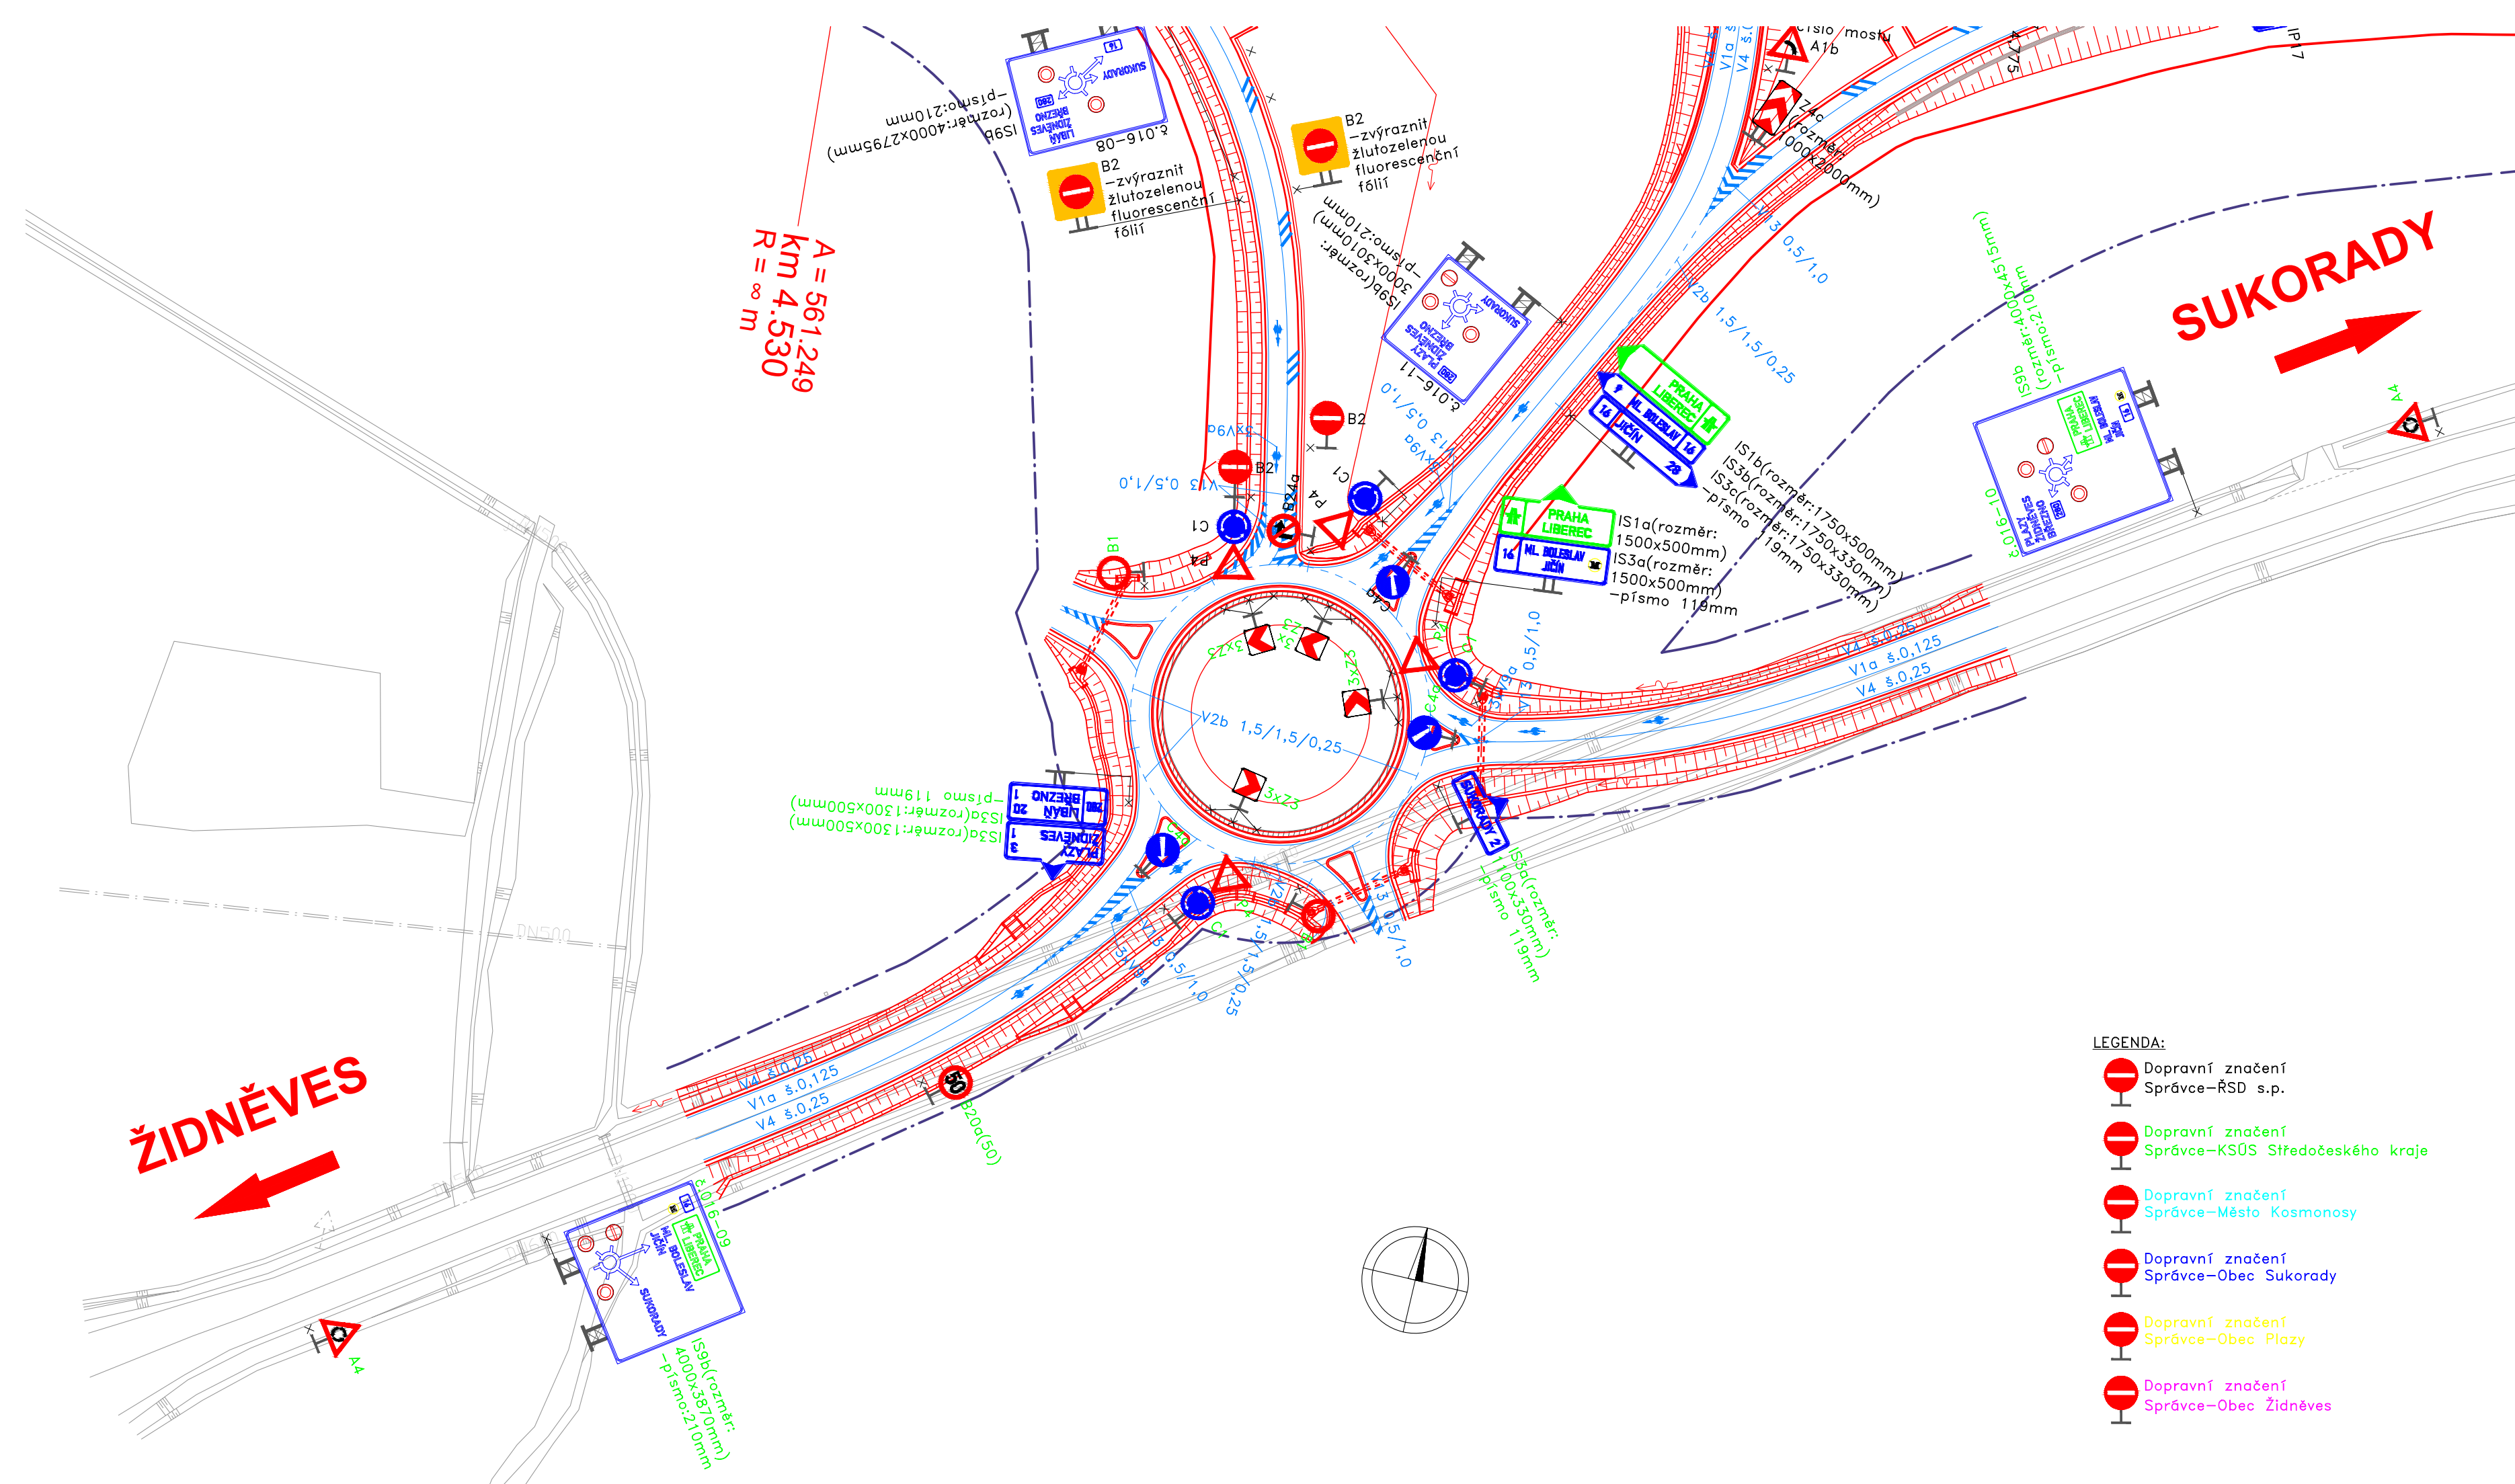

Souřadnicový systém: S-JTSK
Výškový systém: Bpv

SO 125 Napojení původní I/16 do MUK Židněves

Objednatel:



ŘEDITELSTVÍ
SILNIC
A DÁLNIC

Ředitelství silnic a dálnic s. p.
Čerčanská 2023/12, Krč, 140 00 Praha 4

Zhotovitel:



Valbek, spol. s r.o.
Vaňurova 505/17
460 07 Liberec 3

	Vypracoval	STANISLAV KRUPÍČKA		Zak. číslo	024-24
	Zodp. projektant	ING. PETER HAJOŠ		Datum	02/2025
	Tech. kontrola	ANTONÍN SEIDL		Stupeň	PDPS
	Akce I/16 MLADÁ BOLESLAV - MARTINOVICE			Počet formátů	3 x A4
Měřítko				1 : 1000	
Č. přílohy				Paré	
Zhotovitel: DISK s.r.o. Menšíkovská 1239/10 160 00 Praha 6	Příloha DOPRAVNÍ ZNAČENÍ			7	