
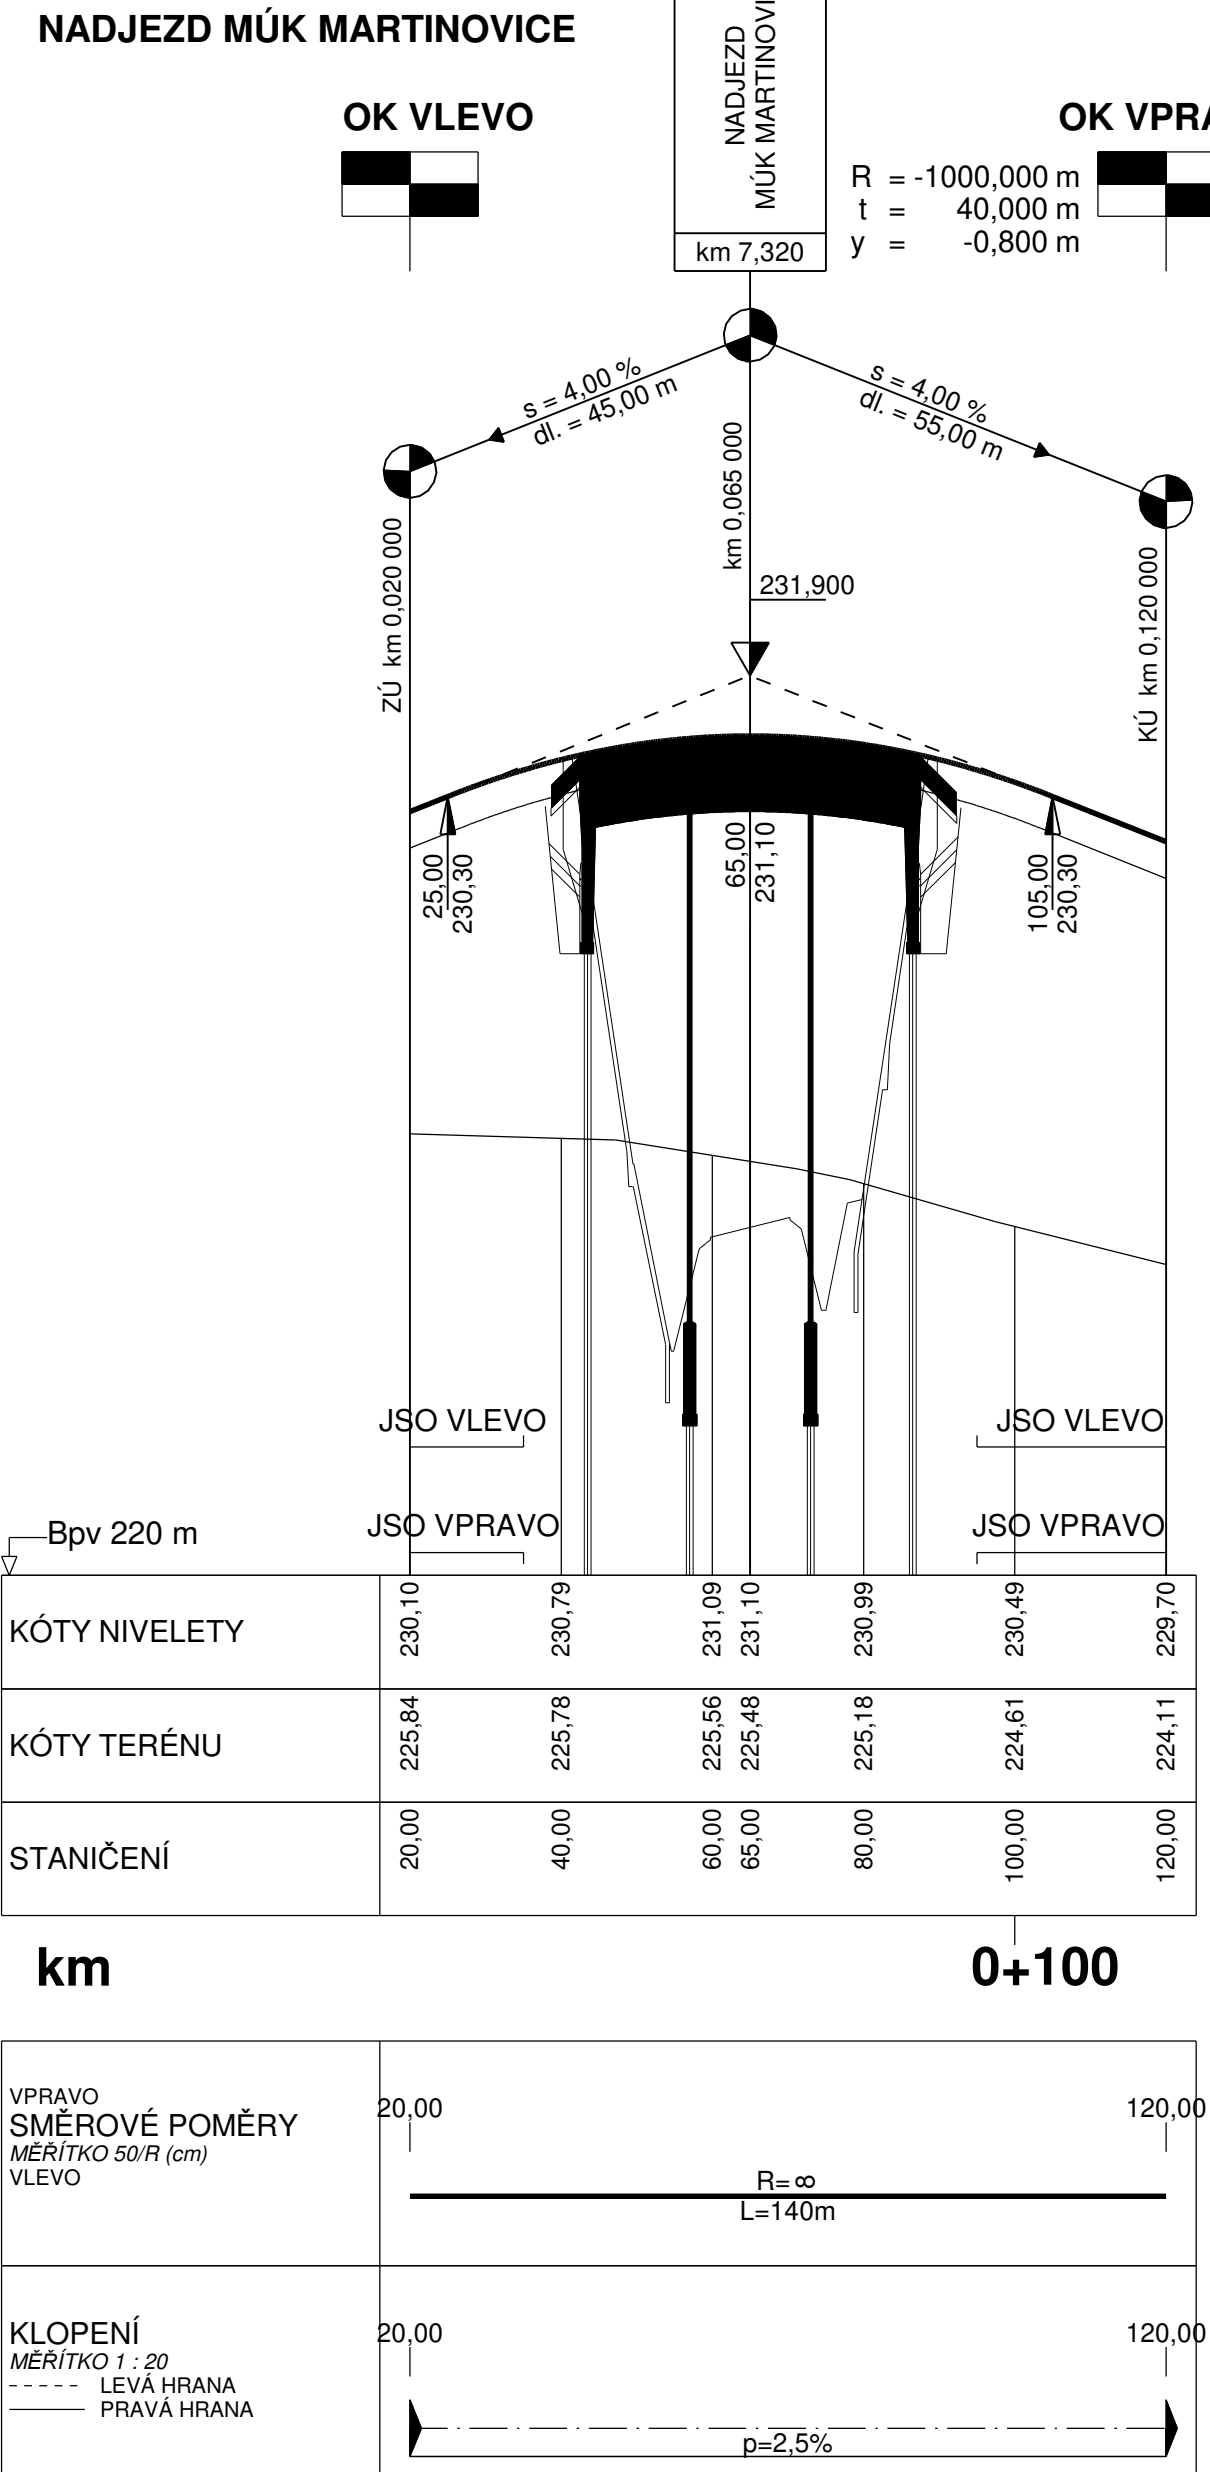
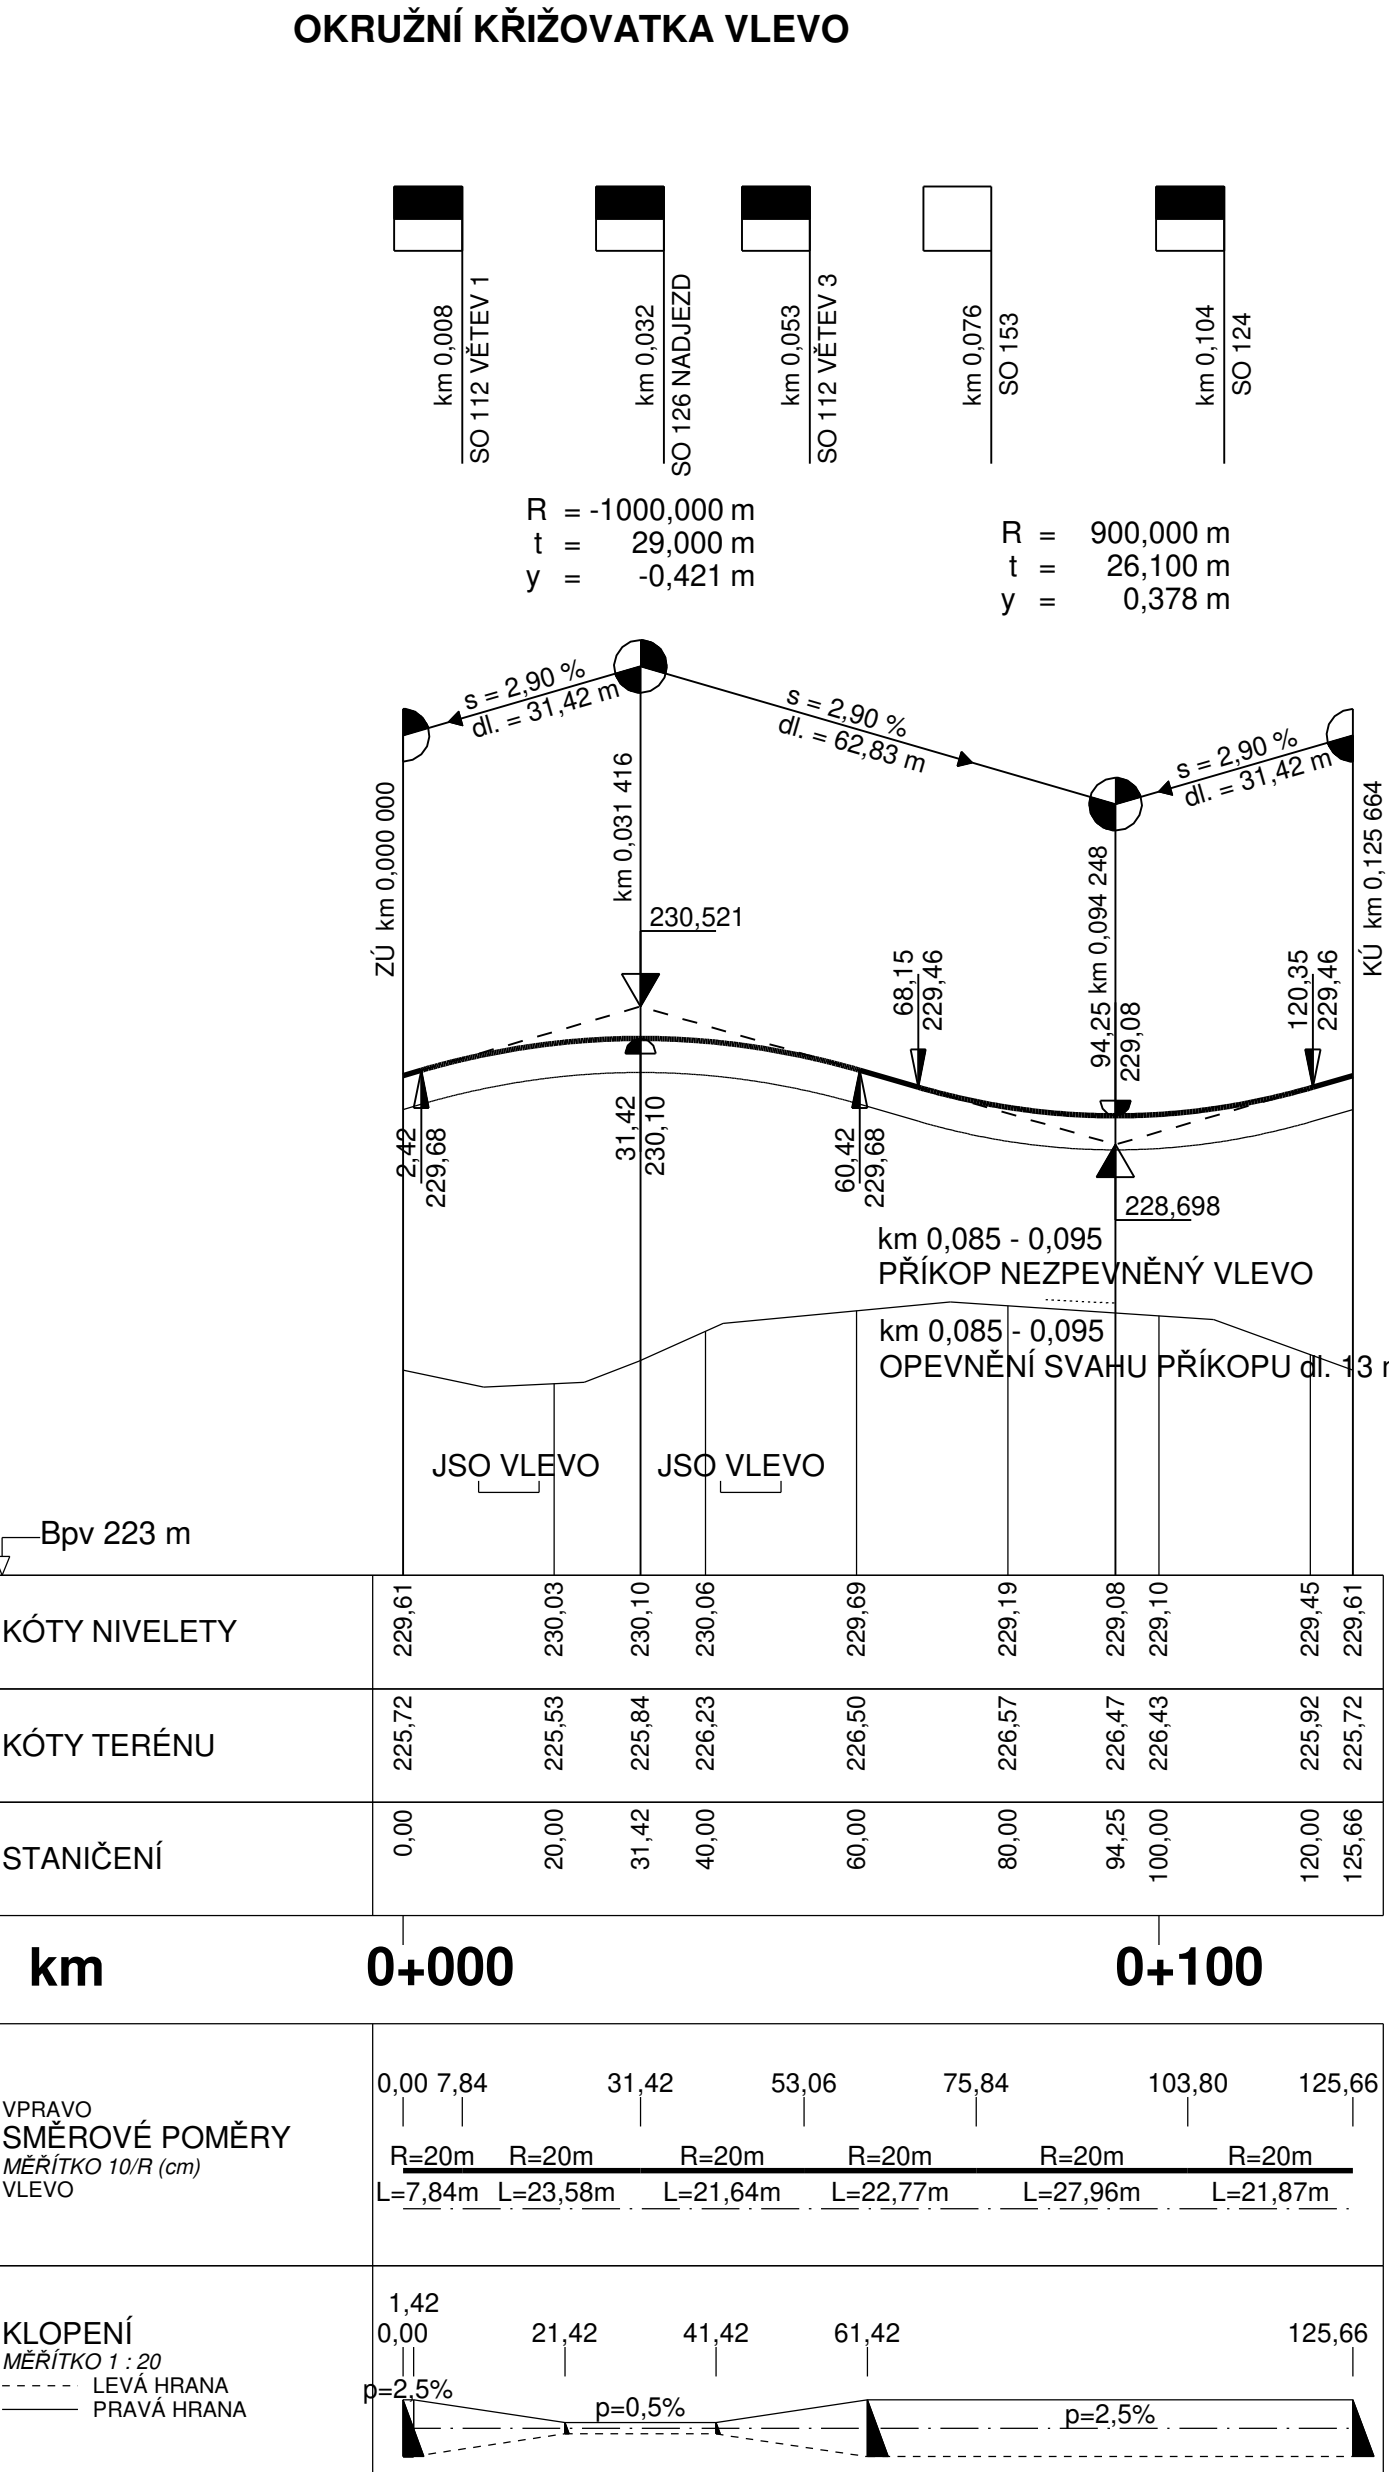
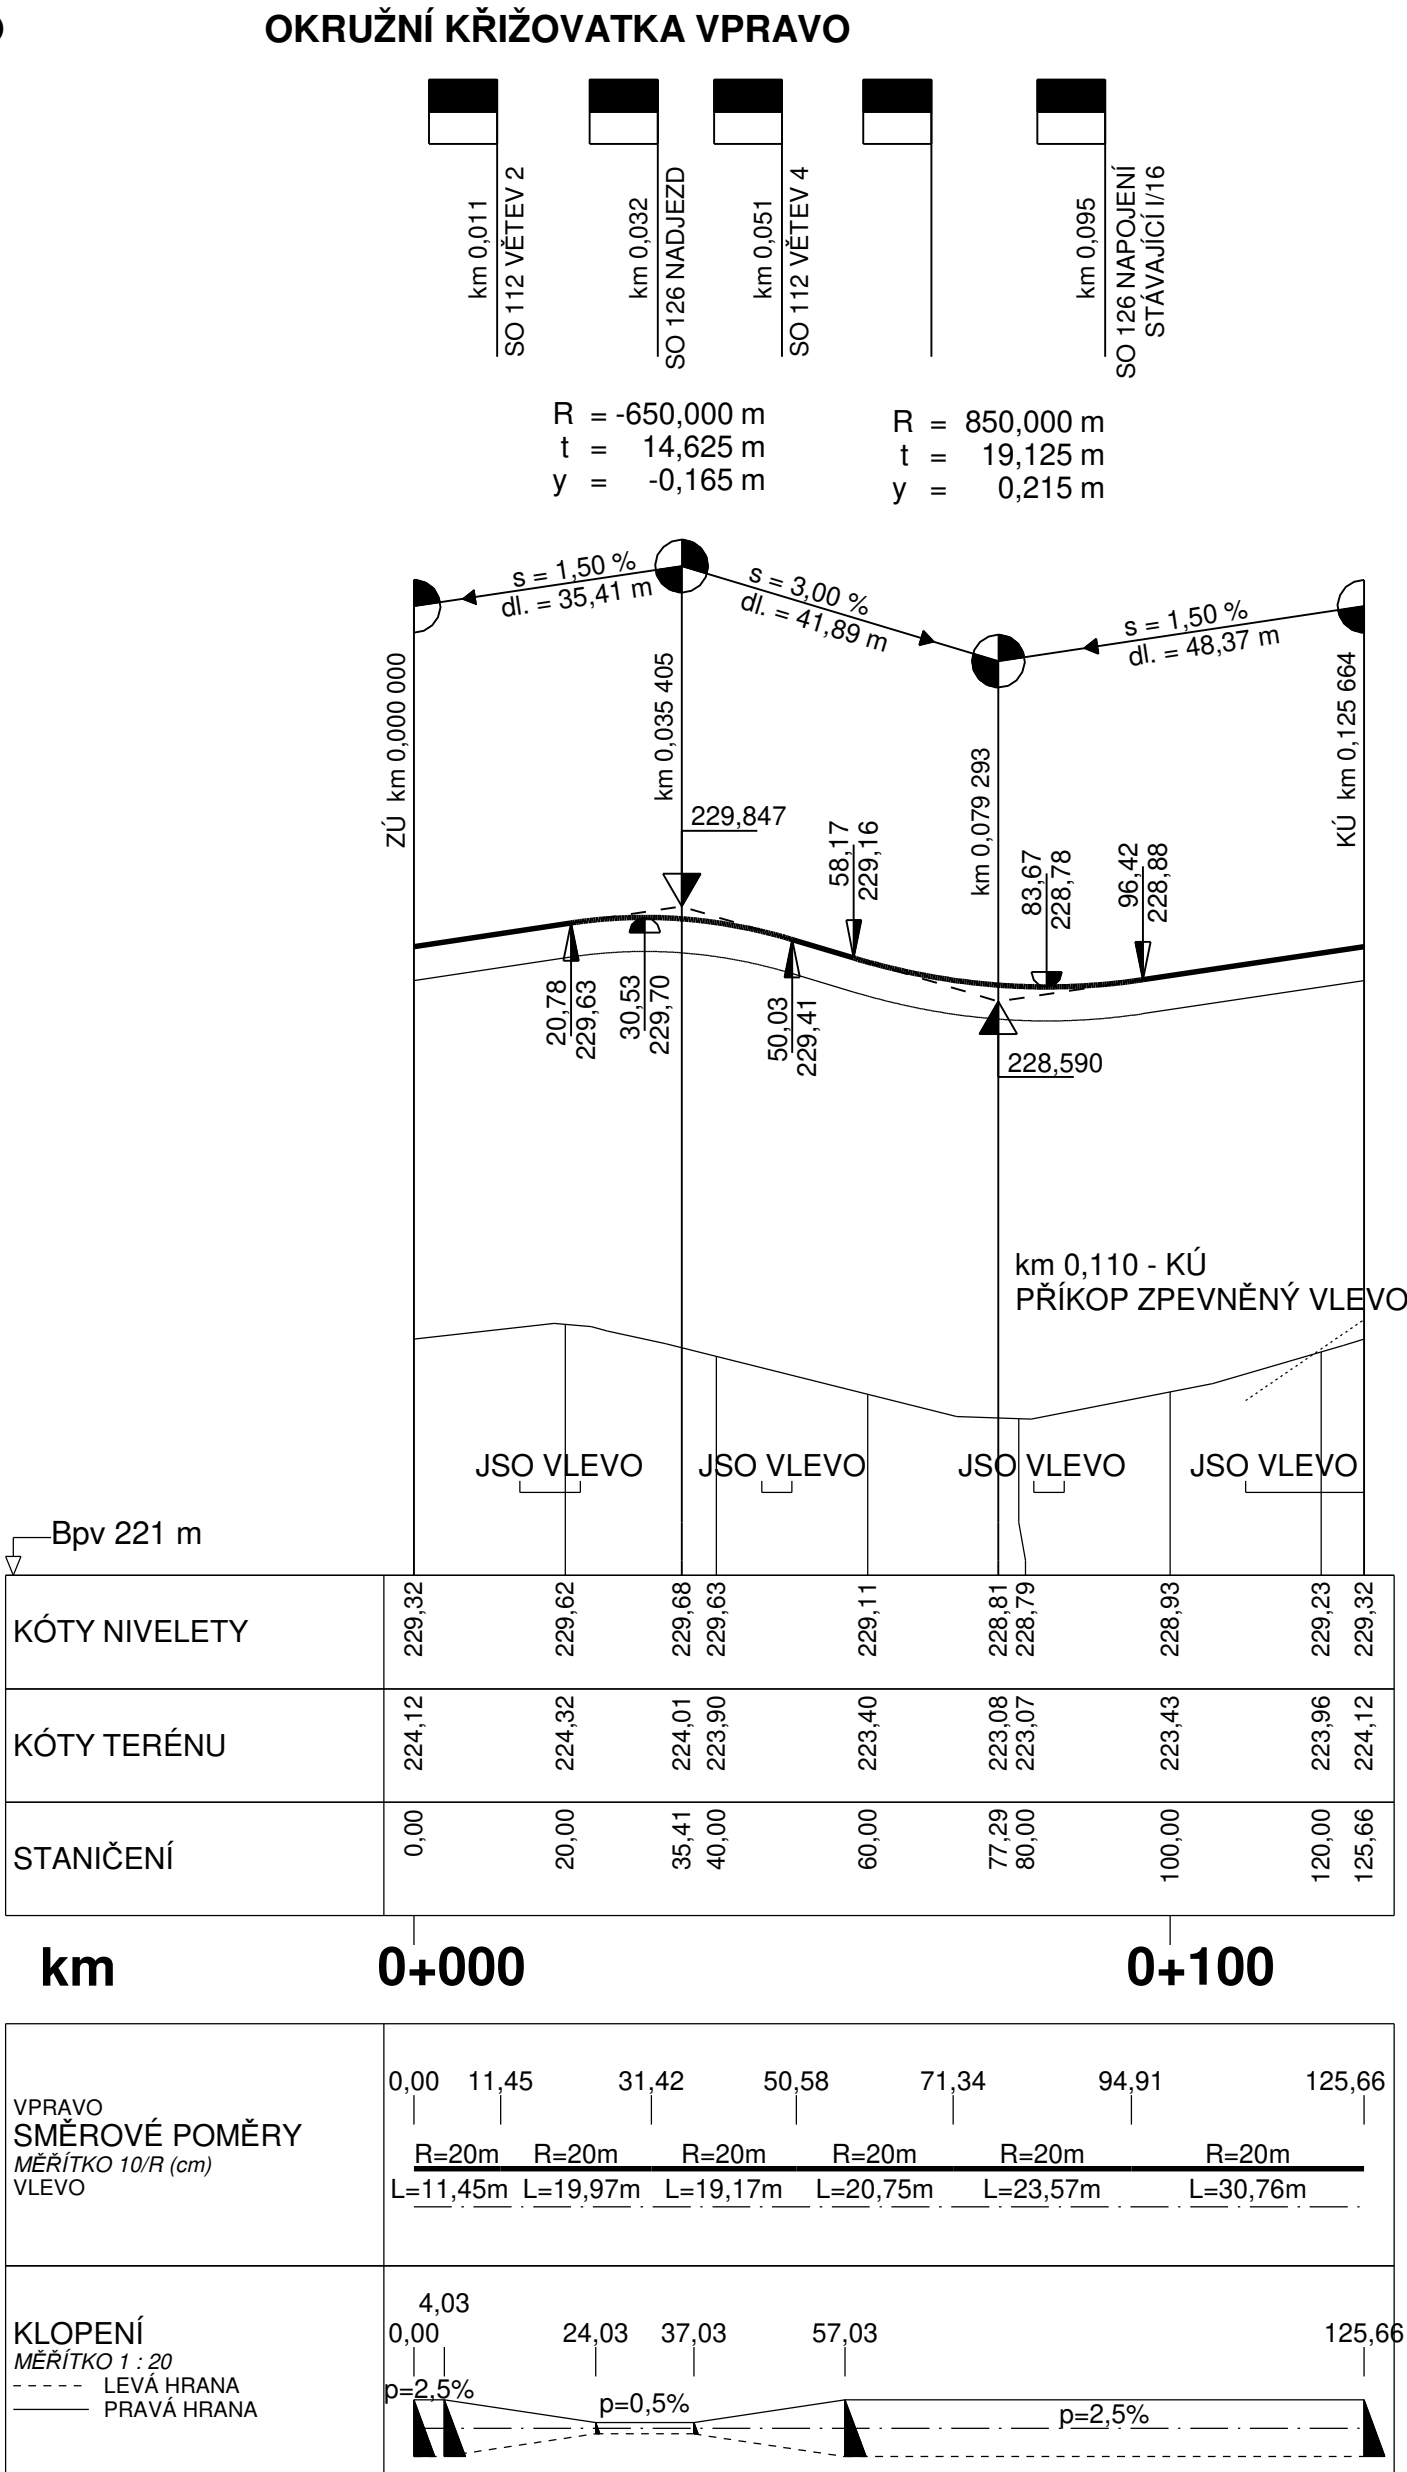


SO 126 - NAPOJENÍ PŮVODNÍ I/16 DO MÚK MARTINOVICE  
PODÉLNÉ PROFILY M 1 : 1 000 / 100

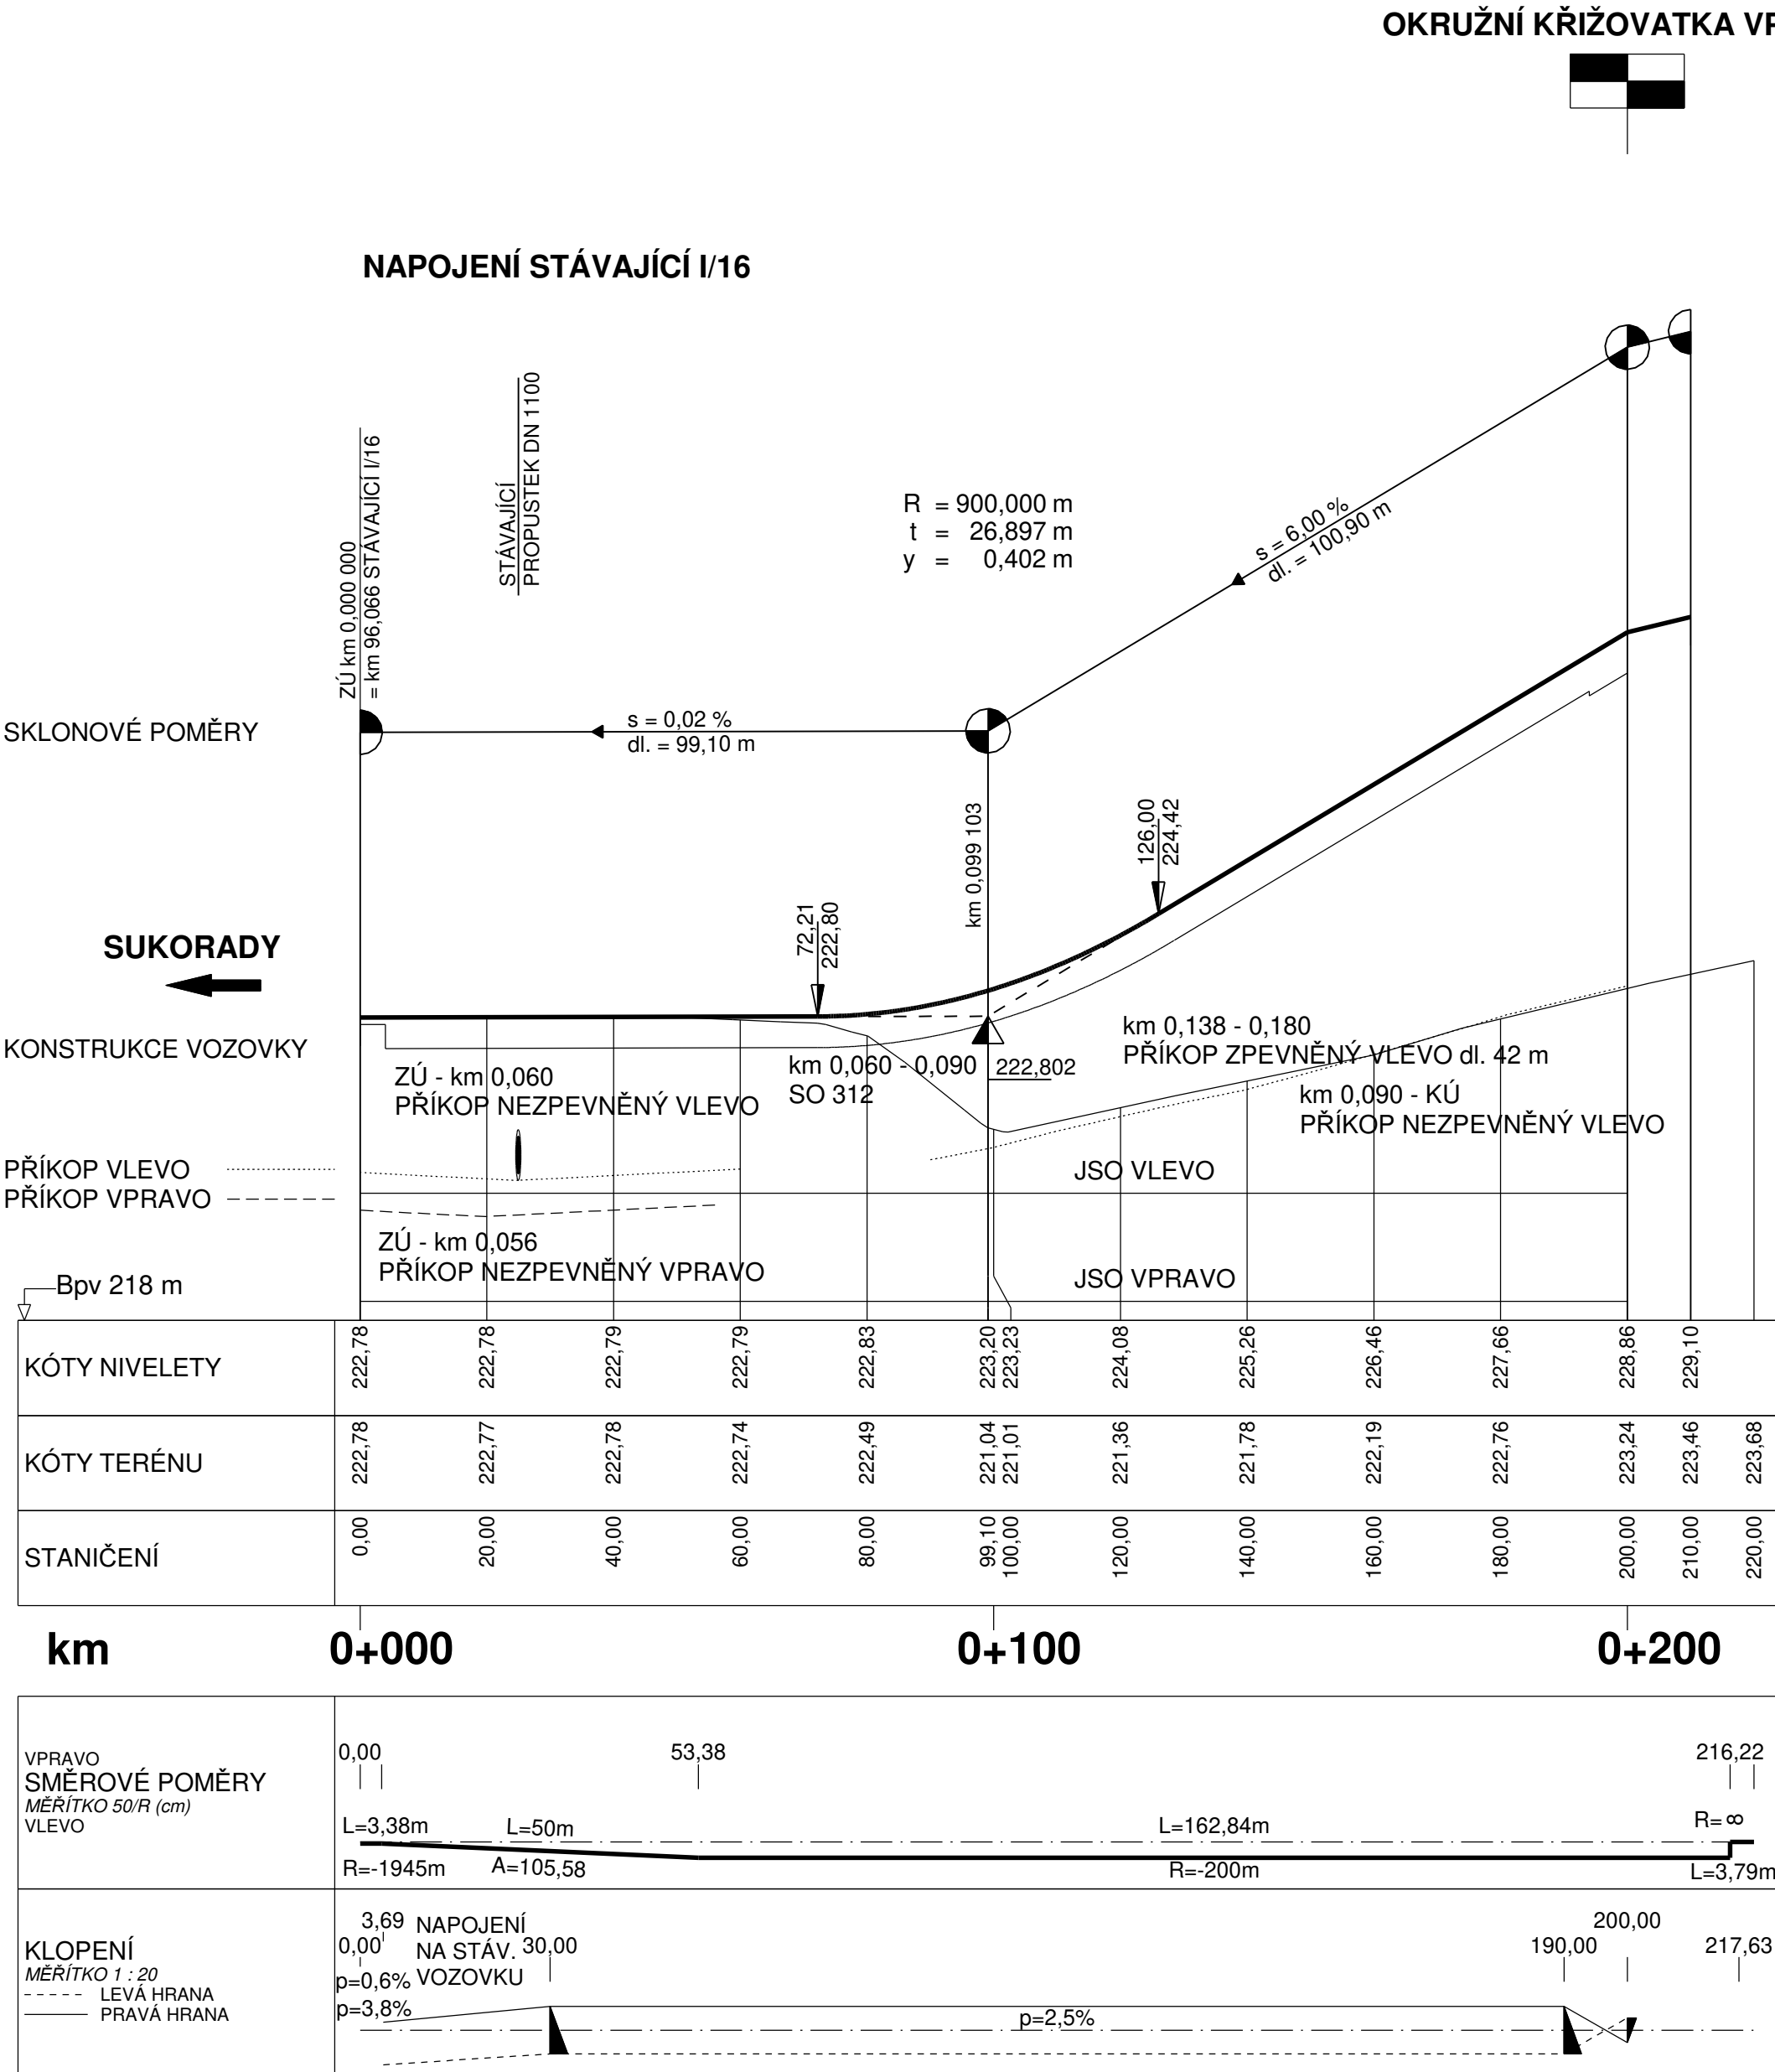

Výškový systém Bpv

SO 126

Napojení původní I/16 do MÚK Martinovice

Objednatel:

**ŘEDITELSTVÍ  
SILNIC  
A DÁLNIC**

Ředitelství silnic a dálnic s. p.  
Čerčanská 2023/12, Krč, 140 00 Praha 4

|   |                                                                    |                         |
|---|--------------------------------------------------------------------|-------------------------|
| Zhotovitel:<br> | <b>Valbek, spol. s r.o.</b><br>Vaňurova 505/17<br>460 07 Liberec 3 | HIP:<br>ING. T. KLIMENT |
|---|--------------------------------------------------------------------|-------------------------|

|                                                                                       |                                  |                        |
|---------------------------------------------------------------------------------------|----------------------------------|------------------------|
|  | Vypracoval M. KOŘÍNEK            | Zak. číslo 21-L113-001 |
|                                                                                       | Zodp. projektant ING. T. KLIMENT | Datum 02/2025          |
|                                                                                       | Tech. kontrola ING. M. HANŽL     | Stupeň PDPS            |
| Akce I/16 MLADÁ BOLESLAV - MARTINOVICE                                                |                                  | Počet formátů 12xA4    |
| Zhotovitel: Valbek, spol. s r.o., Vaňurova 505/17, 460 07 Liberec 3                   |                                  | Měřítko 1 : 1000/100   |
| Příloha PODÉLNÉ PROFILY                                                               |                                  | Č. přílohy Paré        |
|                                                                                       |                                  | 3                      |