




SO 126 - NAPOJENÍ PŮVODNÍ I/16 DO MÚK MARTINOVICE
PŘÍČNÉ ŘEZY OK VPRAVO, M 1 : 100

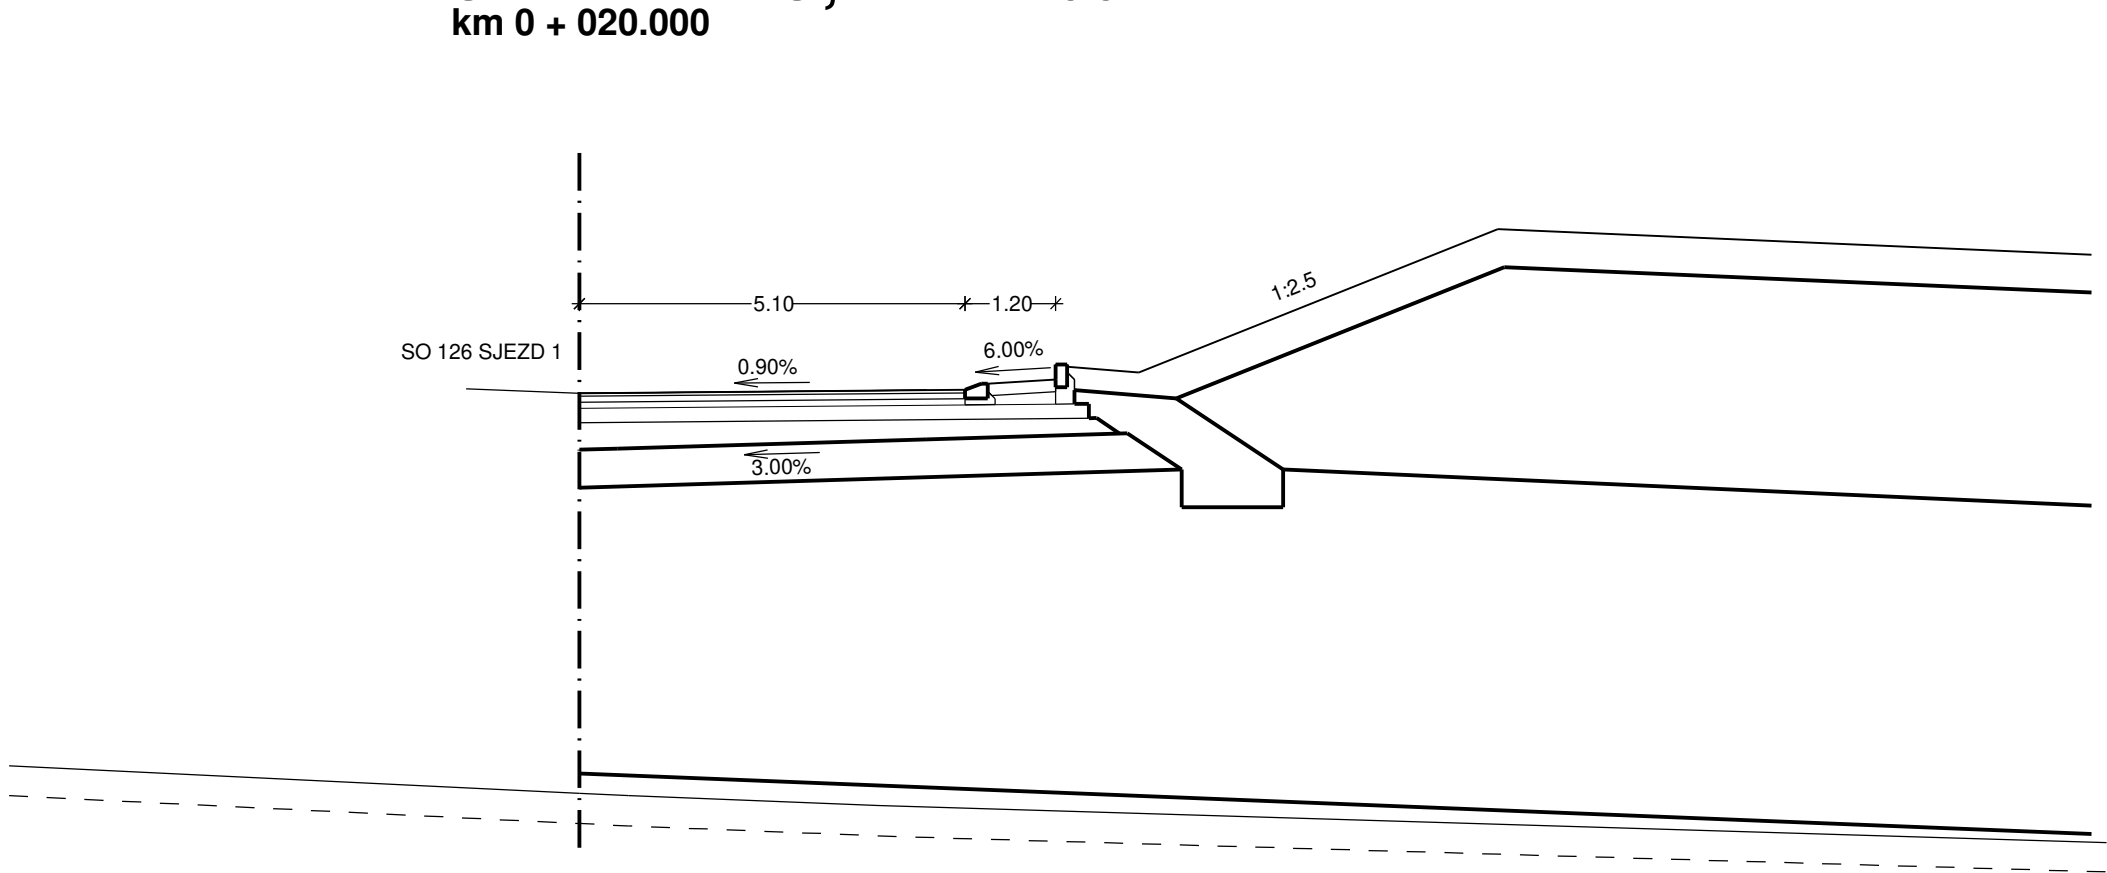


PROJEKTOVANÝ STAV	S. R. 222 m	0.00	226.62	4.60	226.66	5.10	226.66	5.32	226.74	5.40	226.74	6.30	226.80	6.45	226.80	6.45	226.89	7.40	226.89	12.15	231.79	20.00	231.45
ODSAZENÍ OD OSY		0.00	226.62	0.50	226.62																		
STÁVAJÍCÍ TERÉN		0.00	224.33																				
ODSAZENÍ OD OSY			0.65	224.28		3.95	224.16																

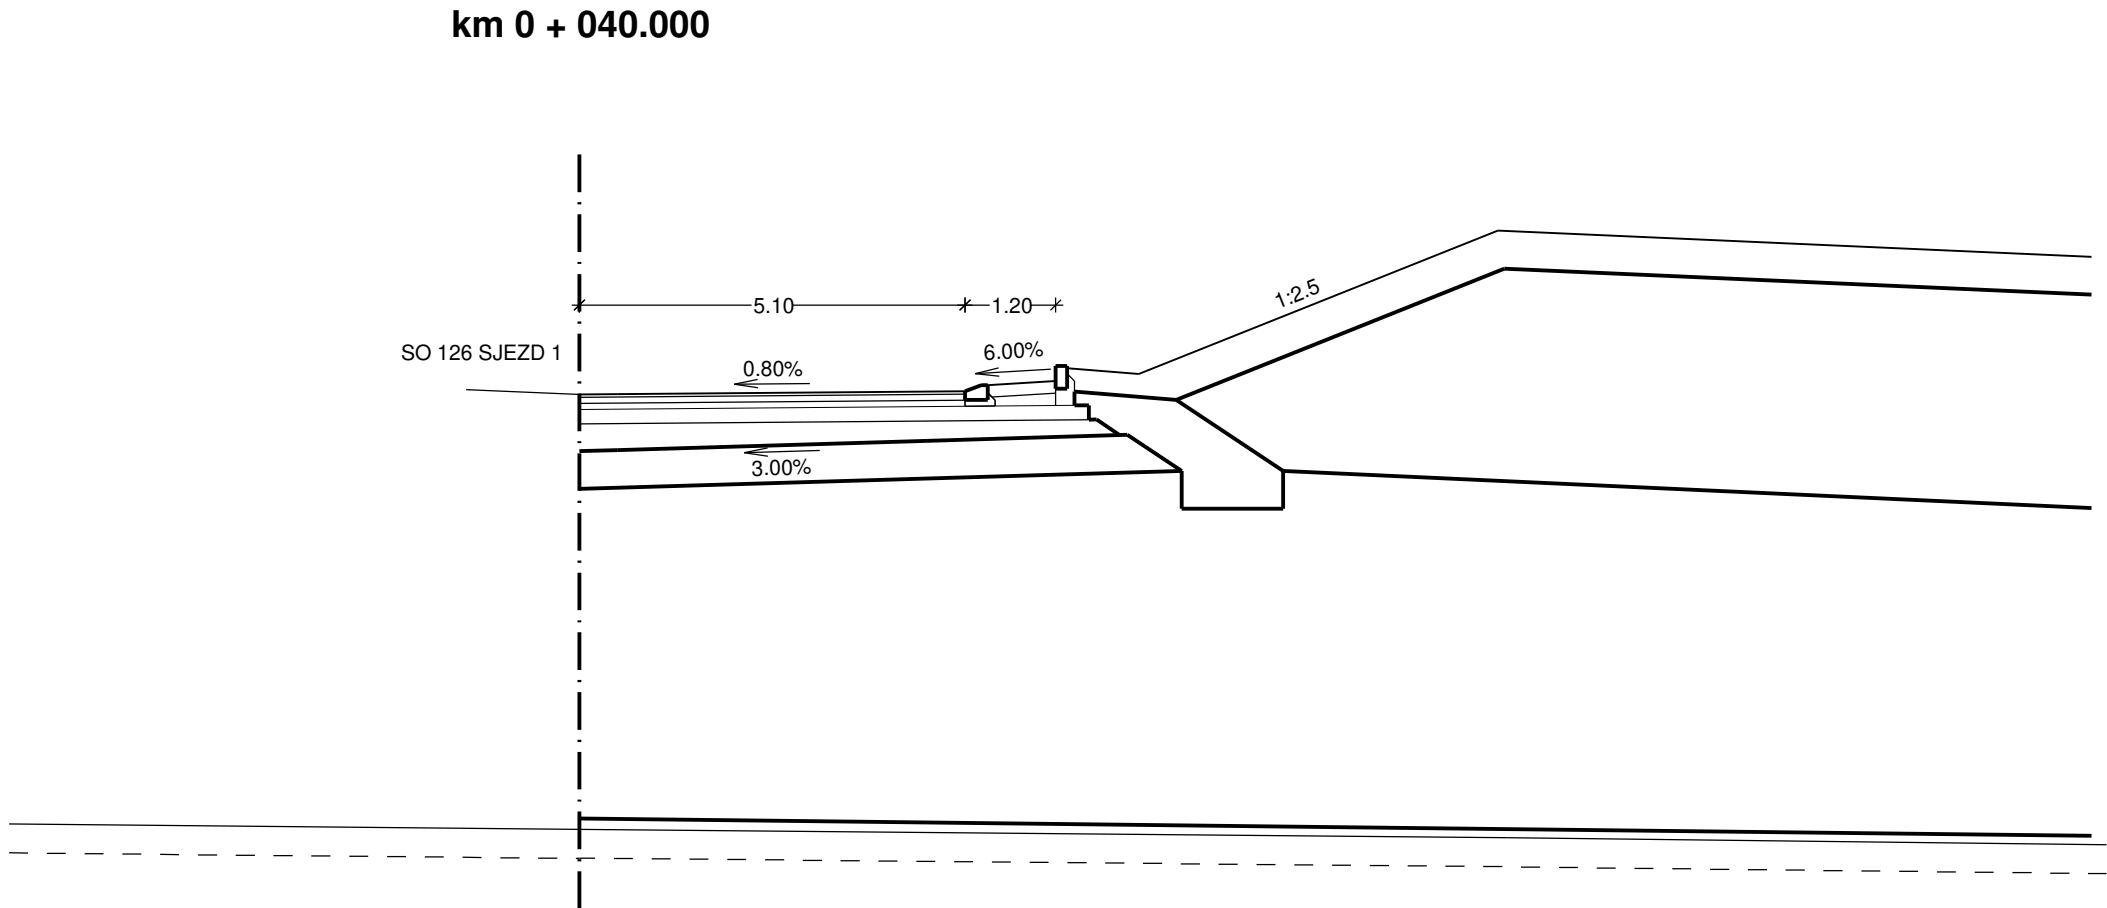


		S. R. 221 m																				
PROJEKTOVANÝ STAV		0.00	229.63																			
ODSAZENÍ OD OSY			0.50	229.64																		

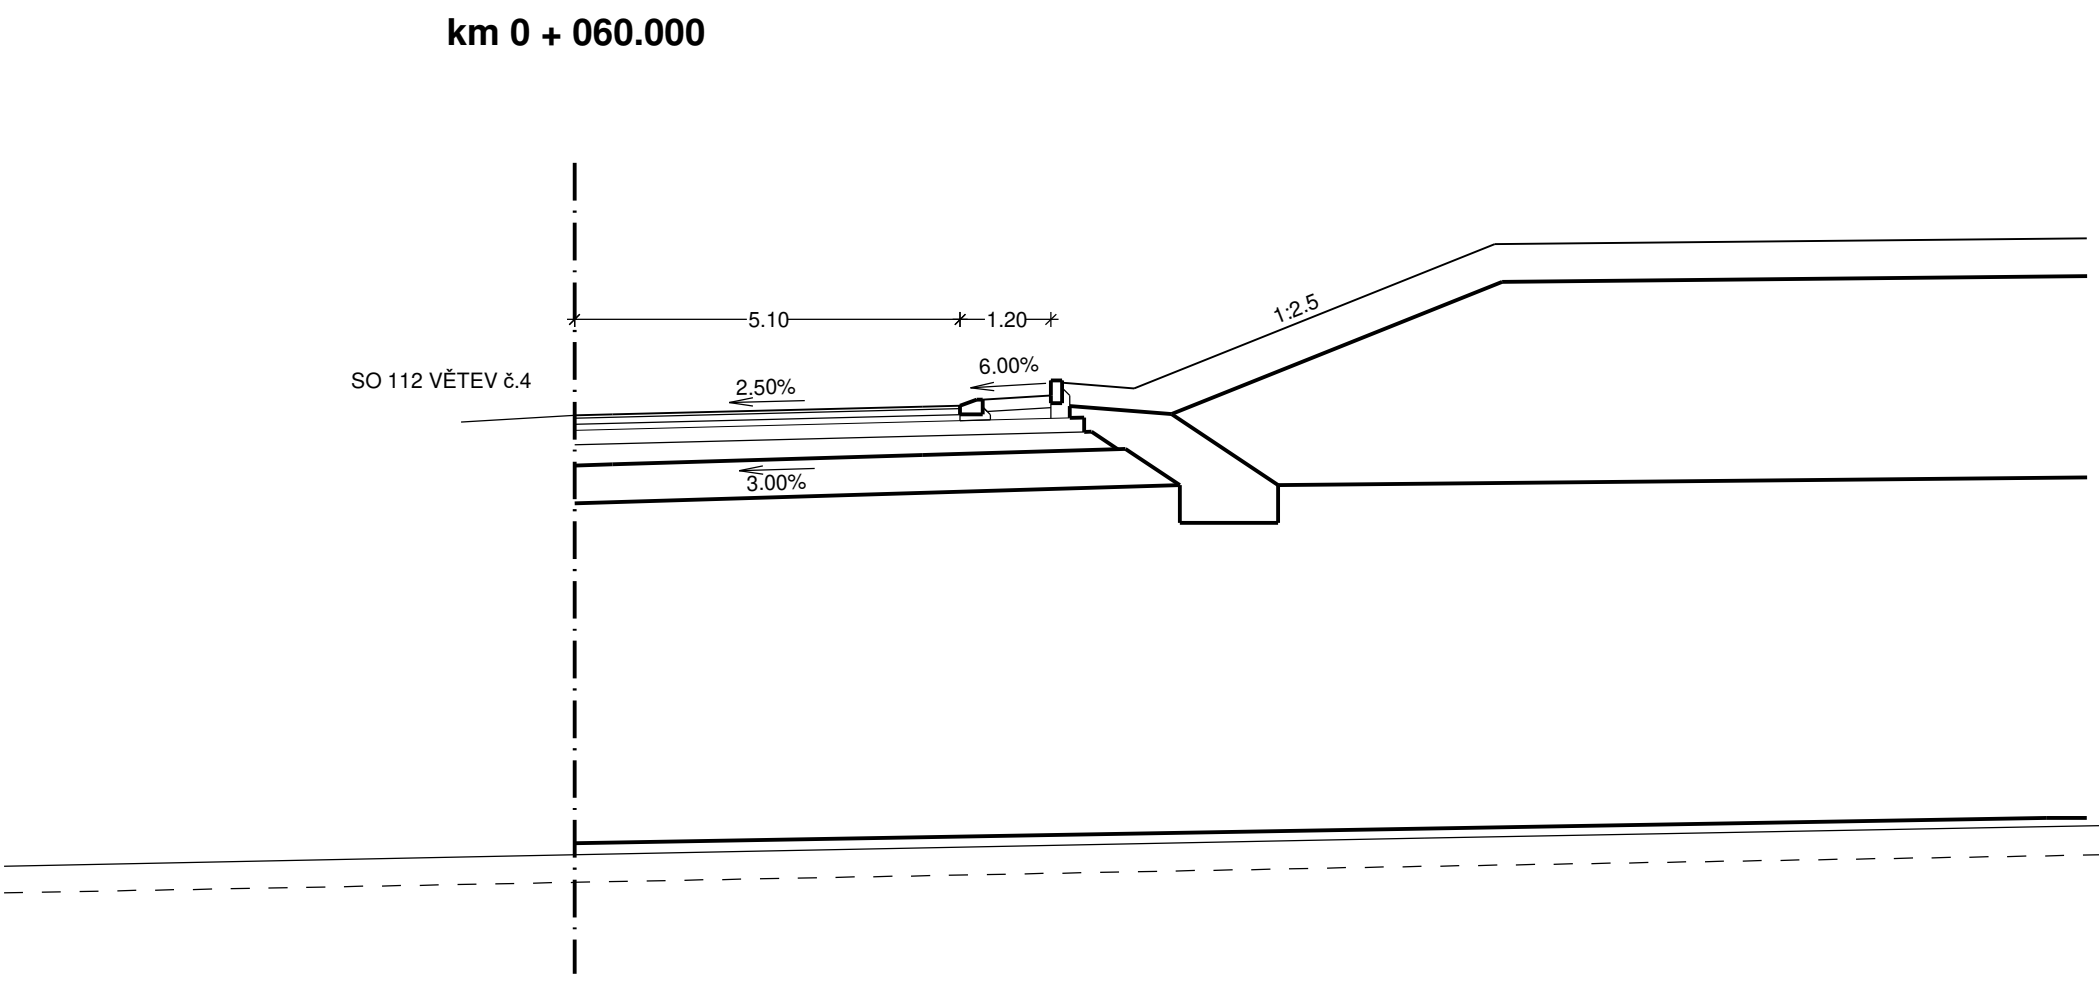


				S. R. 220 m																					
PROJEKTOVANÝ STAV		0.00	229.11																						
ODSAZENÍ OD OSY			0.50	229.12																					
					4.60	229.23	5.10	229.24	5.32	229.32	5.40	229.32	6.30	229.37	6.45	229.37	6.45	229.54	7.40	229.47	12.15	231.37	20.00	231.45	
STÁVAJÍCÍ TERÉN		0.00	223.30																						
ODSAZENÍ OD OSY																							11.23	223.52	

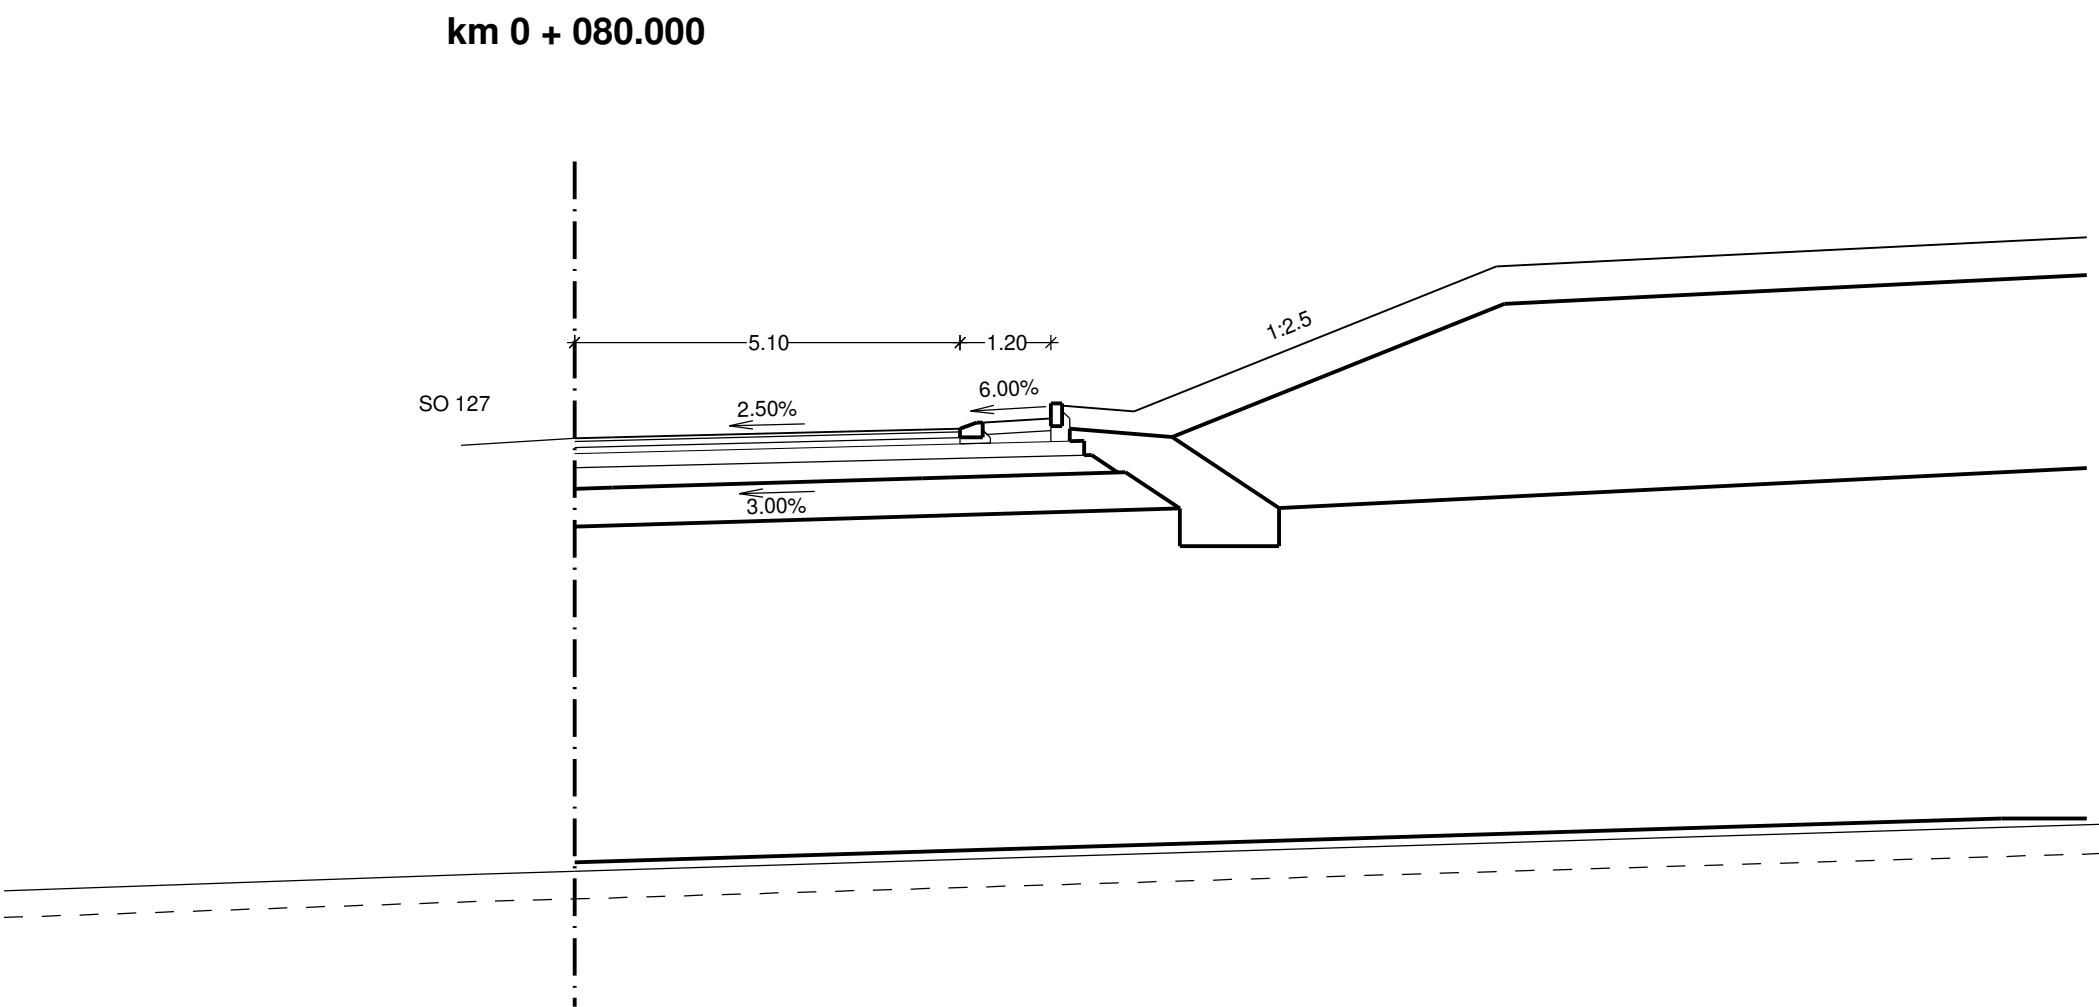

		S. R. 220 m																				
PROJEKTOVANÝ STAV		0.00	228.79																			
ODSAZENÍ OD OSY		0.50	228.80																			

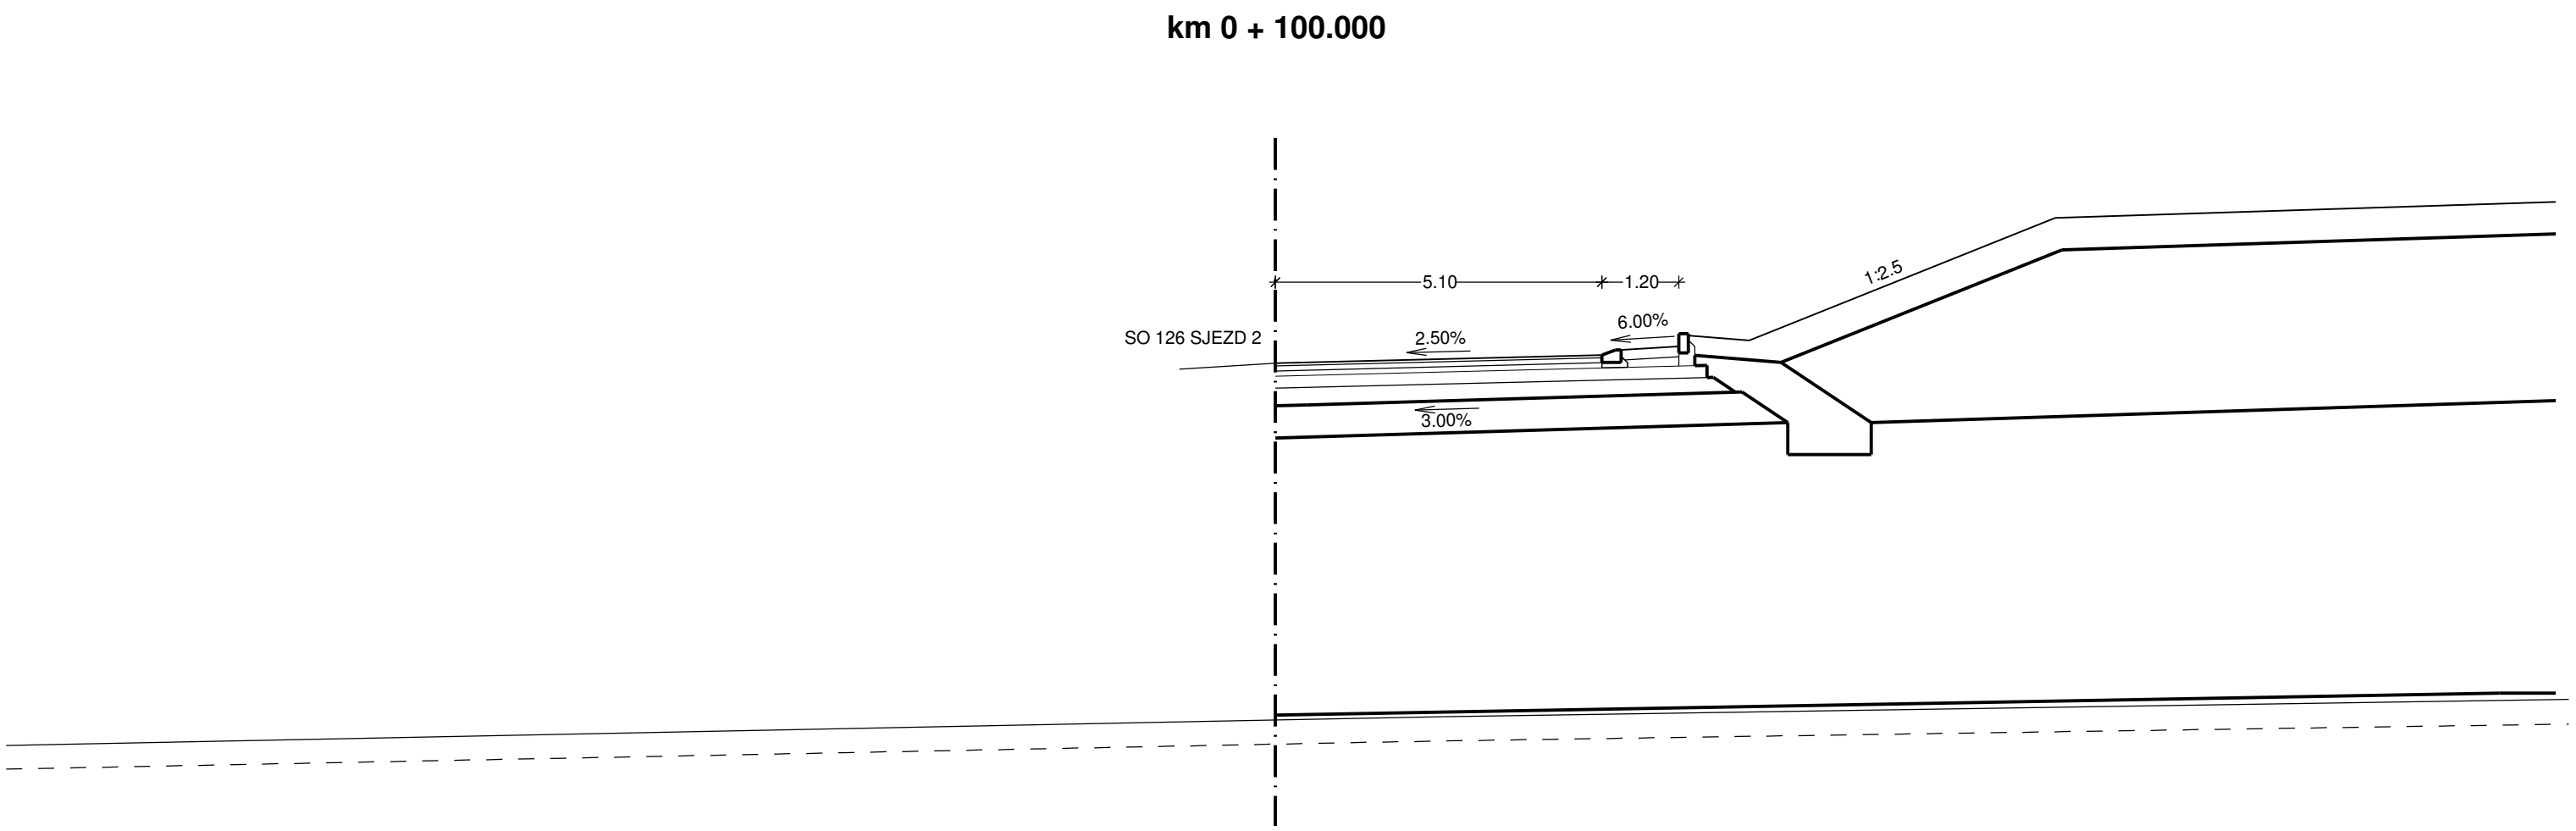

		S. R. 220 m																			
PROJEKTOVANÝ STAV		0,00	228,93	4,60	229,05	5,10	229,06	5,32	229,14	5,40	229,14	6,30	229,19	6,45	229,36	7,40	229,29	12,15	231,19	20,00	231,45
ODSAZENÍ OD OSY		0,00	228,93	0,50	228,94																
STÁVAJÍCÍ TERÉN		0,00	223,36																		
ODSAZENÍ OD OSY				2,62	223,41																

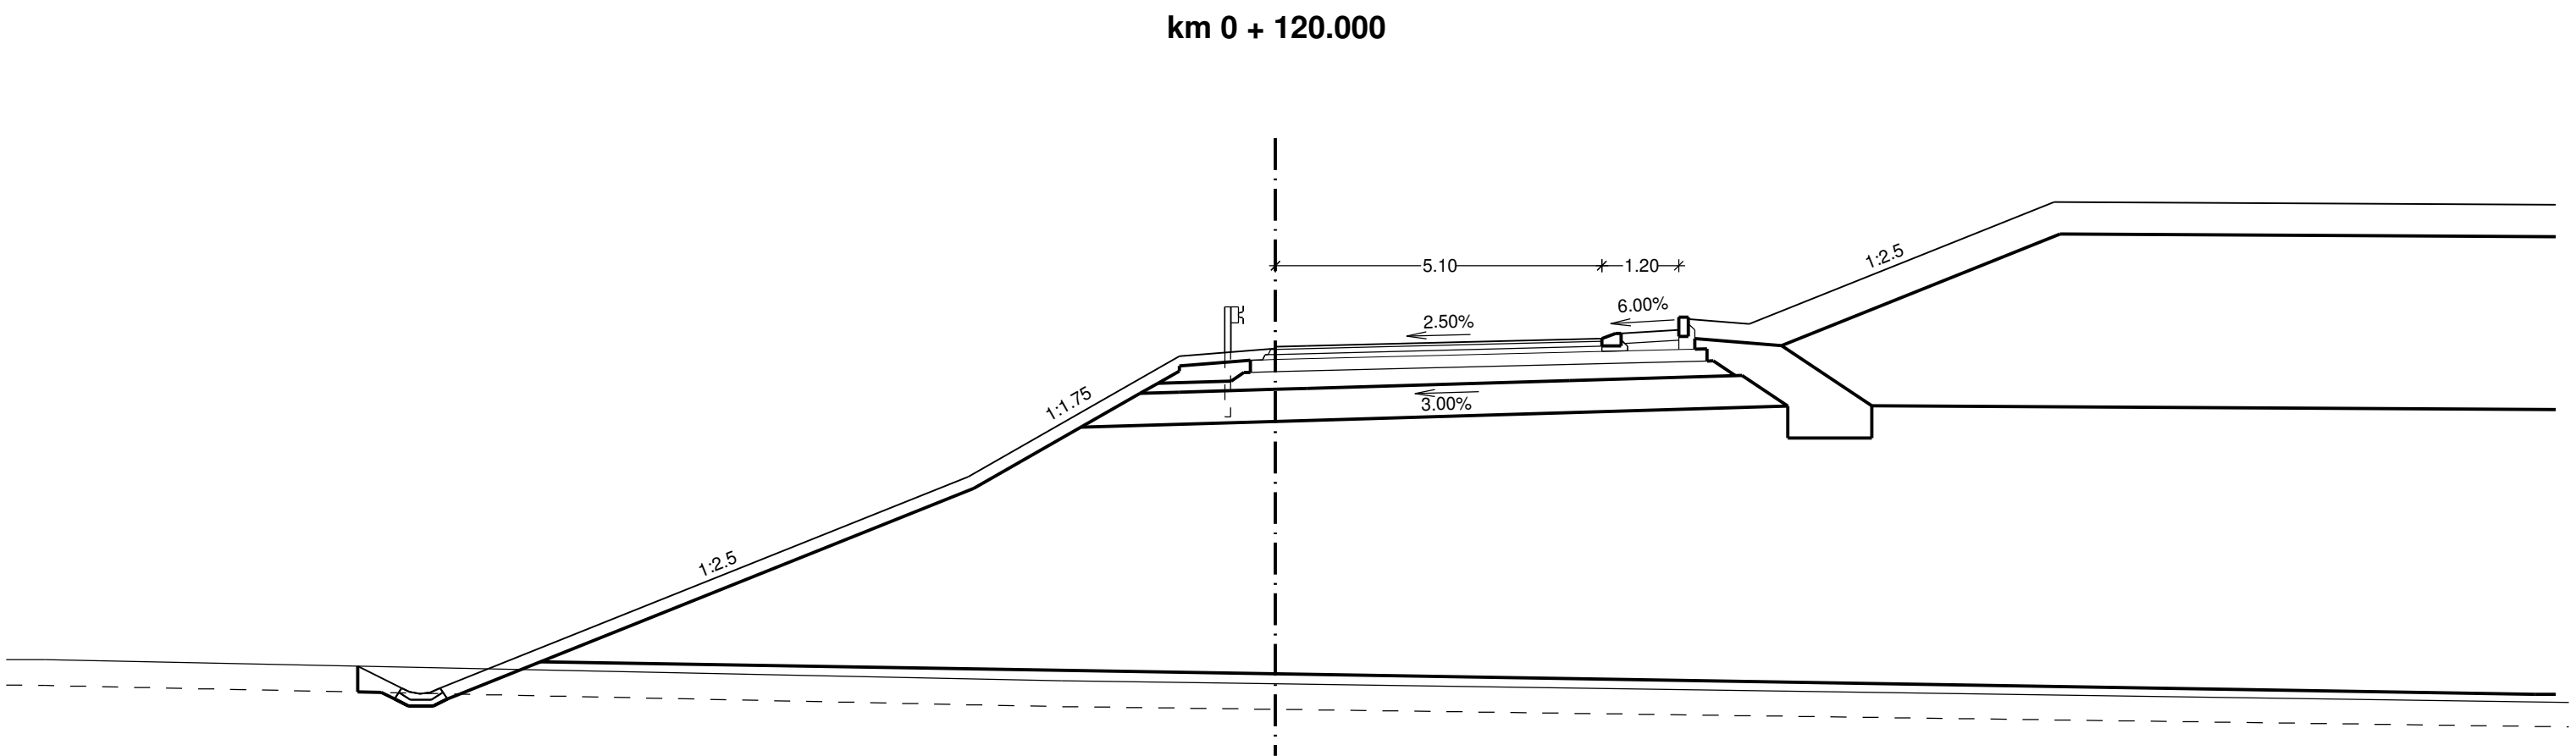

--	--	

Výškový systém: Bpv

SO 126 Napojení původní I/16 do MÚK Martinovice

Objednatel:
**ŘEDITELSTVÍ SILNIC A DÁLNIC**
Ředitelství silnic a dálnic s. p.
Čerčanská 203/12, Krč, 140 00 Praha 4

Zhotovitel:
**Valbek**
Valbek, spol. s r.o.
Vaňurova 505/17
460 07 Liberec 3
HIP:
ING. T. KLIMENT

 Valbek	Vypracoval	M. KOŘÍNEK	Zak. číslo	21-LH3-001
	Zodp. projektant	ING. T. KLIMENT	Datum	02/2025
	Tech. kontrola	ING. M. HANŽL	Stupeň	PDFS
	Akce	I/16 MLADÁ BOLESLAV - MARTINOVICE		Počet formátů
Zhotovitel: Valbek, spol. s r.o. Vaňurova 505/17 460 07 Liberec 3	Příloha	PŘÍČNÉ ŘEZY OK VPRAVO	Měřítko	1 : 100
			Č. přílohy	Paré
			5.2	