
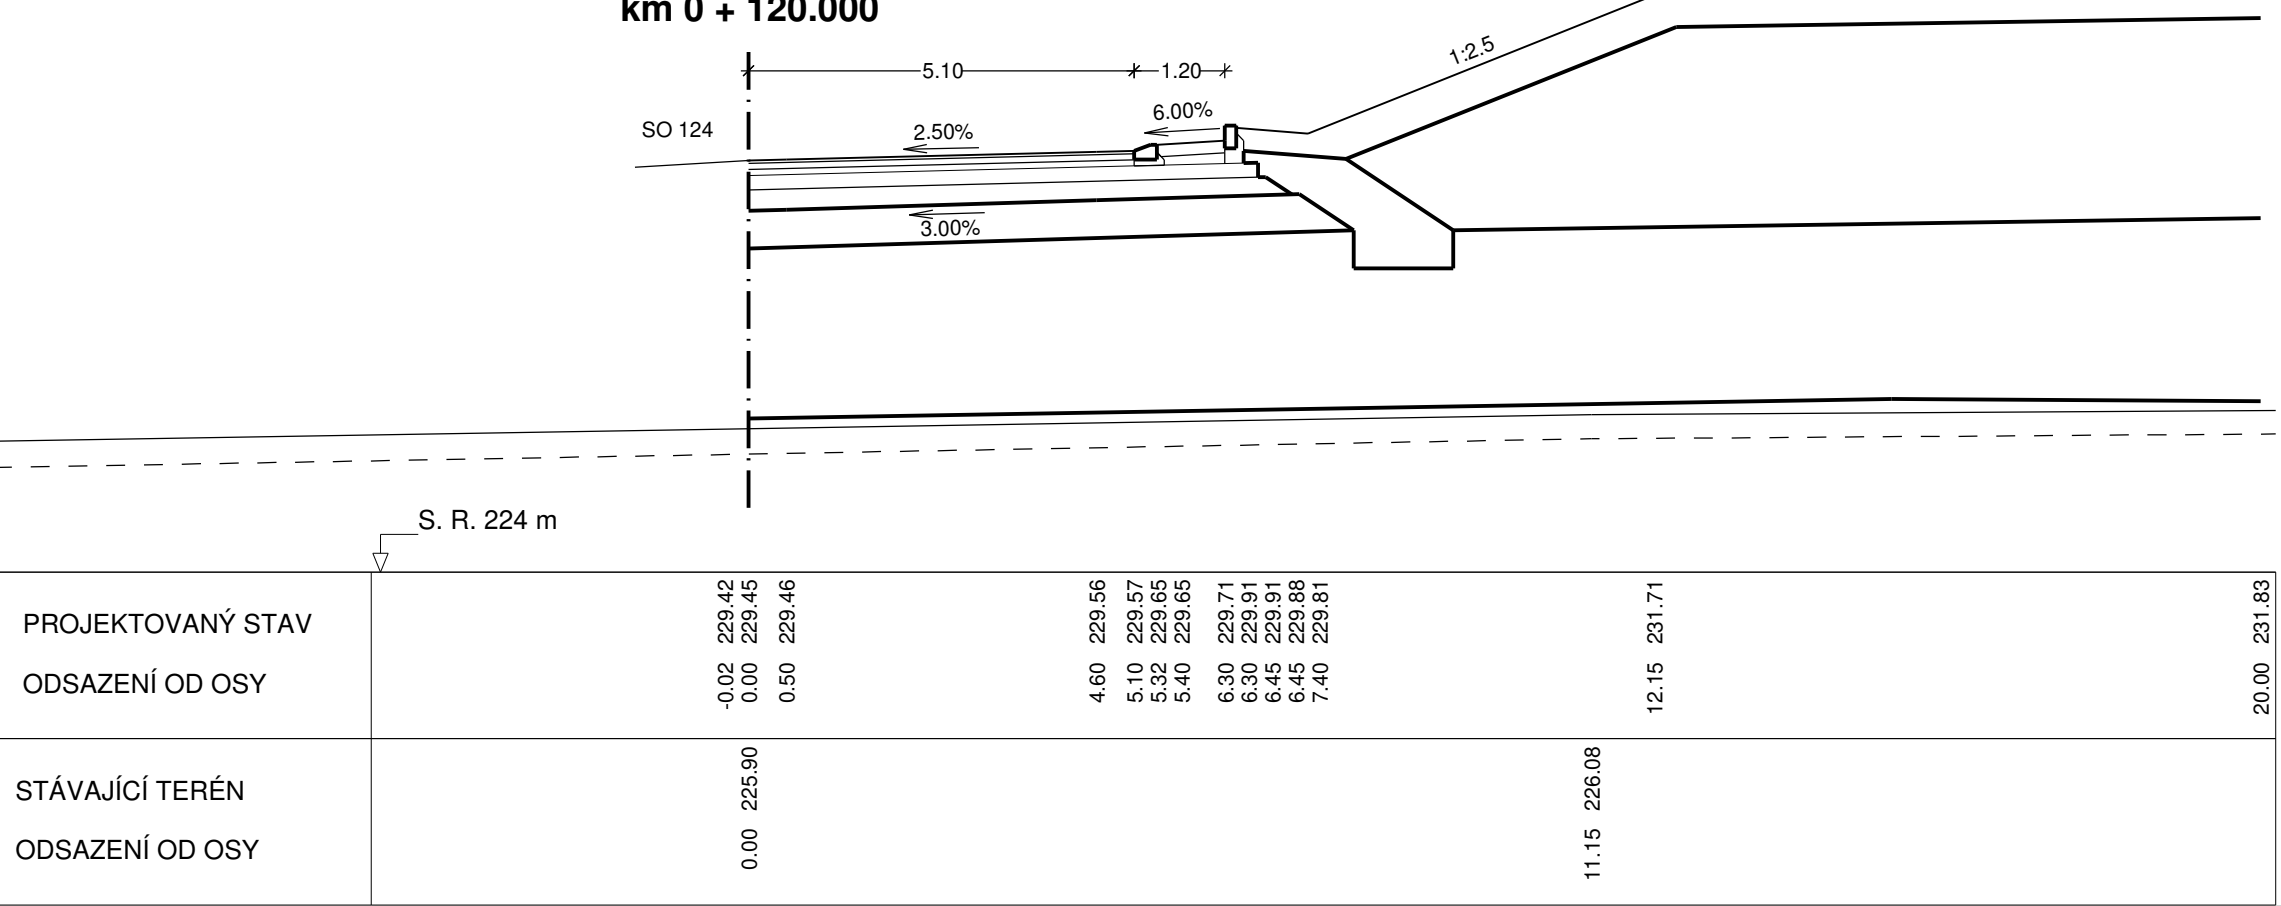
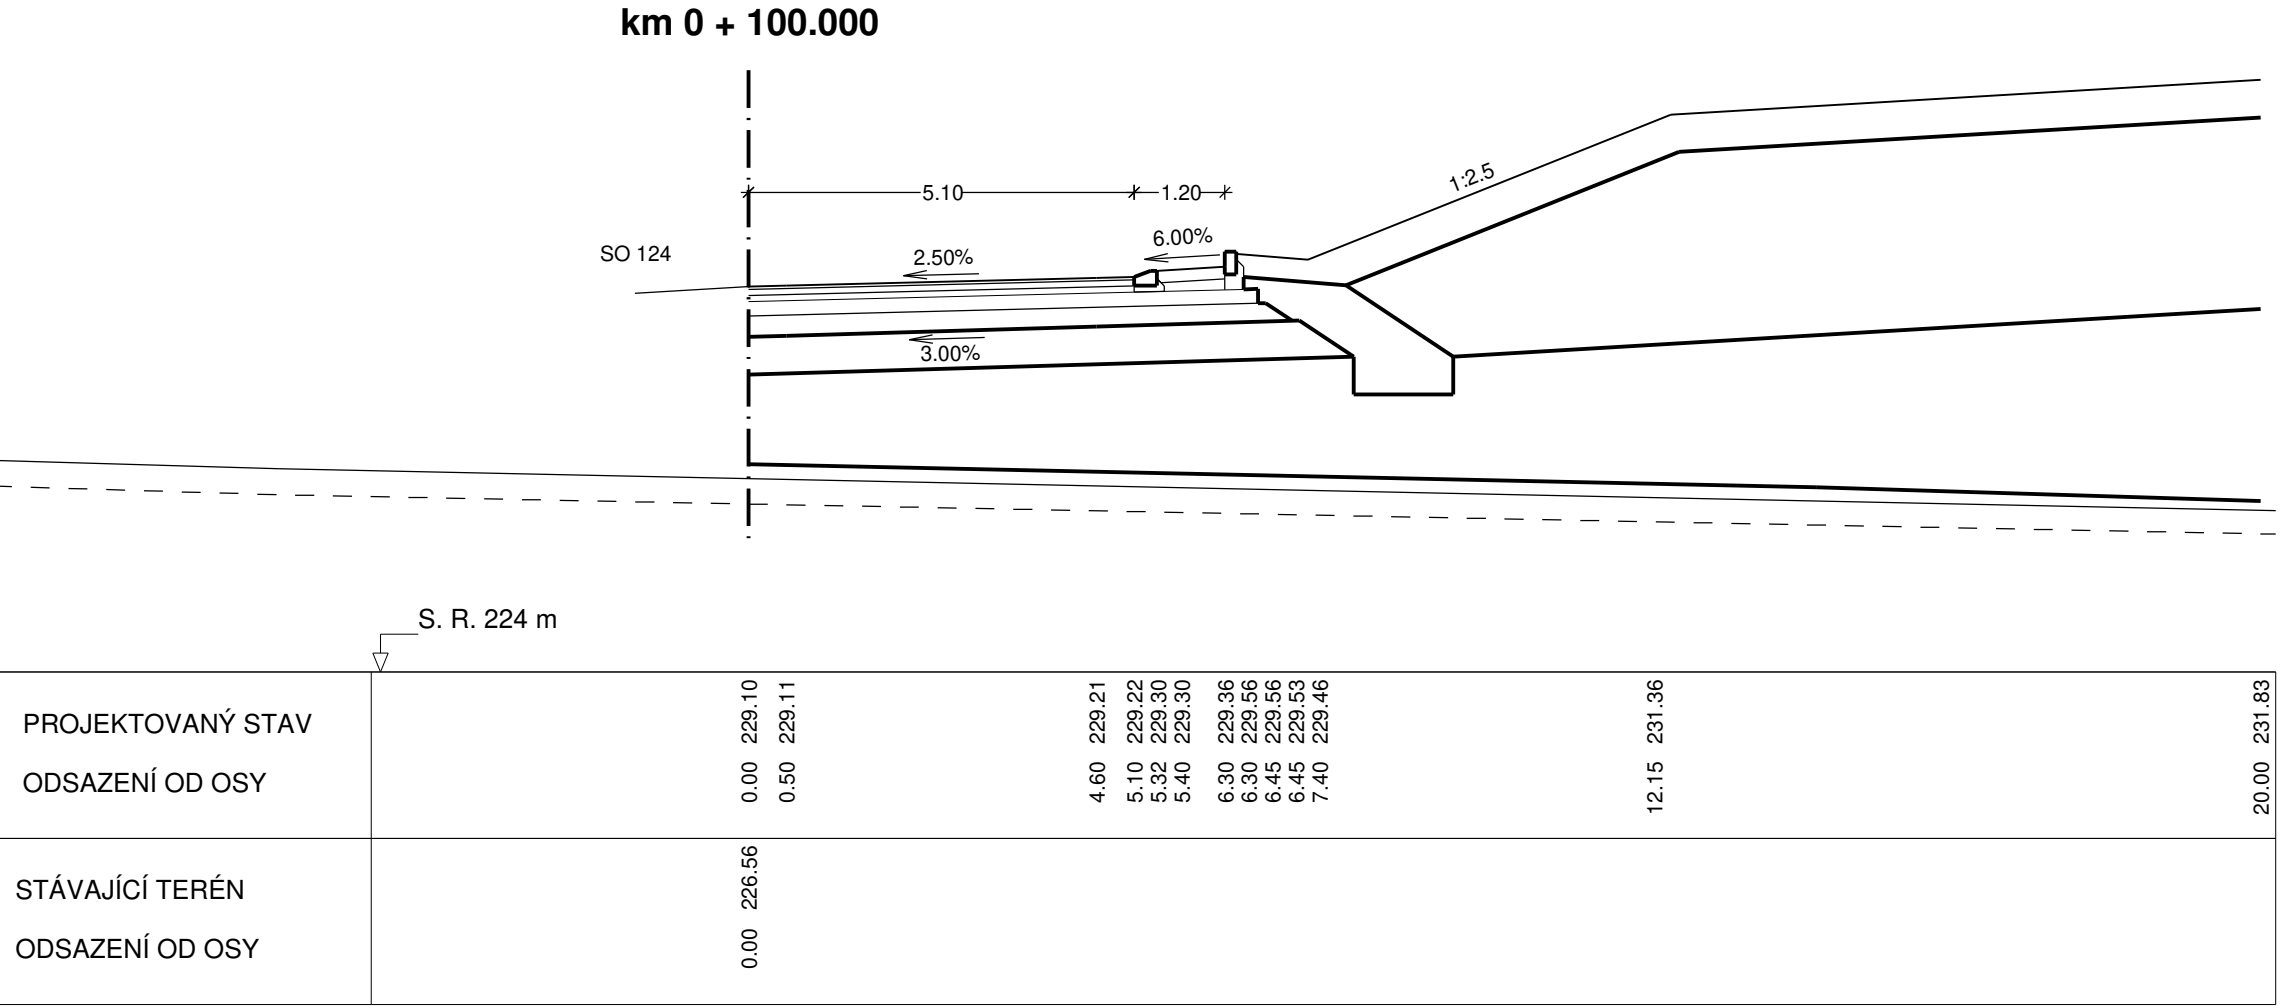
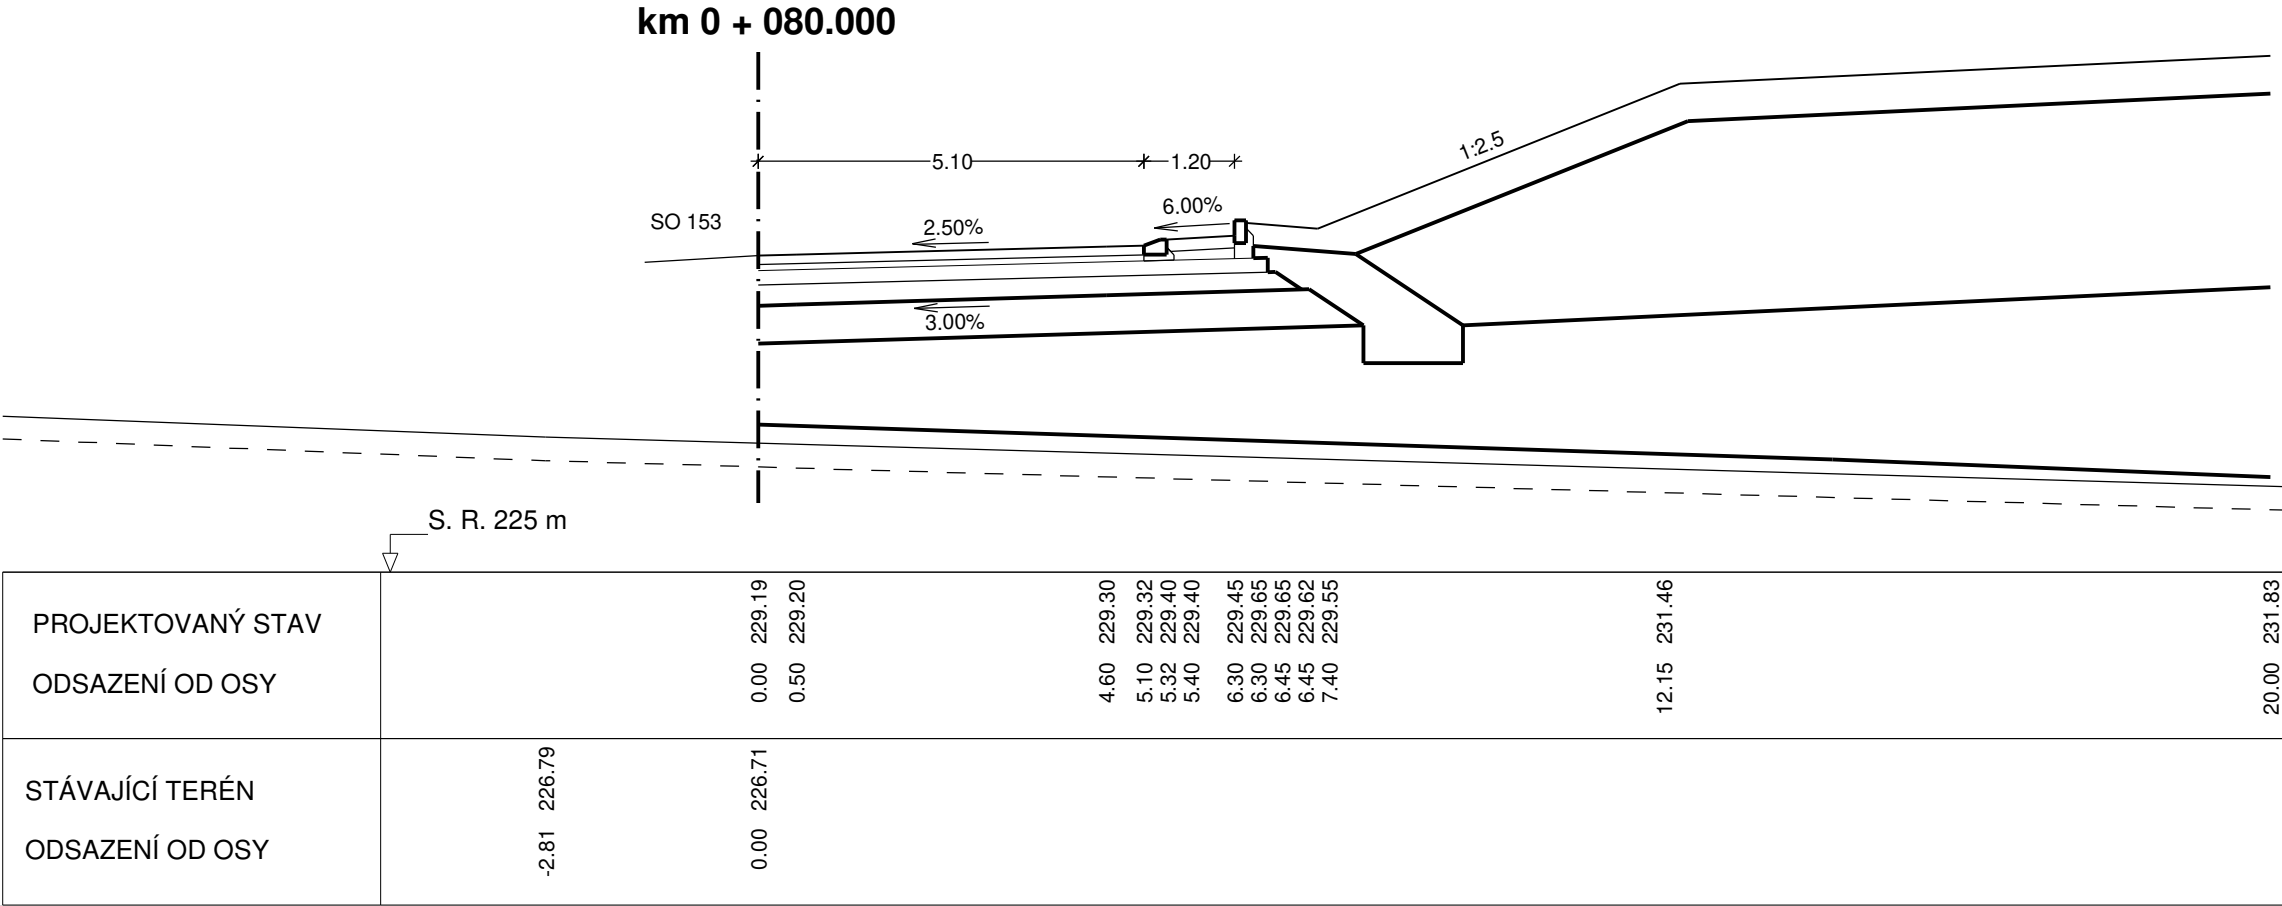
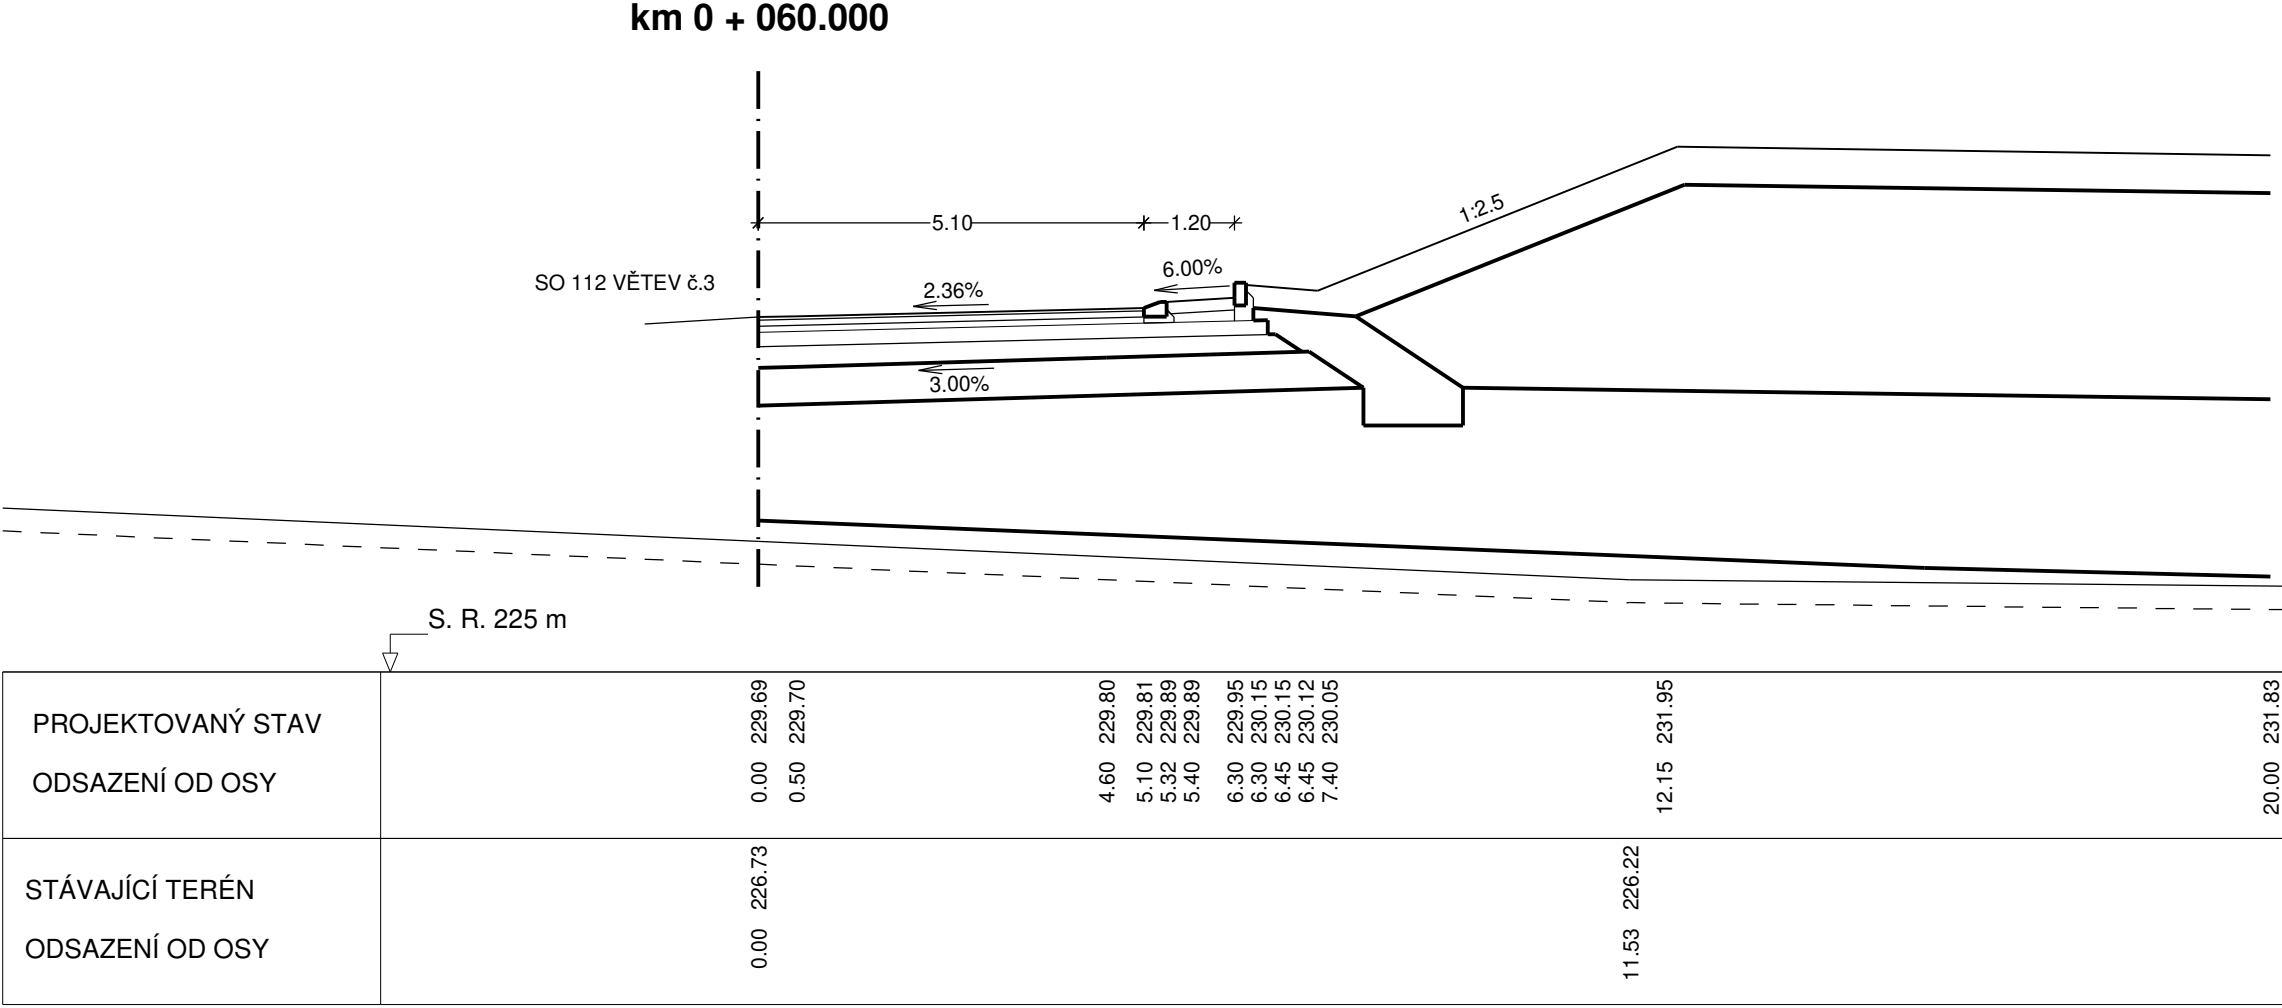
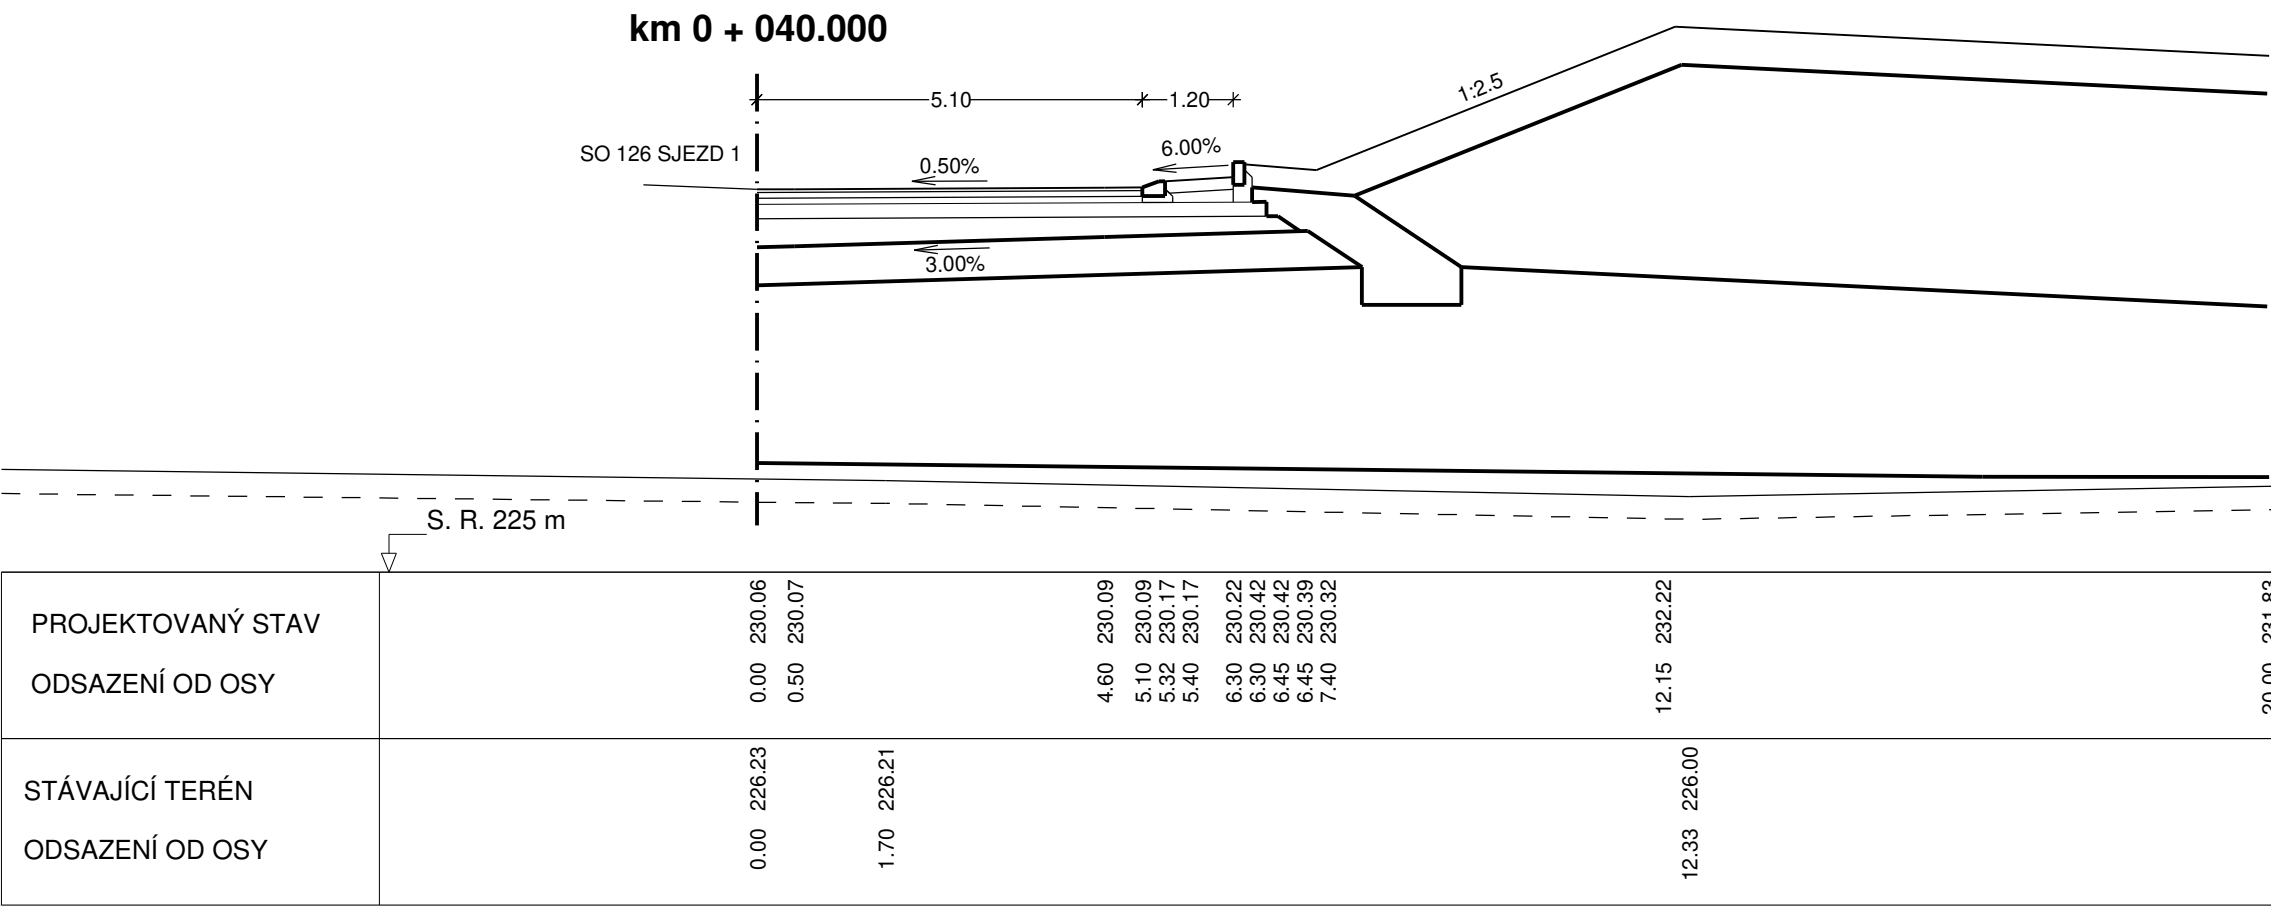


SO 126 - NAPOJENÍ PŮVODNÍ I/16 DO MÚK MARTINOVICE
PŘÍČNÉ ŘEZY OK VLEVO, M 1 : 100

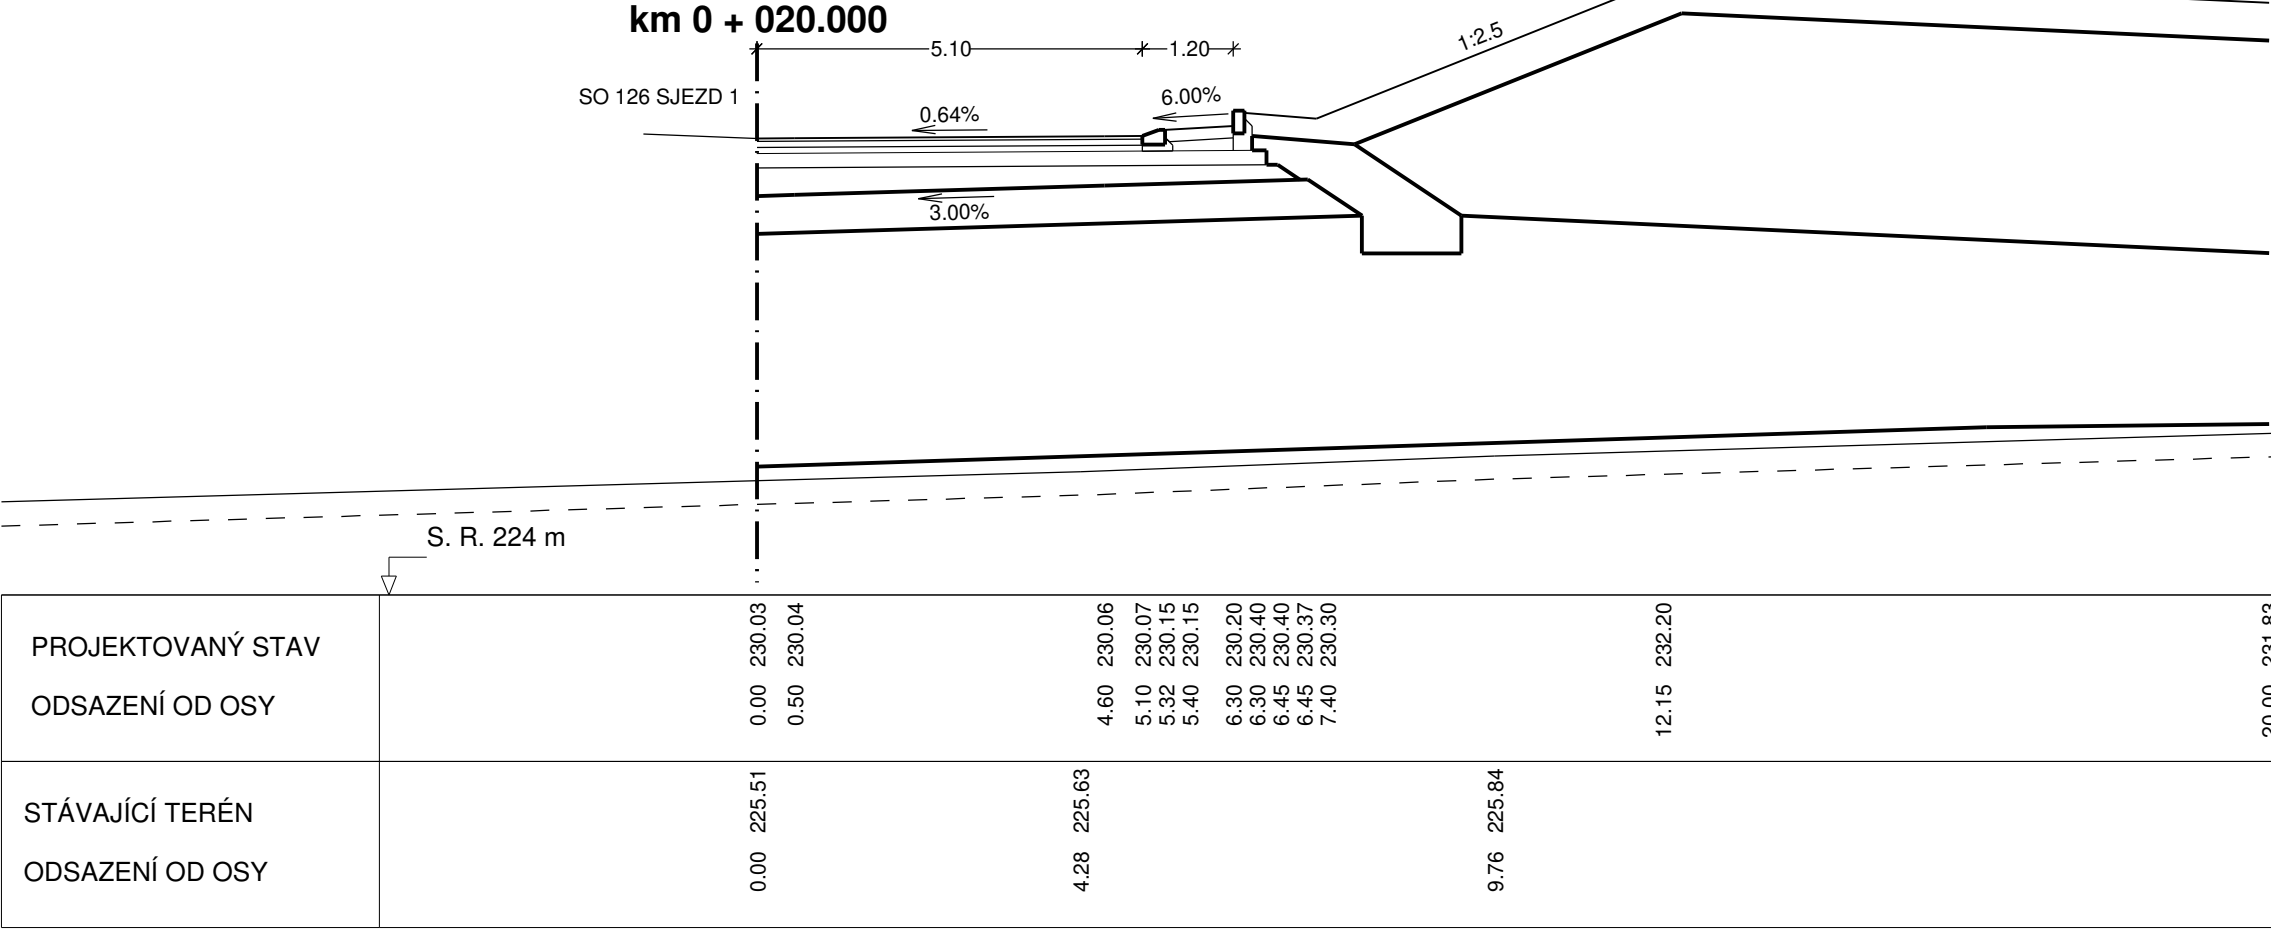

Výškový systém: Bpv

SO 126 Napojení původní I/16 do MÚK Martinovice

Objednatel:



Ředitelství silnic a dálnic s. p.
Čerčanská 2023/12, Krč, 140 00 Praha 4

Zhotovitel:



Valbek, spol. s r.o.
Vaňurova 505/17
460 07 Liberec 3

HIP:

ING. T. KLIMENT



Valbek, spol. s r.o.
Vaňurova 505/17
460 07 Liberec 3

Vypracoval	M. KOŘÍNEK	Zak. číslo	21-LI13-001
Zodp. projektant	ING. T. KLIMENT	Datum	02/2025
Tech. kontrola	ING. M. HANŽL	Stupeň	PDPS
I/16 MLADÁ BOLESLAV - MARTINOVICE		Počet formátů	6 x A4
		Měřítko	1 : 100
		Č. přílohy	Paré
Příloha		PŘÍČNÉ ŘEZY OK VLEVO	
Zhotovitel:		5.3	

Valbek, spol. s r.o.
Vaňurova 505/17
460 07 Liberec 3