


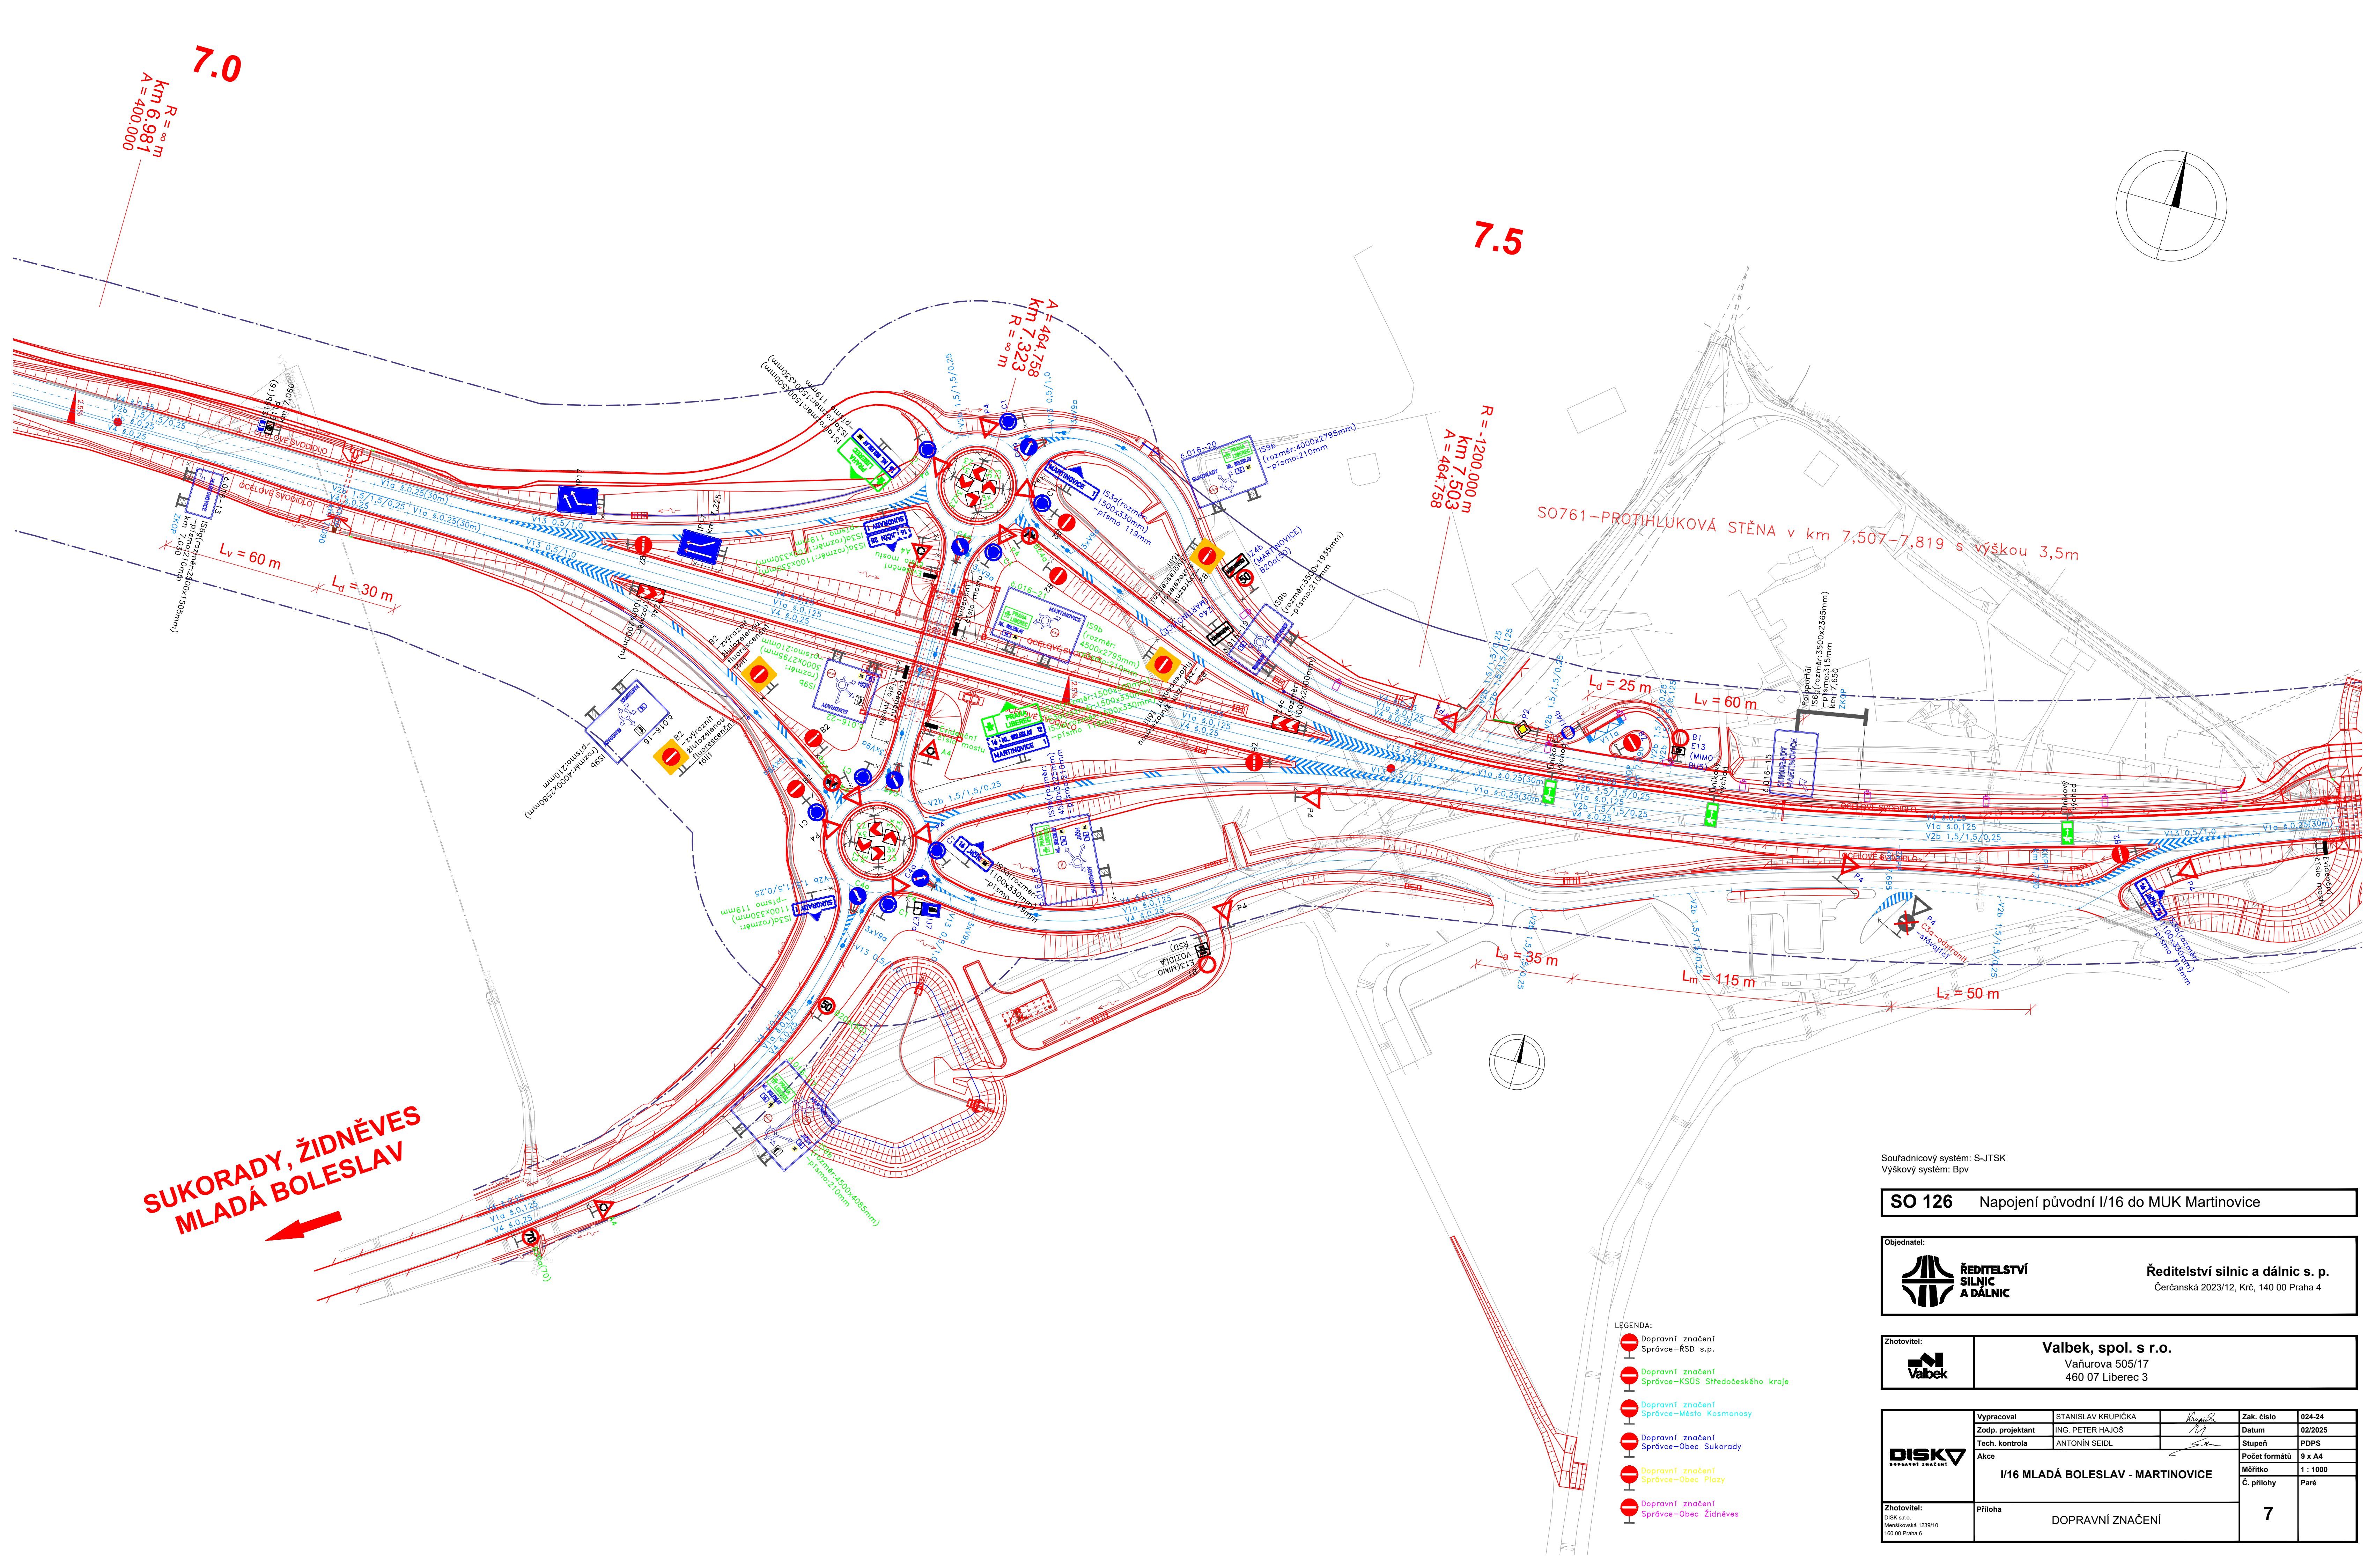

SUKORADY, ŽIDNĚVES
MLADÁ BOLESLAV

- LEGENDA:
- Dopravní značení
Správce-RSD s.p.
 - Dopravní značení
Správce-KSÚS Středočeského kraje
 - Dopravní značení
Správce-Město Kosmonosy
 - Dopravní značení
Správce-Obec Sukorady
 - Dopravní značení
Správce-Obec Plazy
 - Dopravní značení
Správce-Obec Židněves

Souřadnicový systém: S-JTSK
Výškový systém: Bpv

SO 126 Napojení původní I/16 do MUK Martinovice

Objednatel:

 **ŘEDITELSTVÍ
SILNIC
A DÁLNIC**

Ředitelství silnic a dálnic s. p.
Čerčanská 2023/12, Krč, 140 00 Praha 4

Zhotovitel:

 **Valbek**

Valbek, spol. s r.o.
Vaňurova 505/17
460 07 Liberec 3

	Vypracoval	STANISLAV KRUPÍČKA	Zak. číslo	024-24	
	Zodp. projektant	ING. PETER HAJOŠ	Datum	02/2025	
	Tech. kontrola	ANTONÍN SEIDL	Stupeň	PDPS	
	Akce	I/16 MLADÁ BOLESLAV - MARTINOVICE			
Zhotovitel: DISK s.r.o. Mentšikovská 1239/10 160 00 Praha 6	Příloha DOPRAVNÍ ZNAČENÍ			Počet formátů	9 x A4
				Měřítko	1 : 1000
				Č. přílohy	Paré
7					