


SO 127 - NAPOJENÍ ČSPH NA SILNICI I/16
SITUACE, M 1 : 1 000

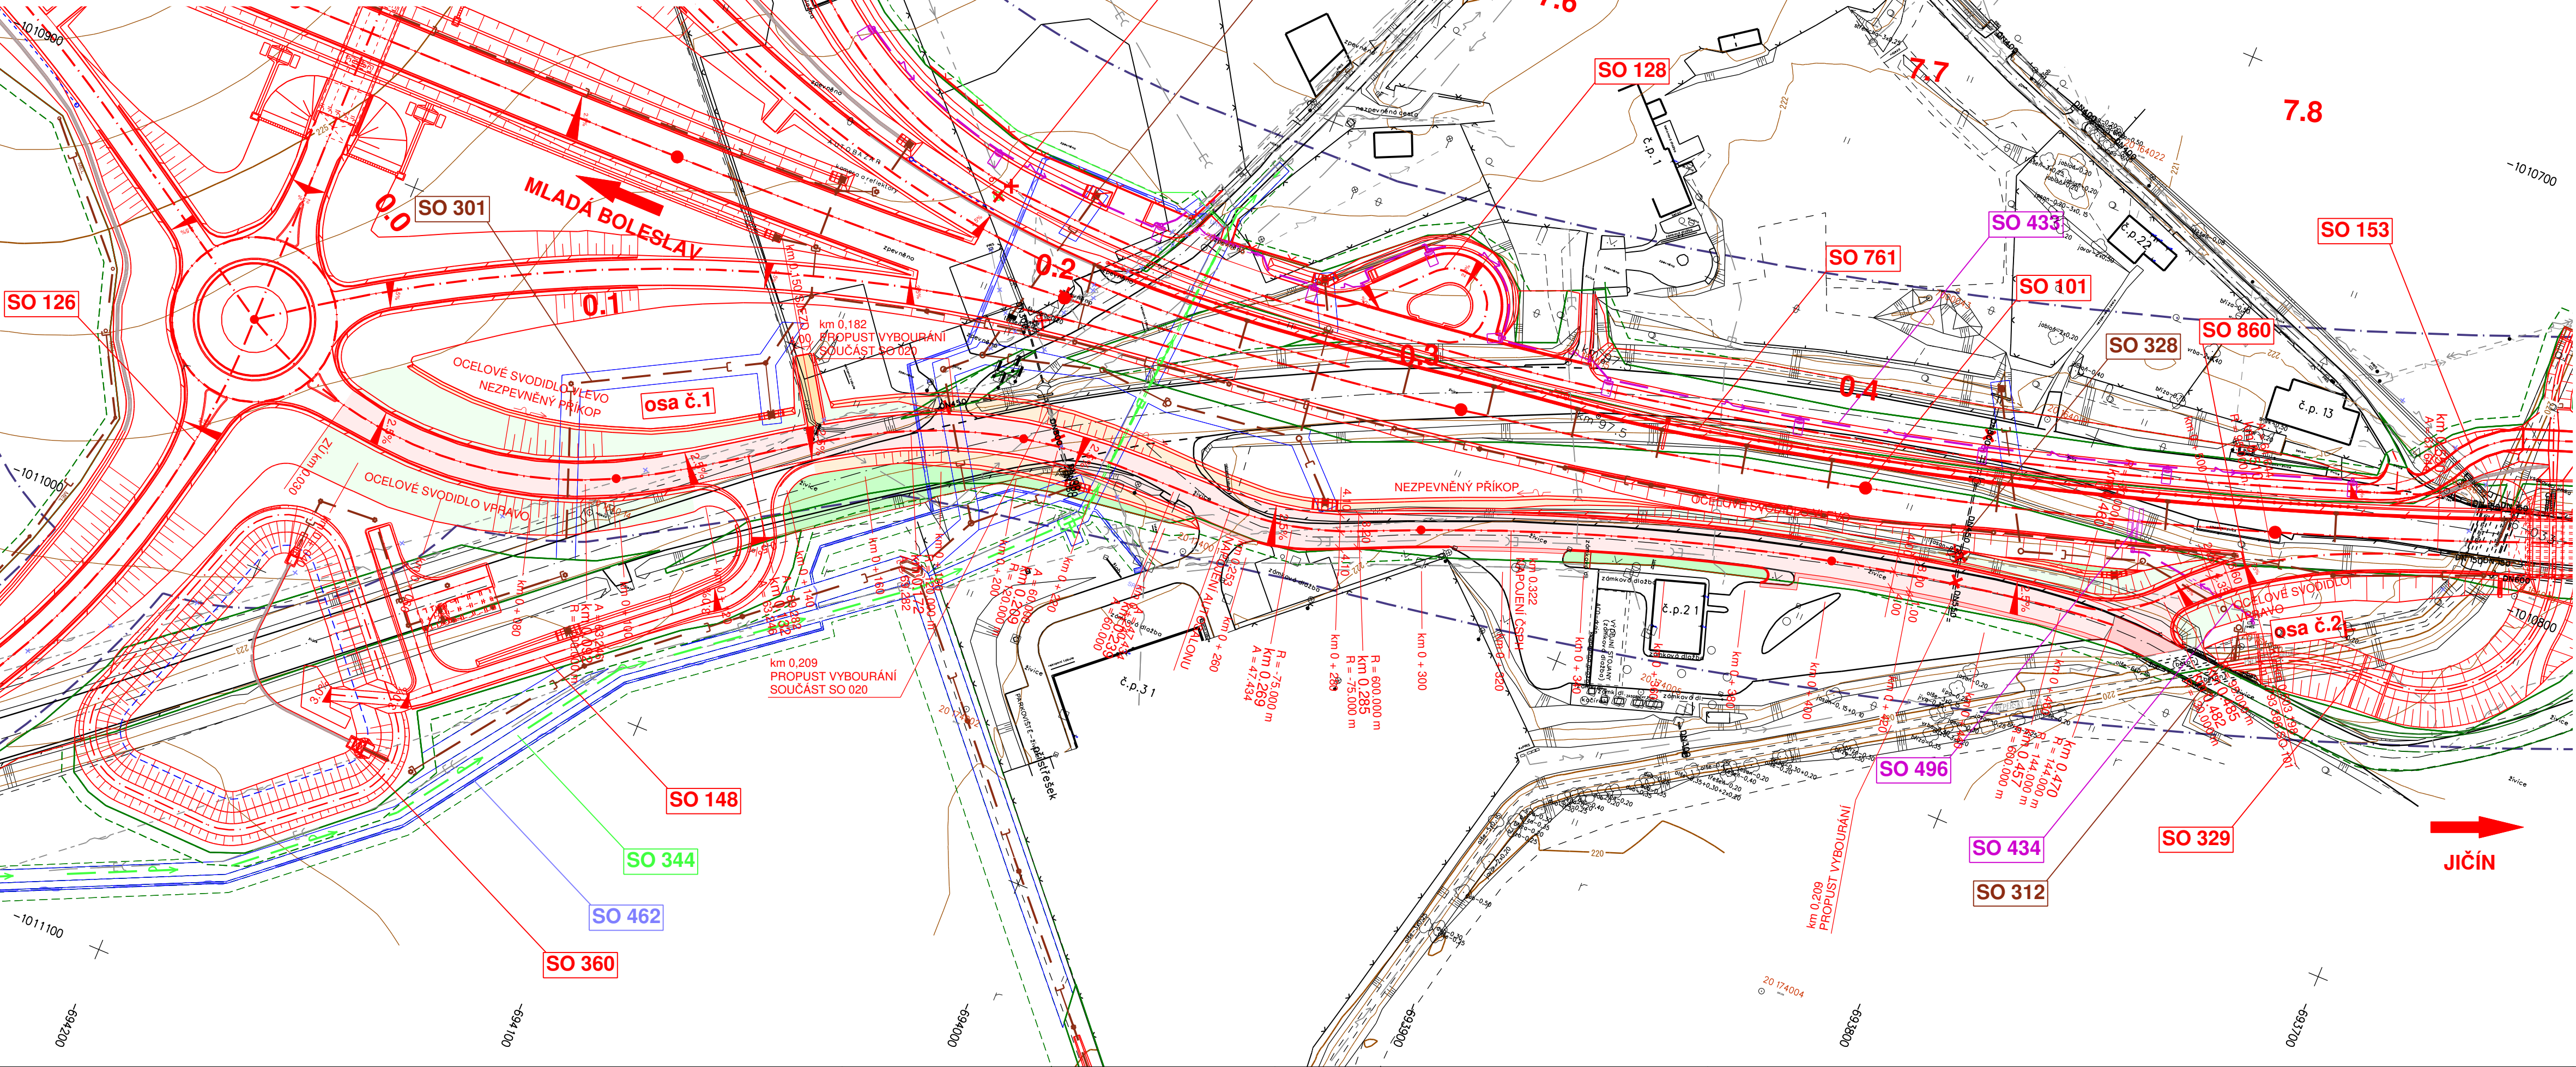

LEGENDA:		NOVÉ IS	
PLOCHY		VOZOVKA - ASFALTOVÝ KRYT	DEŠŤOVÁ KANALIZACE
		VOZOVKA - FRÉZOVANÁ	MELIORACE
		VOZOVKA - POLNÍ CESTY	VÝTLAK
		CHODNÍK	VODOVOD
		DLAŽBA VOZOVKY	NADZEMNÍ VEDENÍ NN
		SVAHY VÝKOPU	NADZEMNÍ VEDENÍ VN
		SVAHY NÁSYPU	PODZEMNÍ VEDENÍ NN
		VEGETAČNÍ ÚPRAVY	PODZEMNÍ SDĚLOVACÍ VEDENÍ
		TRVALÝ ZÁBOR	PLYNOVOD - STL
		DOČASNÝ ZÁBOR	
OBVOD STAVBY		STÁVAJÍCÍ IS - INFORMATIVNÍ ZÁKRES	
			PODZEMNÍ VEDENÍ NN
			PODZEMNÍ VEDENÍ VN
			NADZEMNÍ VEDENÍ NN
			NADZEMNÍ VEDENÍ VN
			NADZEMNÍ VEDENÍ VVN
			DEŠŤOVÁ KANALIZACE
			PLYNOVOD - STL
			PODZEMNÍ SDĚLOVACÍ VEDENÍ
			VODOVOD

Souřadnicový systém: S-JTSK
Výškový systém: Bpv

SO 127 Napojení ČSPH na silnici I/16

Objednatel:



**ŘEDITELSTVÍ
SILNIC
A DÁLNIC**

Ředitelství silnic a dálnic s. p.
Čerčanská 2023/12, Krč, 140 00 Praha 4

Zhotovitel:	Valbek, spol. s r.o. Vaňurova 505/17 460 07 Liberec 3	HIP:
		ING. T. KLIMENT

	Vypracoval	M. KOŘÍNEK	Zak. číslo	21-LI13-001	
	Zodp. projektant	ING. T. KLIMENT	Datum	02/2025	
	Tech. kontrola	ING. M. HANŽL	Stupeň	PDPS	
	Akce I/16 MLADÁ BOLESLAV - MARTINOVICE		Počet formátů	4 x A4	
			Měřítko	1 : 1 000	
Zhotovitel: Valbek, spol. s r.o. Vaňurova 505/17 460 07 Liberec 3	Příloha SITUACE		2	Č. přílohy	Paré