
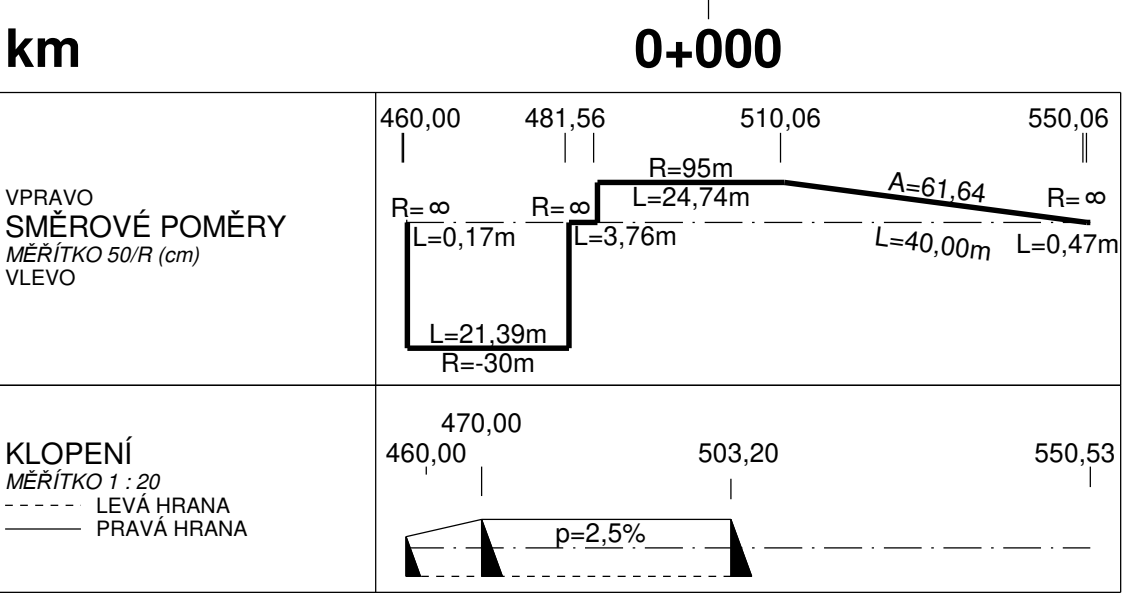
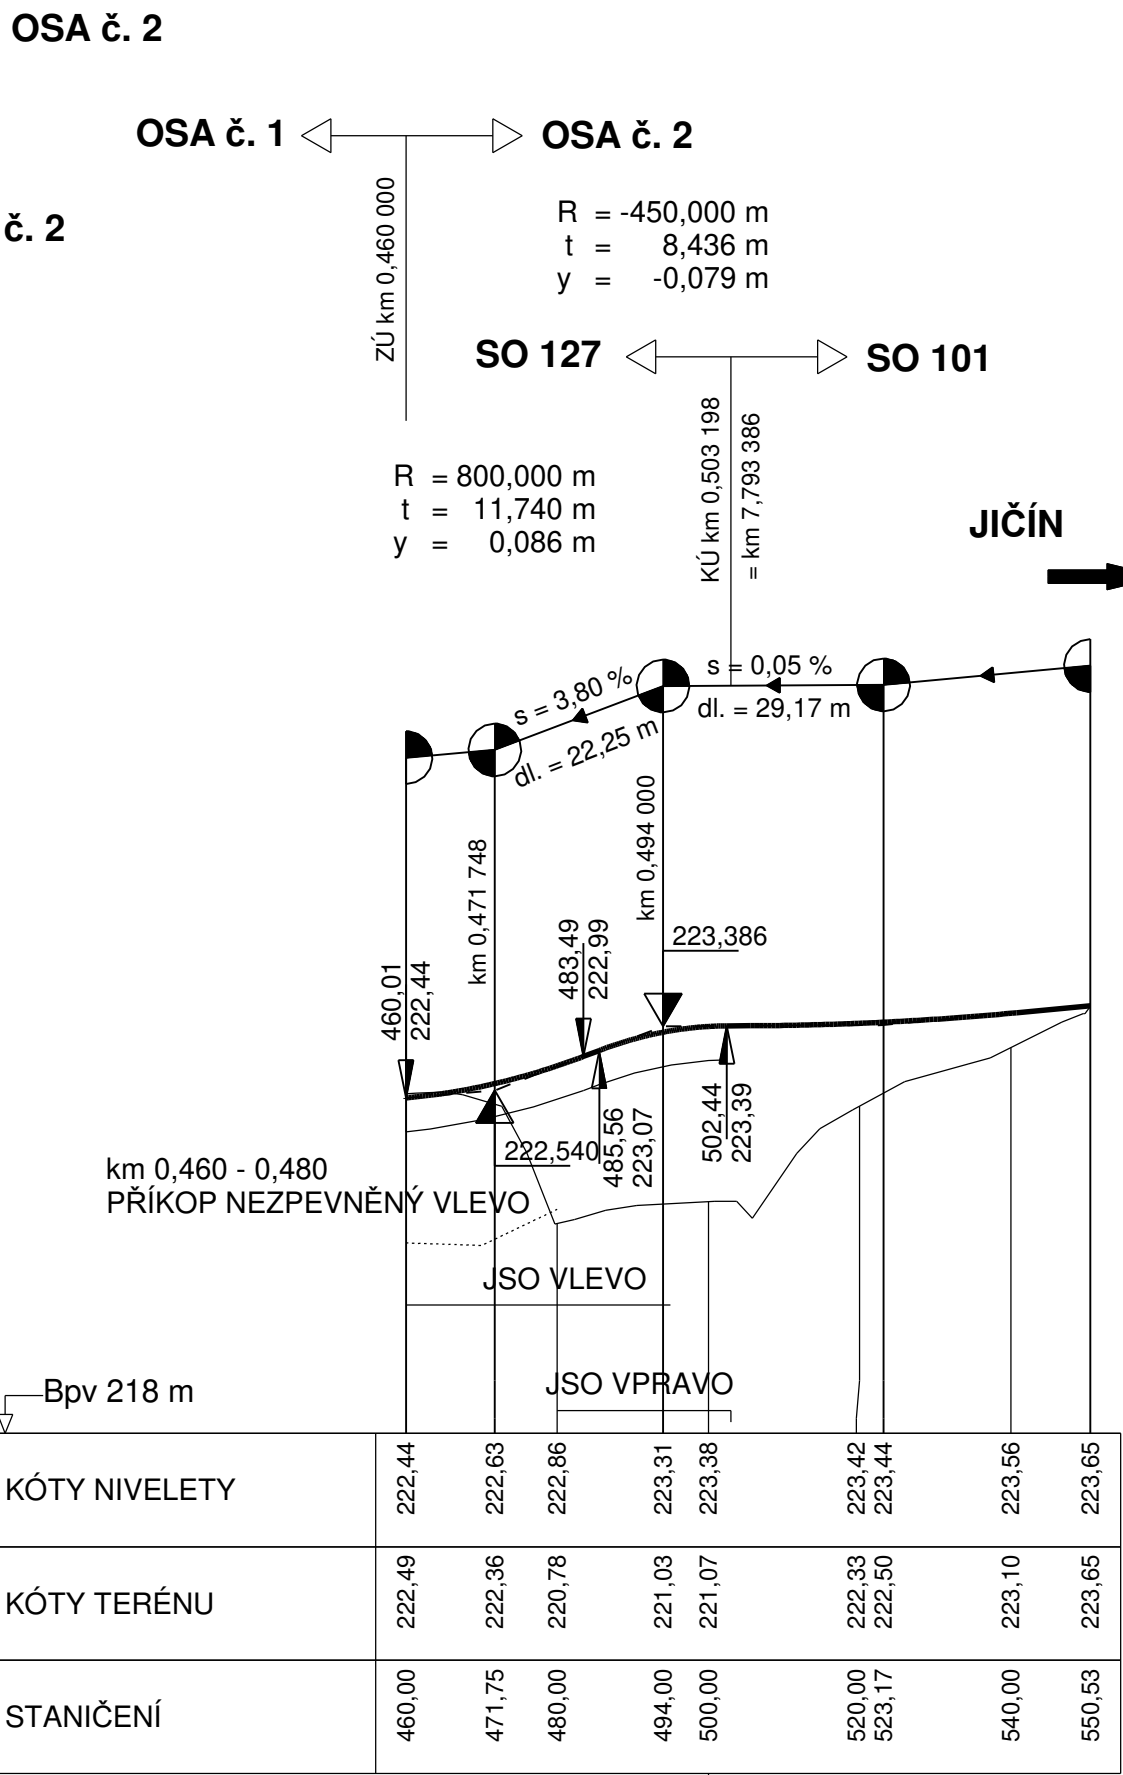
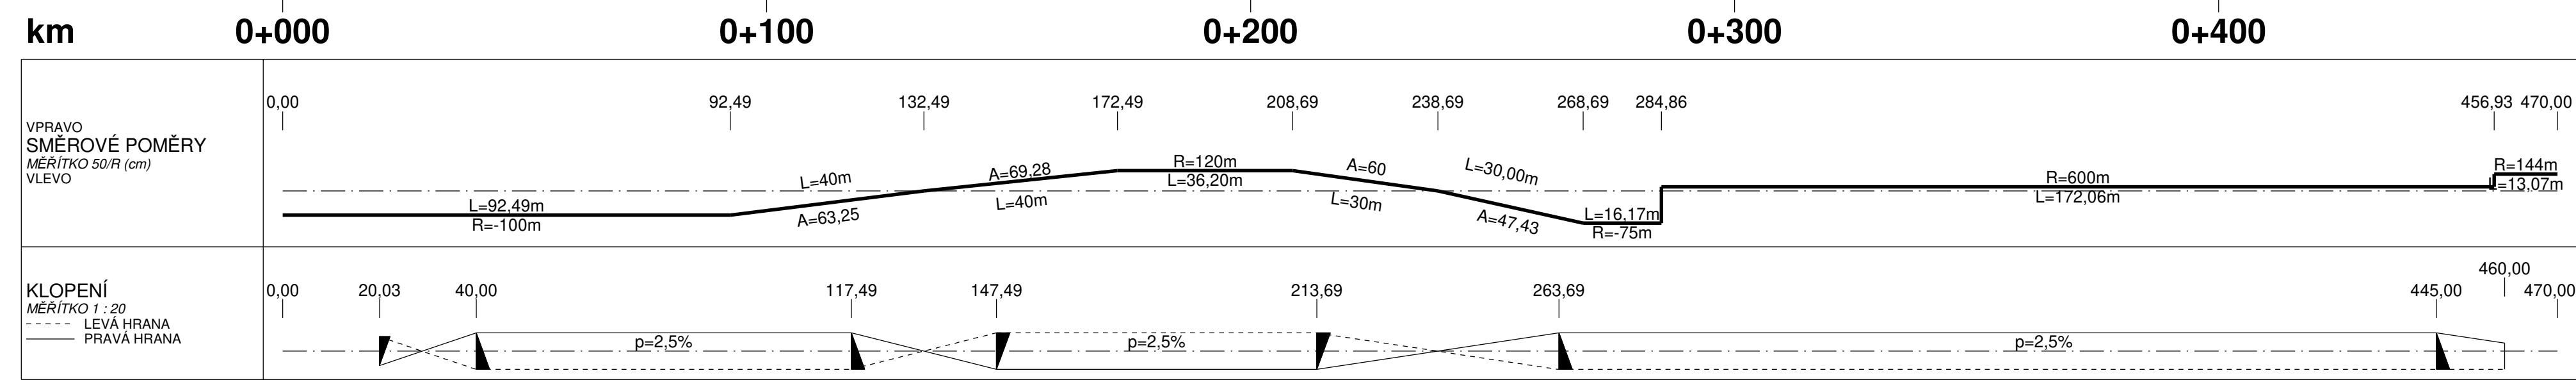


SO 127 - NAPOJENÍ ČSPH NA SILNICI I/16
PODÉLNÉ PROFILY M 1 : 1 000 / 100

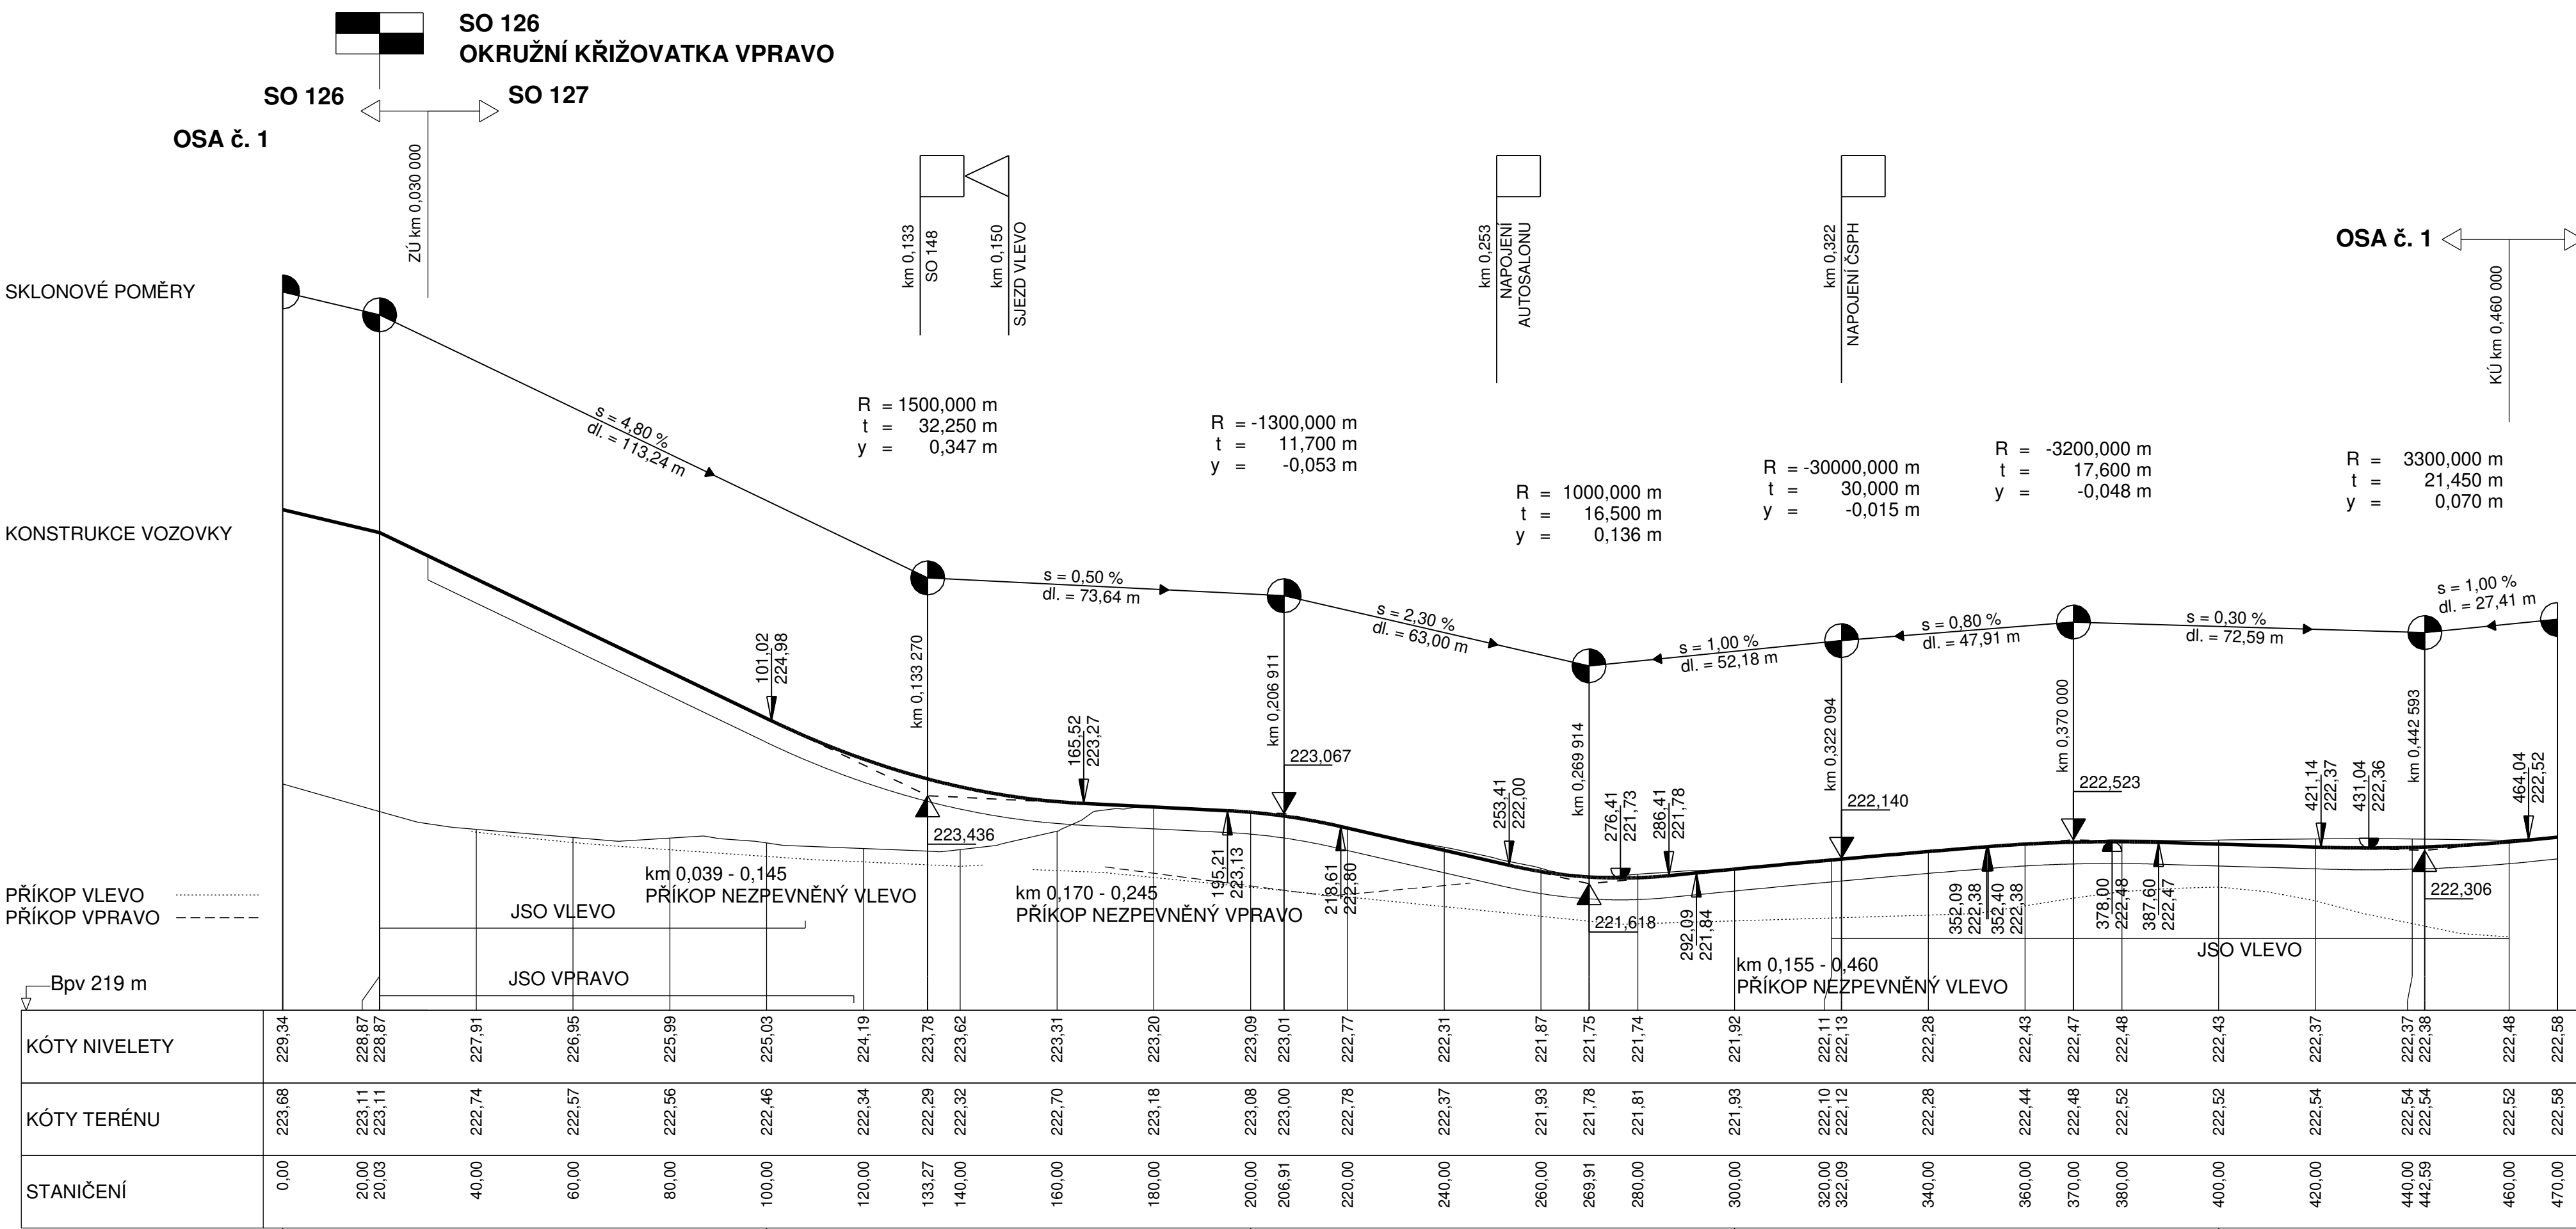

Výškový systém Bpv

SO 127	Napojení ČSPH na silnici I/16
---------------	-------------------------------

Objednatel:



**ŘEDITELSTVÍ
SILNIC
A DÁLNIC**

Ředitelství silnic a dálnic s. p.
Čerčanská 2023/12, Krč, 140 00 Praha 4

Zhotovitel:	Valbek, spol. s r.o. Vaňurova 505/17 460 07 Liberec 3	HIP:
		ING. T. KLIMENT

	Vypracoval	M. KOŘÍNEK		Zak. číslo	21-L113-001
	Zodp. projektant	ING. T. KLIMENT		Datum	02/2025
	Tech. kontrola	ING. M. HANŽL		Stupeň	PDPS
	Akce I/16 MLADÁ BOLESLAV - MARTINOVICE			Počet formátů 10x44	Měřítko 1 : 1000/100
Zhotovitel: Valbek, spol. s r.o. Vahurova 505/17 460 07 Liberec 3	Příloha PODÉLNÉ PROFILY			Č. přílohy 3	Paré