


SO 127 - NAPOJENÍ ČSPH NA SILNICI I/16
VZOROVÉ PŘÍČNÉ ŘEZY, M 1 : 50



SO 127 Napojení ČSPH na silnici I/16

Objednatel:

Ředitelství silnic a dálnic

Ředitelství silnic a dálnic s. p.
Čerčanská 2023/12, Krč, 140 00 Praha 4

Zhotovitel:

Valbek, spol. s r.o.
Vaňurova 505/17
460 07 Liberec 3

HIP:

ING. T. KLIMENT

	Vypracoval	M. KOŘINEK	Zak. číslo	21-L113-001
	Zodp. projektant	ING. T. KLIMENT	Datum	02/2025
	Tech. kontrola	ING. M. HANŽL	Stupeň	PDPS
	Akce	I/16 MLADÁ BOLESLAV - MARTINOVICE		
	Příloha		Počet formátů	7 x A4
			Měřítko	1 : 50
			Č. přílohy	Paré
Zhotovitel:		4		
Valbek, spol. s r.o.				
Vaňurova 505/17				
460 07 Liberec 3				