SO 127 - NAPOJENÍ ČSPH NA SILNICI I/16
PŘÍČNÉ ŘEZY km 0,040 - 0,200, M 1 : 100

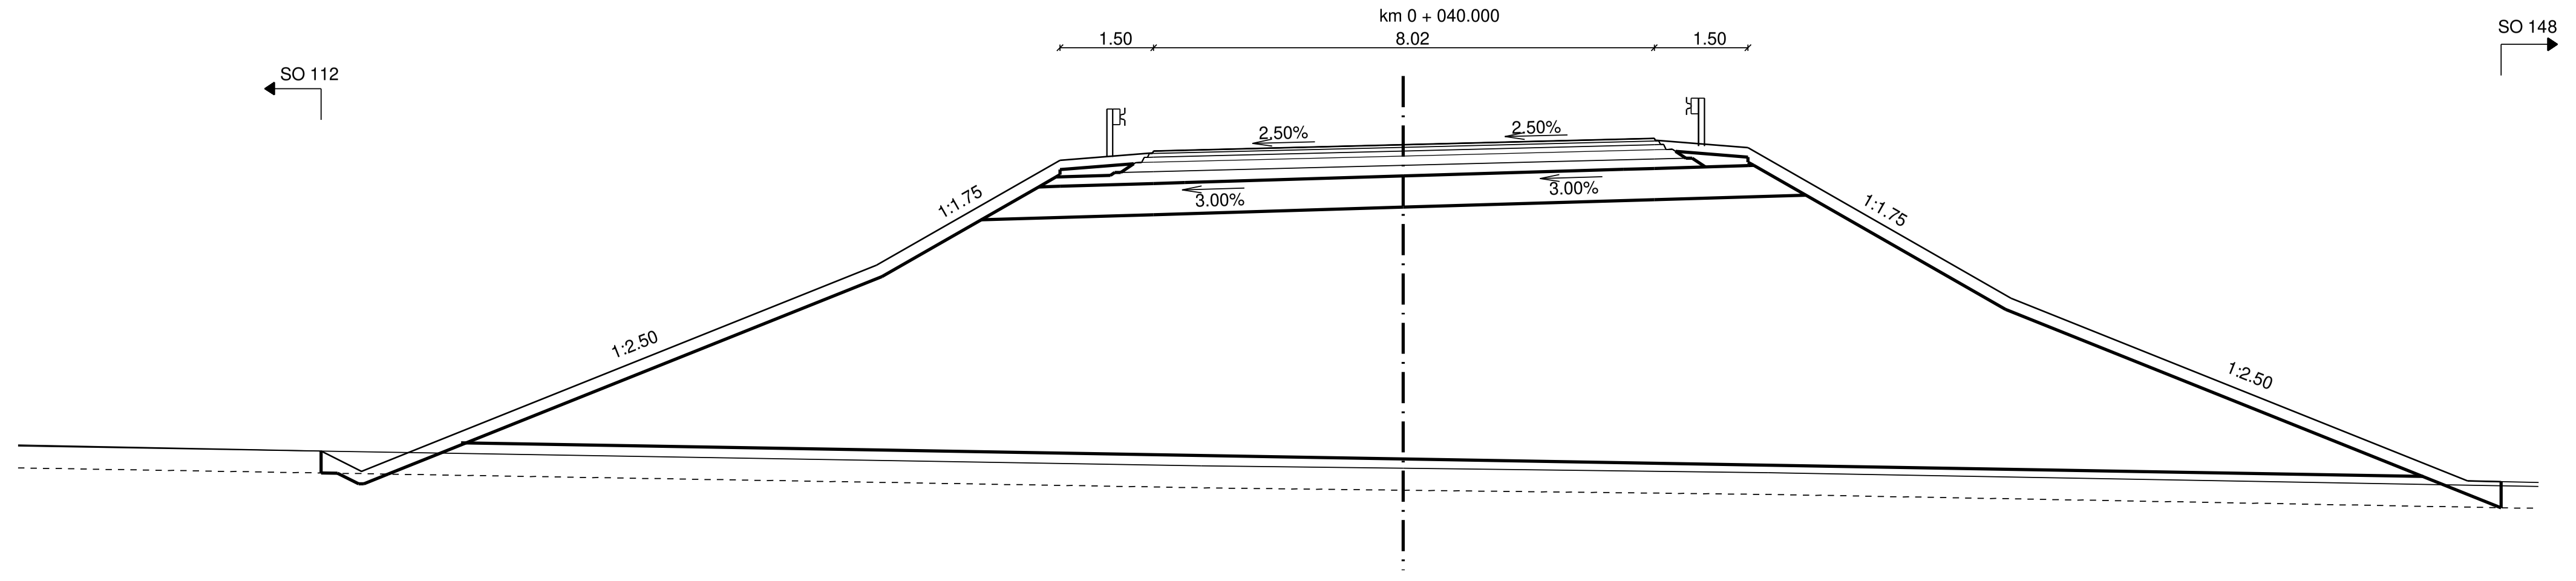
km 0 + 040.000
1.50
8.02
1.50
SO 112
SO 148
2.50%
2.50%
3.00%
3.00%
1:1.75
1:1.75
1:2.50
1:2.50

S. R. 220 m

ODSAZENÍ OD OSY	PROJEKTOVANÝ STAV
-16.69	222.68
-15.94	222.98
-8.44	225.98
-5.50	227.66
-4.02	227.78
-4.00	227.81
-3.50	227.83
0.00	227.91
3.52	228.00
4.02	228.01
4.04	227.98
5.52	227.86
9.74	225.45
17.05	222.53
17.59	222.45

ODSAZENÍ OD OSY	STÁVAJÍCÍ TERÉN
-3.24	222.77
0.00	222.73
5.85	222.66

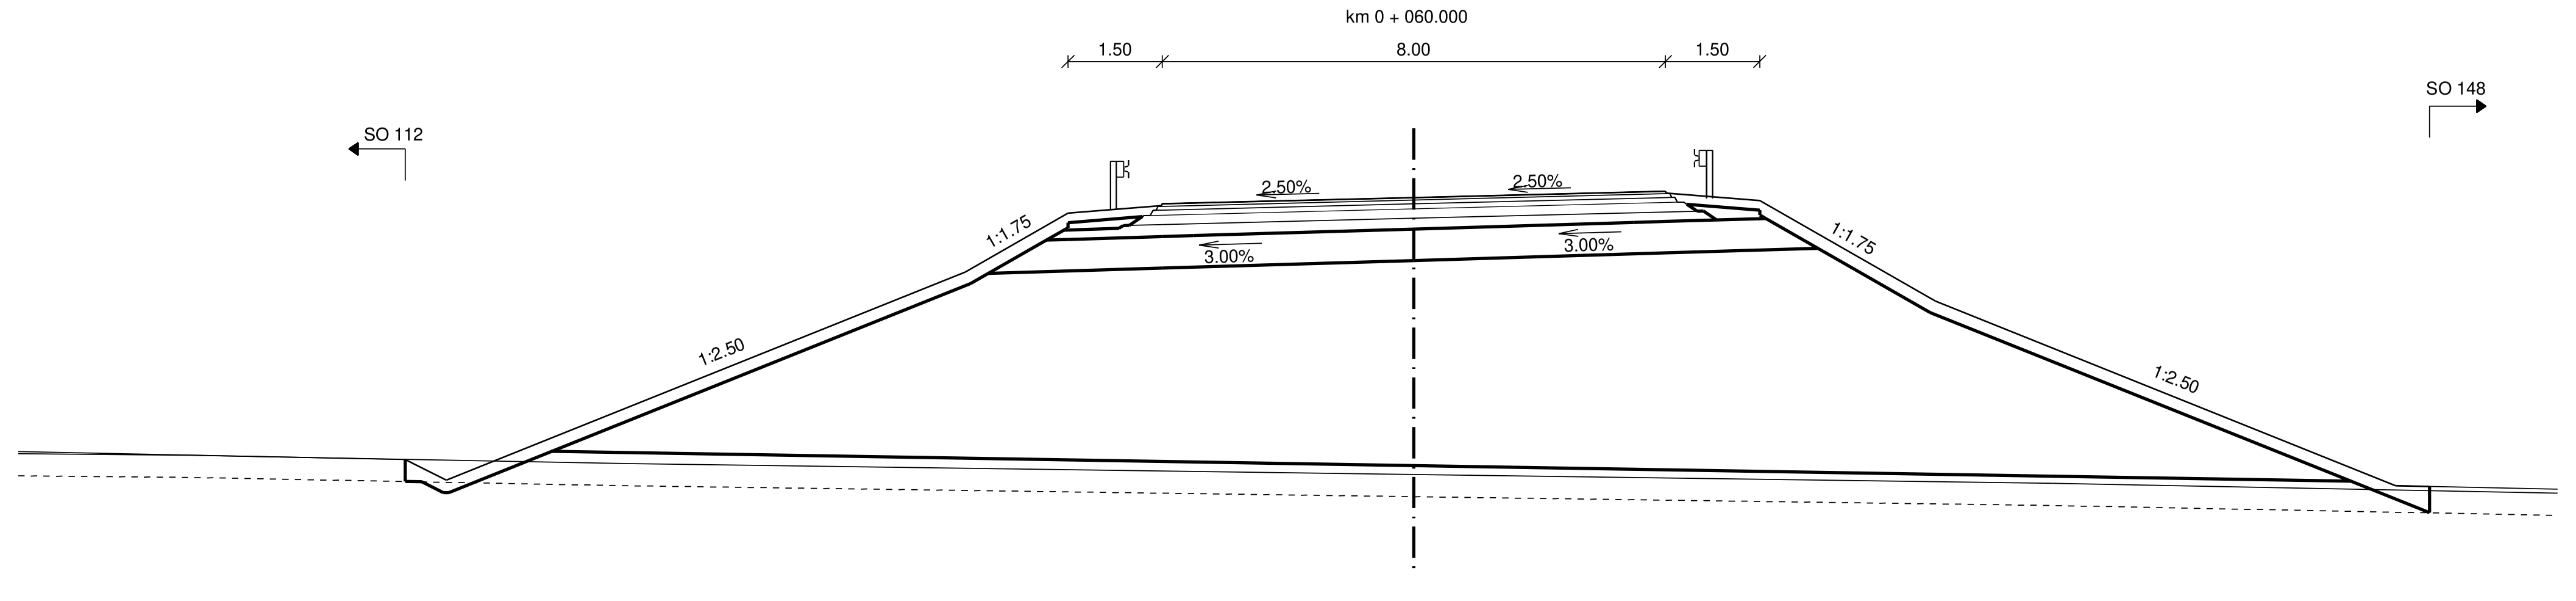
km 0 + 060.000
1.50
8.00
1.50
SO 112
SO 148
2.50%
2.50%
3.00%
3.00%
1:1.75
1:1.75
1:2.50
1:2.50

S. R. 219 m

ODSAZENÍ OD OSY	PROJEKTOVANÝ STAV
-16.04	222.80
-15.39	222.47
-14.64	222.77
-7.14	225.77
-5.50	226.70
-4.02	226.82
-4.00	226.85
-3.50	226.87
0.00	226.95
3.50	227.04
4.00	227.05
4.02	227.02
5.50	226.90
8.30	225.31
15.61	222.38
16.15	222.30

ODSAZENÍ OD OSY	STÁVAJÍCÍ TERÉN
-12.52	222.73
0.00	222.56
10.16	222.42

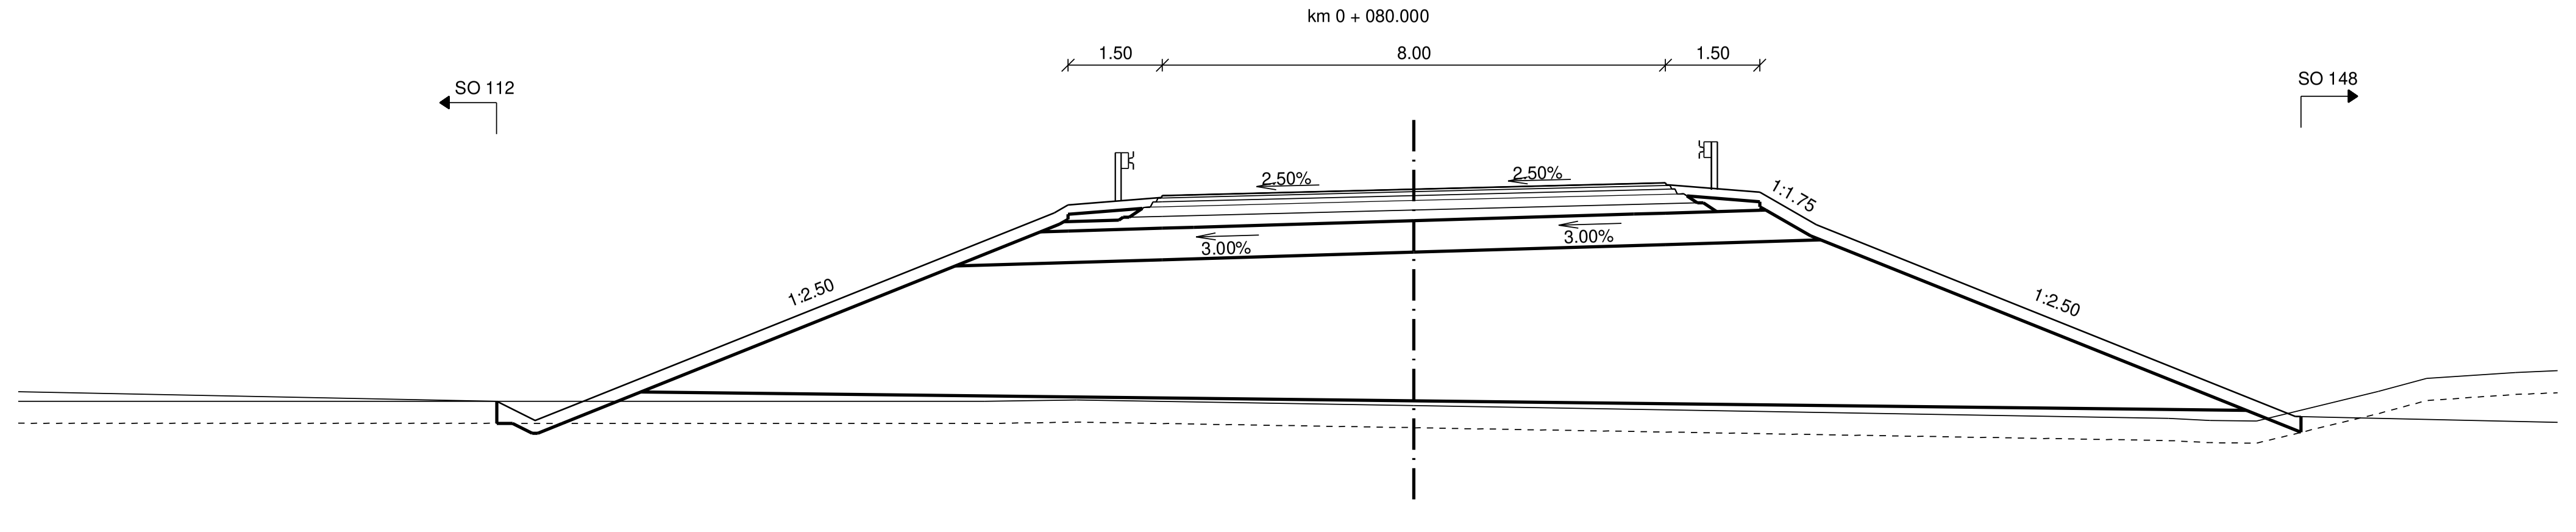
km 0 + 080.000
1.50
8.00
1.50
SO 112
SO 148
2.50%
2.50%
3.00%
3.00%
1:1.75
1:2.50
1:2.50

S. R. 219 m

ODSAZENÍ OD OSY	PROJEKTOVANÝ STAV
-14.59	222.62
-13.97	222.32
-13.21	222.62
-5.72	225.62
-5.50	225.74
-4.02	225.86
-4.00	225.89
-3.50	225.91
0.00	225.99
3.50	226.08
4.00	226.09
4.02	226.06
5.50	225.94
6.40	225.43
13.90	222.43
14.11	222.48

ODSAZENÍ OD OSY	STÁVAJÍCÍ TERÉN
-6.82	222.62
-5.36	222.64
0.00	222.55
12.00	222.35
12.66	222.32
13.40	222.31
15.33	222.78
16.11	222.99
17.52	223.08

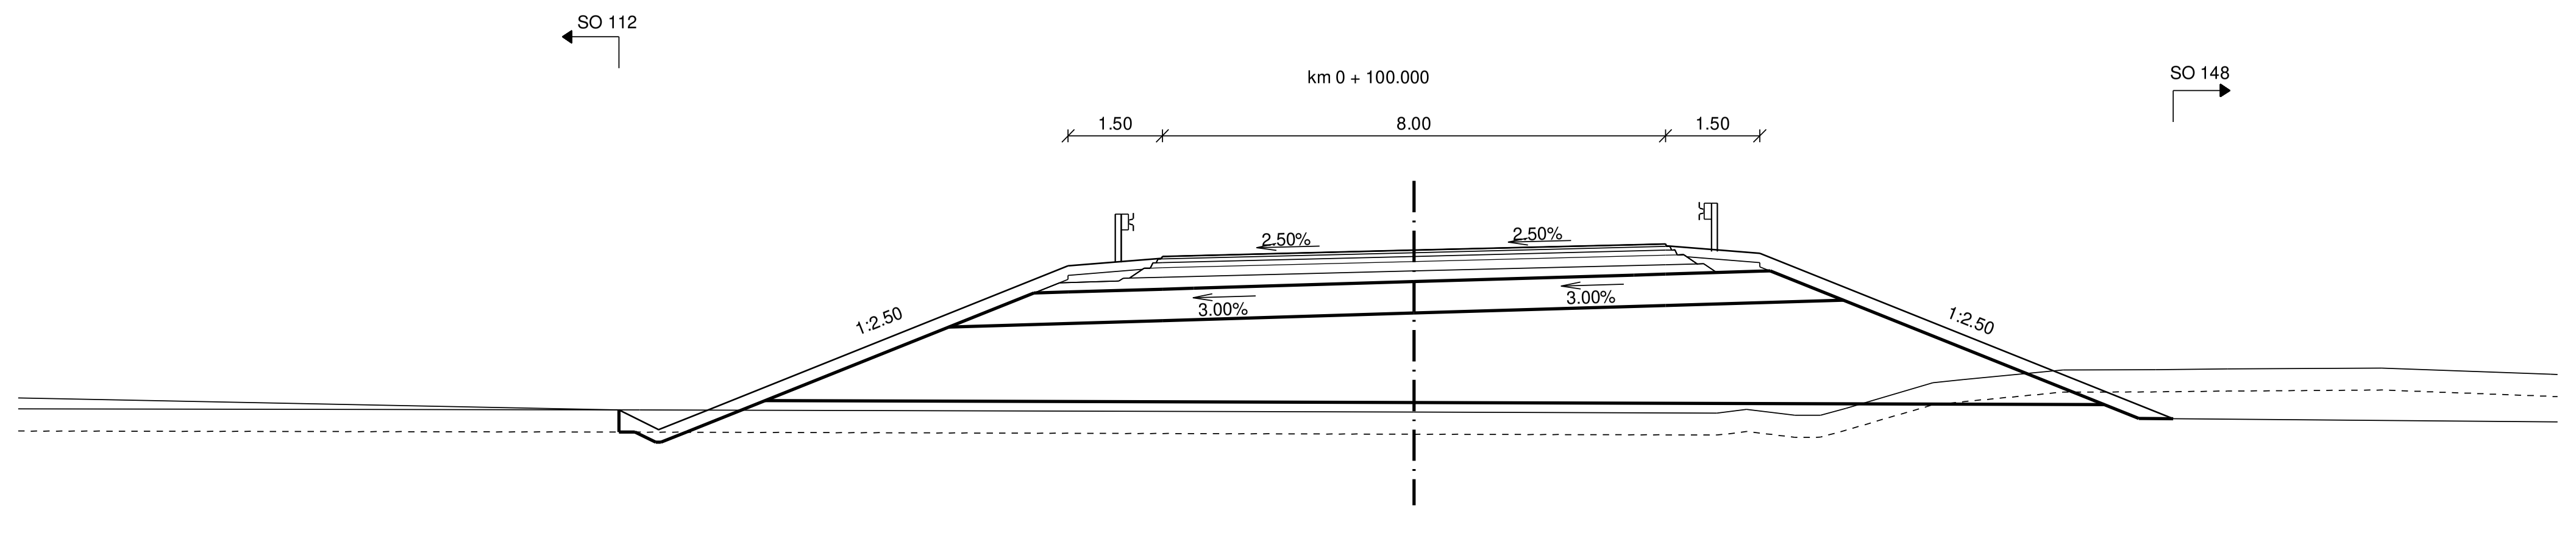
km 0 + 100.000
1.50
8.00
1.50
SO 112
SO 148
2.50%
2.50%
3.00%
3.00%
1:2.50
1:2.50

S. R. 219 m

ODSAZENÍ OD OSY	PROJEKTOVANÝ STAV
-12.64	222.49
-12.01	222.18
-11.23	222.49
-5.50	224.78
-4.02	224.90
-4.00	224.93
-3.50	224.95
0.00	225.03
3.50	225.12
4.00	225.13
4.02	225.10
5.50	224.98
10.18	223.11
12.07	222.35

ODSAZENÍ OD OSY	STÁVAJÍCÍ TERÉN
-12.31	222.49
0.00	222.46
4.82	222.44
5.29	222.50
6.06	222.41
6.47	222.41
6.87	222.52
8.25	222.92
8.74	222.98
10.32	223.13
11.80	223.13
12.94	223.15
15.39	223.16

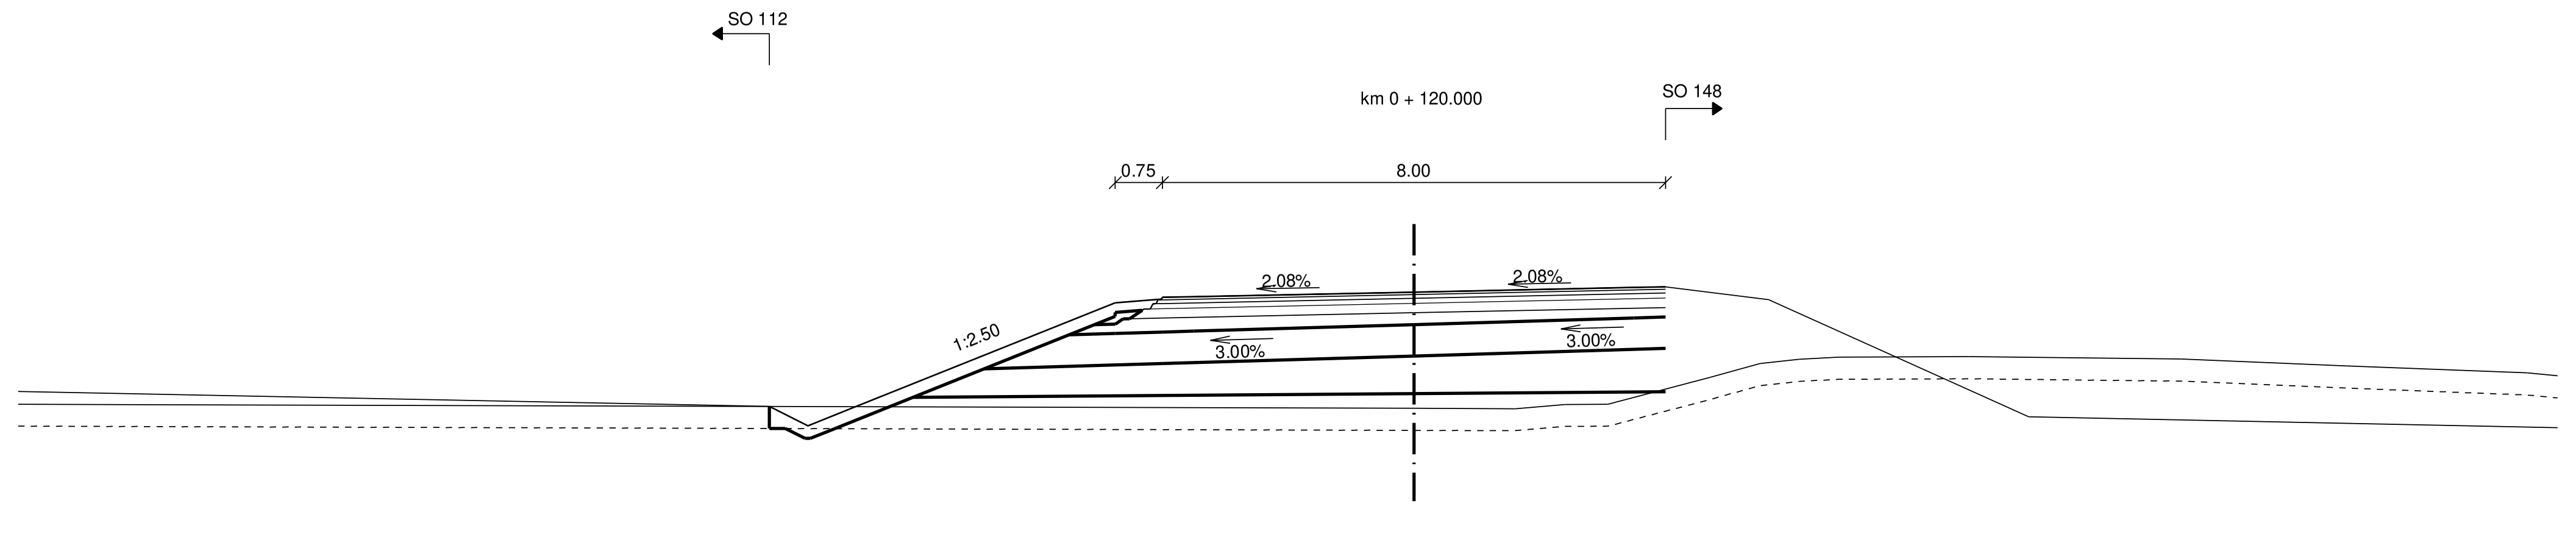
km 0 + 120.000
0.75
8.00
SO 112
SO 148
2.08%
2.08%
3.00%
3.00%
1:2.50

S. R. 219 m

ODSAZENÍ OD OSY	PROJEKTOVANÝ STAV
-10.25	222.37
-9.64	222.07
-9.63	222.07
-8.88	222.37
-4.75	224.02
-4.02	224.08
-4.00	224.11
-3.50	224.12
0.00	224.19
3.50	224.27
4.00	224.28

ODSAZENÍ OD OSY	STÁVAJÍCÍ TERÉN
0.00	222.34
1.61	222.34
2.40	222.41
3.08	222.41
4.71	222.84
5.51	223.05
6.13	223.12
6.76	223.16
8.83	223.17
12.21	223.13
14.83	223.02
17.71	222.91

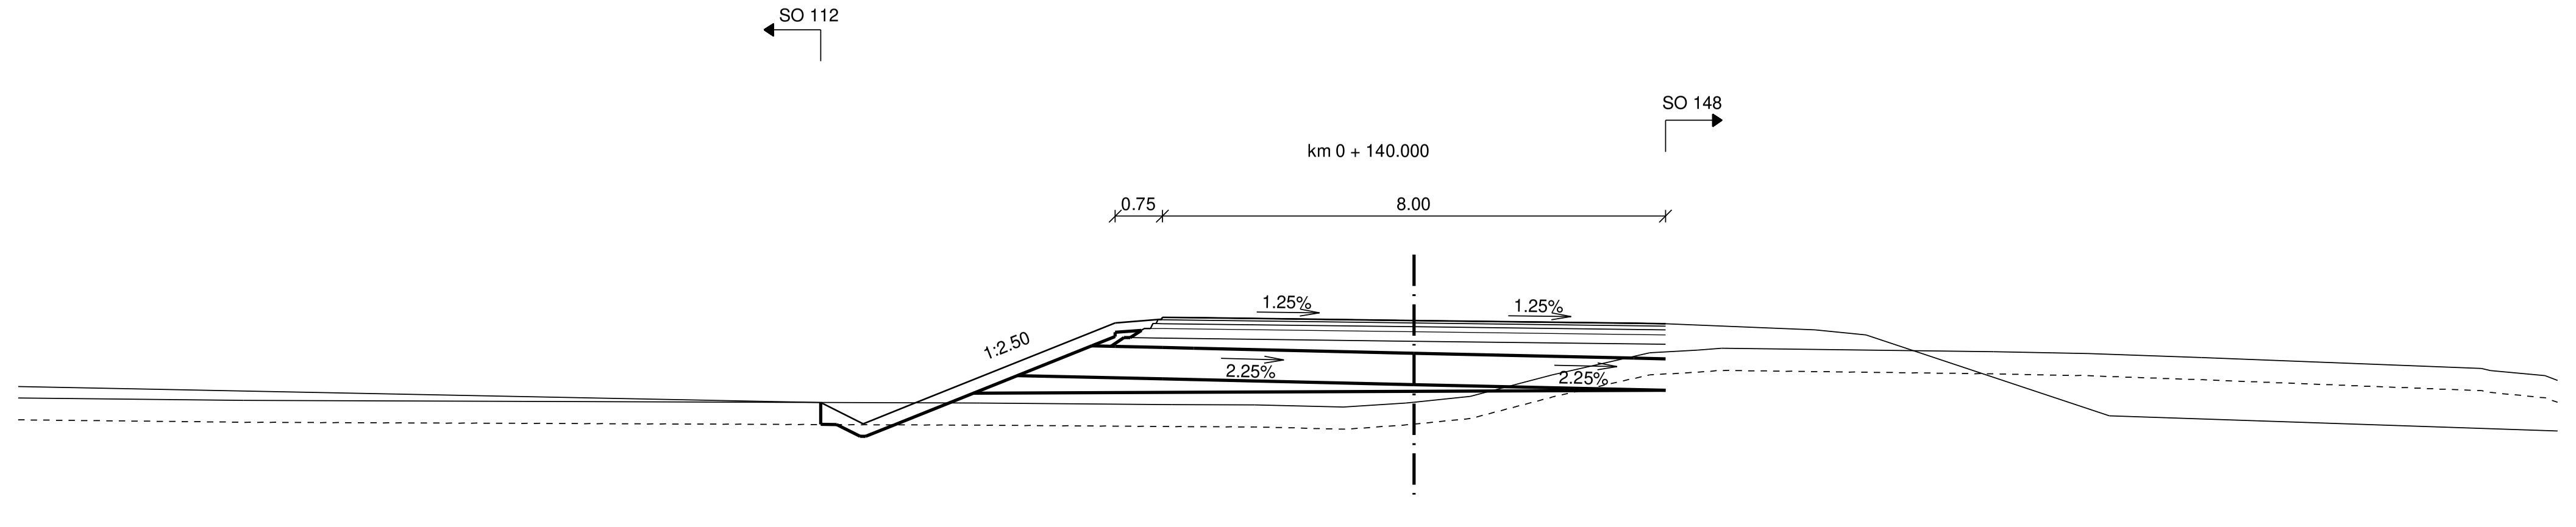
km 0 + 140.000
0.75
8.00
SO 112
SO 148
1.25%
1.25%
2.25%
2.25%
1:2.50

S. R. 219 m

ODSAZENÍ OD OSY	PROJEKTOVANÝ STAV
-9.43	222.31
-8.76	221.98
-7.93	222.31
-4.75	223.58
-4.02	223.64
-4.00	223.67
-3.50	223.66
0.00	223.62
3.50	223.58
4.00	223.57
4.02	223.54
4.75	223.48
5.53	223.17
5.88	223.16

ODSAZENÍ OD OSY	STÁVAJÍCÍ TERÉN
-6.91	222.31
-3.85	222.28
-2.53	222.28
-1.12	222.24
-0.13	222.31
0.00	222.32
0.89	222.41
2.20	222.75
3.75	223.10
4.51	223.15
4.90	223.18
9.21	223.12
10.72	223.09
12.52	223.03
16.97	222.86
17.12	222.82
17.99	222.74

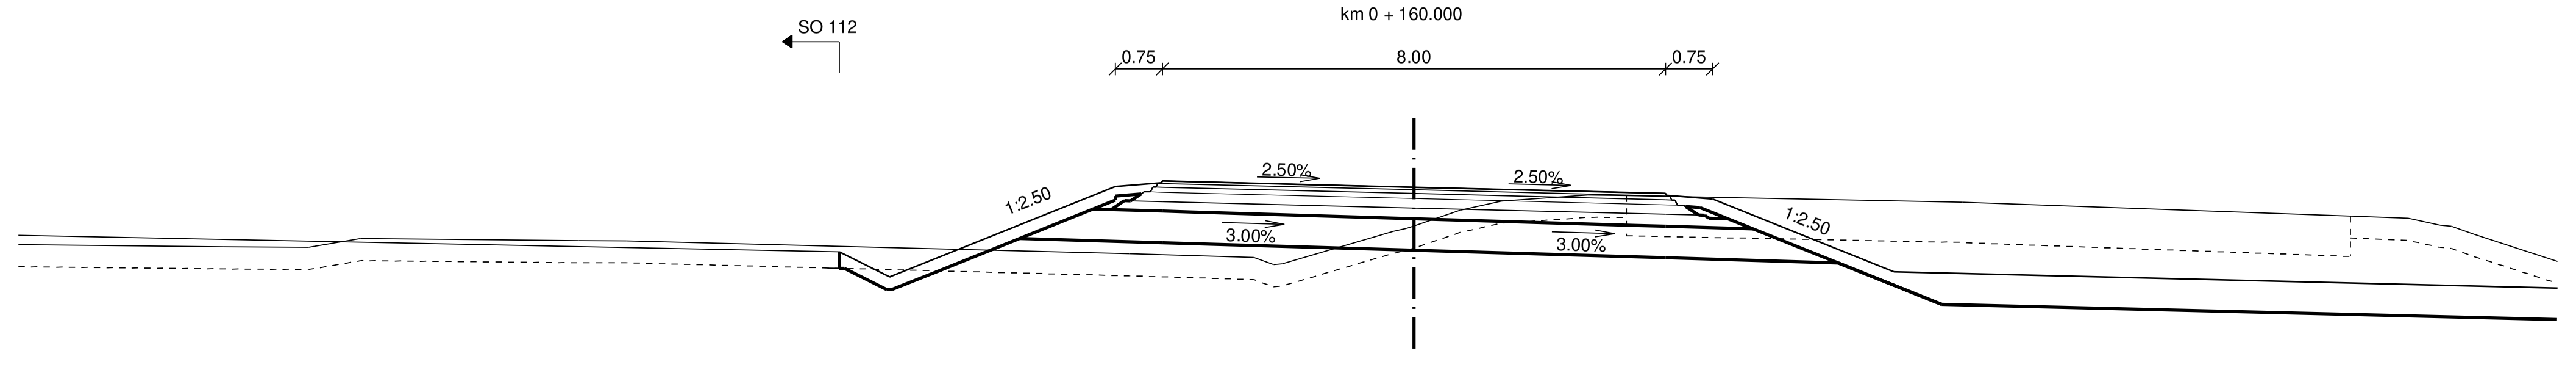
km 0 + 160.000
0.75
8.00
0.75
SO 112
2.50%
2.50%
3.00%
3.00%
1:2.50
1:2.50

S. R. 219 m

ODSAZENÍ OD OSY	PROJEKTOVANÝ STAV
-9.14	222.29
-8.34	221.89
-7.24	222.33
-4.75	223.32
-4.02	223.38
-4.00	223.41
-3.50	223.40
0.00	223.31
3.50	223.22
4.00	223.21
4.02	223.18
4.75	223.12
7.63	221.97

ODSAZENÍ OD OSY	STÁVAJÍCÍ TERÉN
-16.75	222.50
-13.28	222.46
-12.52	222.46
-4.53	222.26
-2.55	222.20
-2.23	222.08
-2.09	222.09
-0.33	222.61
-0.12	222.66
0.00	222.70
0.73	222.94
1.39	223.09
1.49	223.10
2.77	223.19
3.38	223.18
8.72	223.07
14.89	222.85
15.81	222.82
16.32	222.71
16.50	222.69
16.85	222.56

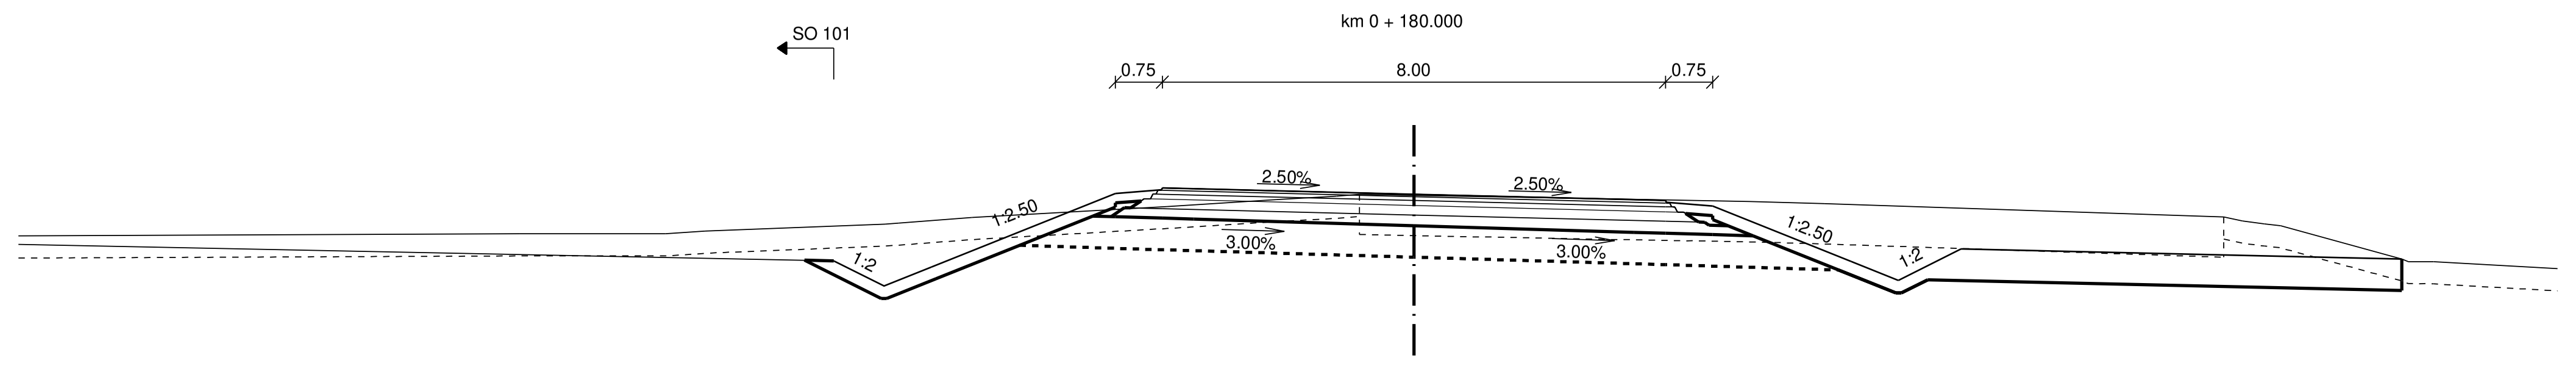
km 0 + 180.000
0.75
8.00
0.75
SO 101
2.50%
2.50%
3.00%
3.00%
1:2
1:2
1:2.50
1:2.50

S. R. 219 m

ODSAZENÍ OD OSY	PROJEKTOVANÝ STAV
-9.22	222.14
-8.42	221.74
-7.67	222.04
-4.75	223.21
-4.02	223.27
-4.00	223.30
-3.50	223.29
0.00	223.20
3.50	223.11
4.00	223.10
4.02	223.07
4.75	223.01
6.95	222.13
7.70	221.83
8.70	222.33
15.71	222.17

ODSAZENÍ OD OSY	STÁVAJÍCÍ TERÉN
-14.22	222.57
-11.90	222.57
-11.27	222.62
-8.41	222.73
-8.19	222.74
-7.03	222.83
-3.92	223.01
-2.20	223.12
-1.23	223.17
-0.87	223.20
0.00	223.18
2.87	223.13
5.33	223.09
6.53	223.05
12.88	222.84
13.18	222.78
13.52	222.73
13.78	222.70
15.71	222.17
15.82	222.13
16.22	222.13

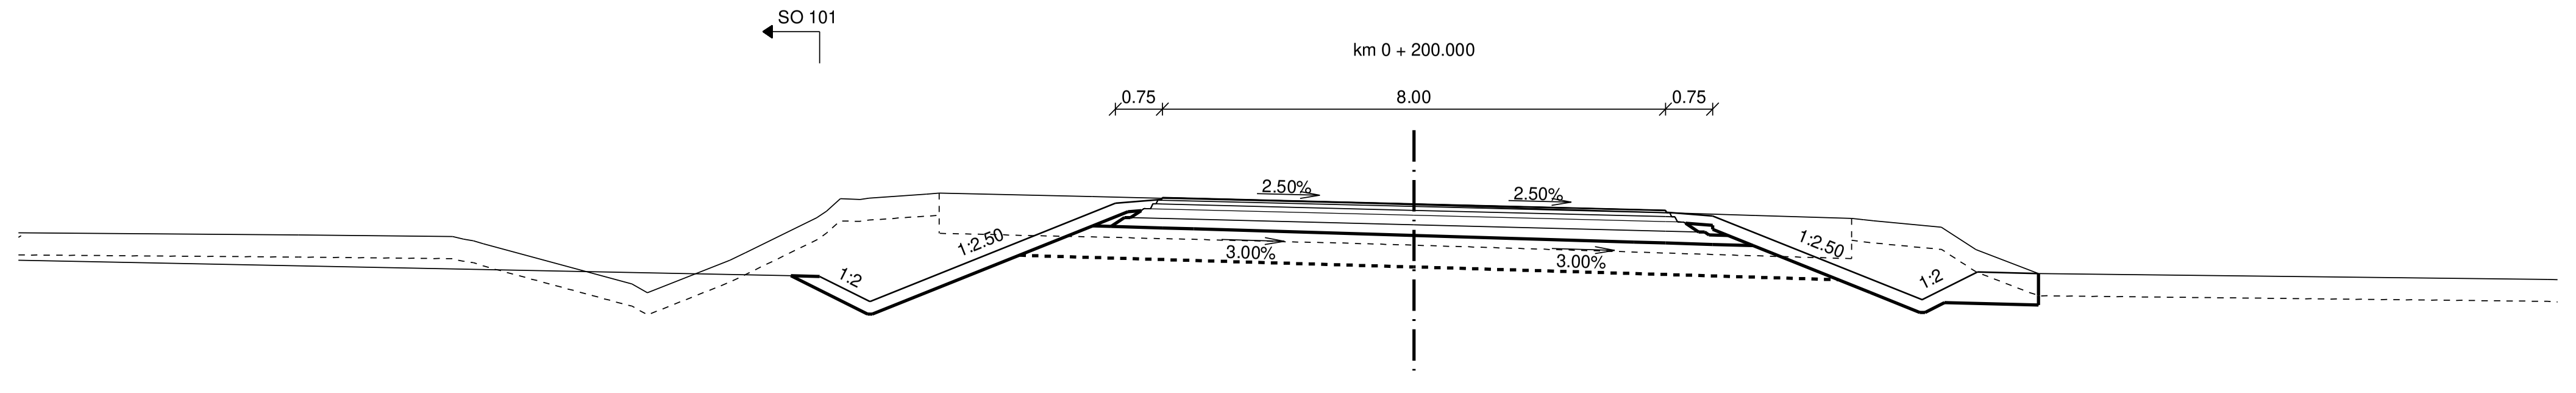
km 0 + 200.000
0.75
8.00
0.75
SO 101
2.50%
2.50%
3.00%
3.00%
1:2
1:2
1:2.50
1:2.50

S. R. 219 m

ODSAZENÍ OD OSY	PROJEKTOVANÝ STAV
-9.45	221.94
-8.65	221.54
-4.75	223.10
-4.02	223.16
-4.00	223.19
-3.50	223.18
0.00	223.09
3.50	223.01
4.00	222.99
4.02	222.96
4.75	222.90
8.08	221.57
8.96	222.01
9.93	221.99

ODSAZENÍ OD OSY	STÁVAJÍCÍ TERÉN
-15.29	222.58
-15.11	222.53
-14.96	222.51
-14.80	222.46
-12.44	221.82
-12.19	221.68
-10.88	222.20
-10.63	222.32
-9.49	222.88
-9.34	222.98
-9.12	223.18
-8.81	223.17
-8.66	223.19
-7.75	223.25
-7.55	223.27
-5.12	223.21
-1.00	223.11
0.00	223.08
5.42	222.91
6.96	222.87
7.15	222.84
7.31	222.82
8.39	222.72
8.94	222.37
9.93	221.99

Výškový systém Bpv

SO 127 Napojení ČSPH na silnici I/16

Objednatel:
ŘEDITELSTVÍ SILNIC A DÁLNIC
Ředitelství silnic a dálnic s. p.
Čerčanská 2023/12, Krč, 140 00 Praha 4

Zhotovitel:
Valbek
Valbek, spol. s r.o.
Vaňurova 505/17
460 07 Liberec 3

HIP:
ING. T. KLIMENT

Vypracoval	M. KOŘÍNEK		**Zak. číslo**	21-LI13-001
Zodp. projektant	ING. T. KLIMENT		**Datum**	02/2025
Tech. kontrola	ING. M. HANŽL		**Stupeň**	PDPS
Akce	I/16 MLADÁ BOLESLAV - MARTINOVICE		**Počet formátů**	14xA4
			Měřítko	1 : 100
Příloha	PŘÍČNÉ ŘEZY km 0,040 - 0,200		**Č. přílohy**	**Paré**
			5.1	

Zhotovitel:
Valbek
Valbek, spol. s r.o.
Vaňurova 505/17
460 07 Liberec 3