




**SŮ 127 - NÁPOJENÍ ČSPH NA SILNICI I/16
PŘÍČNÉ ŘEZY km 0,220 - 0,380, M 1 : 100**

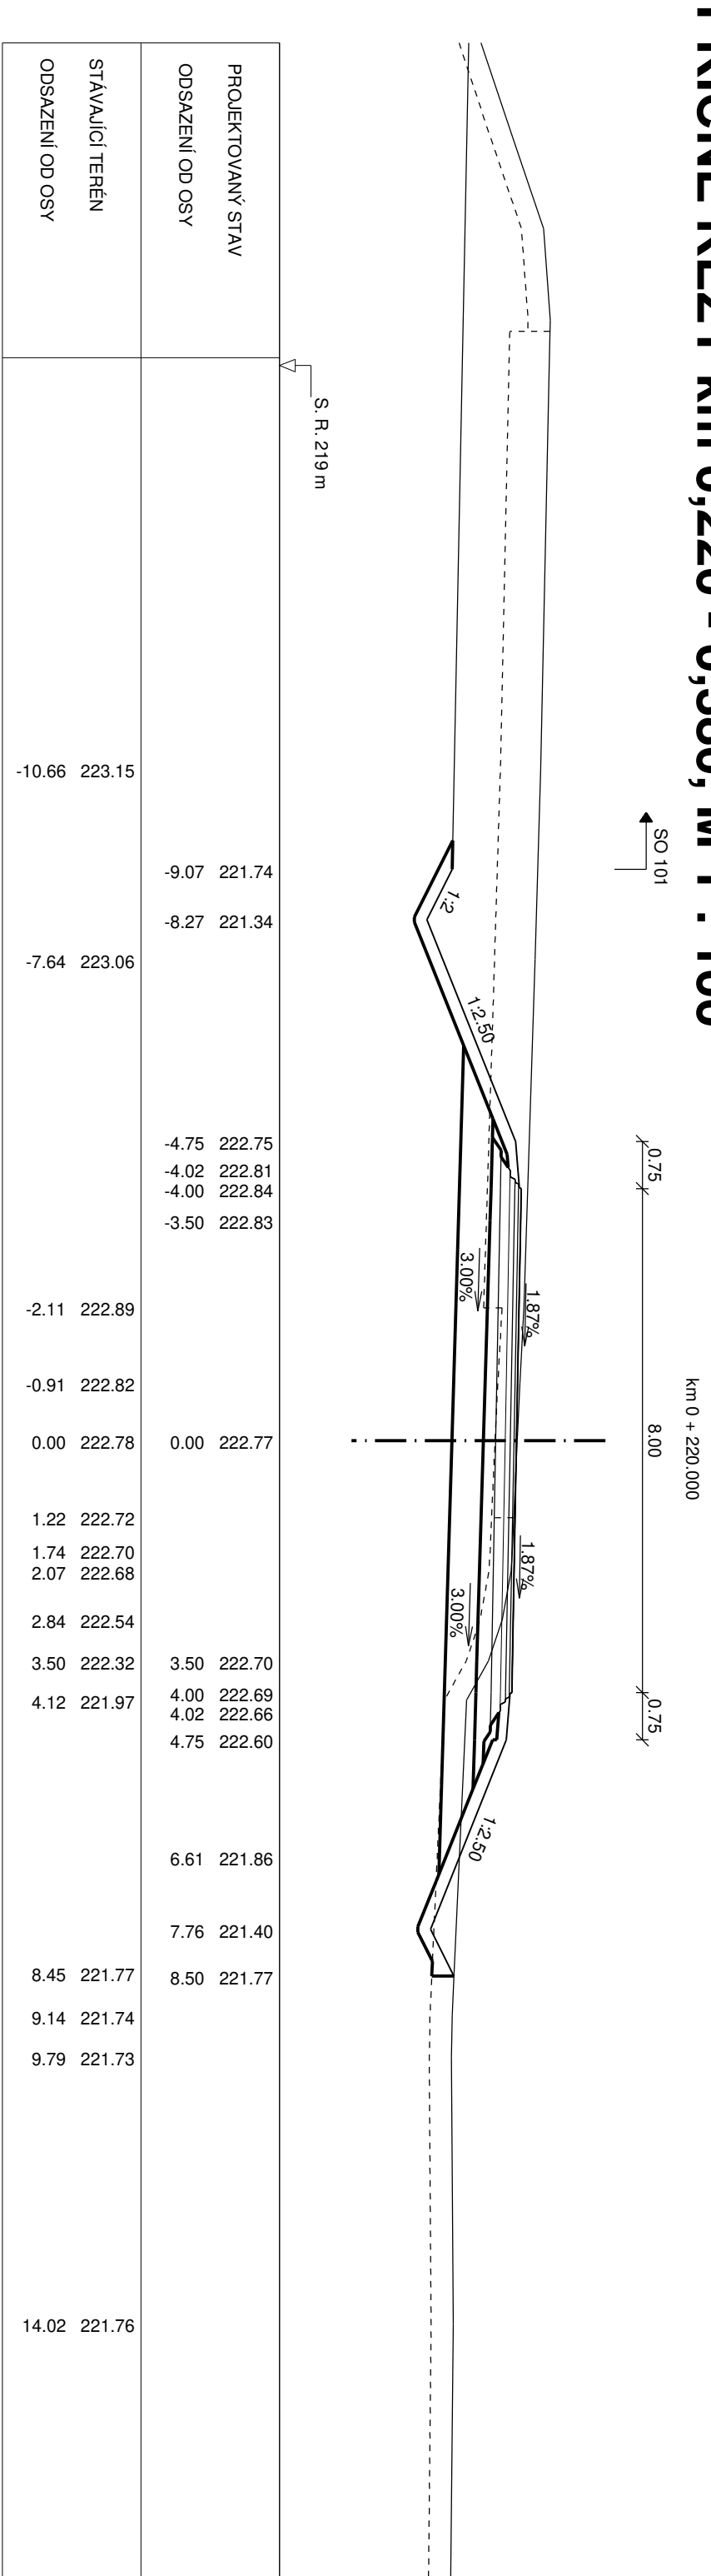


PROJEKTOVANY STAV ODSAZENI OD OSY	STAVAJICI TEREN ODSAZENI OD OSY
-9.07 221.74	-10.66 223.15
-8.27 221.34	-7.64 223.06
-4.75 222.75	-2.11 222.89
-4.02 222.81	-0.91 222.82
-4.00 222.84	0.00 222.78
-3.50 222.83	1.22 222.72
	1.74 222.70
	2.07 222.68
	2.84 222.54
	3.50 222.32
	4.12 221.97
3.50 222.70	
4.00 222.69	
4.02 222.66	
4.75 222.60	
6.61 221.86	
7.76 221.40	
8.50 221.77	8.45 221.77
	9.14 221.74
	9.79 221.73
	14.02 221.76

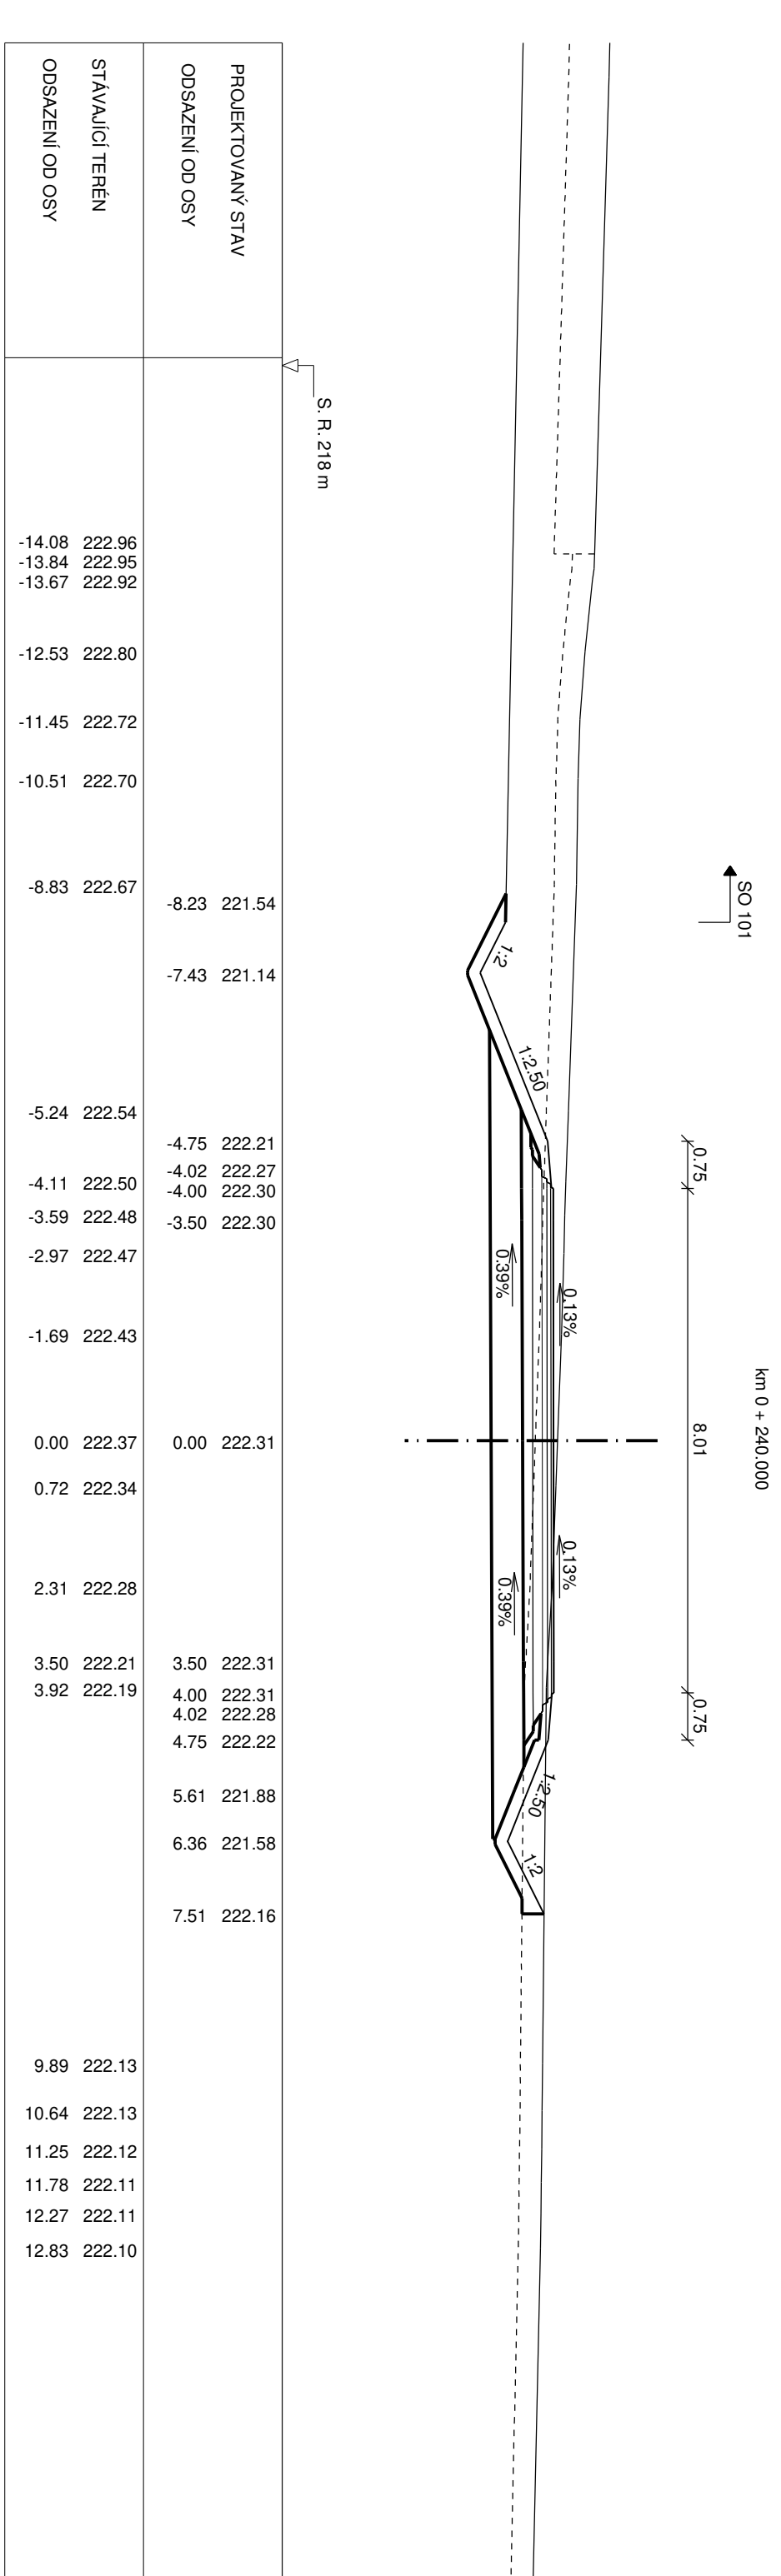


STAVAJUĆI IZREK ODRAŽAVAJUĆI OD OSY	PROJEKTOVANI STAV ODRAŽAVAJUĆI OD OSY
-14.08 222.96 -13.84 222.95 -13.67 222.92	
-12.53 222.80	
-11.45 222.72	
-10.51 222.70	
-8.83 222.67	-8.23 221.54
	-7.43 221.14
-5.24 222.54	-4.75 222.21
-4.11 222.50	-4.02 222.27
-3.59 222.48	-4.00 222.30
-2.97 222.47	-3.50 222.30
-1.69 222.43	4.75 222.22
0.00 222.37	0.00 222.31
0.72 222.34	
2.31 222.28	
3.50 222.21	3.50 222.31
3.92 222.19	4.00 222.31
	4.02 222.28
	4.75 222.22
	5.61 221.88
	6.36 221.58
	7.51 222.16
9.89 222.13	
10.64 222.13	
11.25 222.12	
11.78 222.11	
12.27 222.11	
12.83 222.10	

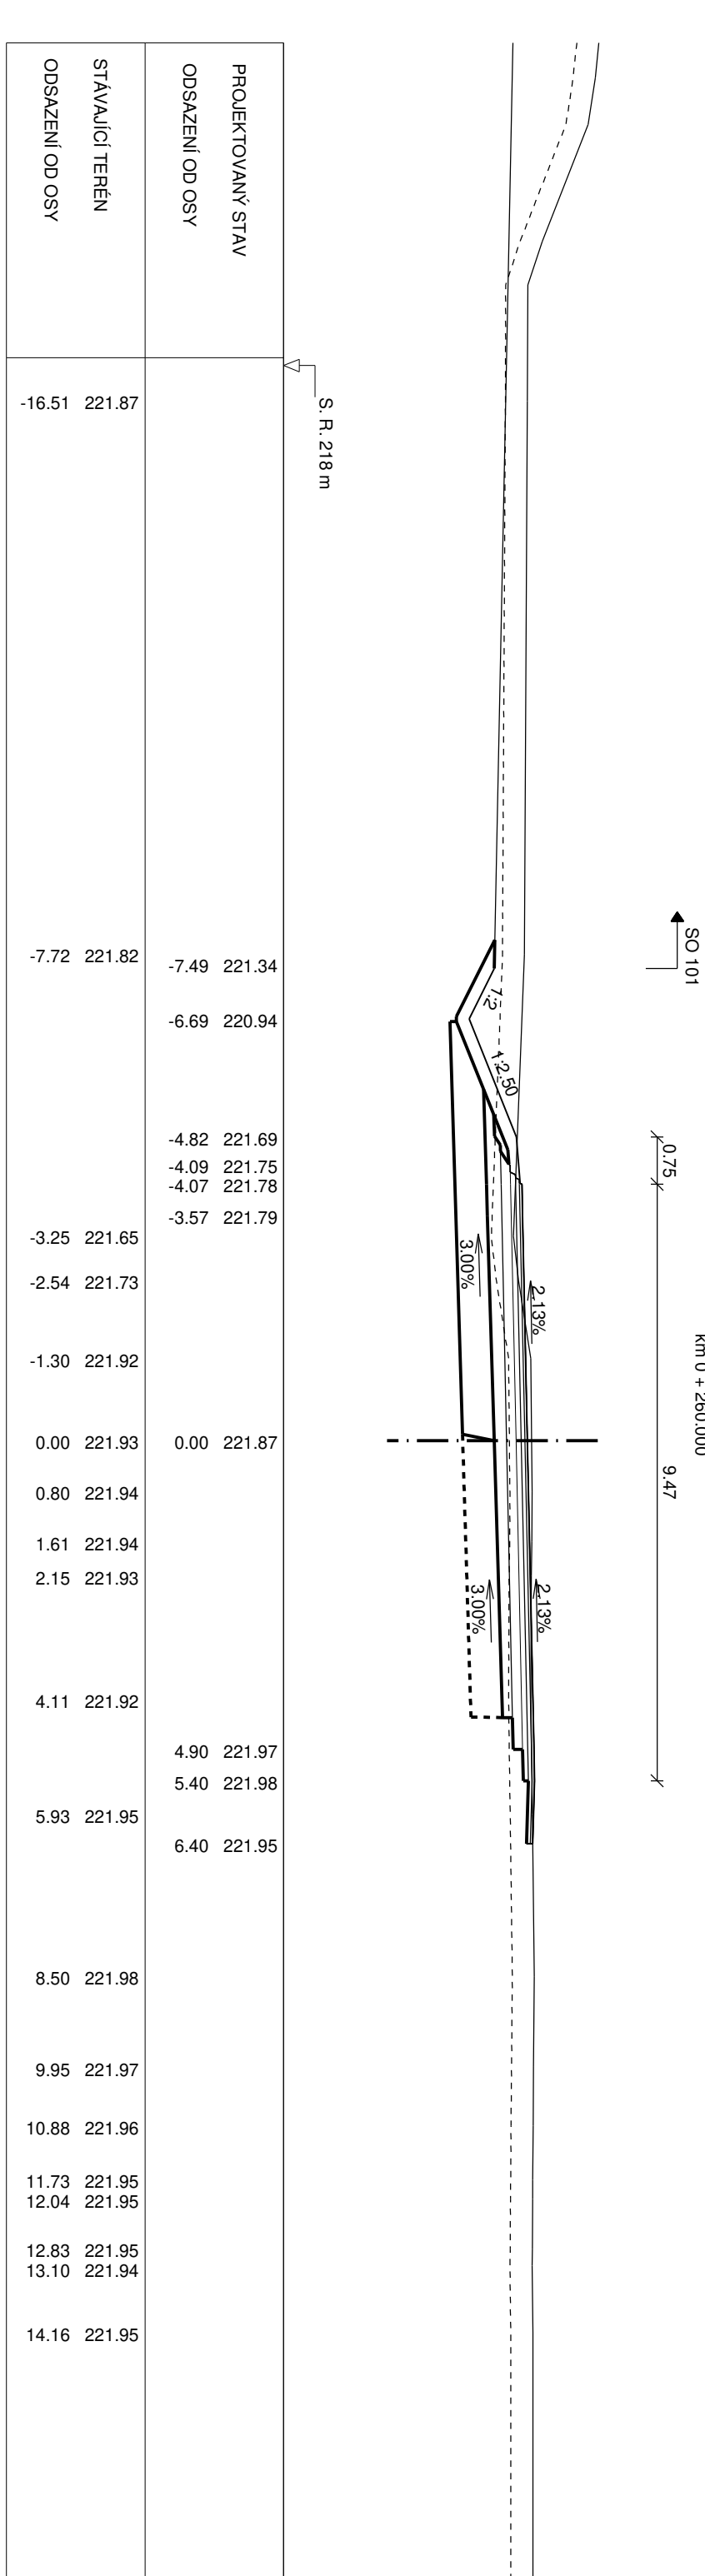



PROJEKTOVANÝ STAV OBSAŽENÍ OD OSY	STÁVAJÍCÍ TERÉN OBSAŽENÍ OD OSY
-16.51 221.87	-7.72 221.82
-7.49 221.34	-6.69 220.94
-4.82 221.69	-4.09 221.75
-4.07 221.78	-3.57 221.79
-3.25 221.65	-2.54 221.73
-1.30 221.92	0.00 221.93
0.80 221.94	1.61 221.94
2.15 221.93	4.11 221.92
4.90 221.97	5.40 221.98
6.40 221.95	8.50 221.98
9.95 221.97	10.88 221.96
11.73 221.95	12.04 221.95
12.83 221.95	13.10 221.94
14.16 221.95	

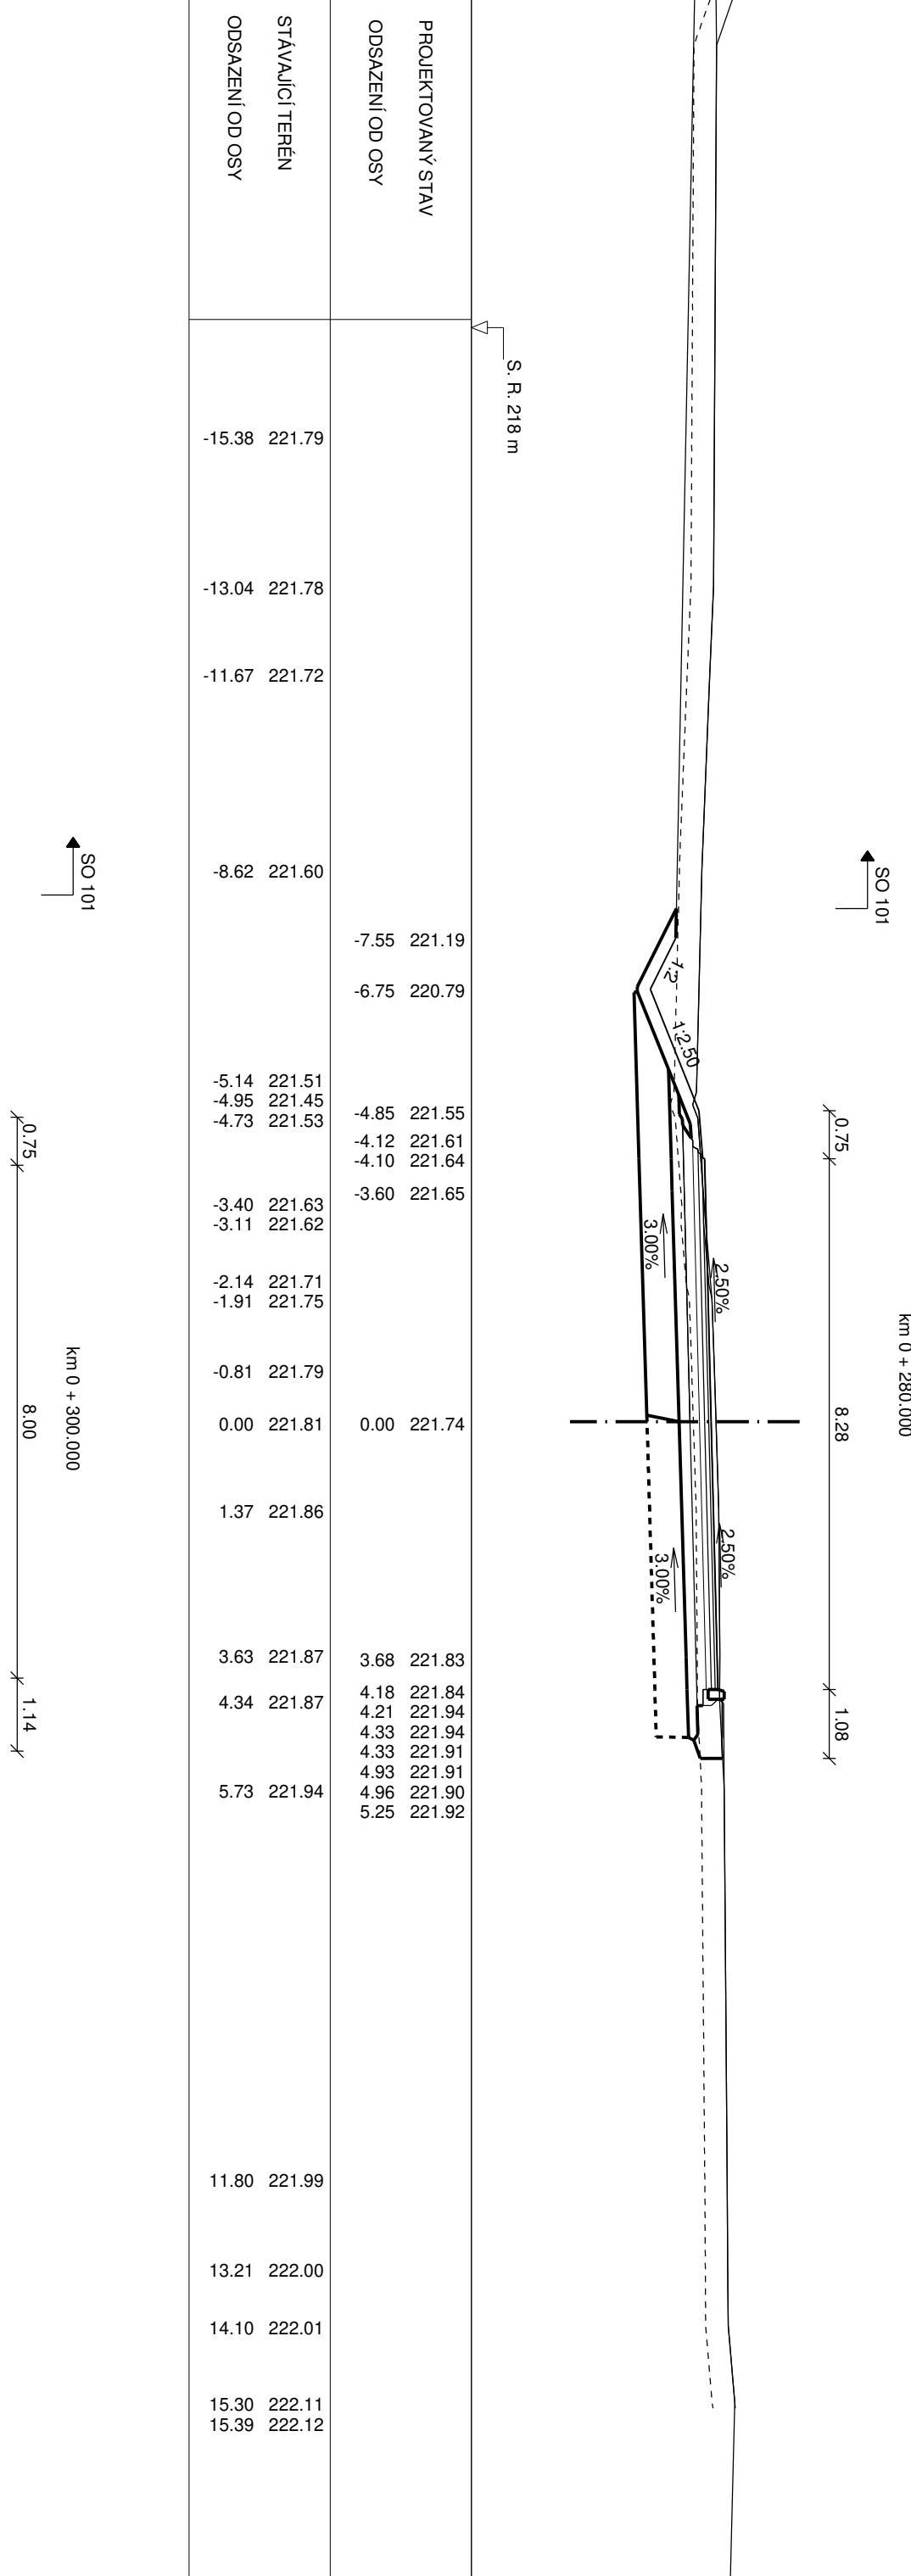

PROJEKOVANÝ STAV OSAZENÍ OD OSY	STAV PO UJEDNĚNÍ OSAZENÍ OD OSY
-7.55 221.19	-15.38 221.79
-6.75 220.79	-13.04 221.78
-4.85 221.55	-11.67 221.72
-4.12 221.61	-8.62 221.60
-4.10 221.64	-5.14 221.51
-3.60 221.65	-4.95 221.45
	-4.73 221.53
	-3.40 221.63
	-3.11 221.62
	-2.14 221.71
	-1.91 221.75
0.00 221.74	-0.81 221.79
	0.00 221.81
	1.37 221.86
3.68 221.83	3.63 221.87
4.18 221.84	4.34 221.87
4.21 221.94	
4.33 221.94	
4.33 221.91	
4.93 221.91	5.73 221.94
4.96 221.90	
5.25 221.92	
	11.80 221.99
	13.21 222.00
	14.10 222.01
	15.30 222.11
	15.39 222.12

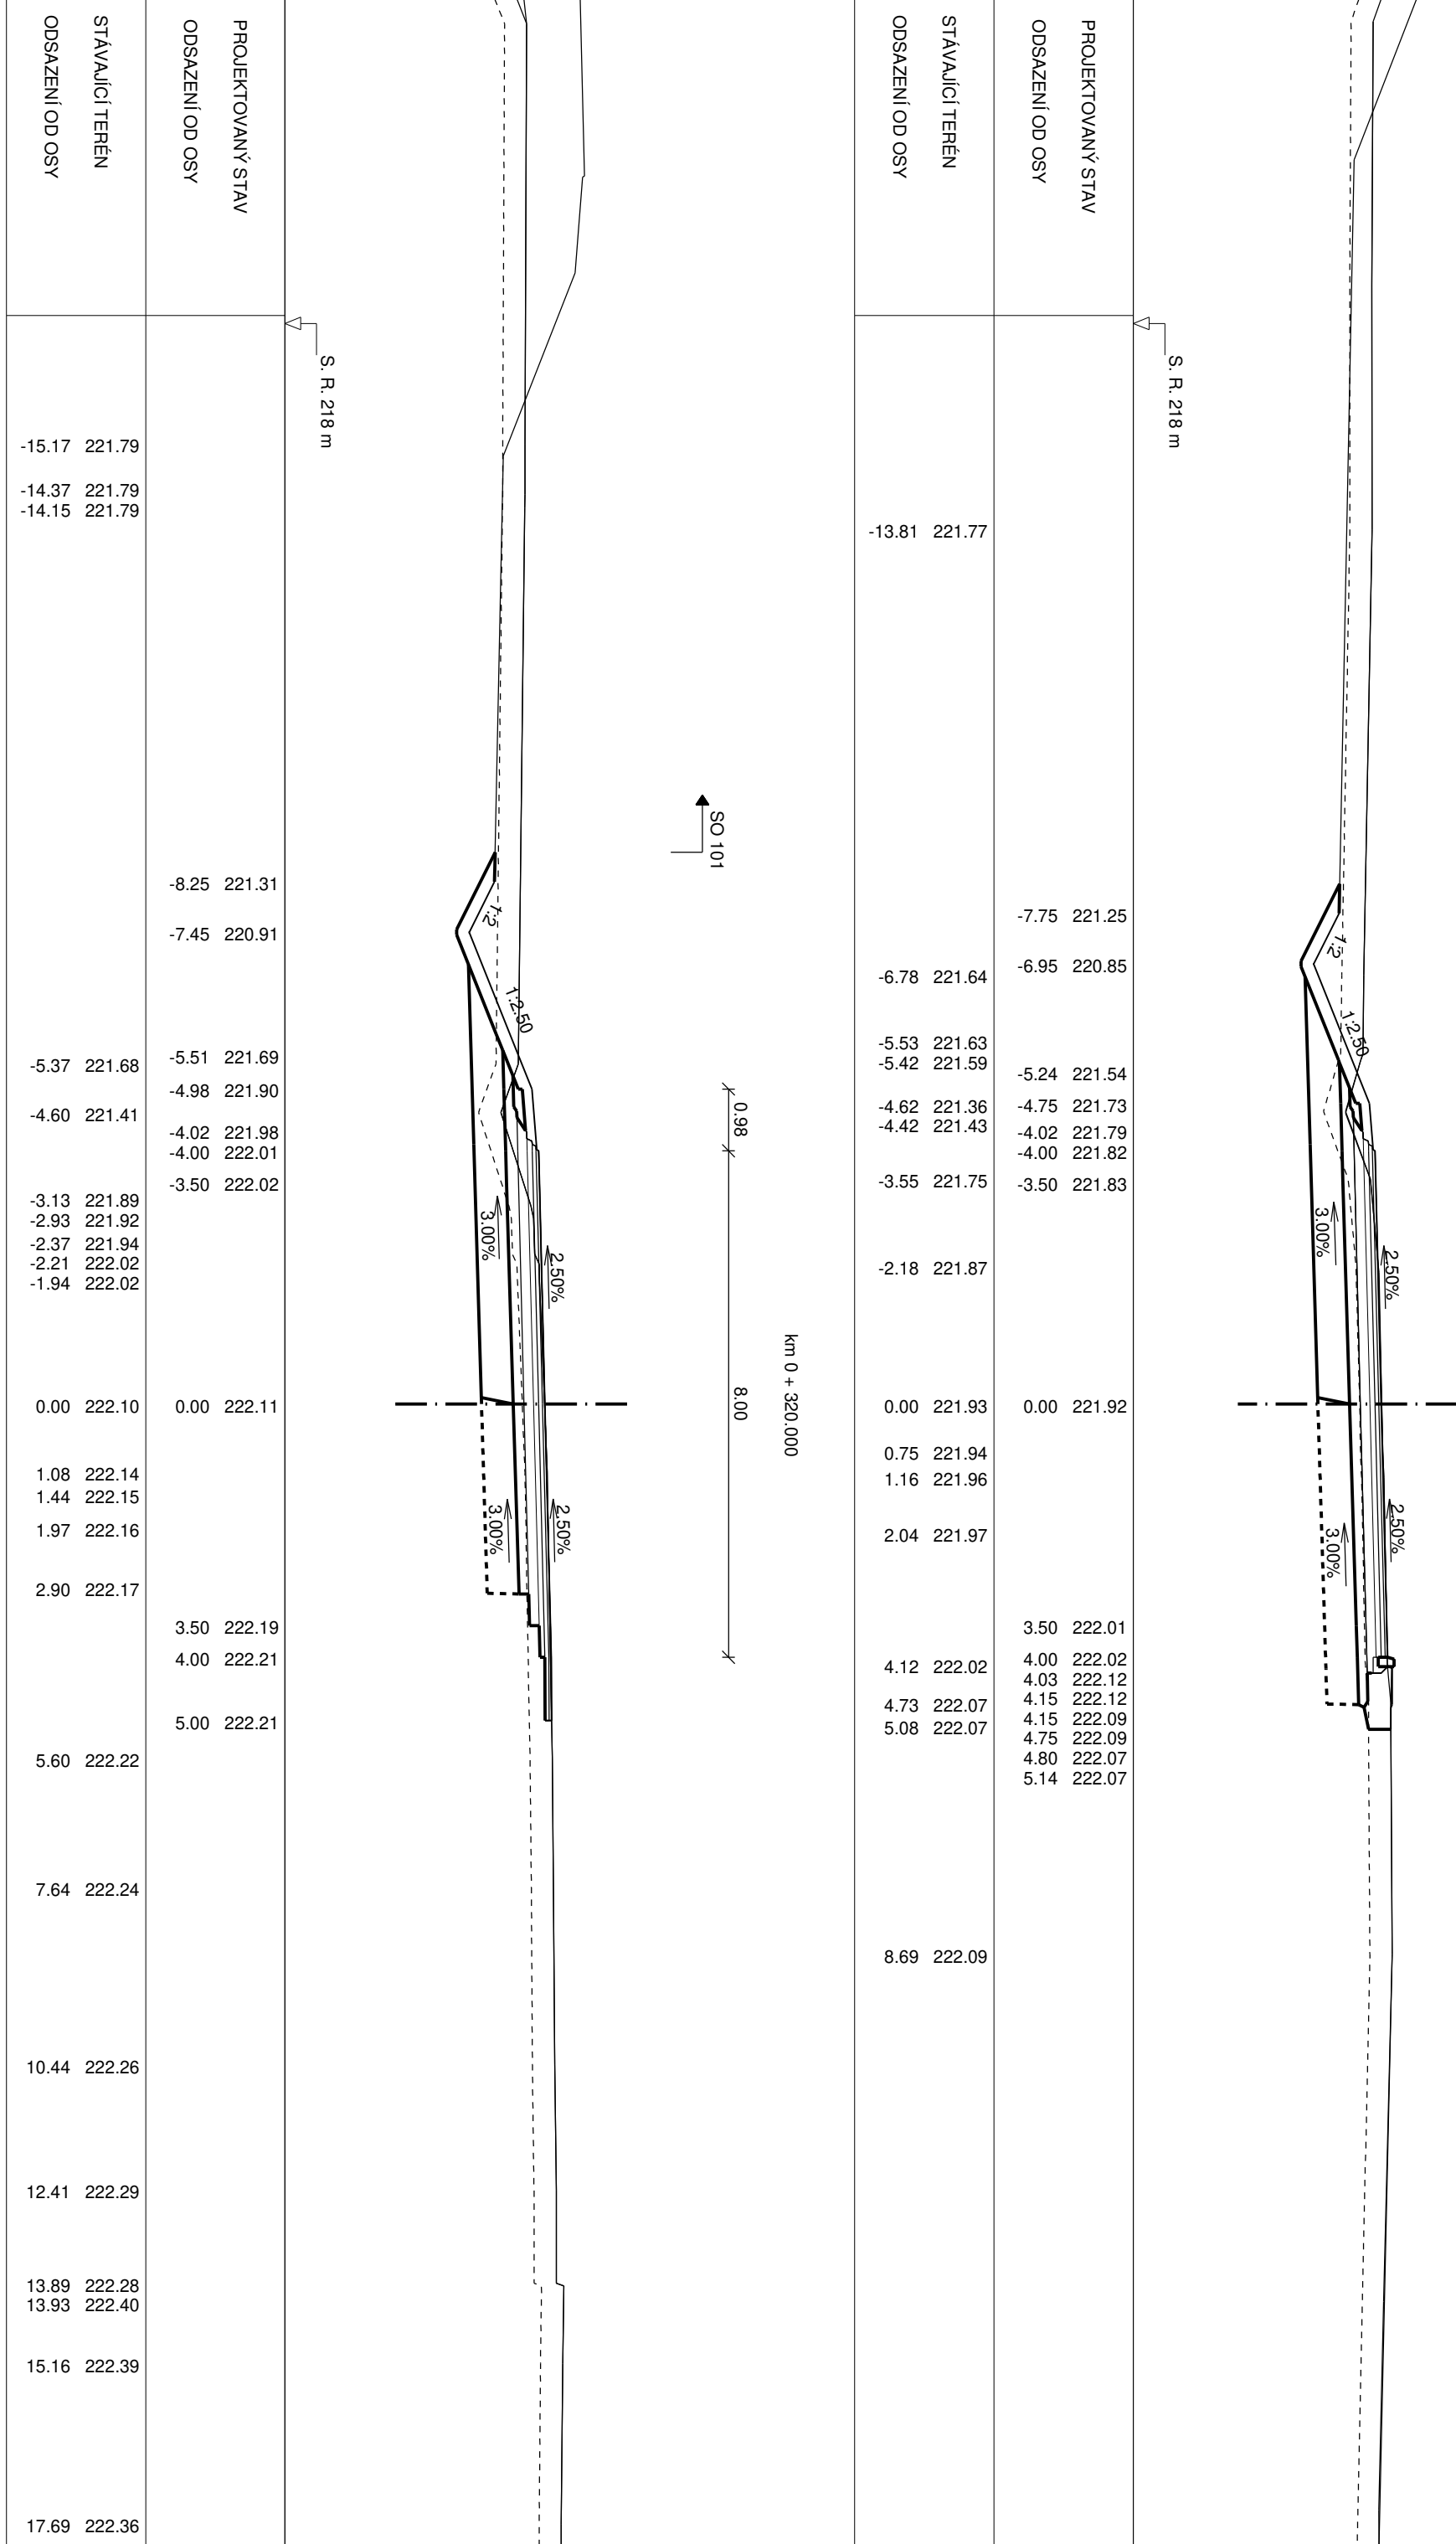

PROJEKTOWANY STAW OSŁAZENI (OD OSY)	STANOWIĄCY TEREN OSŁAZENI (OD OSY)	PROJEKTOWANY STAW OSŁAZENI (OD OSY)	STANOWIĄCY TEREN OSŁAZENI (OD OSY)
-15.17 221.79 -14.37 221.79 -14.15 221.79	-13.81 221.77	-8.25 221.31 -7.45 220.91	-7.75 221.25 -6.95 220.85
-5.37 221.68 -4.60 221.41	-5.53 221.63 -5.42 221.59 -4.62 221.36 -4.42 221.43	-5.51 221.69 -4.98 221.90 -4.02 221.98 -4.00 222.01	-5.24 221.54 -4.75 221.73 -4.02 221.79 -4.00 221.82
-3.13 221.89 -2.93 221.92 -2.37 221.94 -2.21 222.02 -1.94 222.02	-3.55 221.75	-3.50 222.02	-3.50 221.83
0.00 222.10 1.08 222.14 1.44 222.15 1.97 222.16	-2.18 221.87	0.00 222.11	0.00 221.92
2.90 222.17	0.00 221.93 0.75 221.94 1.16 221.96 2.04 221.97	3.50 222.19 4.00 222.21	3.50 222.01 4.00 222.02 4.03 222.13 4.15 222.12 4.15 222.09 4.75 222.09 4.80 222.07 5.14 222.07
5.60 222.22	4.12 222.02 4.73 222.07 5.08 222.07	5.00 222.21	8.69 222.09
7.64 222.24			
10.44 222.26			
12.41 222.29			
13.89 222.28 13.93 222.40			
15.16 222.39			
17.69 222.36			

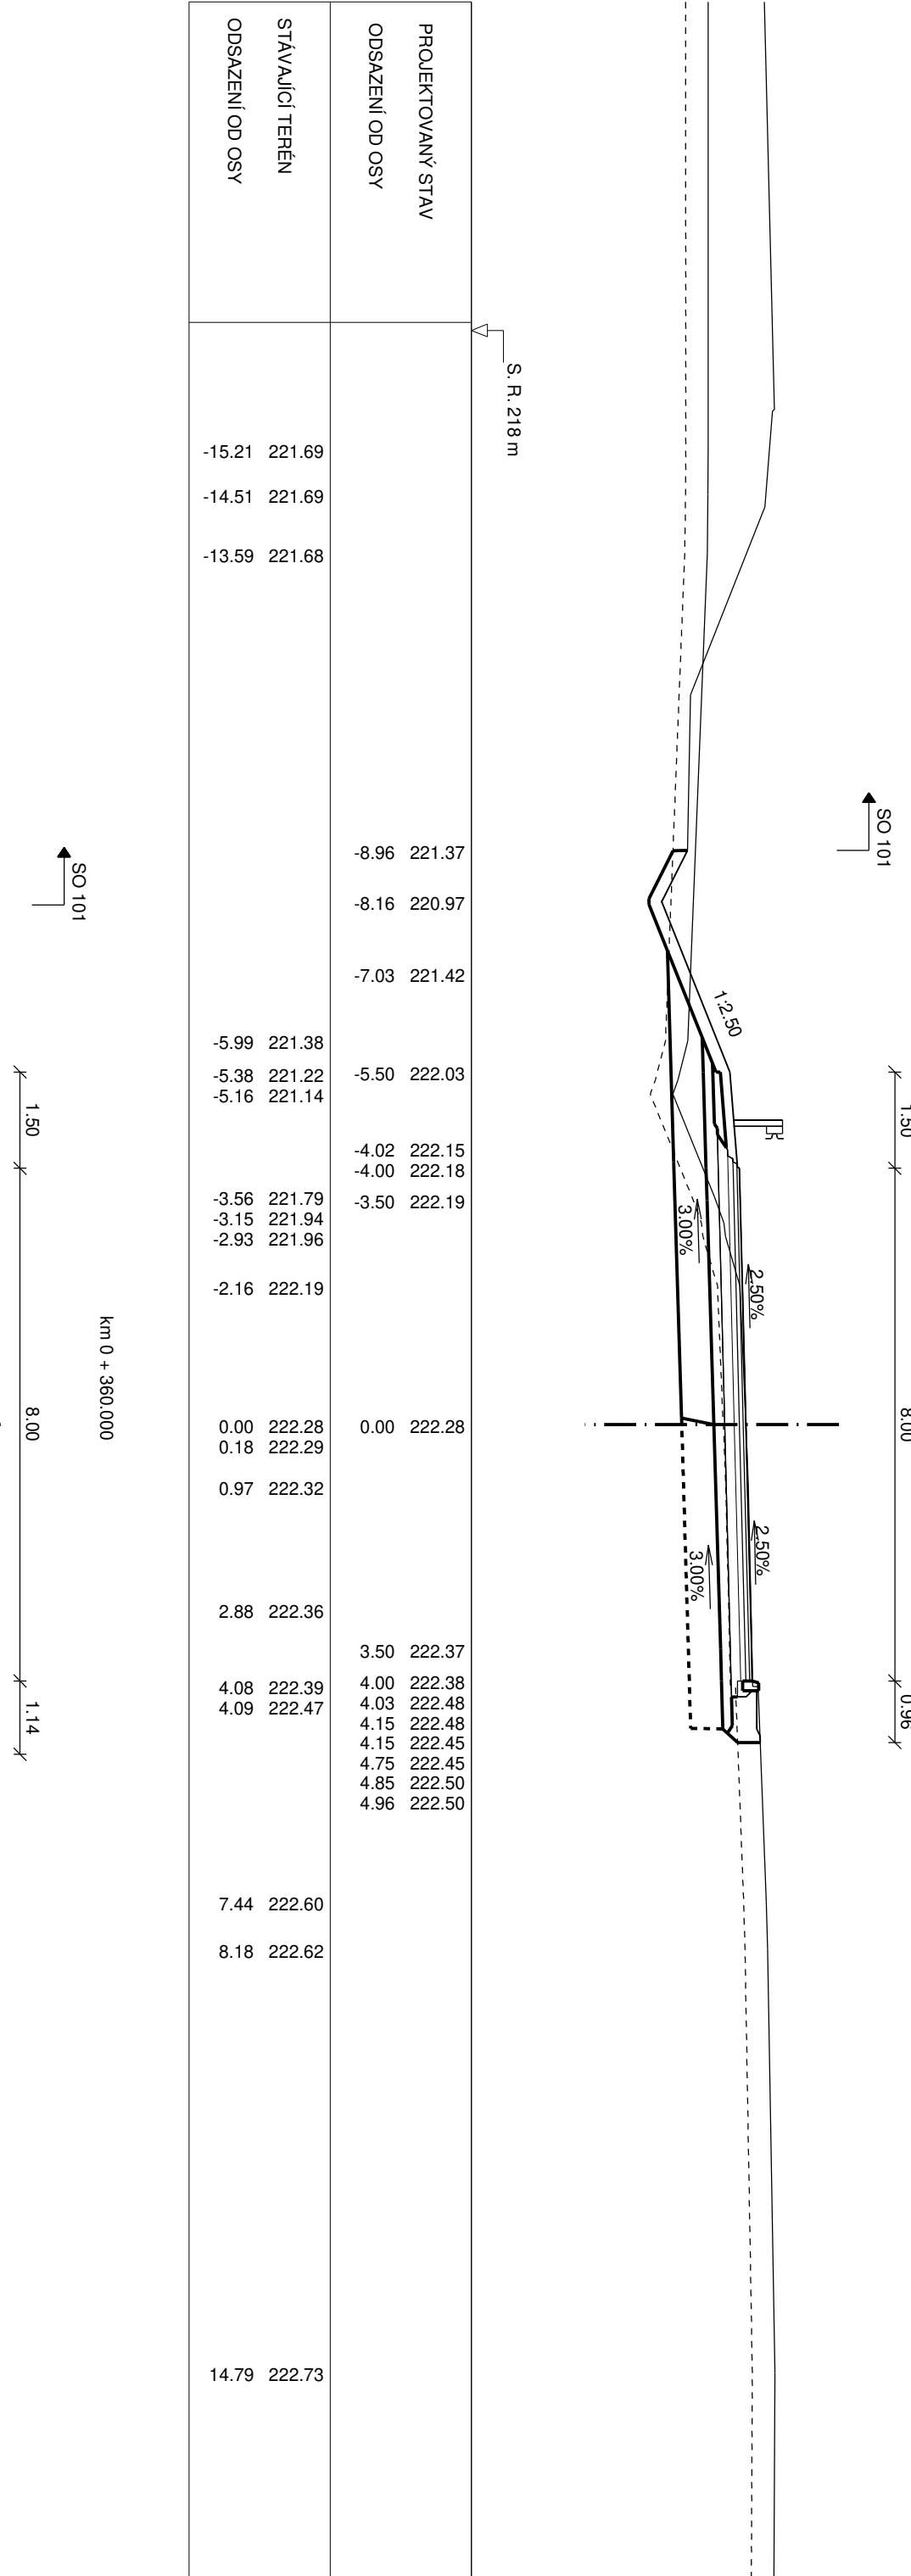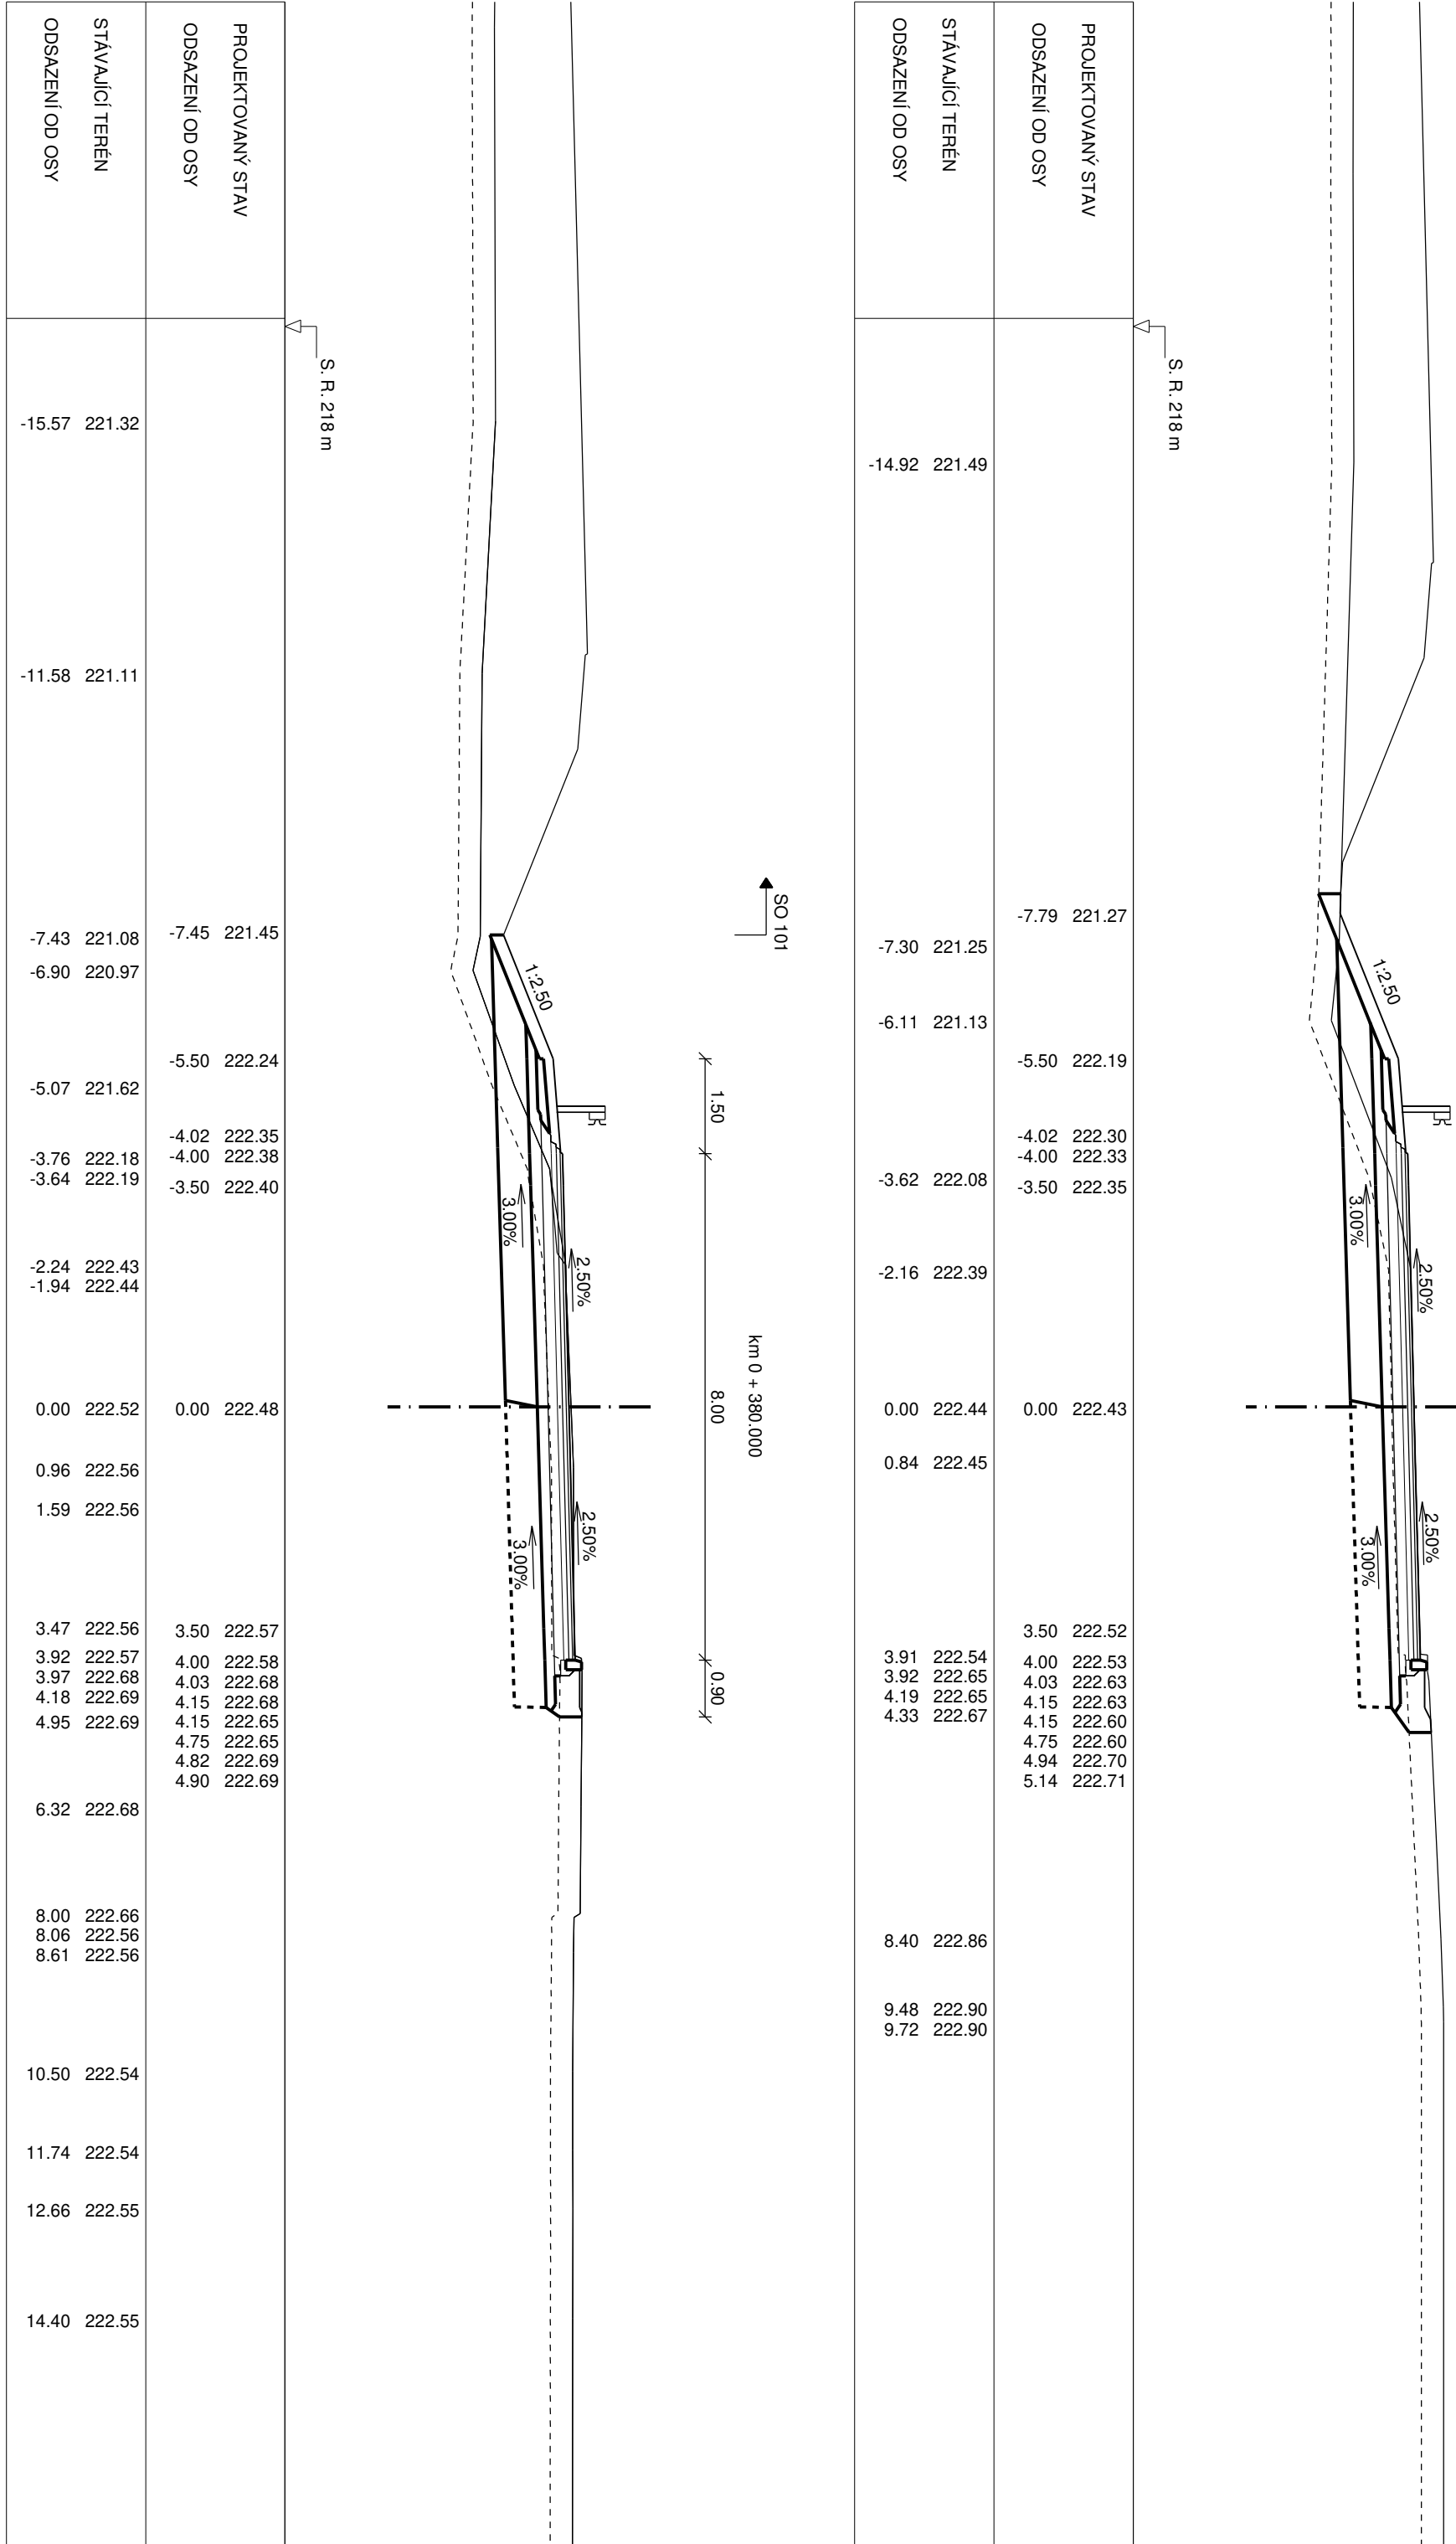[illegible]

PROJEKOVANJ STAV OSNAŽENI OD OSV	STAVANJE TEREN OSNAŽENI OD OSV	PROJEKOVANJ STAV OSNAŽENI OD OSV	STAVANJE TEREN OSNAŽENI OD OSV
-15.57 221.32	-11.58 221.11	-7.43 221.08 -6.90 220.97	-14.92 221.49
-5.07 221.62	-3.76 222.18 -3.64 222.19	-7.45 221.45 -5.50 222.24 -4.02 222.35 -4.00 222.38 -3.50 222.40	-6.11 221.13 -3.62 222.08 -2.16 222.39
-2.24 222.43 -1.94 222.44	0.00 222.52	0.00 222.48	0.00 222.44 0.84 222.45
0.96 222.56 1.59 222.56	3.47 222.56 3.92 222.57 3.97 222.68 4.18 222.69 4.95 222.69	3.50 222.57 4.00 222.58 4.03 222.68 4.15 222.68 4.15 222.65 4.76 222.65 4.82 222.69 4.90 222.69	3.50 222.52 4.00 222.53 4.03 222.63 4.15 222.63 4.15 222.60 4.76 222.60 4.94 222.70 5.14 222.71
6.32 222.68	8.00 222.66 8.06 222.56 8.61 222.56	8.40 222.86	9.48 222.90 9.72 222.90
10.50 222.54	11.74 222.54		
12.66 222.55	14.40 222.55		

**Ředitelství
silnic
a dálnic**

Ředitelství silnic a dálnic s. p.
Čerťanská 2023/12, Koč, 140 00 Praha 4

Značkovitost:	 Valbek, spol. s r.o. Vaňuňova 505/17 460 07 Liberec 3	HIP:
		ING. T. KLIMENT

 Valbek	Významostní		Zah. dok.	21-11-15001
	Zodp. projektant		M. KOŘÍNEK	02/2025
	Tech. kontrola		ING. J. KLIMENT	02/2025
	Akce		ING. M. HANZL	02/2025
	I/6 MLAĐA BOLESLAV - MARTINOVICE		Stupeň	PDS
Průřez	PŘÍČNÉ ŘEZY km 0,220 - 0,380		Počet formátů	14x44
			Měřítko	1 : 100
			C. měřeno	Paré
Zhotovitel: 10 Vydání: 05/07 100% (stavba)			5.2	