
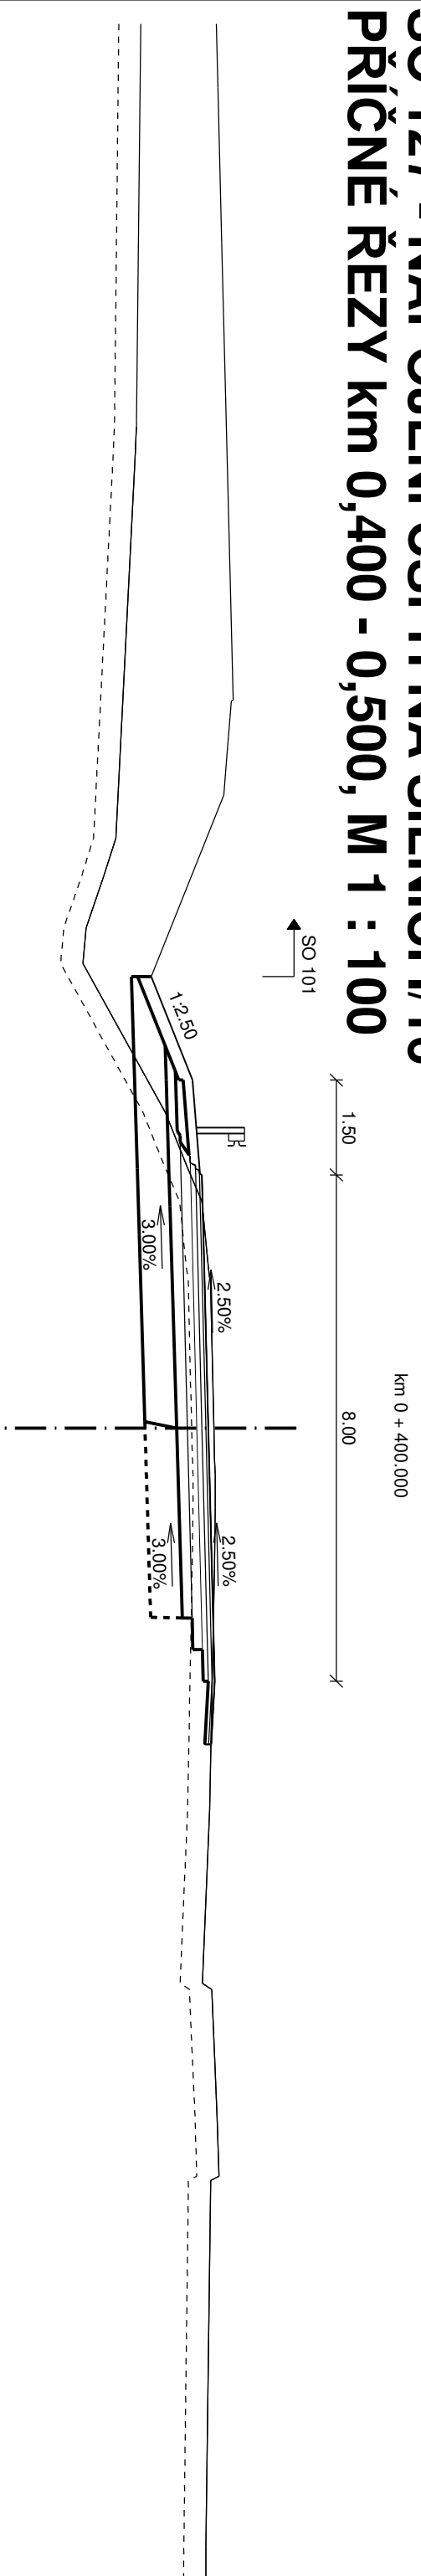
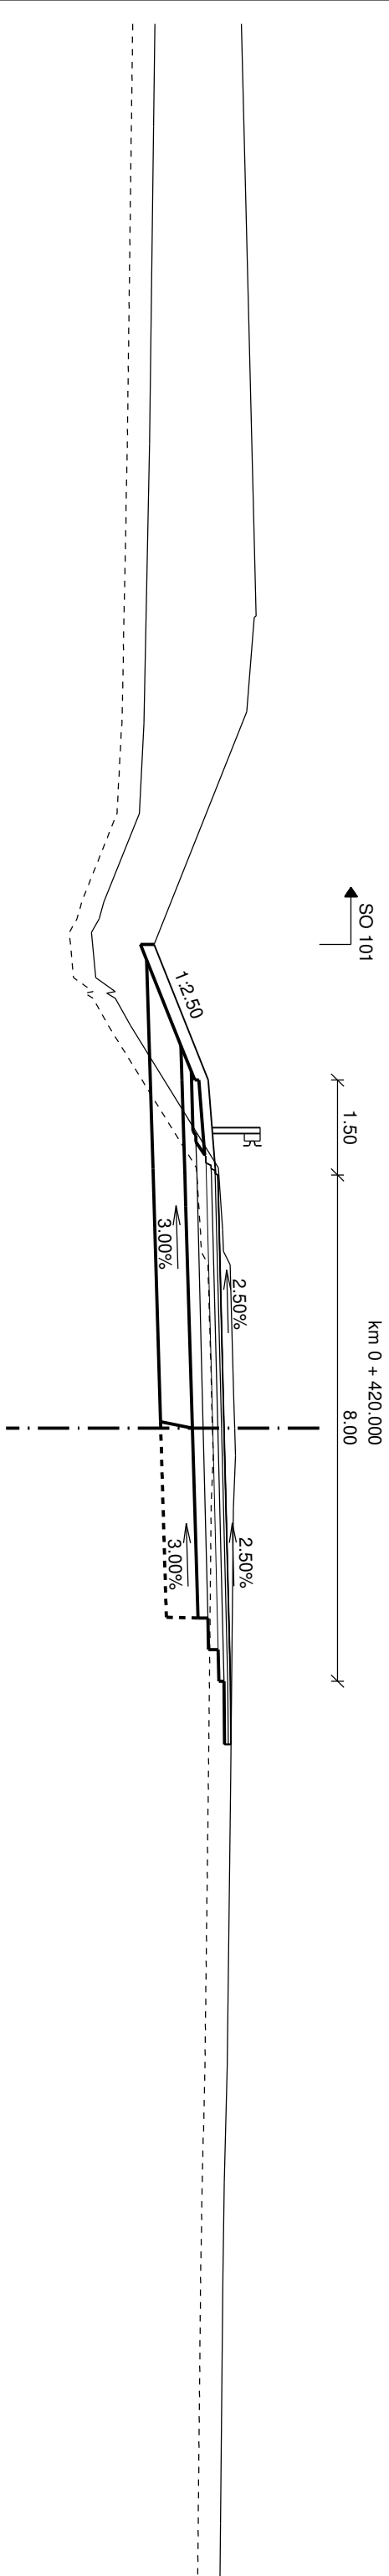



**SO 127 - NAPOJENÍ ČSPH NA SILNICI I/16
PŘÍČNÉ ŘEZY km 0,400 - 0,500, M 1 : 100**

[illegible]


STYMLJ[C]I TEREEN ODSAZENI OD OSY	PROJEKTOVANÝ STAV ODSAZENI OD OSY
-15.56 221.20	
-11.13 221.11	
-9.71 221.03	
-8.31 220.47	
-8.05 220.40	
-7.83 220.28	-7.65 221.27
-7.12 220.34	
-6.90 220.65	
-6.87 220.52	
-6.79 220.65	
-6.36 220.89	-5.50 222.12
-4.11 222.28	-4.02 222.24
	-4.00 222.27
-3.13 222.35	-3.50 222.29
-2.79 222.36	
-2.58 222.47	
-0.52 222.53	0.00 222.37
0.00 222.54	
0.44 222.55	
1.27 222.52	
	3.50 222.46
	4.00 222.47
	5.00 222.48
5.56 222.48	
10.10 222.42	
11.92 222.38	
13.39 222.36	
17.32 222.32	

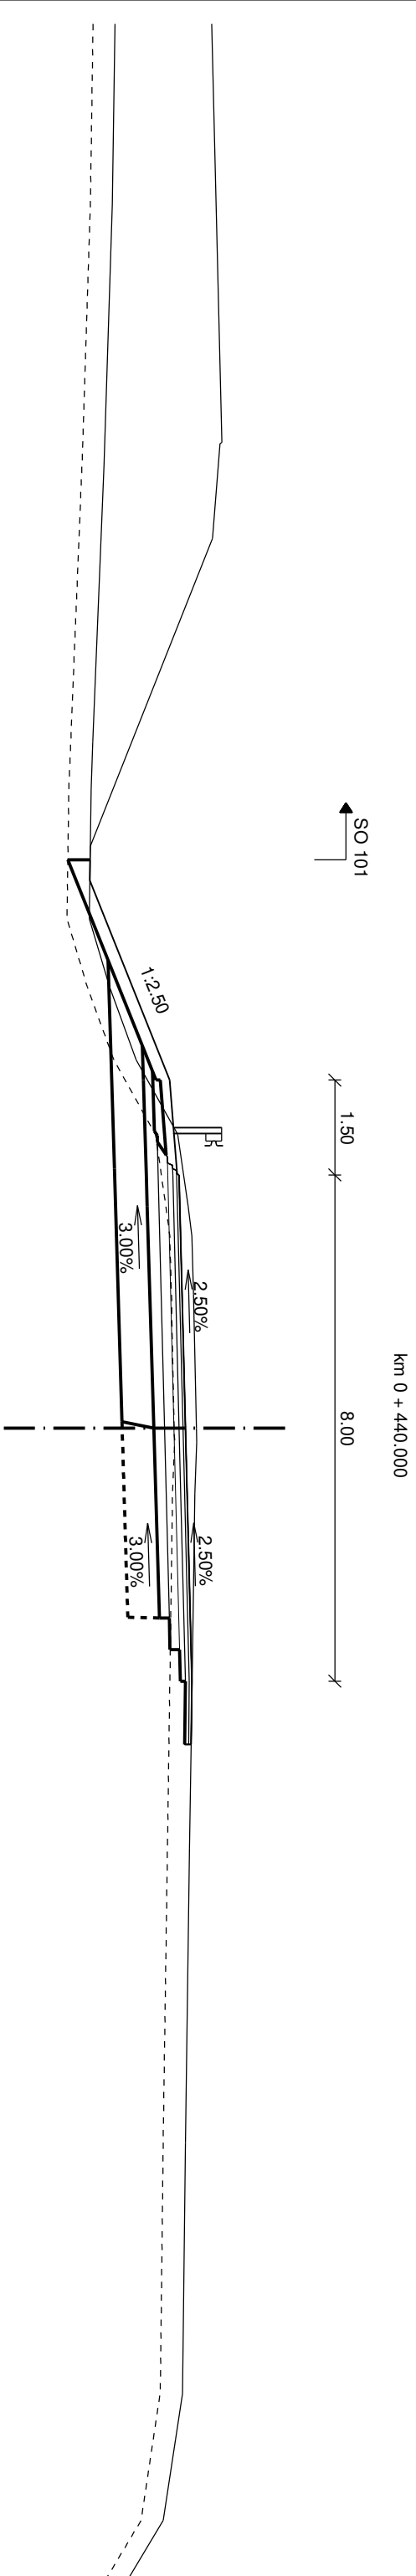

STÁLJÍCÍ TERÉN OPSÁZENÍ OD OSY	PROJEKTOVANÝ STAV OPSÁZENÍ OD OSY
-15.22 221.08	
-10.84 220.90	
-10.10 220.88	
	-8.95 220.86
-8.05 220.85	
-6.97 221.17	
-5.82 221.59	
	-5.50 222.12
-4.64 222.24	
	-4.02 222.24
-3.51 222.41	
-3.03 222.47	
	-3.50 222.28
-2.12 222.50	
0.00 222.54	0.00 222.37
0.22 222.55	
1.04 222.51	
	3.50 222.45
4.28 222.47	4.00 222.47
	5.00 222.46
6.65 222.43	
11.30 222.37	
15.26 222.32	
15.99 222.21	
17.26 222.02	

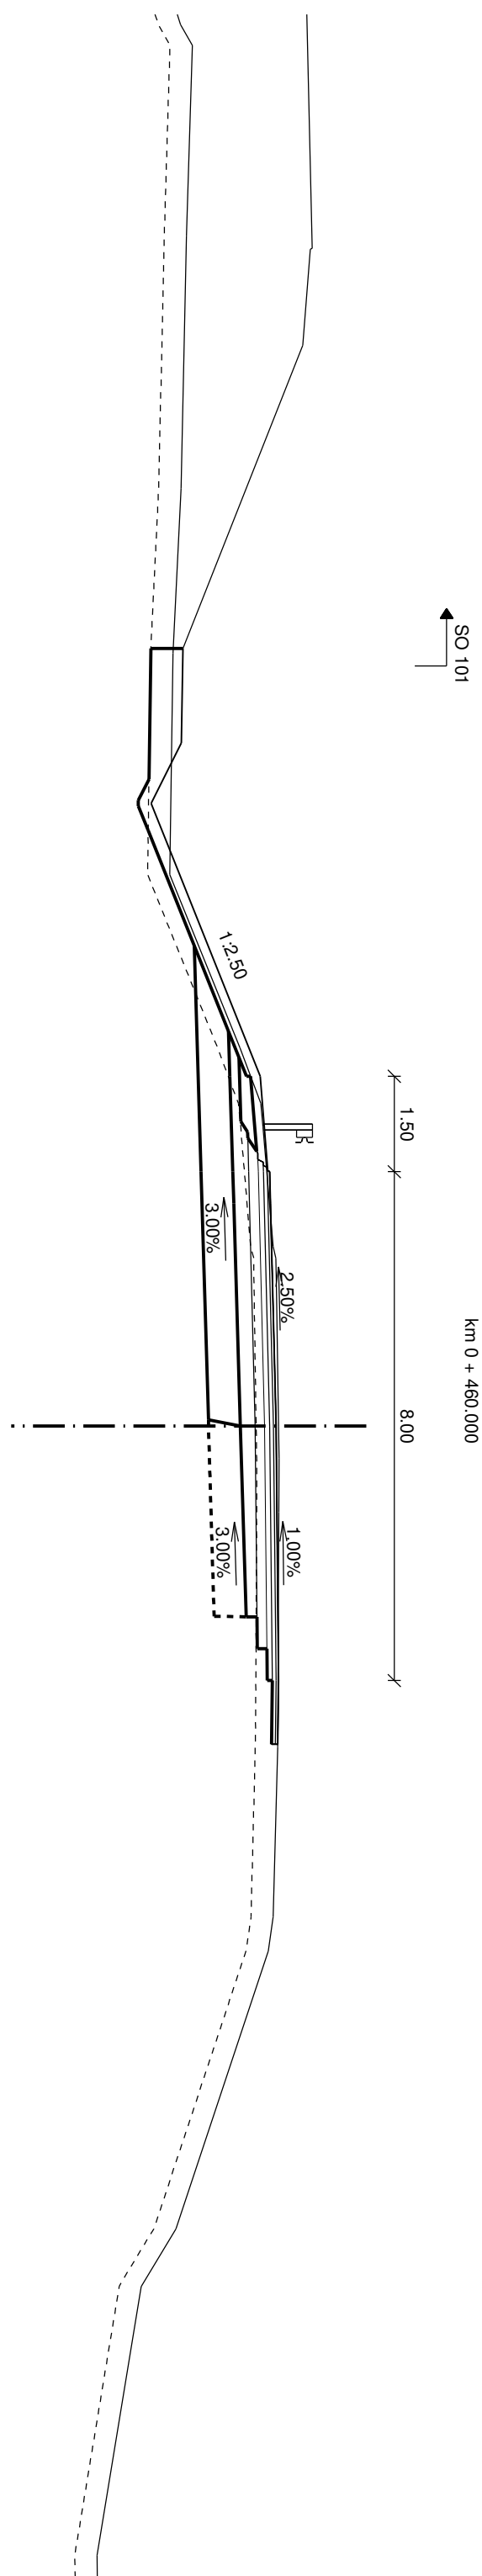

PROJEKTOVANÝ STAV ODSAZENÍ OD OSY	STAVAJÍCÍ TERÉN ODSAZENÍ OD OSY
-11.84 220.87	-14.74 220.99
-10.43 220.84	-12.15 220.86
-9.79 220.52	
-9.04 220.82	-8.67 220.81
	-5.94 221.91
-5.50 222.23	-5.07 222.24
-4.02 222.35	-4.71 222.28
-4.00 222.38	
-3.50 222.39	-2.82 222.44
	-2.64 222.48
	-2.23 222.49
0.00 222.48	0.00 222.52
	0.50 222.53
	1.35 222.53
3.50 222.52	
4.00 222.52	
5.00 222.51	5.04 222.51
	7.72 222.44
	8.25 222.36
	12.62 220.91
	13.53 220.36
	17.75 219.67

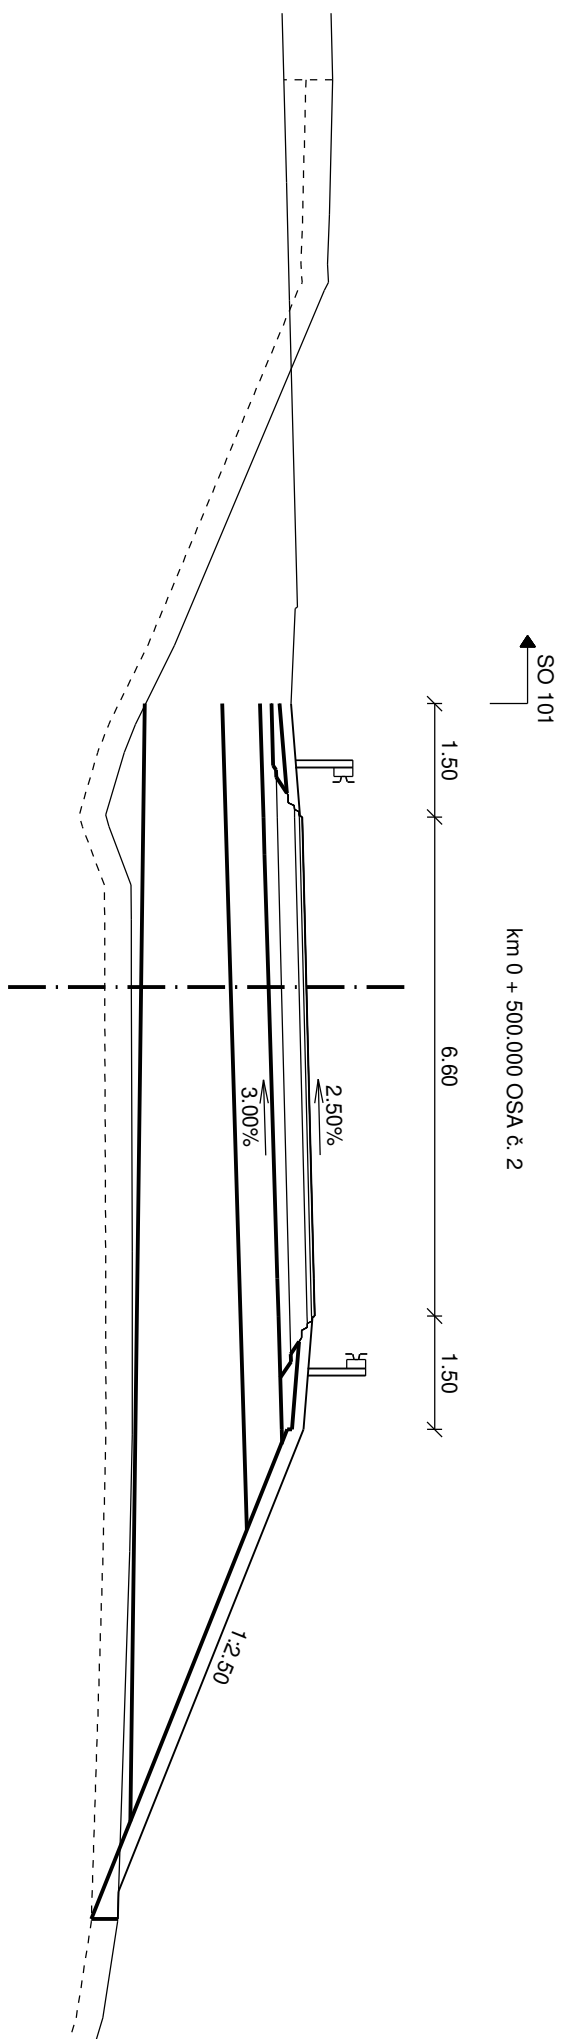

STAVAJÍCÍ TĚŘEN OPSÁZENÍ OD OSY	PROJEKTOVANÝ STAV OPSÁZENÍ OD OSY
-9.56 223.66 -9.52 223.67 -9.22 223.62	-6.02 222.27
-4.52 221.64	-3.75 223.18
-3.48 221.12 -3.10 220.97	-2.27 223.30 -2.25 223.33
-2.28 220.73 -2.13 220.77	-1.75 223.34
-1.35 221.06 -0.89 221.06	0.00 223.38
0.00 221.07	
3.49 221.08	3.85 223.48 4.35 223.49 4.37 223.46
5.91 221.08	5.85 223.34
7.47 221.04	
12.36 220.88	11.96 220.90 12.33 220.89

SO 127	Napojení ČSPH na silnici I/16
--------	-------------------------------

Výškový systém Bpw

Objednatel: **Ředitelství silnic a dálnic**

Zhotovitel:	 Valbek	HP:
	Valbek, spol. s r.o. Vahurova 505/17 460 07 Liberec 3	ING. T. KLIMENT

	Wyprowadzi	M. KOBIŃSKI		Znak, číslo	21-113-001
	Zoob. projektant	ING. T. KLIMENT		Datum	02/2025
	Tech. kontrola	ING. M. HANZL		Stupeň	PPPS
	Acqa			Počet fórmulí	10x44
				Měřitko	1 : 100
I/16 MLADÁ BOLESLAV - MARTINOVICE				č. přílohy	Páté
Zpracovatel: Ing. Tomáš Kliment Valbeka s.r.o. Valbeka s.r.o. 17 460 07, Lábeň 3	Příloha PŘÍLOHÉ ŘEZY km 0,400 - 0,500	5.3			