


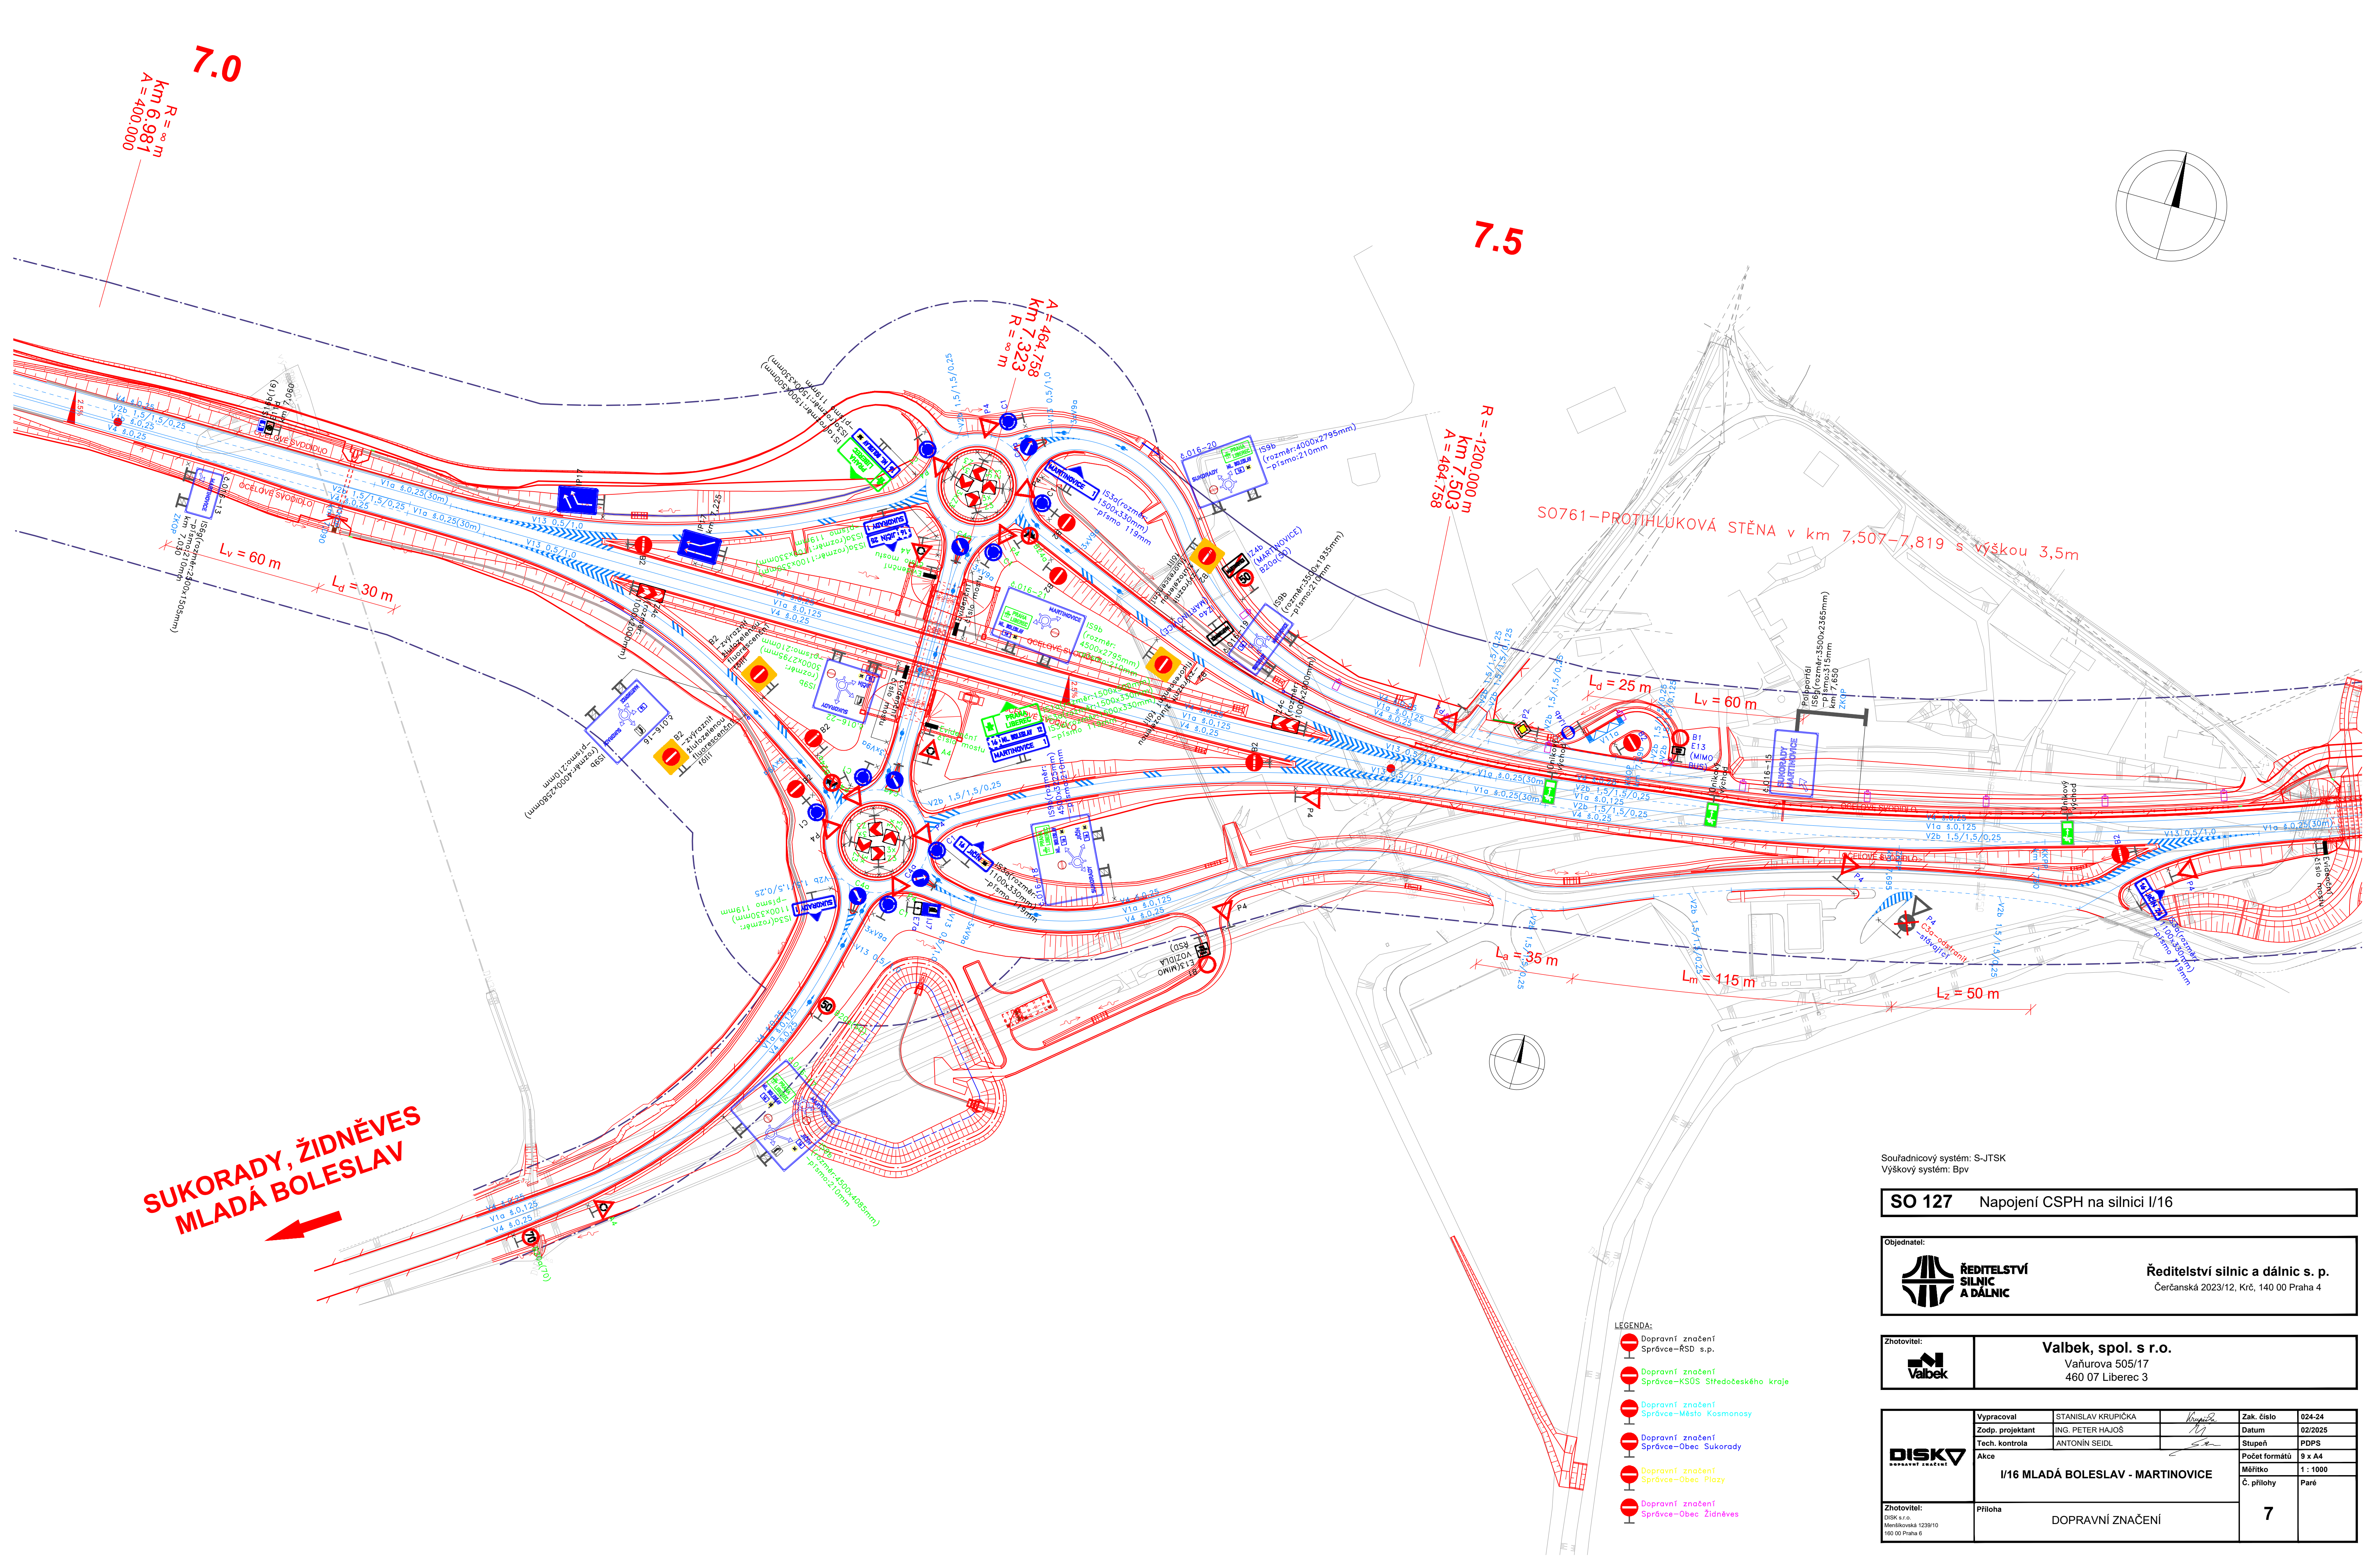

Souřadnicový systém: S-JTSK
Výškový systém: Bpv

SO 127 Napojení CSPH na silnici I/16

Objednatel:



Ředitelství silnic a dálnic s. p.
Čerčanská 2023/12, Krč, 140 00 Praha 4

Zhotovitel:



Valbek, spol. s r.o.
Vaňurova 505/17
460 07 Liberec 3

DISKY DOPRAVNÍ ZNAČENÍ	Vypracoval	STANISLAV KRUPÍČKA	Zak. číslo	024-24
	Zodp. projektant	ING. PETER HAJDŮŠ	Datum	02/2025
	Tech. kontrola	ANTONIN SEIDL	Stupeň	PDPs
	Akce	I/16 MLADÁ BOLESLAV - MARTINOVCE		
Zhotovitel: Disky s. a. Mentšikovská 1239/10 160 00 Praha 6	Příloha DOPRAVNÍ ZNAČENÍ			Počet formátů 9 x A4
				Měřítka 1:1000 C. přílohy Paré
			7	