


I/16 MLADÁ BOLESLAV - MARTINOVICE
SO 127 NAPOJENÍ CSPH NA SILNICI I/16
VEGETAČNÍ ÚPRAVY M 1:1 000

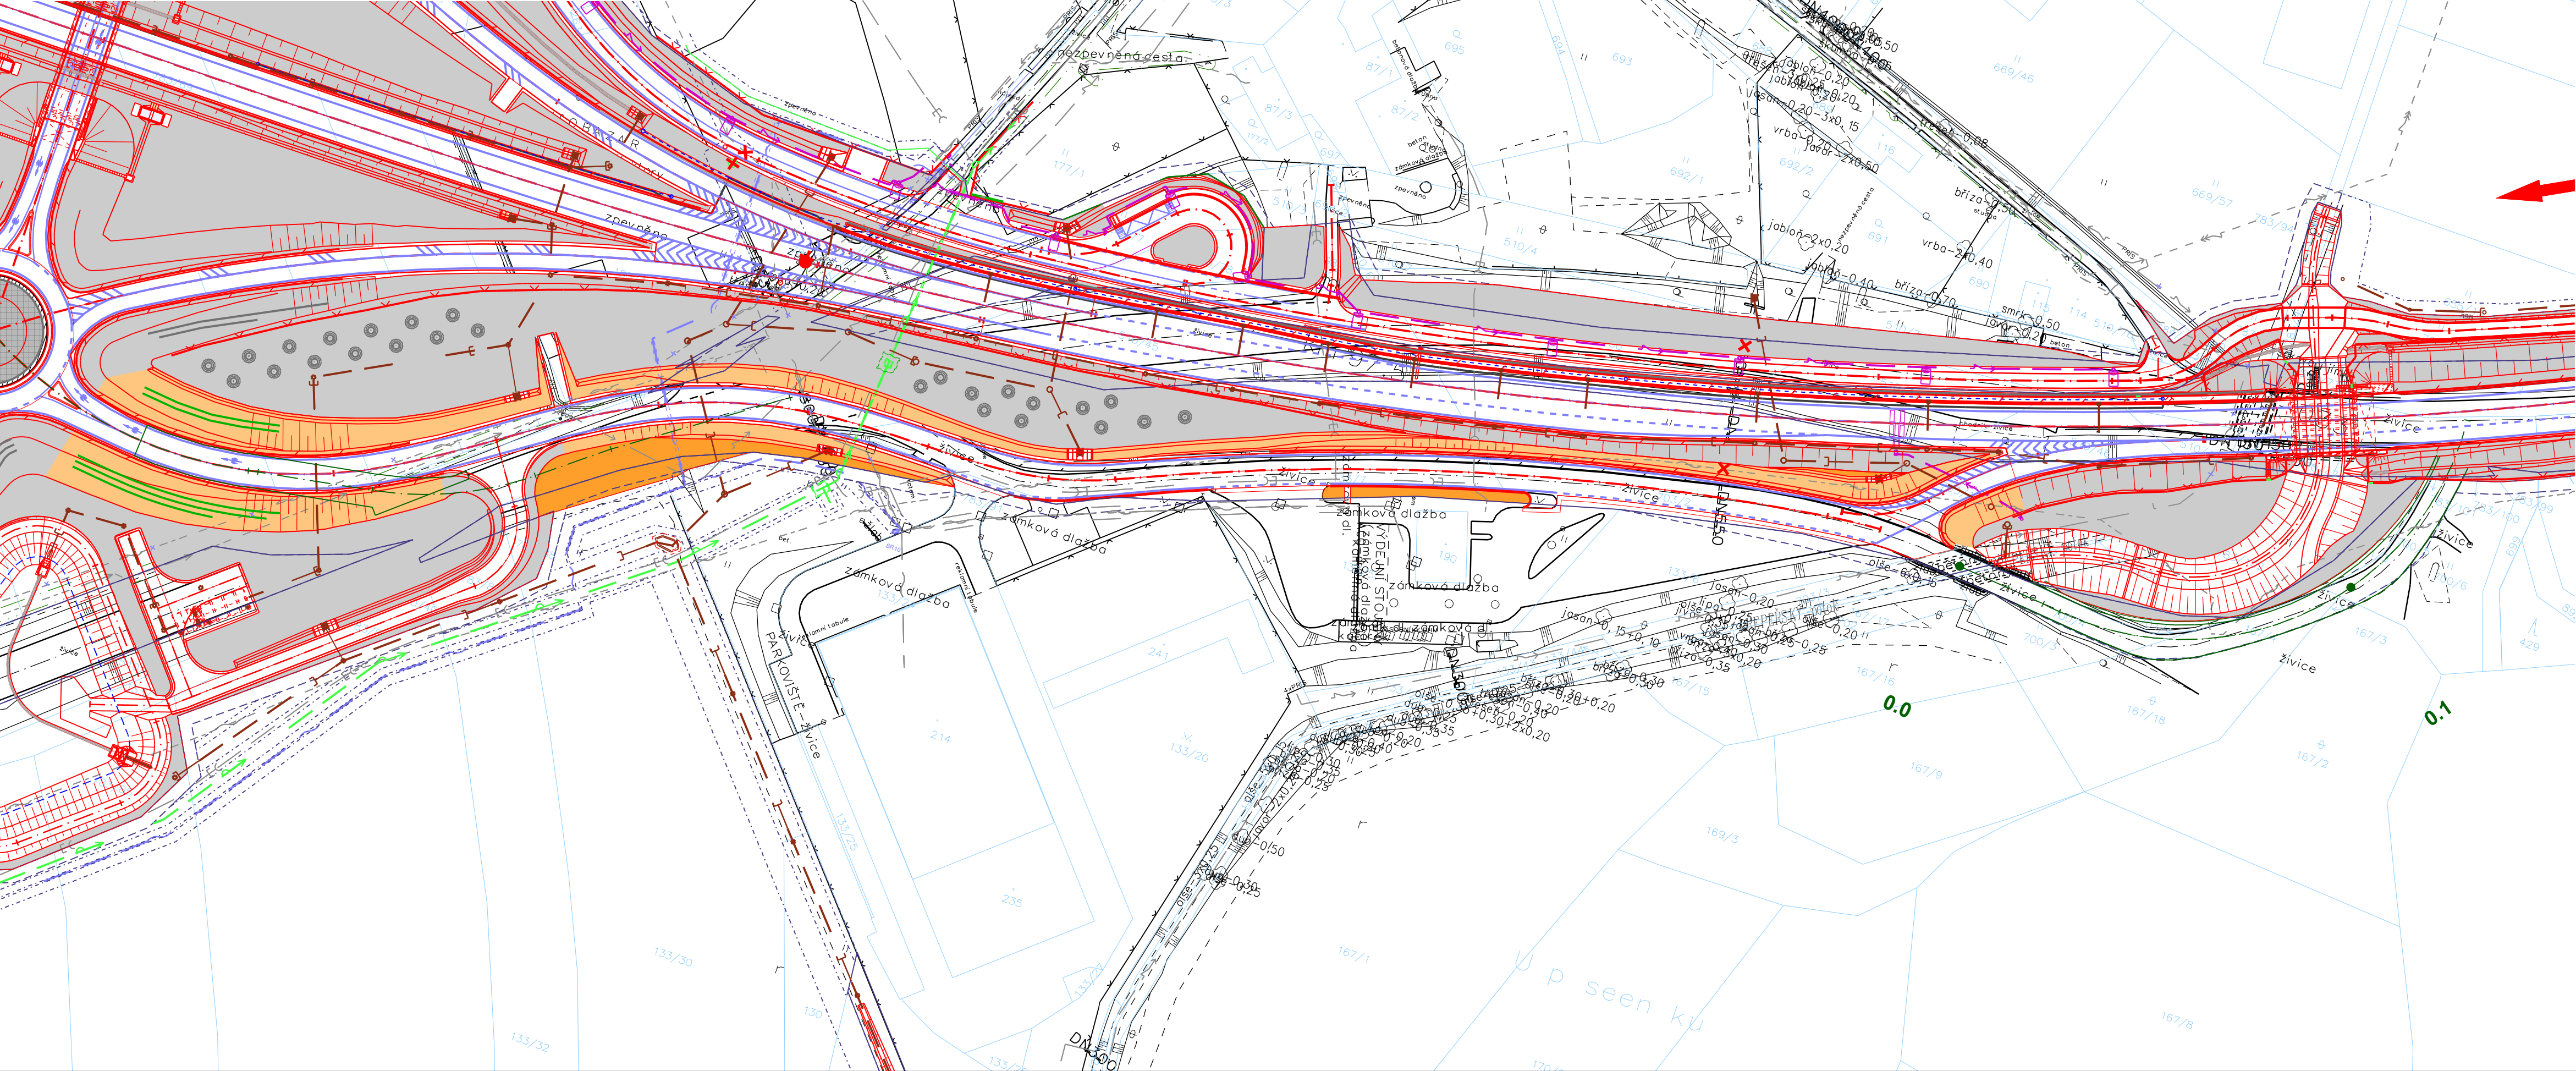

- LEGENDA
- Vegetační úpravy
- ZATRAVNĚNÍ V ROVINĚ
 - ZATRAVNĚNÍ VE SVAHU
 - VÝSADBA KEŘŮ PLOŠNĚ
 - VÝSADBA KEŘŮ V PÁSECH
 - VÝSADBA STROMŮ
- Vegetační úpravy ostatních správců
- ZATRAVNĚNÍ
 - VÝSADBA KEŘŮ PLOŠNĚ
 - VÝSADBA KEŘŮ V PÁSECH
 - VÝSADBA STROMŮ LISTNATÝCH
 - VÝSADBA STROMŮ JEHLIČNATÝCH
 - MULČOVÁNÍ ŠTĚRKEM

Souřadnicový systém: S-JTSK
Výškový systém: Bpv

SO 127 Napojení CSPH na silnici I/16

Objednatel:



Ředitelství silnic a dálnic s. p.
Čerčanská 2023/12, Krč, 140 00 Praha 4

Zhotovitel:



Valbek, spol. s r.o.
Vaňurova 505/17
460 07 Liberec 3

HIP:

ING. T. KLIMENT



Vypracoval	ING. Š. SOKOLÁŘOVÁ	Zak. číslo	21-L113-001
Zodp. projektant	ING. T. KLIMENT	Datum	02/2025
Tech. kontrola	ING. M. HANŽL	Stupeň	PDPS
Akce I/16 MLADÁ BOLESLAV - MARTINOVICE		Počet formátů	4 x A4
		Měřítko	1 : 1000
		Č. přílohy	Paré
Zhotovitel: Valbek, spol. s r.o. Vaňurova 505/17 460 07 Liberec 3	Příloha VEGETAČNÍ ÚPRAVY		8