



SO 128 - OBRATIŠTĚ BUS MARTINOVICE
VZOROVÝ PŘÍČNÝ ŘEZ, M 1 : 50

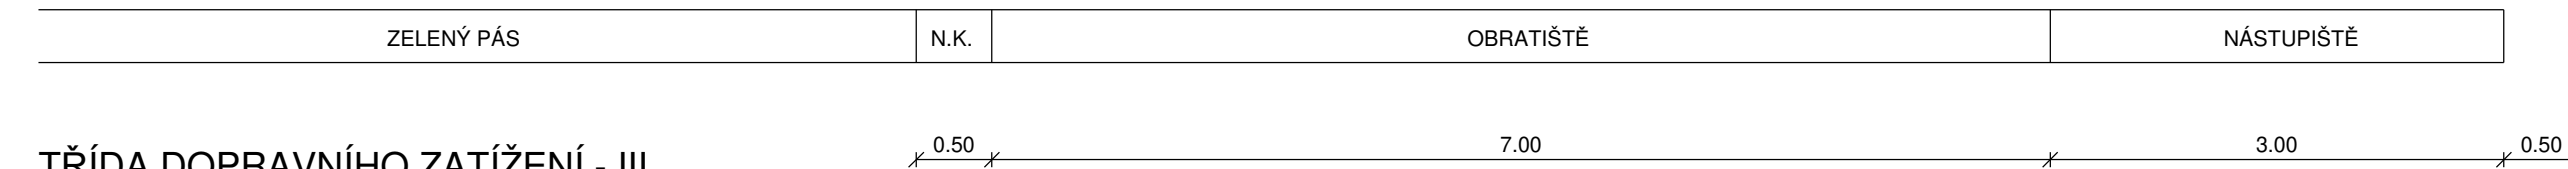


TŘÍDA DOPRAVNÍHO ZATÍŽENÍ - III
NÁVRHOVÁ ÚROVEŇ PORUŠENÍ - D1
TYP PODLOŽÍ - PII (D1-BUS-1)

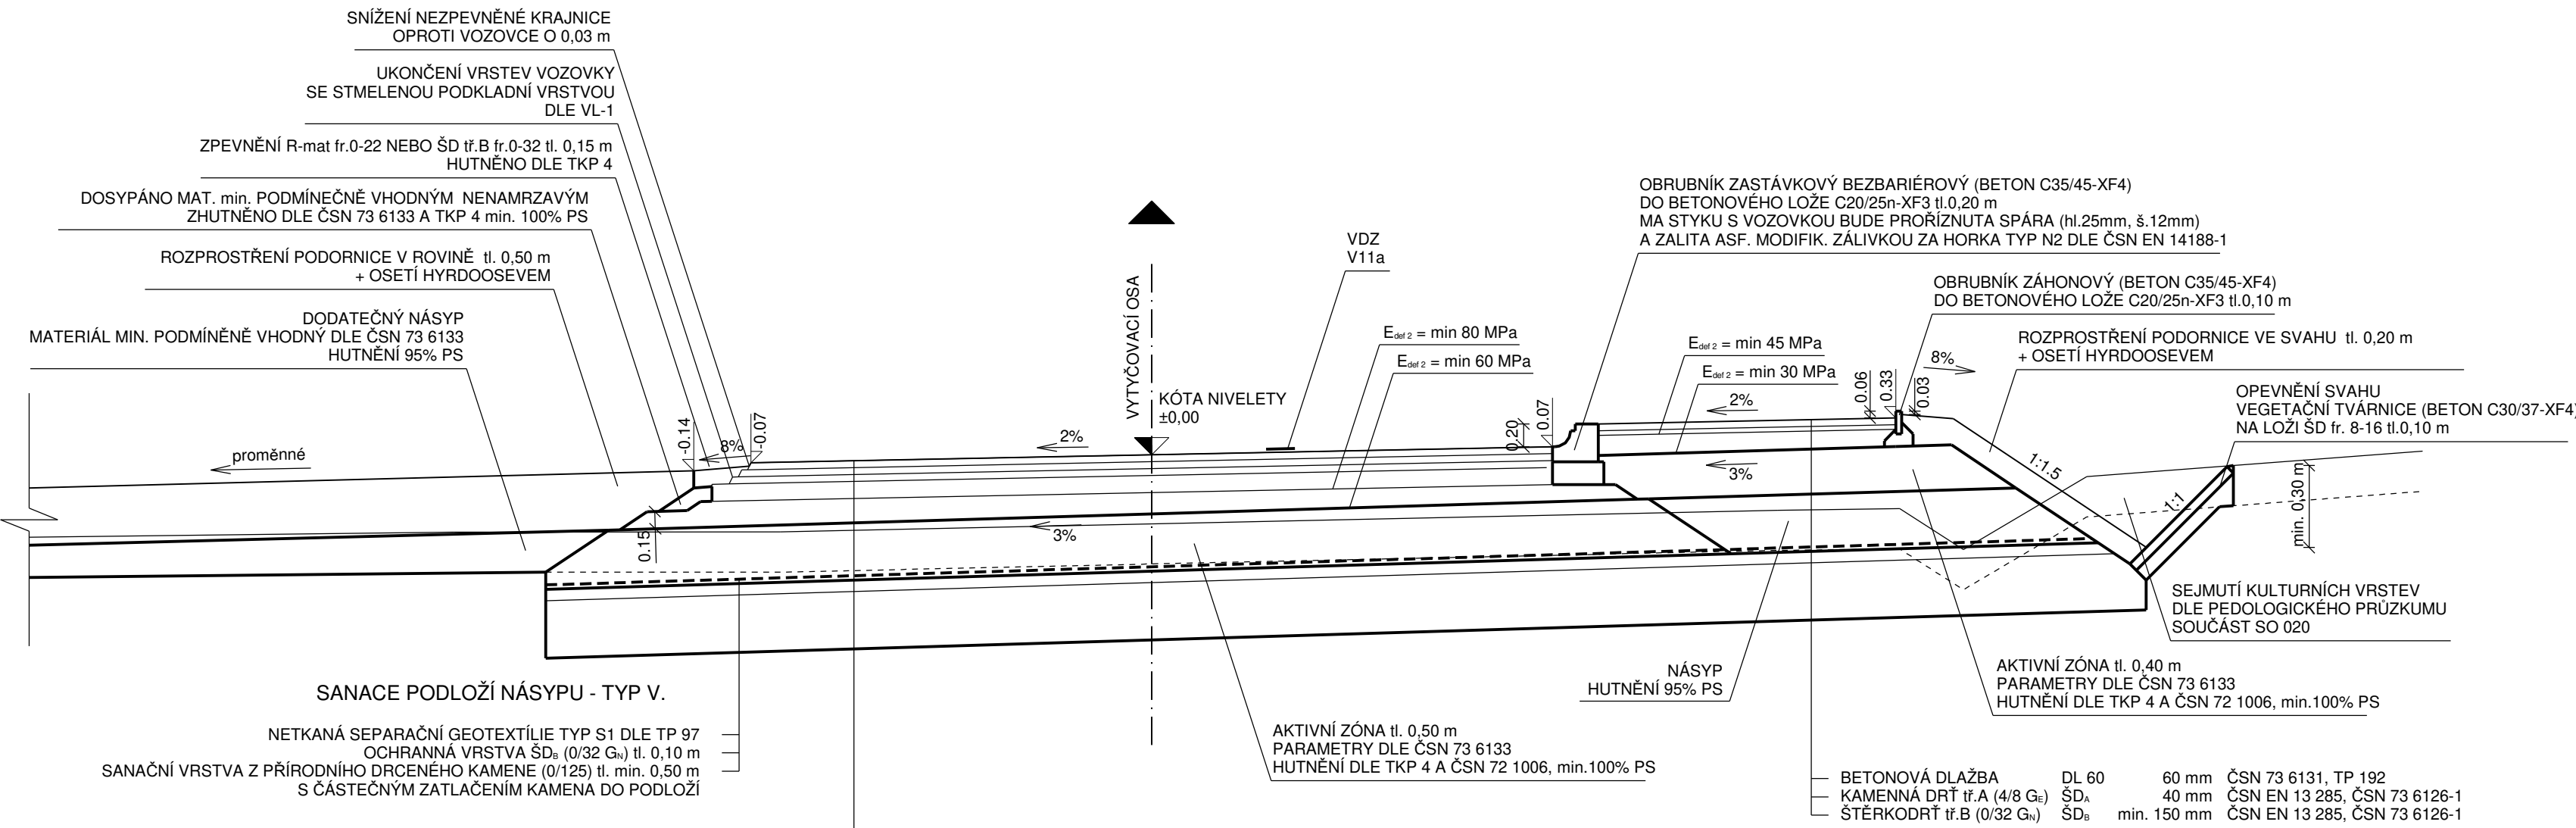




ASFALTOCEMENTOVÝ BETON	ACB 11 50/70	60 mm	ČSN 73 6127-3
SPJOVAČÍ POŠTRÍK EMULZNÍ	PS-C	0,35 kg/m ²	ČSN EN 13808, ČSN 73 6121, ČSN 73 6132
ASFALTOVÝ BETON PRO LOŽNÍ VRSTVY	ACB 16S 50/70	60 mm	ČSN EN 13108-1, ČSN 73 6121
SPJOVAČÍ POŠTRÍK EMULZNÍ	PS-C	0,35 kg/m ²	ČSN EN 13808, ČSN 73 6121, ČSN 73 6132
ASFALTOVÝ BETON PRO PODKLADNÍ VRSTVY	ACP 22S 50/70	60 mm	ČSN EN 13108-1, ČSN 73 6121
SMĚS KAMENIVA STMELENA CEMENTEM	SC 0/32 C _{50/60}	150 mm	ČSN EN 14 227-1, ČSN 73 6124-1
ŠTERKODRŮT A	SD, 0/32 G _E	min. 150 mm	ČSN EN 13 285, ČSN 73 6126-1

CELKEM min 480 mm

POZNÁMKA: NA PODKLADNÍCH VRSTVÁCH SC PROVÉST OPATŘENÍ PROTI VÝVOJI REFLEXNÍCH TRHLIN DLE TP 170, ČSN 73 6124-

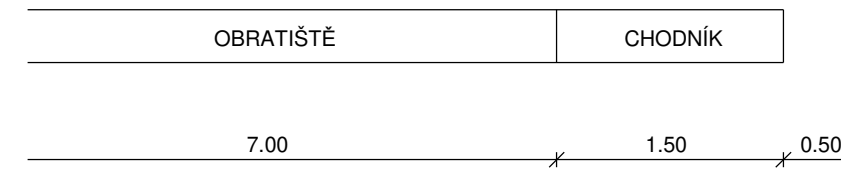

TŘÍDA DOPRAVNÍHO ZATÍŽENÍ - CH
NÁVRHOVÁ ÚROVEŇ PORUŠENÍ - D2
TYP PODLOŽÍ - PIII (D2-D-1)

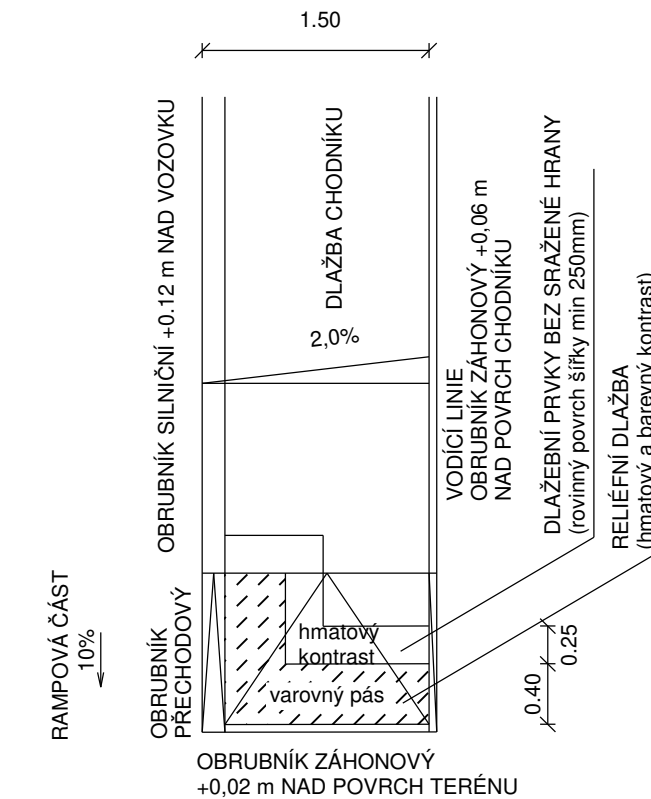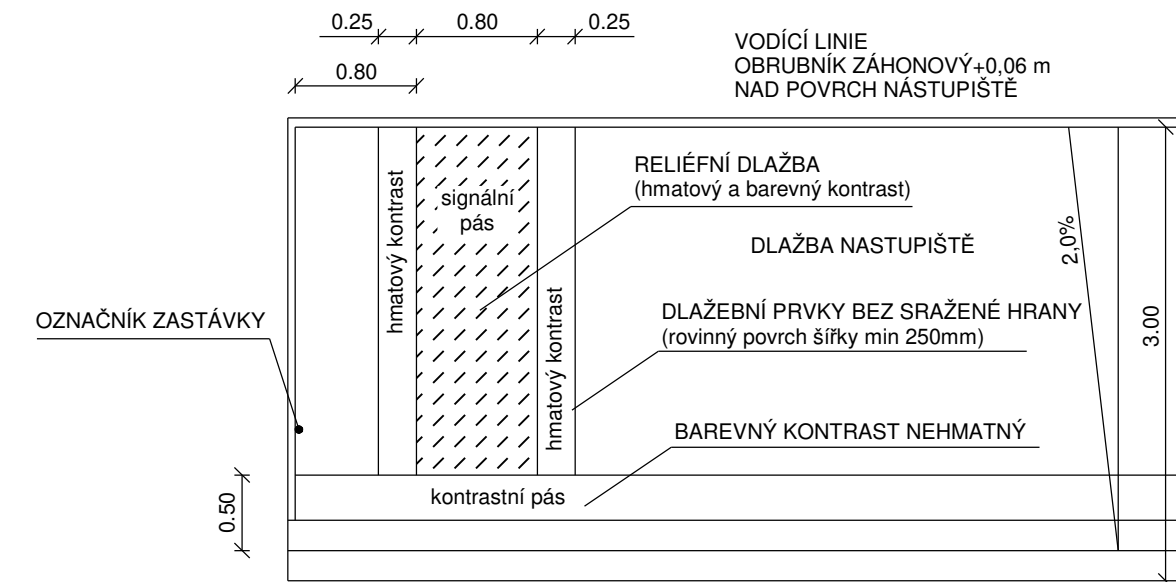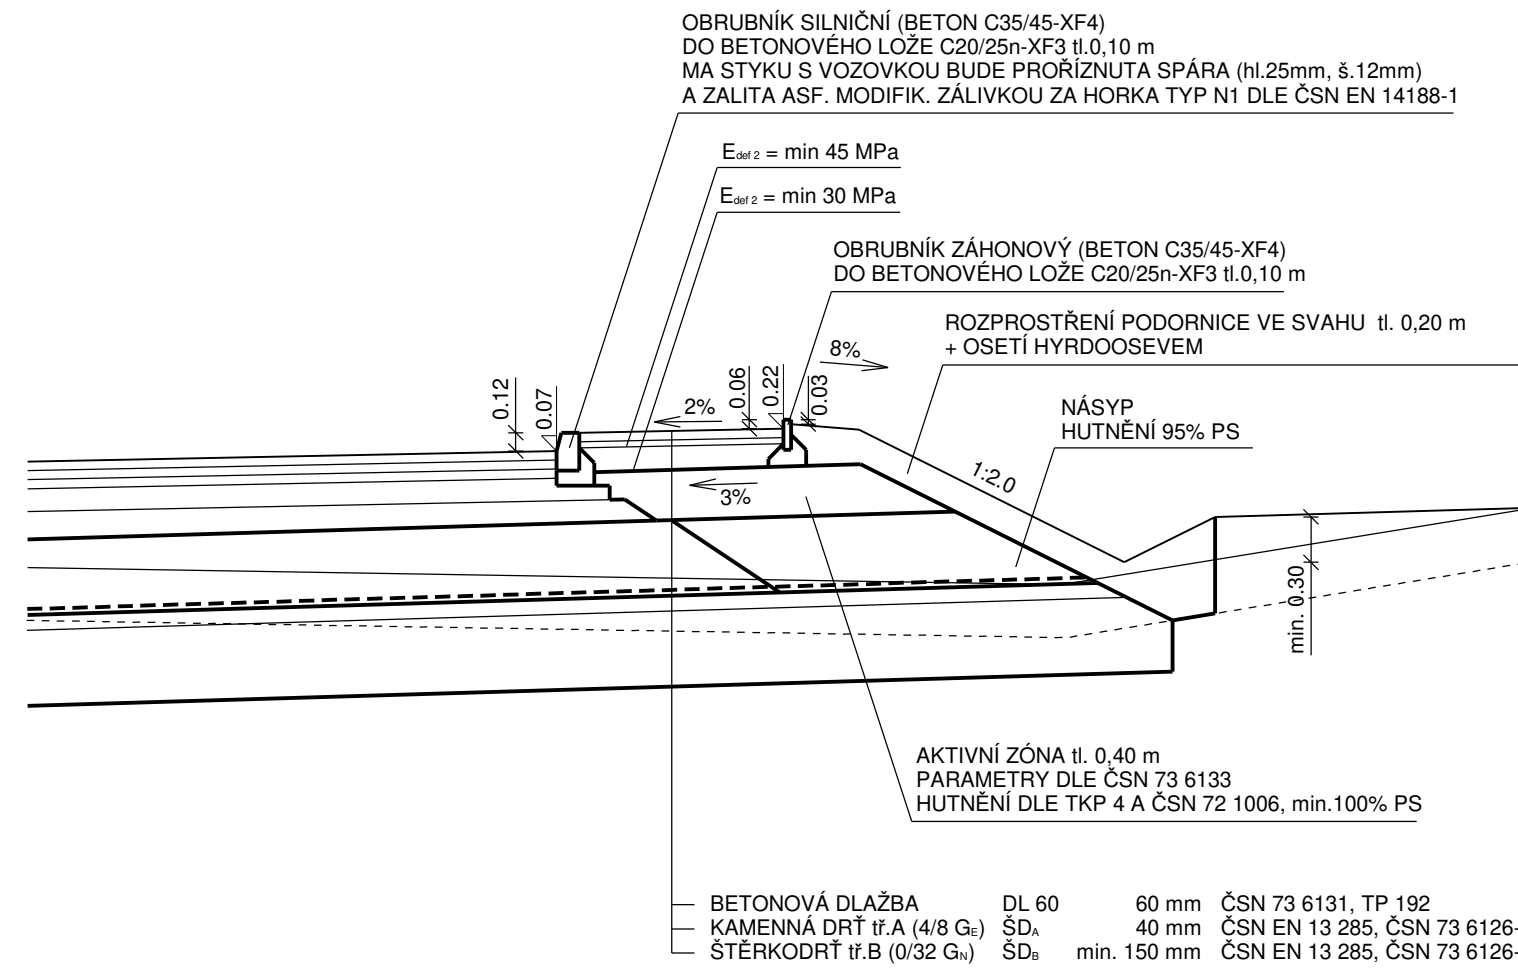**SO 128** Obratiště BUS Martinovice

Ředitelství silnic a dálnic s. p.
Čerčanská 2023/12, Krč, 140 00 Praha 4

Zhotovitel: 	Valbek, spol. s r.o. Vaňurova 505/17 460 07 Liberec 3	HIP: ING. T. KLIMENT
--	--	-----------------------------

	Vypracoval	M. KOŘÍNEK		Zak. číslo	21-L13-001
	Zodp. projektant	ING. T. KLIMENT		Datum	02/2025
	Tech. kontrola	ING. M. HANŽL		Stupeň	PDPS
	Akce			Počet formátů	5 x A4
I/16 MLADÁ BOLESLAV - MARTINOVICE				Měřítko	1: 50
				Č. přílohy	Paré
Zhotovitel: Valbek, spol. s r.o. Vafuřova 505/17 460 07 Liberec 3	Příloha VZOROVÝ PŘÍČNÝ ŘEZ			4	