



SO 128 - OBRATIŠTĚ BUS MARTINOVICE

PŘÍČNÉ ŘEZY M 1 : 100

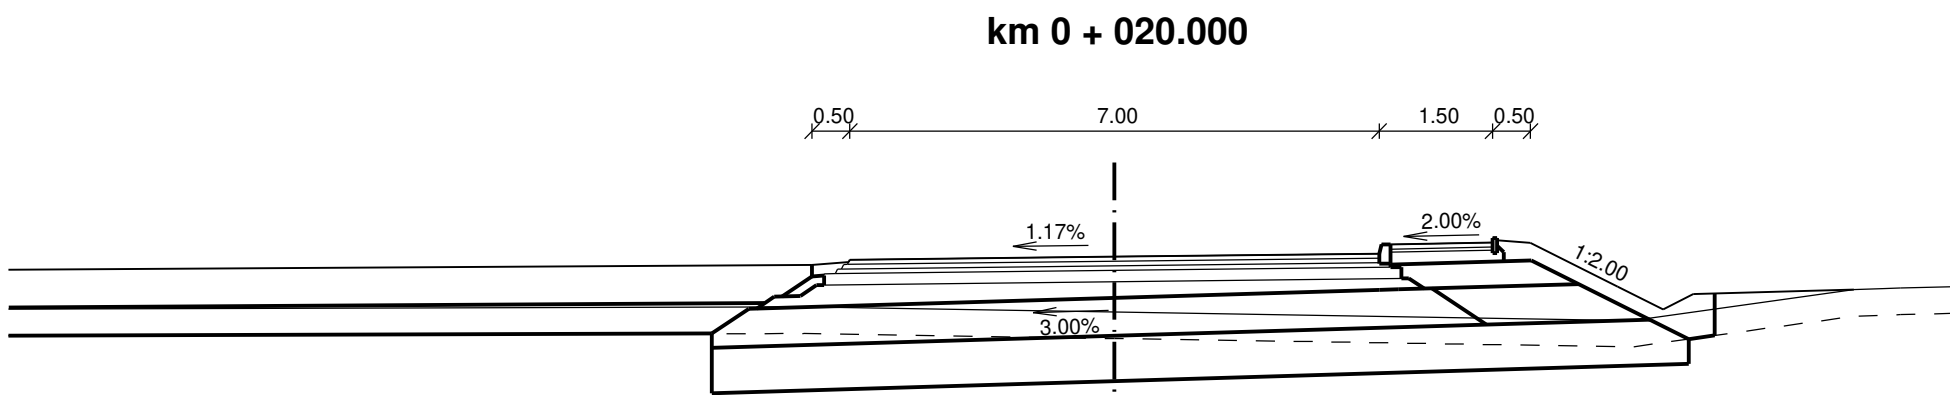

	S. R.	219 m
PROJEKTOVANÝ STAV ODSAZENÍ OD OSY	-4.00 222.55 -3.52 222.58 -3.50 222.61	0.00 222.65 3.50 222.70 3.53 222.82 3.65 222.82 5.00 222.84 5.00 222.90 5.06 222.90 5.06 222.87 5.50 222.84 6.65 222.26 7.25 221.96 7.85 222.26
STÁVAJÍCÍ TERÉN ODSAZENÍ OD OSY	-4.11 221.99	0.00 221.92 6.84 221.81 9.78 222.22 10.16 222.23 10.39 222.24

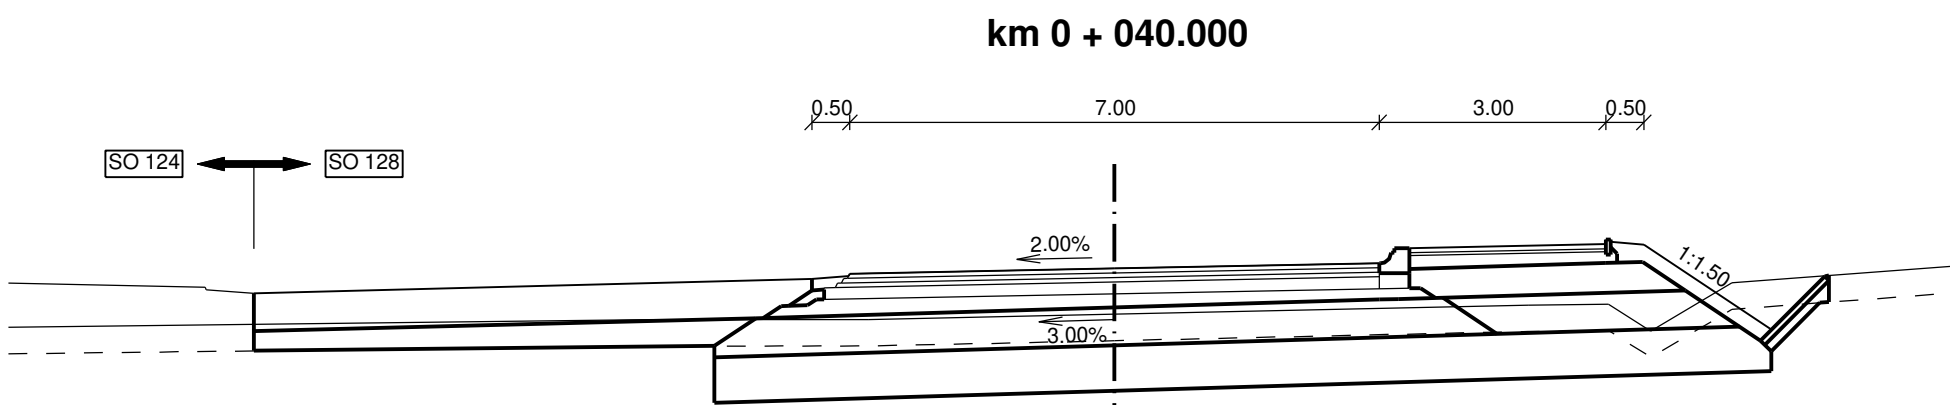

S. R. 219 m	
PROJEKTOVANÝ STAV ODSAZENÍ OD OSY	-4.00 222.53 -3.52 222.57 -3.50 222.60 0.00 222.67 3.50 222.74 3.70 222.94 3.90 222.94 6.50 222.99 6.50 223.05 6.56 223.05 6.56 223.02 7.00 222.98 8.69 221.86 9.45 222.57
STÁVAJÍCÍ TERÉN ODSAZENÍ OD OSY	-6.10 221.99 -3.25 222.00 0.00 222.07 5.47 222.18 6.53 222.20 7.09 221.84 8.17 222.48

Výškový systém: Bpv

SO 128 Obratiště BUS Martinovice**Objednatel:**

**ŘEDITELSTVÍ
SILNIC
A DÁLNIC**

Ředitelství silnic a dálnic s. p.

Čerčanská 2023/12, Krč, 140 00 Praha 4

Zhotovitel:

**Valbek, spol. s r.o.**

Vaňurova 505/17
460 07 Liberec 3

HIP:

ING. T. KLIMENT

	Vypracoval	M. KOŘÍNEK		Zak. číslo	21-LI13-001
	Zodp. projektant	ING. T. KLIMENT		Datum	02/2025
	Tech. kontrola	ING. M. HANŽL		Stupeň	PDPS
	Akce I/16 MLADÁ BOLESLAV - MARTINOVICE			Počet formátů	3 x A4
				Měřítko	1 : 100
			Č. přílohy	Paré	
Zhotovitel: Valbek, spol. s r.o. Vaňurova 505/17 460 07 Liberec 3	Příloha PŘÍČNÉ ŘEZY			5	