


SO 130 - PŘELOŽKA MÍSTNÍ KOMUNIKACE V km 1,713
SITUACE, M 1 : 1000

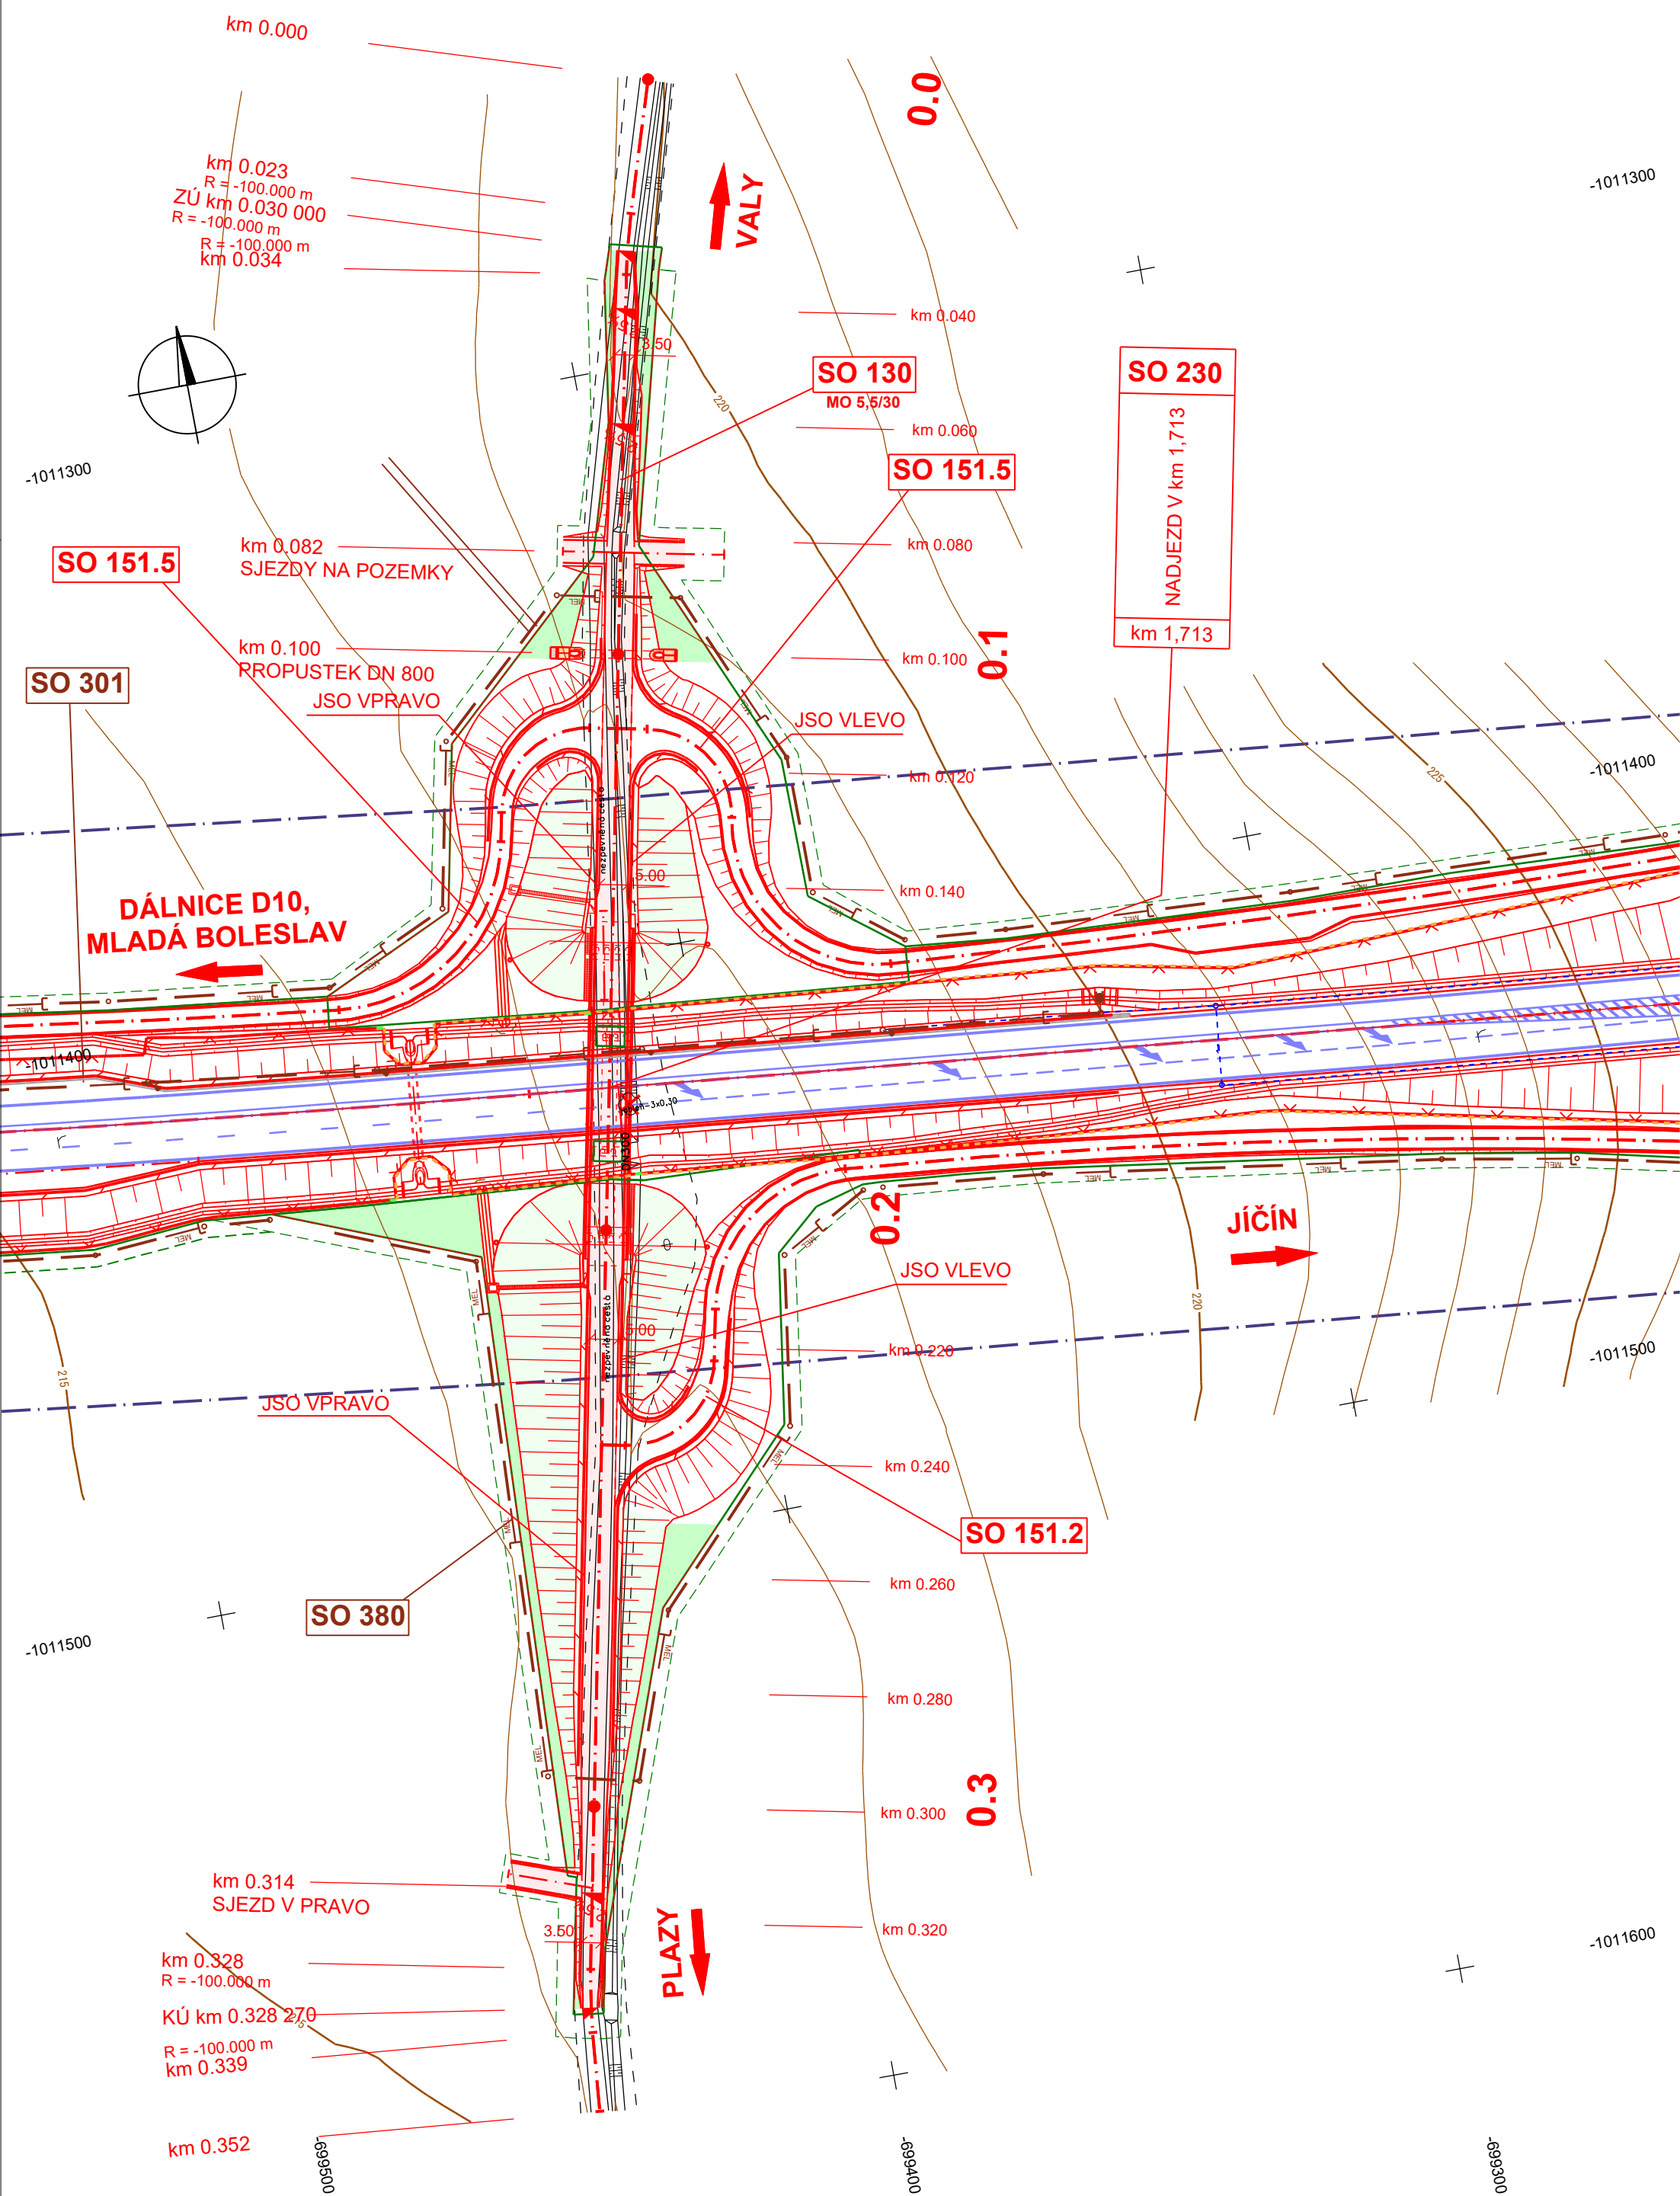

LEGENDA:

PLOCHY

	VOZOVKA - POLNÍ CESTY
	SVAHY VÝKOPU
	SVAHY NÁSYPU
	VEGETAČNÍ ÚPRAVY

KATASTR NEMOVITOSTÍ


 HRANICE K.Ú.
 HRANICE PARCEL
 TRVALÝ ZÁBOR
 DOČASNÝ ZÁBOR

NOVÉ IS

	DEŠŤOVÁ KANALIZACE
	MELIORACE
	VÝTLAK
	VODOVOD
	NADZEMNÍ VEDENÍ NN
	NADZEMNÍ VEDENÍ VN
	PODZEMNÍ VEDENÍ NN
	PODZEMNÍ SDĚLOVACÍ VEDENÍ
	PLYNOVOD - STL

STÁVAJÍCÍ IS - INFORMATIVNÍ ZÁKRES

	PODZEMNÍ VEDENÍ NN
	PODZEMNÍ VEDENÍ VN
	NADZEMNÍ VEDENÍ NN
	NADZEMNÍ VEDENÍ VN
	NADZEMNÍ VEDENÍ VVN
	DEŠŤOVÁ KANALIZACE
	PLYNOVOD - STL
	PODZEMNÍ SDĚLOVACÍ VEDENÍ
	VODOVOD

Souřadnicový systém: S-JTSK
Výškový systém: Bpv

SO 130	Přeložka místní komunikace v km 1,713
---------------	---------------------------------------

Objednatel:

ŘEDITELSTVÍ SILNIC A DÁLNIC

Ředitelství silnic a dálnic s. p.
Čerčanská 2023/12, Krč, 140 00 Praha 4

Zhotovitel:



Valbek, spol. s r.o.
Vaňurova 505/17
460 07 Liberec 3



Vypracoval	P. BARTUSEK	Zak. číslo	21-L113-001
Zodp. projektant	ING. T. KLIMENT	Datum	02/2025
Tech. kontrola	ING. M. HANŽL	Stupeň	PDPS
I/16 MLADÁ BOLESLAV - MARTINOVICE		Počet formátů	6 x A4
		Měřítko	1 : 1 000
		Č. přílohy	Paré
Příloha SITUACE		2	

Zhotovitel:
Valbek, spol. s r.o.
Vaňurova 505/17
460 07 Liberec 3

Příloha	SITUACE
---------	---------

2