


SO 130 - PŘELOŽKA MÍSTNÍ KOMUNIKACE V km 1,317

PODÉLNÝ PROFIL, M 1 : 1 000 / 100

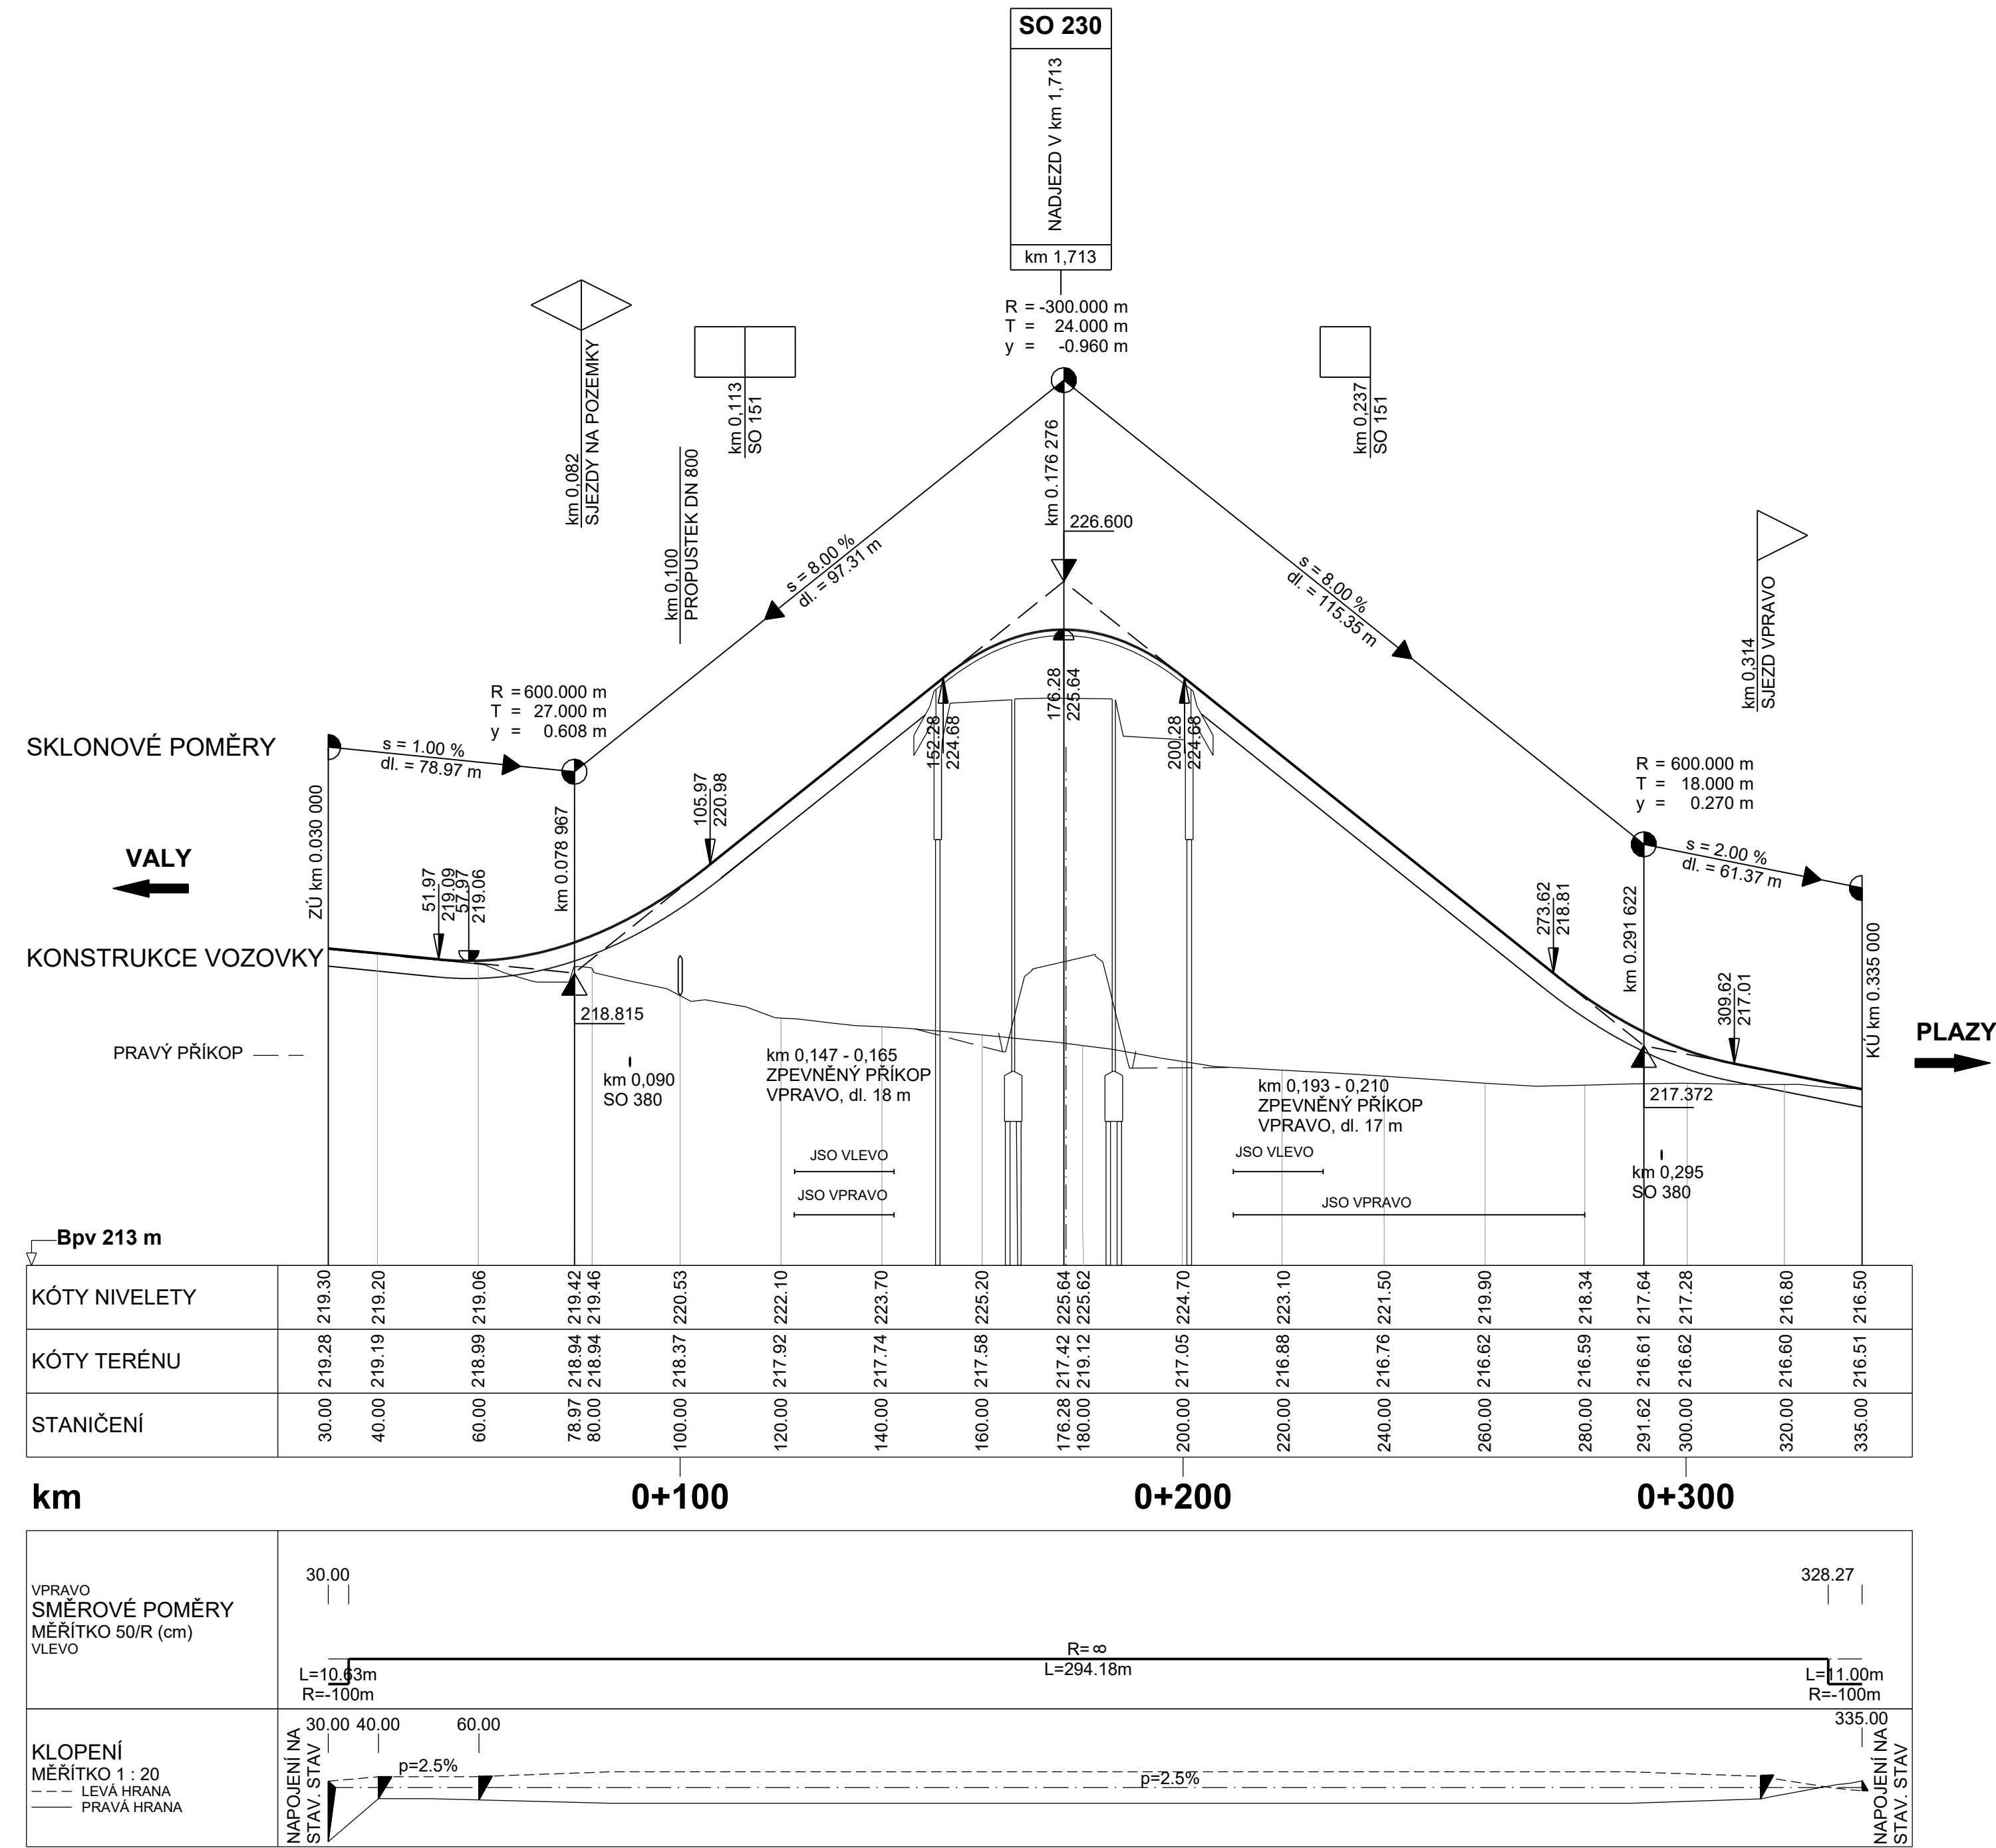

Výškový systém: Bpv

SO 130 Přeložka místní komunikace v km 1,317

Objednatel:

 **ŘEDITELSTVÍ
SILNIC
A DÁLNIC**

Ředitelství silnic a dálnic s. p.
Čerčanská 2023/12, Krč, 140 00 Praha 4

Zhotovitel:

 **Valbek**

Valbek, spol. s r.o.
Vaňurova 505/17
460 07 Liberec 3

	Vypracoval	P. BARTUSEK		Zak. číslo	21-LI13-001
	Zodp. projektant	ING. T. KLIMENT		Datum	02/2025
	Tech. kontrola	ING. M. HANŽL		Stupeň	PDPS
	Akce I/16 MLADÁ BOLESLAV - MARTINOVICE			Počet formátů	6 x A4
				Měřítko	1:1 000/100
Zhotovitel: Valbek, spol. s r.o. Vaňurova 505/17 460 07 Liberec 3	Příloha PODÉLNÝ PROFIL			Č. přílohy	Paré
				3	