


SO 130 - PŘELOŽKA MÍSTNÍ KOMUNIKACE V km 1,713
VZOROVÝ PŘÍČNÝ ŘEZ, M 1 : 50

KATEGORIE MO1 5,5/30
JEDNOPRUHOVÁ, OBOUSMĚRNÁ
TŘÍDA DOPRAVNÍHO ZATÍŽENÍ VI
NÁVRHOVÁ ÚROVEŇ PORUŠENÍ D1
TYP PODLOŽÍ PIII (D1-A-2)

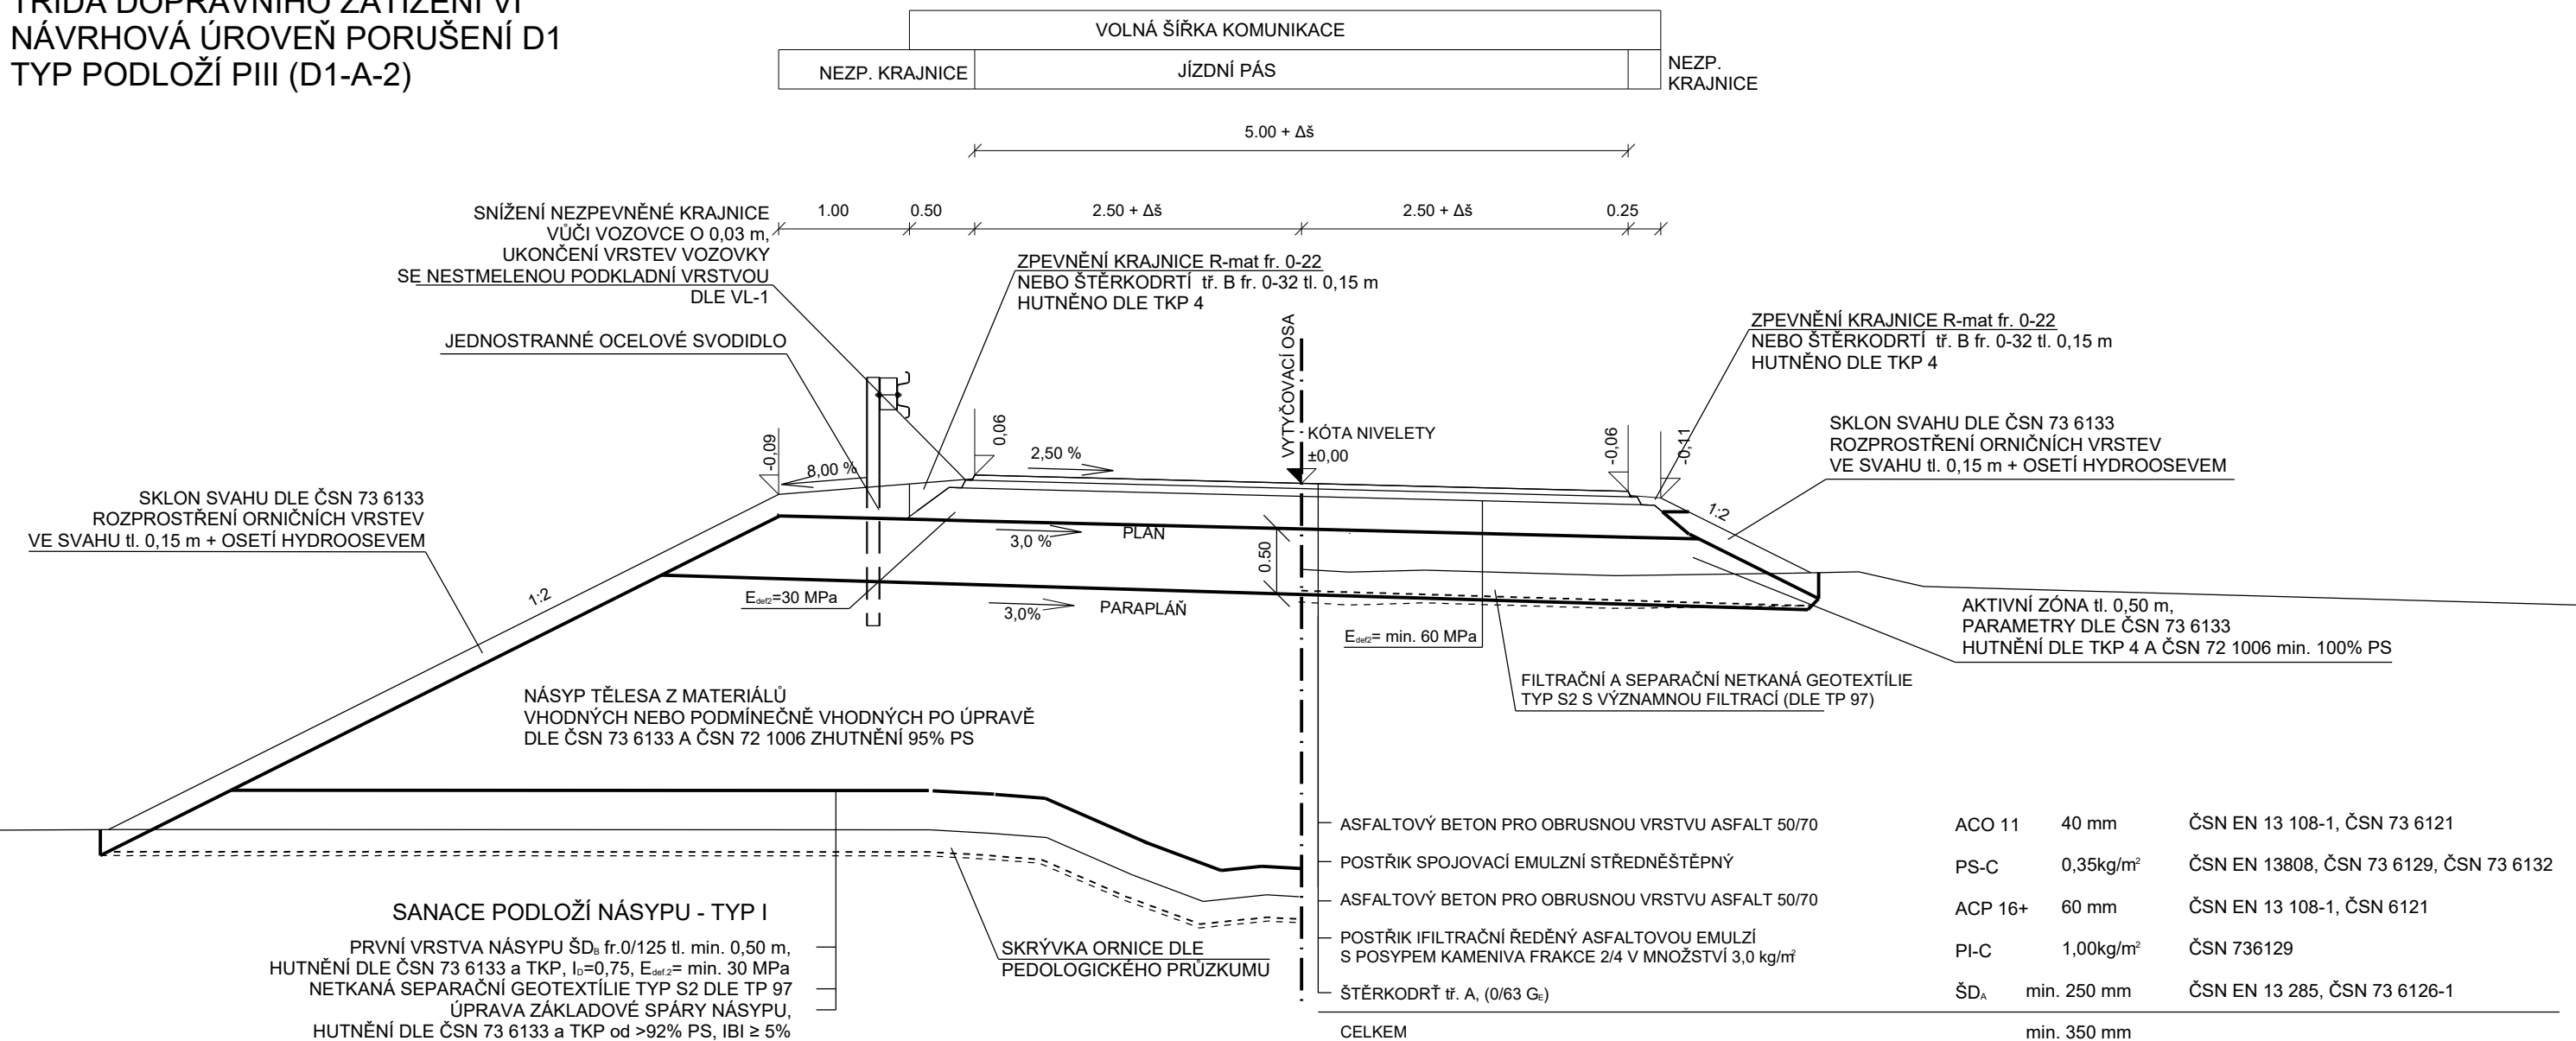

Výškový systém: Bpv

SO 130 Přeložka místní komunikace v km 1,713**Objednatel:**

ŘEDITELSTVÍ SILNIC A DÁLNIC

Ředitelství silnic a dálnic s. p.
Čerčanská 2023/12, Krč, 140 00 Praha 4

Zhotovitel:

Valbek, spol. s r.o.
Vaňurova 505/17
460 07 Liberec 3

	Vypracoval	P. BARTUSEK		Zak. číslo	21-L113-001
	Zodp. projektant	ING .T. KLIMENT		Datum	02/2025
	Tech. kontrola	ING. M. HANŽL		Stupeň	PDPS
	Akce I/16 MLADÁ BOLESLAV - MARTINOVICE			Počet formátů	3 x A4
				Měřítko	1 : 50
Zhotovitel: Valbek, spol. s r.o. Vaňurova 505/17 460 07 Liberec 3	Příloha VZOROVÝ PŘÍČNÝ ŘEZ			Č. přílohy	Paré
				4	