SO 130 - PŘELOŽKA MÍSTNÍ KOMUNIKACE V km 1,713
PŘÍČNÉ ŘEZY, M 1 : 100

km 0 + 040.000

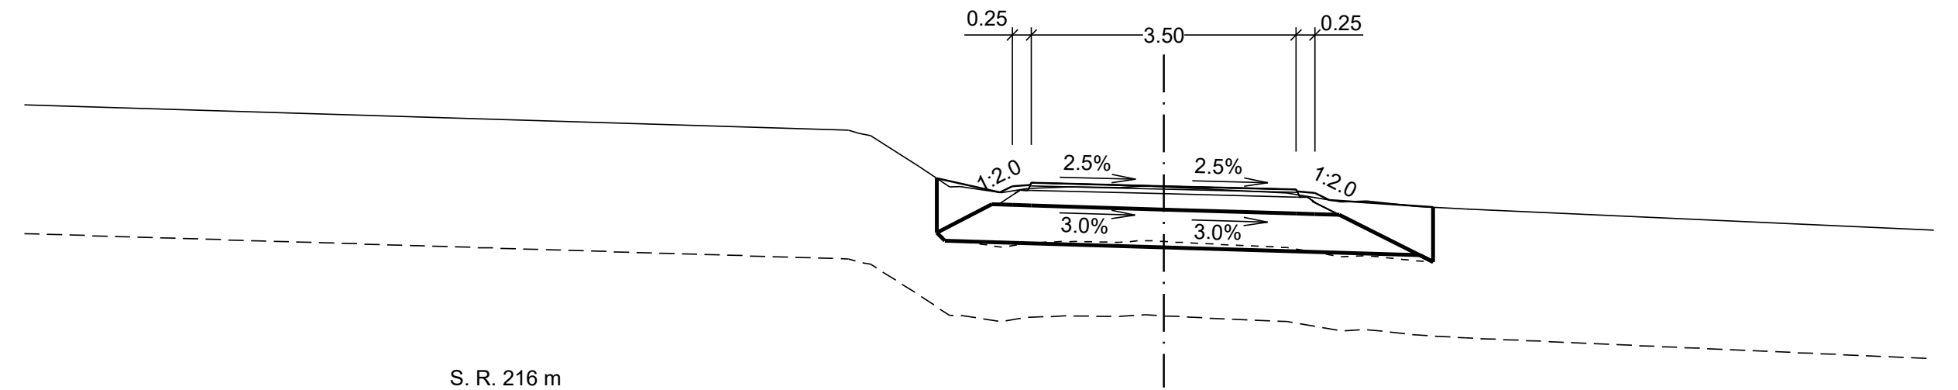
0.25
3.50
0.25
1:2.0
2.5%
2.5%
1:2.0
3.0%
3.0%
S. R. 216 m

PROJEKTOVANÝ STAV	219.31	219.11	219.20	219.22	219.25	219.20	219.16	219.13	219.12	219.02	218.93
ODSAZENÍ OD OSY	-3.00	-2.14	-2.00	-1.76	-1.75	0.00	1.75	1.76	2.00	2.19	3.56

STÁVAJÍCÍ TERÉN	219.94	219.90	219.87	219.47	219.20	219.20	219.12	219.17	219.19	219.18	219.21	219.19	219.15	219.12	218.99	219.01	218.94	218.90
ODSAZENÍ OD OSY	-4.17	-4.03	-3.88	-3.24	-2.83	-2.70	-2.14	-1.80	-1.25	-0.59	-0.25	0.00	0.92	1.63	2.34	2.68	3.35	3.99

km 0 + 060.000

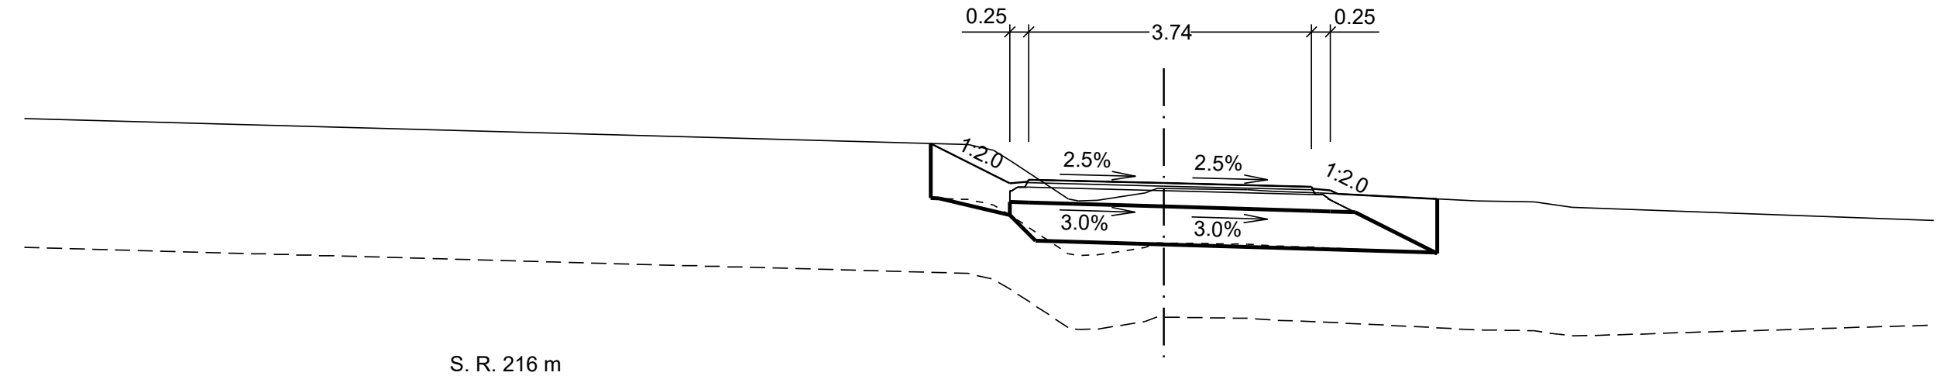
0.25
3.74
0.25
1:2.0
2.5%
2.5%
1:2.0
3.0%
3.0%
S. R. 216 m

PROJEKTOVANÝ STAV	219.58	219.06	219.07	219.10	219.06	219.01	218.98	218.96	218.91	218.85
ODSAZENÍ OD OSY	-3.08	-2.03	-1.79	-1.78	0.00	1.95	1.96	2.20	2.29	3.62

STÁVAJÍCÍ TERÉN	219.57	219.49	219.35	218.85	218.82	218.83	218.93	218.99	218.97	218.95	218.93	218.82	218.81	218.76	218.74
ODSAZENÍ OD OSY	-2.58	-2.25	-2.02	-1.26	-1.12	-0.87	-0.25	-0.09	1.11	1.44	2.06	4.14	4.90	5.23	5.40

km 0 + 080.000

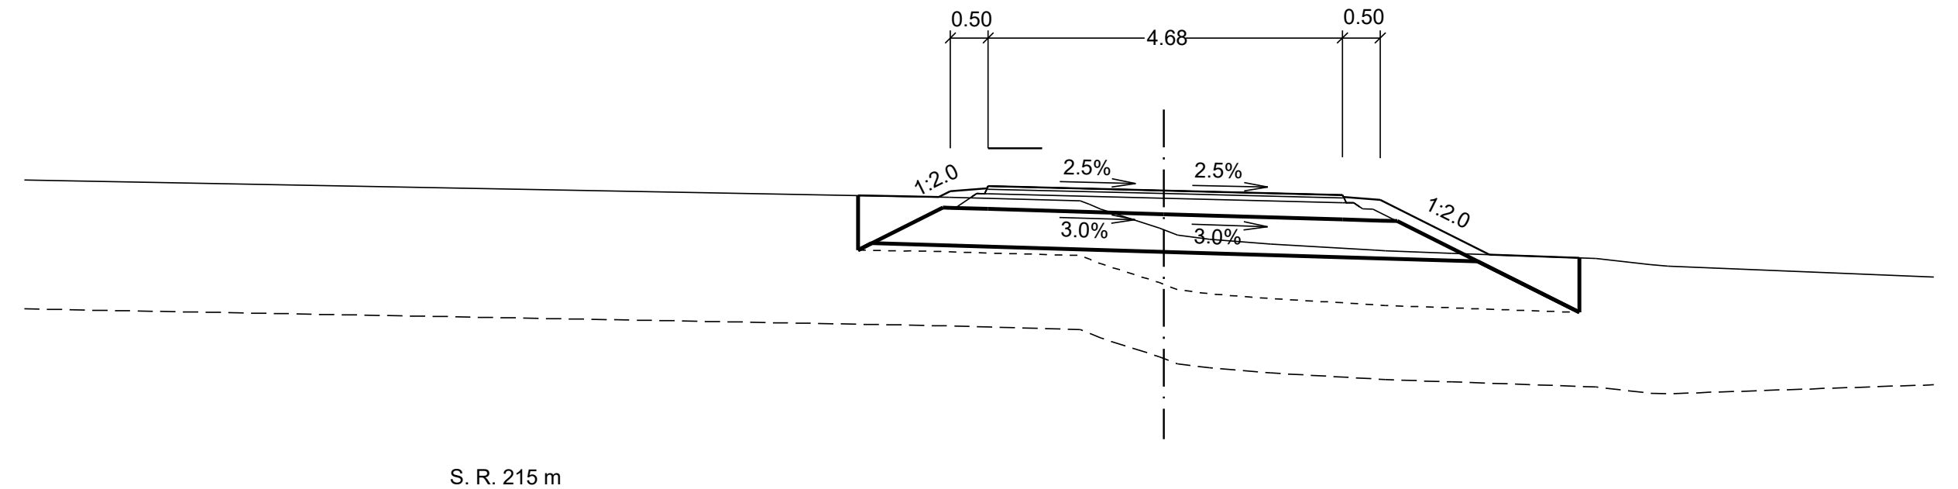
0.50
4.68
0.50
1:2.0
2.5%
2.5%
1:2.0
3.0%
3.0%
S. R. 215 m

PROJEKTOVANÝ STAV	219.39	219.38	219.45	219.49	219.52	219.46	219.40	219.37	219.34	218.61	218.57
ODSAZENÍ OD OSY	-4.04	-2.98	-2.82	-2.33	-2.32	0.00	2.36	2.37	2.86	4.31	5.50

STÁVAJÍCÍ TERÉN	219.37	219.32	219.28	219.21	218.96	218.87	218.82	218.75	218.67	218.66	218.63	218.56	218.48	218.46
ODSAZENÍ OD OSY	-2.84	-1.11	-0.98	-0.83	-0.06	0.18	0.60	1.41	2.80	2.93	3.81	5.72	6.43	6.67

km 0 + 100.000

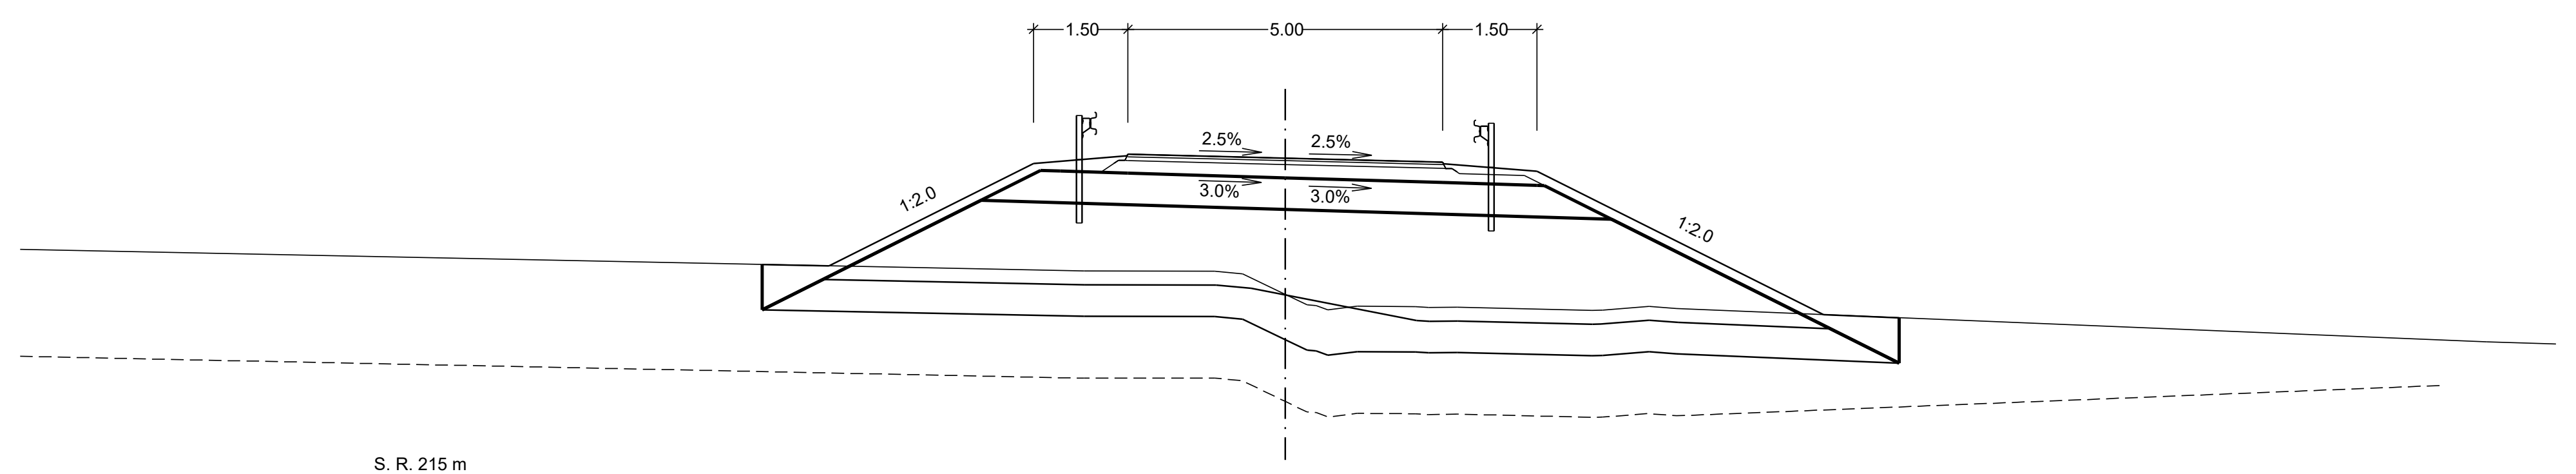
1.50
5.00
1.50
2.5%
2.5%
3.0%
3.0%
1:2.0
1:2.0
S. R. 215 m

PROJEKTOVANÝ STAV	218.84	218.82	220.44	220.56	220.59	220.53	220.47	220.44	220.32	218.04	217.99
ODSAZENÍ OD OSY	-8.31	-7.25	-4.00	-2.51	-2.50	0.00	2.50	2.51	4.00	8.55	9.76

STÁVAJÍCÍ TERÉN	218.74	218.73	218.69	218.37	218.20	218.19	218.12	218.18	218.17	218.16	218.16	218.11	218.12	218.17	218.14	217.61
ODSAZENÍ OD OSY	-3.20	-1.12	-0.68	0.00	0.35	0.49	0.68	1.14	2.07	2.28	2.74	4.88	5.05	5.78	6.22	19.10

km 0 + 120.000

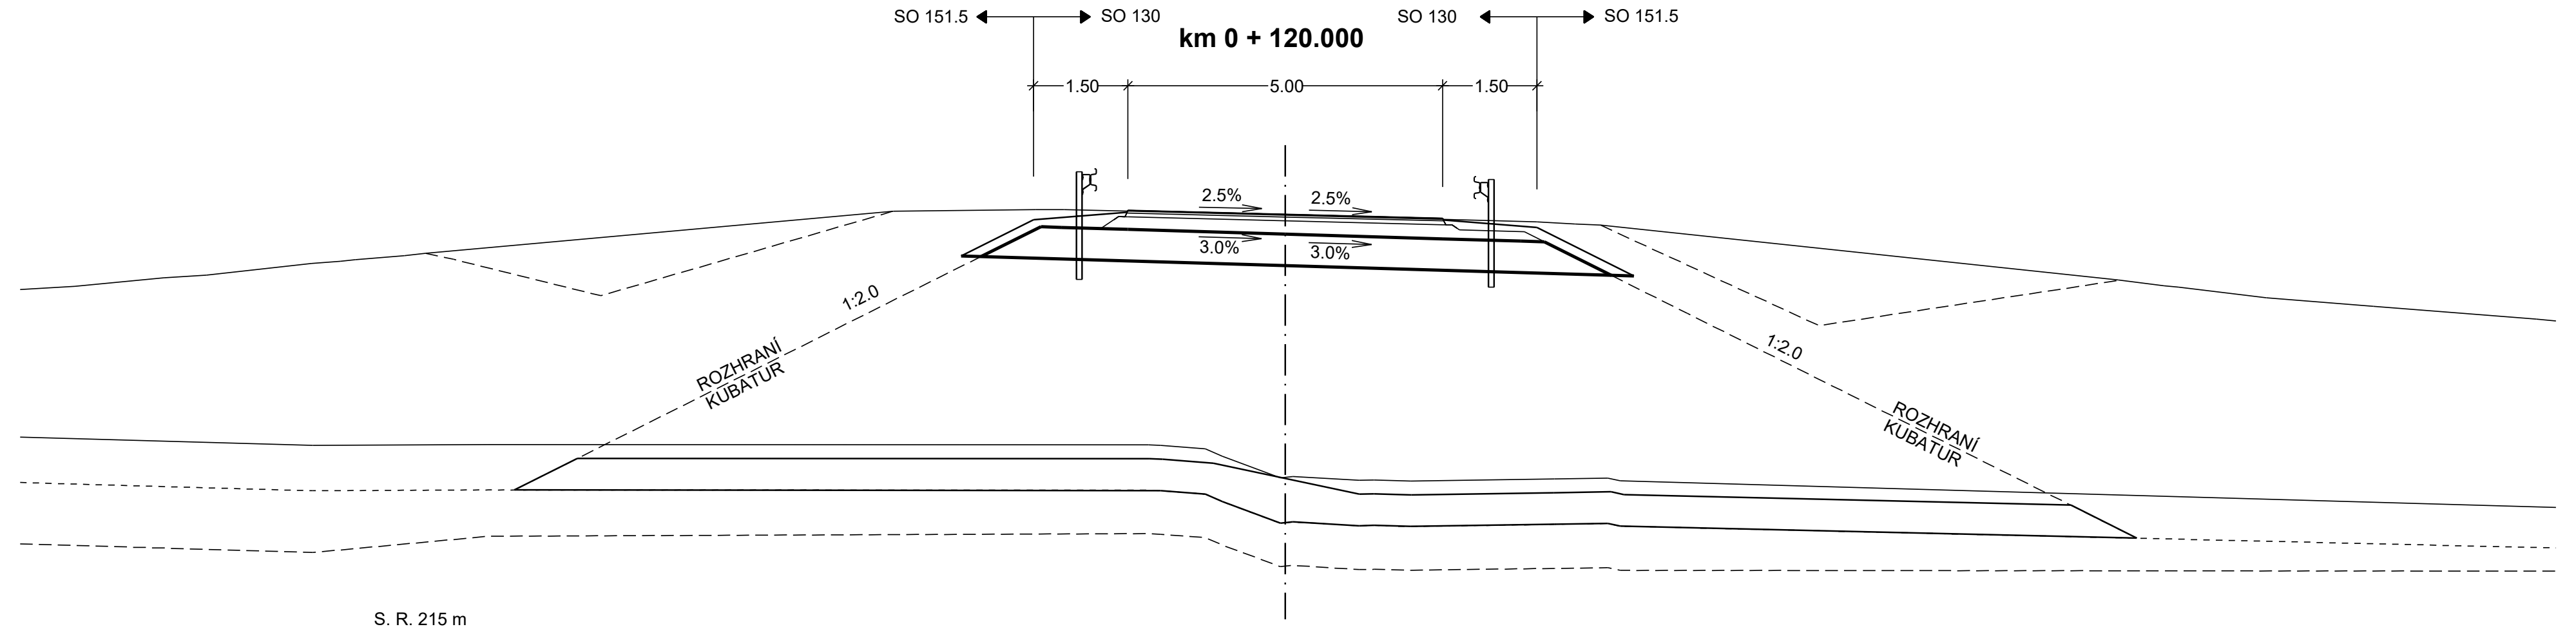
SO 151.5
SO 130
SO 130
SO 151.5
1.50
5.00
1.50
2.5%
2.5%
3.0%
3.0%
1:2.0
ROZHRANÍ KUBATUR
1:2.0
ROZHRANÍ KUBATUR
S. R. 215 m

PROJEKTOVANÝ STAV	218.44	218.44	221.44	222.01	222.16	222.16	222.10	222.04	222.01	221.89	220.66	217.66	217.63
ODSAZENÍ OD OSY	-12.62	-11.51	-5.51	-4.00	-2.51	-2.50	0.00	2.50	2.51	4.00	6.68	12.68	13.76

STÁVAJÍCÍ TERÉN	218.44	218.44	218.43	218.37	218.26	217.91	217.93	217.87	217.88	217.86	217.89	217.91	217.86
ODSAZENÍ OD OSY	-12.66	-2.17	-1.98	-1.27	-1.00	-0.08	0.12	1.17	1.41	2.00	4.28	5.13	5.32

km 0 + 140.000

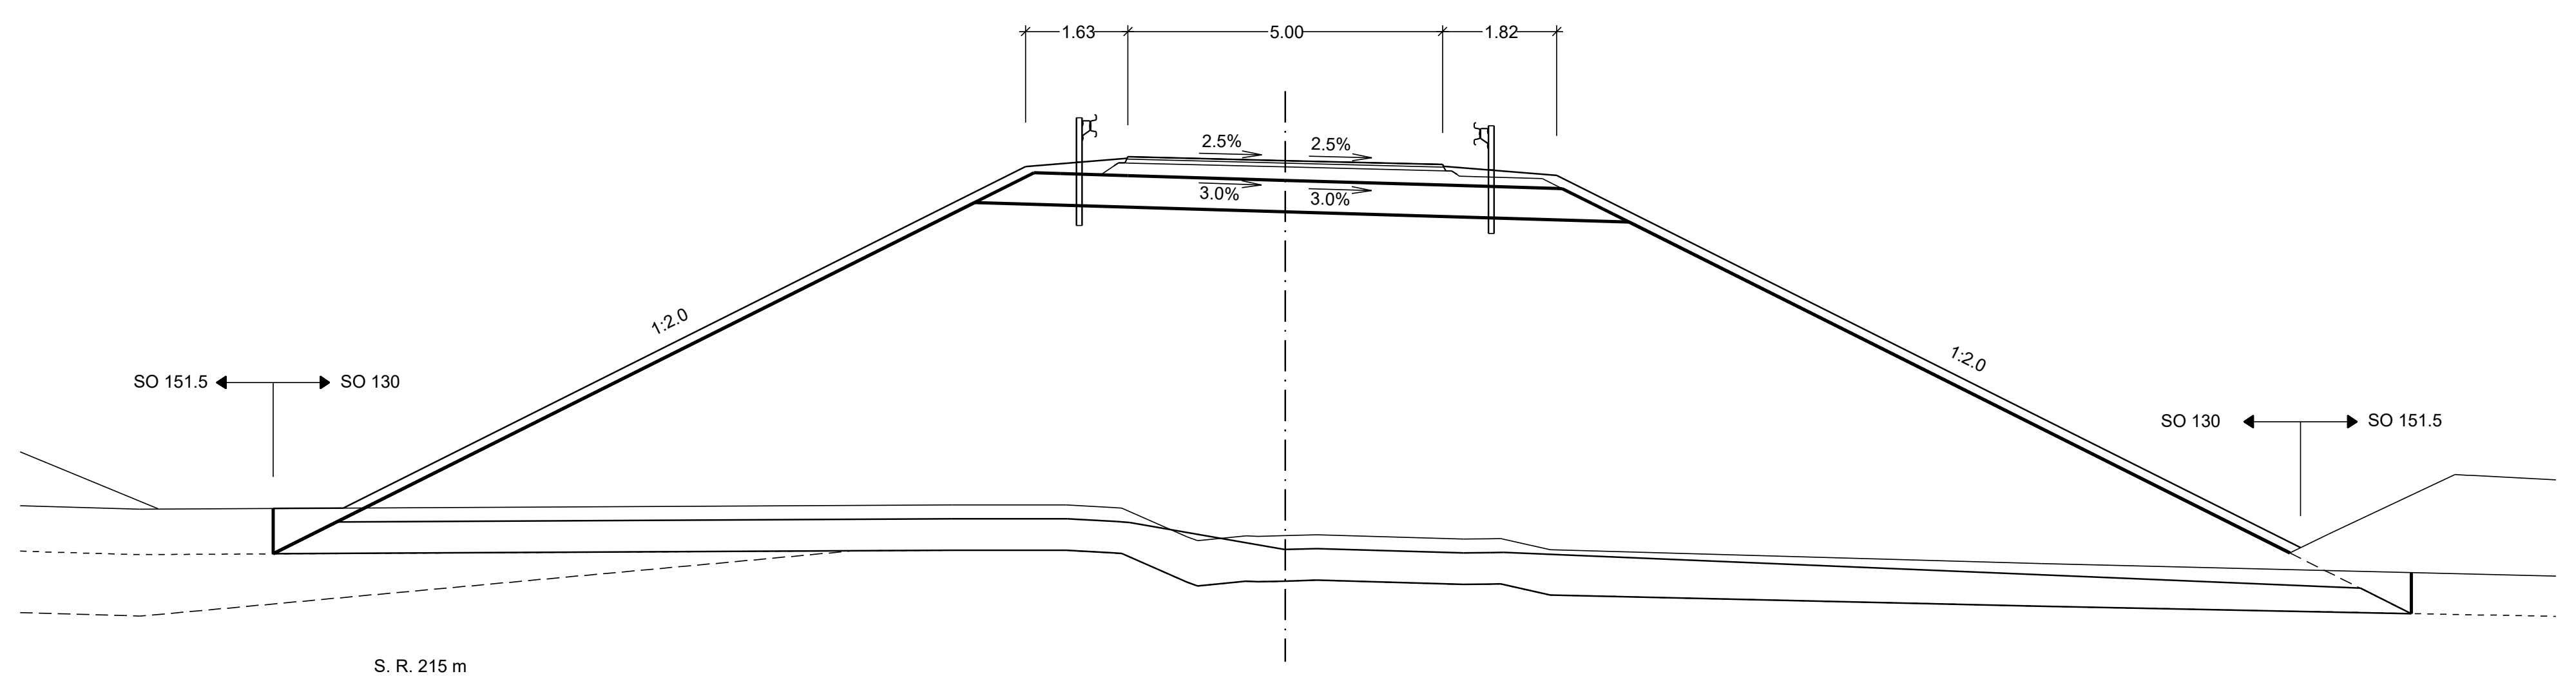
1.63
5.00
1.82
2.5%
2.5%
3.0%
3.0%
1:2.0
1:2.0
SO 151.5
SO 130
SO 130
SO 151.5
S. R. 215 m

PROJEKTOVANÝ STAV	221.18	223.60	223.73	223.76	223.70	223.64	223.61	223.46	223.17	220.17	217.17	217.15
ODSAZENÍ OD OSY	-9.37	-4.13	-2.51	-2.50	0.00	2.50	2.51	4.32	5.15	11.15	17.15	18.16

STÁVAJÍCÍ TERÉN	218.23	218.23	218.19	218.18	217.72	217.66	217.74	217.73	217.74	217.76	217.69	217.70	217.70	217.52	217.30
ODSAZENÍ OD OSY	-5.30	-3.48	-2.72	-2.60	-1.56	-1.39	-0.62	-0.43	0.00	0.50	2.83	3.26	3.42	4.21	12.02

km 0 + 220.000

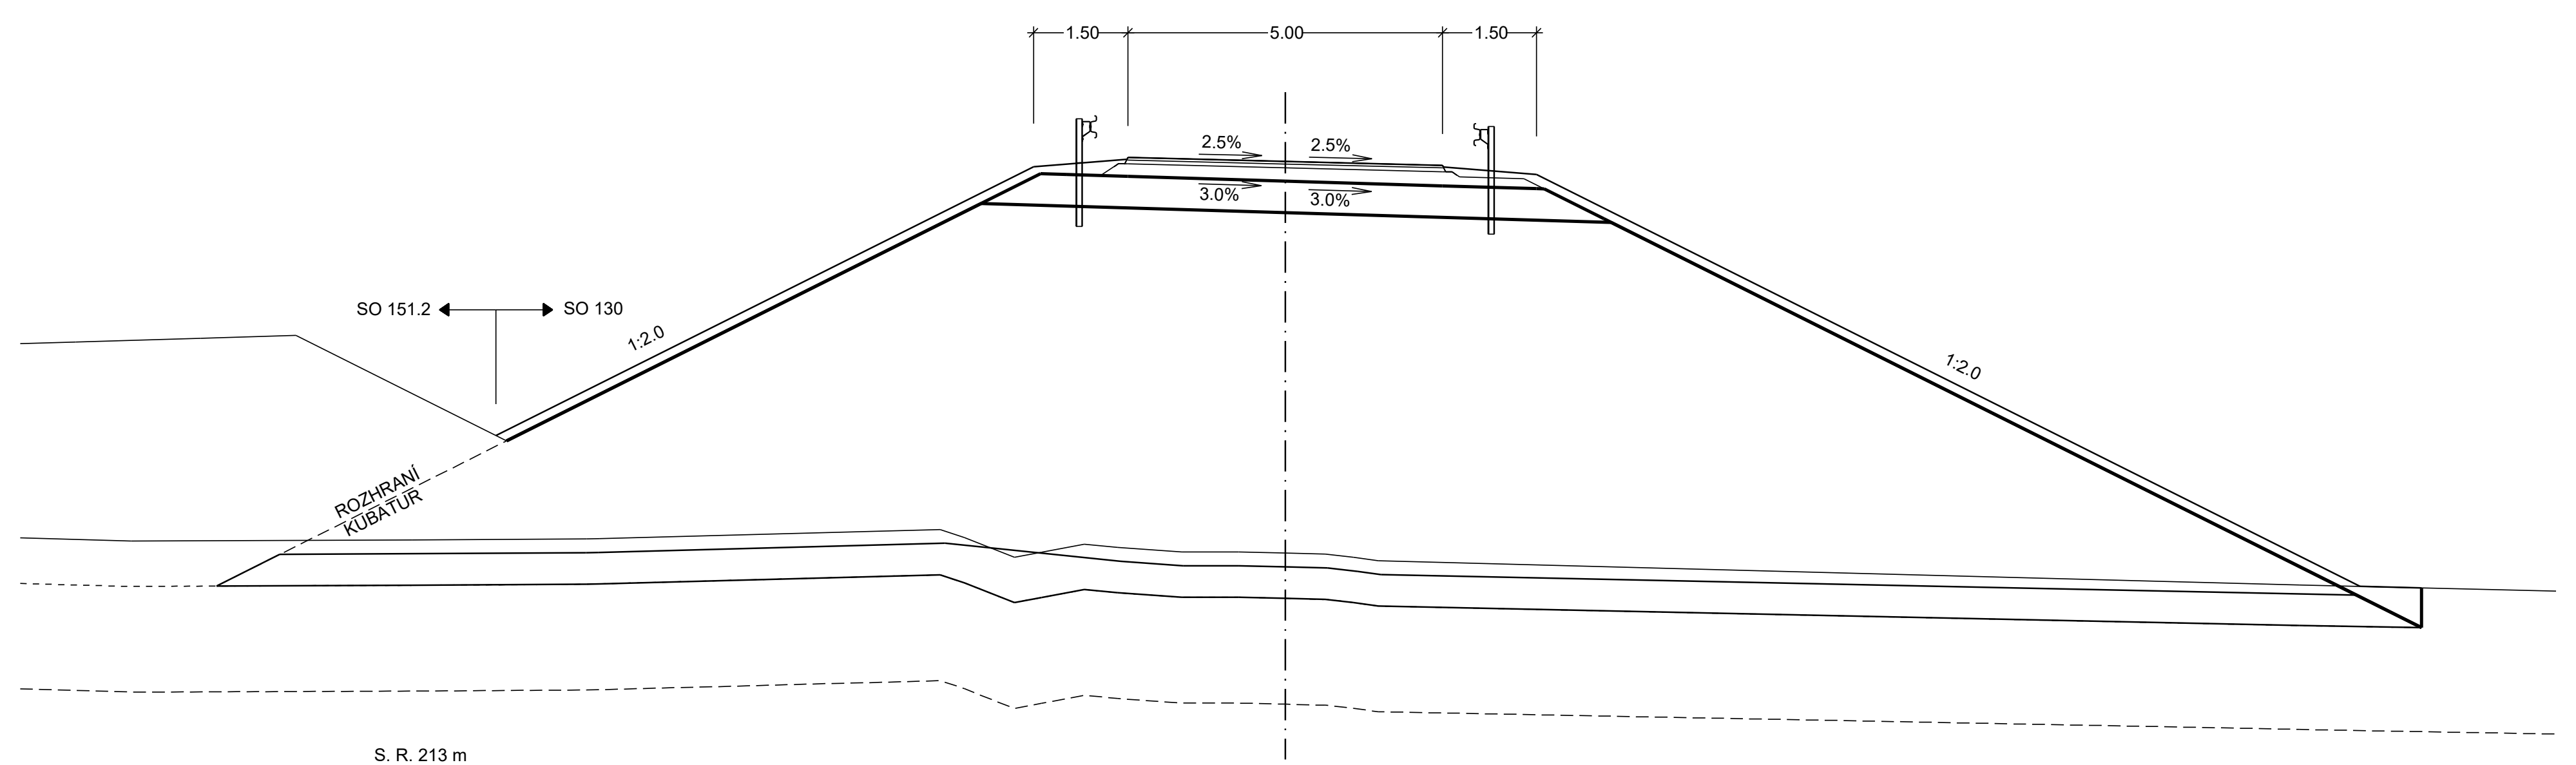
1.50
5.00
1.50
2.5%
2.5%
3.0%
3.0%
SO 151.2
SO 130
1:2.0
1:2.0
ROZHRANÍ KUBATUR
S. R. 213 m

PROJEKTOVANÝ STAV	220.08	223.08	223.02	223.13	223.16	223.10	223.04	223.01	222.89	222.34	219.34	216.35	216.33
ODSAZENÍ OD OSY	-10.24	-4.24	-4.00	-2.51	-2.50	0.00	2.50	2.50	4.00	5.31	11.31	17.08	18.06

STÁVAJÍCÍ TERÉN	217.09	217.10	217.11	217.25	217.12	216.81	216.89	217.02	216.97	216.90	216.90	216.88	216.86	216.81	216.76	216.37
ODSAZENÍ OD OSY	-13.88	-11.11	-10.90	-5.48	-5.10	-4.30	-3.87	-3.19	-2.66	-1.64	-0.74	0.00	0.64	1.08	1.48	16.11

km 0 + 240.000

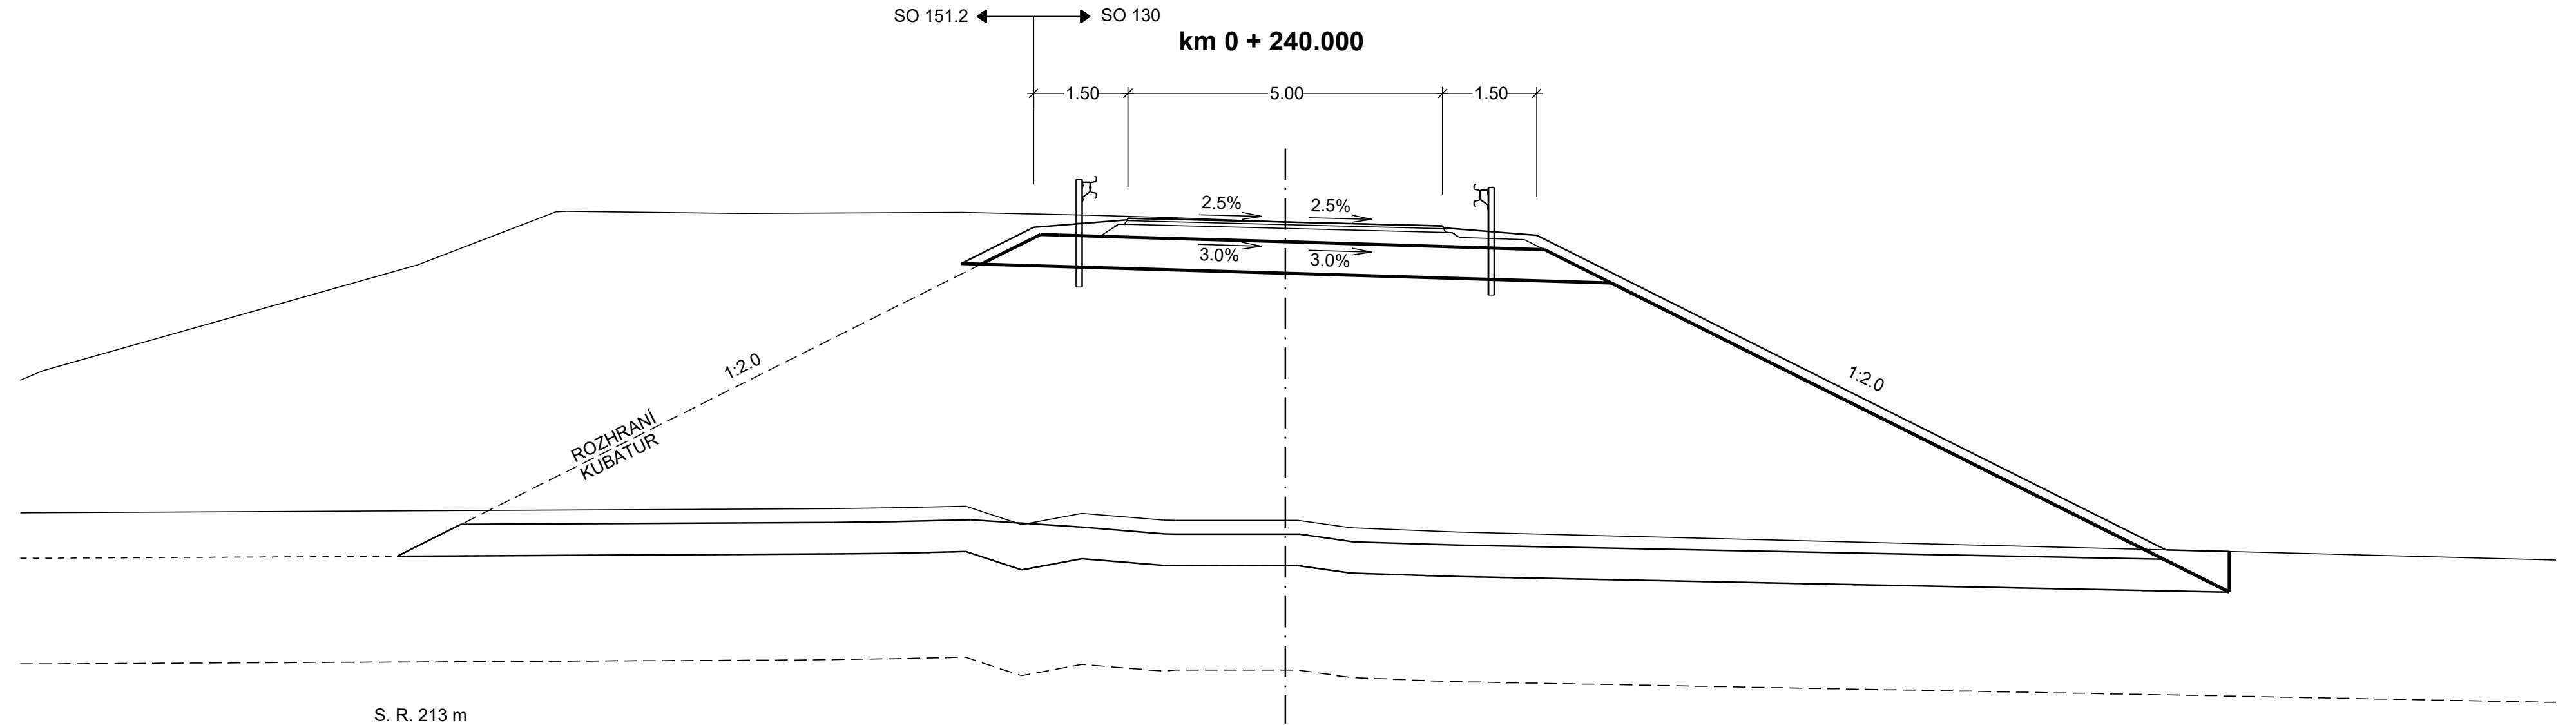
SO 151.2
SO 130
1.50
5.00
1.50
2.5%
2.5%
3.0%
3.0%
1:2.0
ROZHRANÍ KUBATUR
1:2.0
S. R. 213 m

PROJEKTOVANÝ STAV	216.91	216.92	219.92	221.42	221.53	221.56	221.50	221.44	221.43	221.29	219.29	216.29	216.26
ODSAZENÍ OD OSY	-14.49	-13.37	-7.37	-4.00	-2.51	-2.50	0.00	2.50	2.51	4.00	8.22	14.00	15.00

STÁVAJÍCÍ TERÉN	216.95	216.96	216.99	216.70	216.87	216.77	216.76	216.76	216.76	216.64	216.58	216.27
ODSAZENÍ OD OSY	-7.18	-6.25	-5.08	-4.19	-3.23	-1.94	-1.74	0.00	0.20	1.05	2.73	14.86

km 0 + 260.000

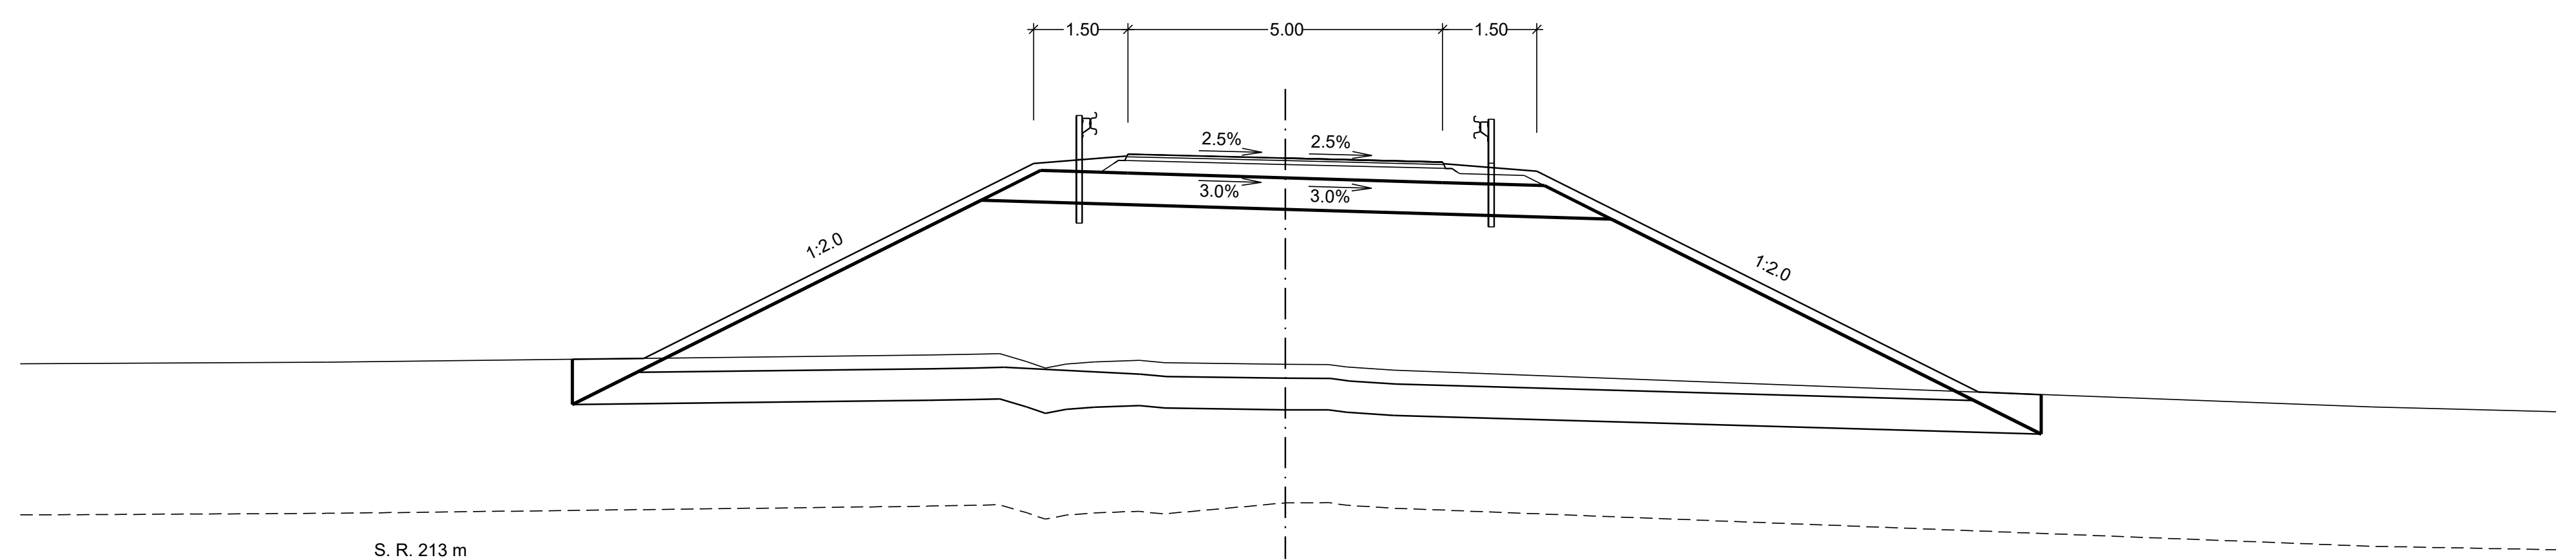
1.50
5.00
1.50
2.5%
2.5%
3.0%
3.0%
1:2.0
1:2.0
S. R. 213 m

PROJEKTOVANÝ STAV	216.71	216.72	219.72	219.82	219.93	219.96	219.90	219.84	219.83	219.69	219.17	216.18	216.14
ODSAZENÍ OD OSY	-11.33	-10.20	-4.57	-4.00	-2.51	-2.50	0.00	2.50	2.51	4.00	5.25	11.02	12.02

STÁVAJÍCÍ TERÉN	216.77	216.79	216.80	216.67	216.57	216.63	216.66	216.69	216.65	216.62	216.62	216.58	216.53	215.95
ODSAZENÍ OD OSY	-5.66	-4.92	-4.53	-4.11	-3.81	-3.48	-3.03	-2.32	-1.91	0.00	0.69	0.98	1.73	17.27

km 0 + 280.000

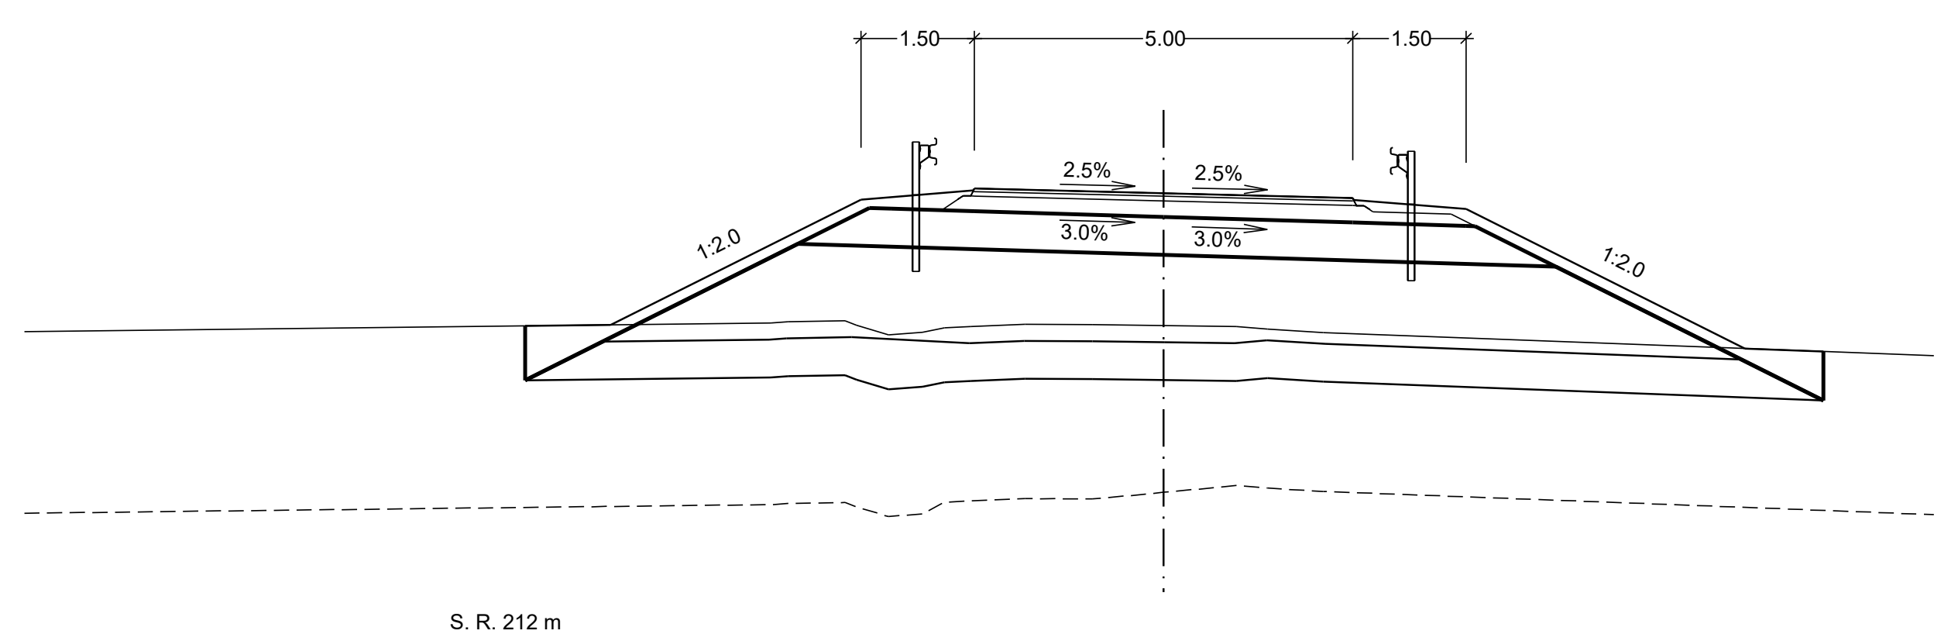
1.50
5.00
1.50
2.5%
2.5%
3.0%
3.0%
1:2.0
1:2.0
S. R. 212 m

PROJEKTOVANÝ STAV	216.58	216.60	218.25	218.37	218.40	218.34	218.27	218.24	218.13	216.28	216.24
ODSAZENÍ OD OSY	-8.44	-7.31	-4.00	-2.51	-2.50	0.00	2.50	2.51	4.00	7.69	8.72

STÁVAJÍCÍ TERÉN	216.62	216.64	216.65	216.59	216.46	216.50	216.56	216.58	216.60	216.60	216.59	216.57	216.54	216.49	216.25
ODSAZENÍ OD OSY	-5.20	-4.96	-4.21	-4.06	-3.64	-3.19	-2.90	-2.54	-1.83	-0.94	0.00	0.96	1.38	2.11	8.54

km 0 + 300.000

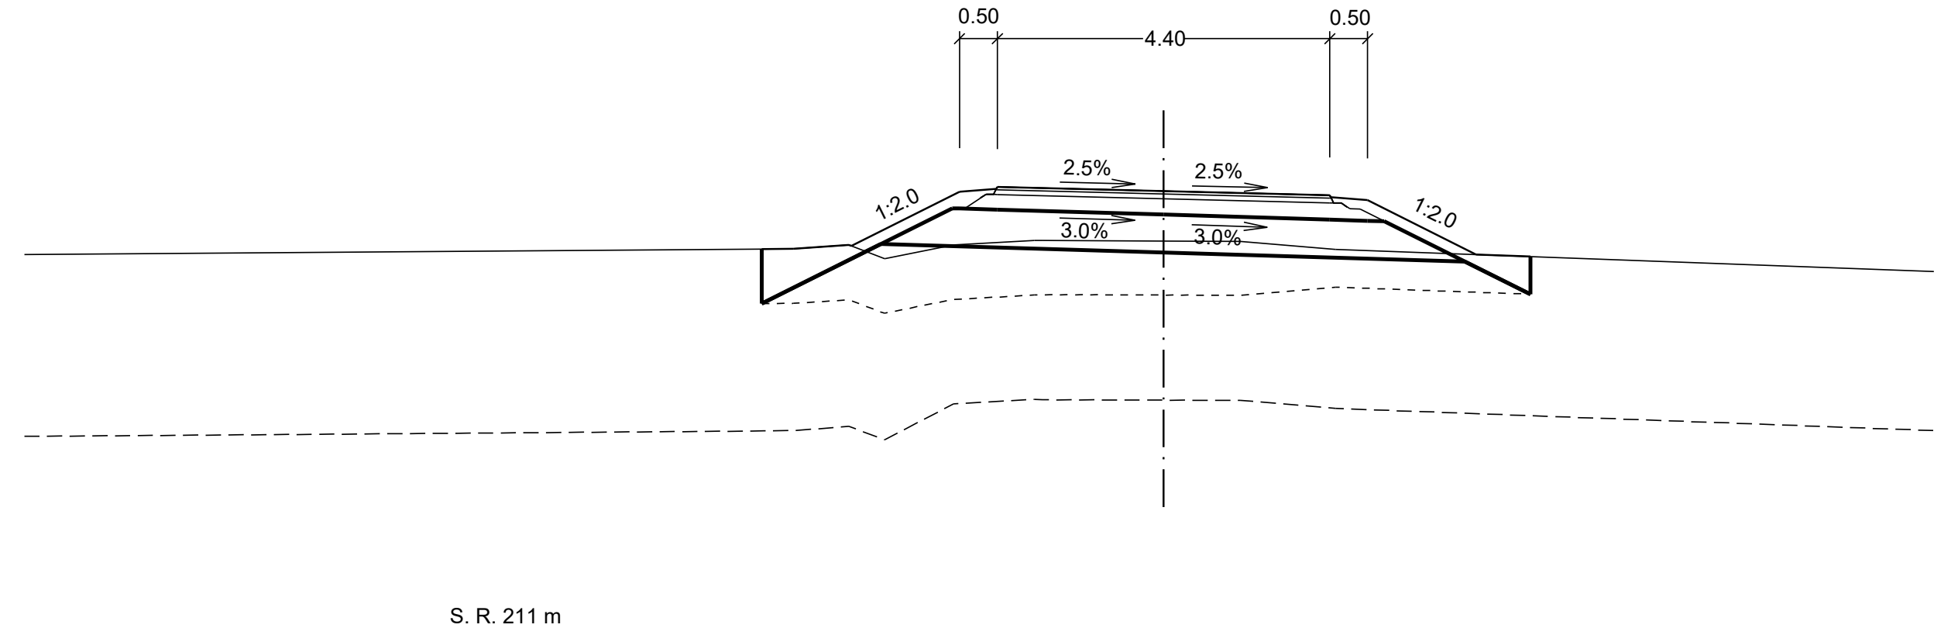
0.50
4.40
0.50
1:2.0
2.5%
2.5%
1:2.0
3.0%
3.0%
S. R. 211 m

PROJEKTOVANÝ STAV	216.52	216.56	217.27	217.31	217.34	217.28	217.23	217.20	217.16	216.44	216.42
ODSAZENÍ OD OSY	-5.31	-4.13	-2.70	-2.21	-2.20	0.00	2.20	2.21	2.70	4.13	4.85

STÁVAJÍCÍ TERÉN	216.52	216.52	216.57	216.39	216.57	216.63	216.63	216.62	216.62	216.51
ODSAZENÍ OD OSY	-5.29	-4.90	-4.16	-3.69	-2.78	-1.71	-1.60	0.00	1.01	2.27

km 0 + 320.000

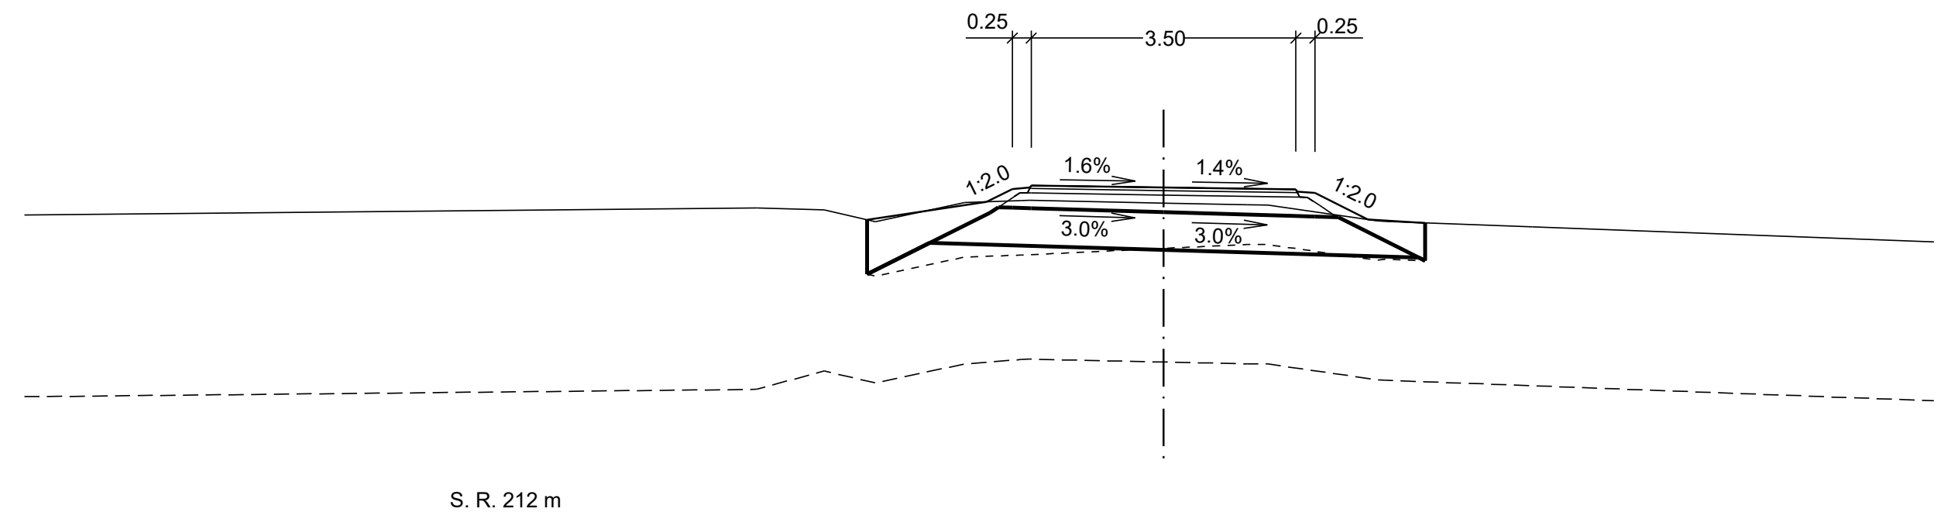
0.25
3.50
0.25
1:2.0
1.6%
1.4%
1:2.0
3.0%
3.0%
S. R. 212 m

PROJEKTOVANÝ STAV	216.38	216.62	216.79	216.80	216.83	216.80	216.78	216.75	216.73	216.38	216.34
ODSAZENÍ OD OSY	-3.92	-2.34	-2.00	-1.76	-1.75	0.00	1.75	1.76	2.00	2.70	3.46

STÁVAJÍCÍ TERÉN	216.54	216.51	216.35	216.61	216.63	216.64	216.60	216.58	216.58	216.37	216.36	216.28
ODSAZENÍ OD OSY	-5.37	-4.49	-3.81	-2.63	-1.88	-1.77	0.00	1.10	1.38	2.81	2.93	4.88

Výškový systém: Bpv

SO 130 Přeložka místní komunikace v km 1,713

Objednatel:

ŘEDITELSTVÍ SILNIC A DÁLNIC

Ředitelství silnic a dálnic s. p.
Čerčanská 2023/12, Krč, 140 00 Praha 4

Zhotovitel:

Valbek, spol. s r.o.
Vaňurova 505/17
460 07 Liberec 3

Vypracoval	P. BARTUSEK	Zak. číslo	21-LI13-001
Zodp. projektant	ING. T. KLIMENT	Datum	02/2025
Tech. kontrola	ING. M. HANŽL	Stupeň	PDPS
Akce	I/16 MLADÁ BOLESLAV - MARTINOVICE	Počet formátů	16 x A4
		Měřítko	1 : 100
		Č. přílohy	Paré
Příloha	PŘÍČNÉ ŘEZY	5	

Zhotovitel:
Valbek, spol. s r.o.
Vaňurova 505/17
460 07 Liberec 3