
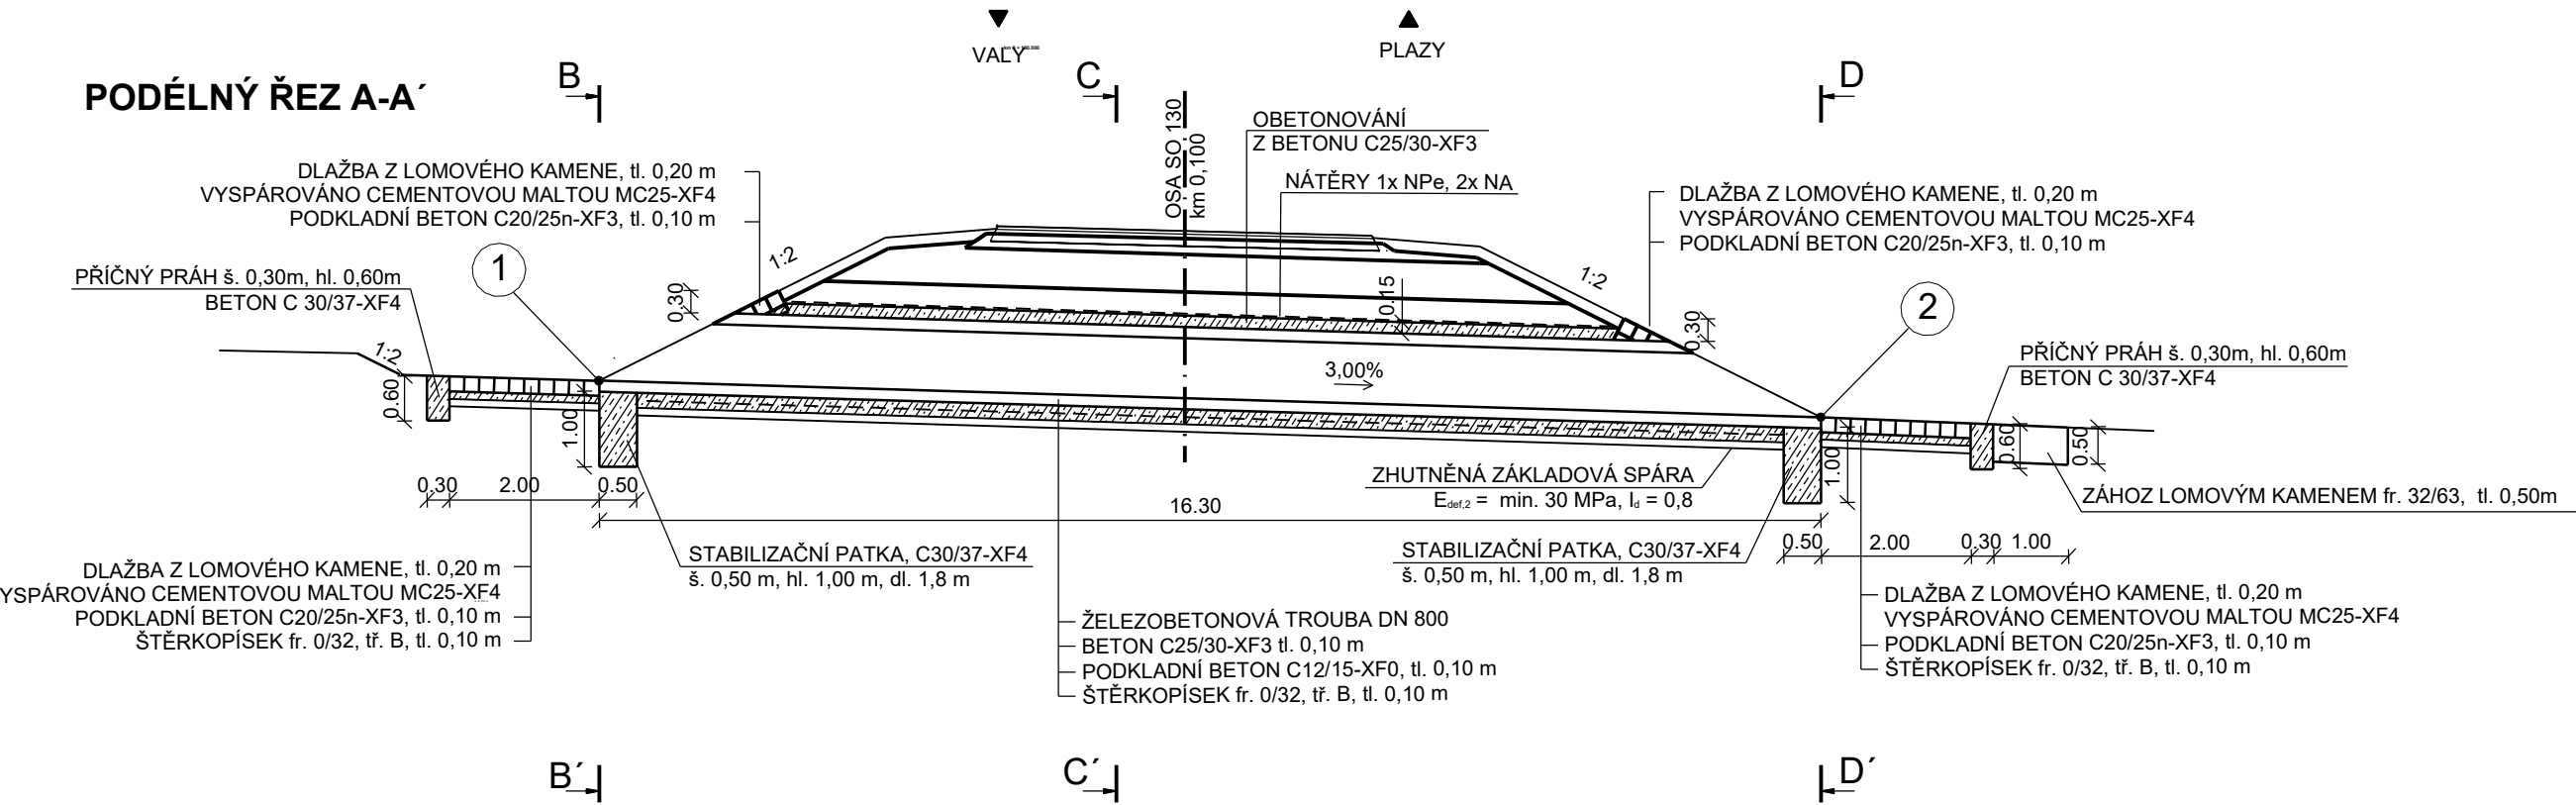



SO 130 - PŘELOŽKA MÍSTNÍ KOMUNIKACE V km 1,713

PROPUSTEK DN 800 V km 0,100


M 1 : 100

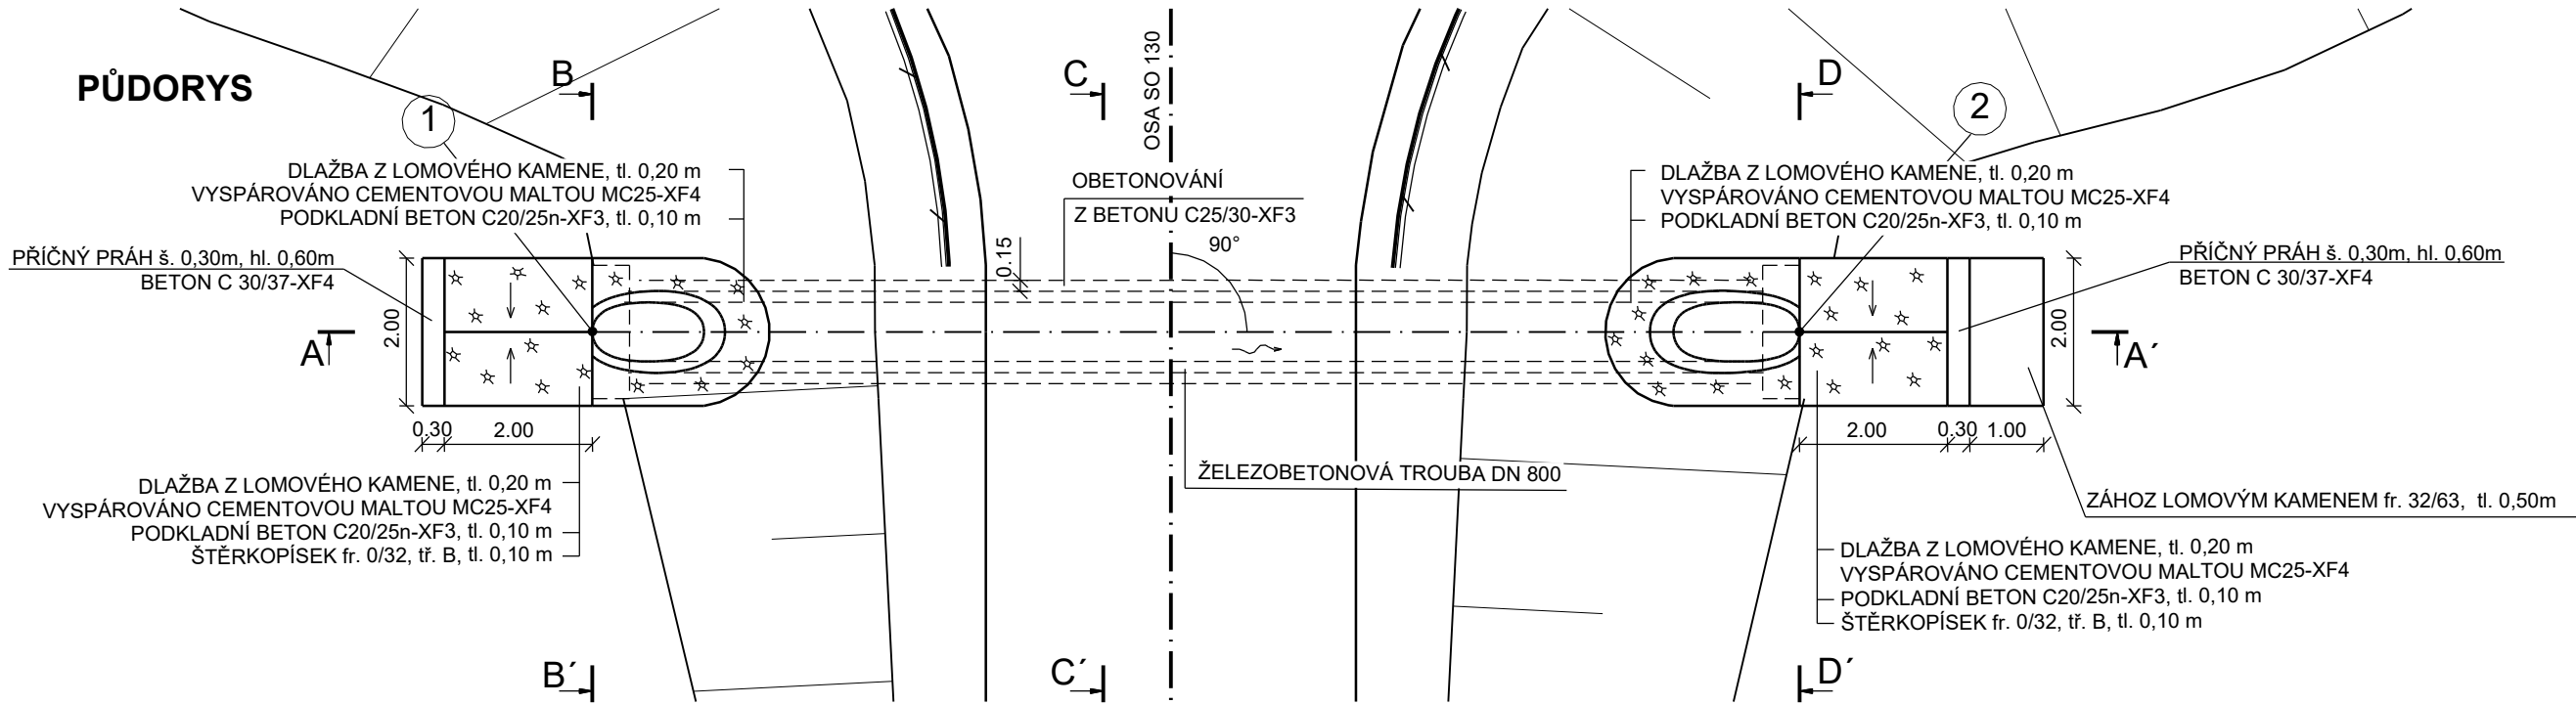


POHLED NA VTOK ŘEZ B-B'

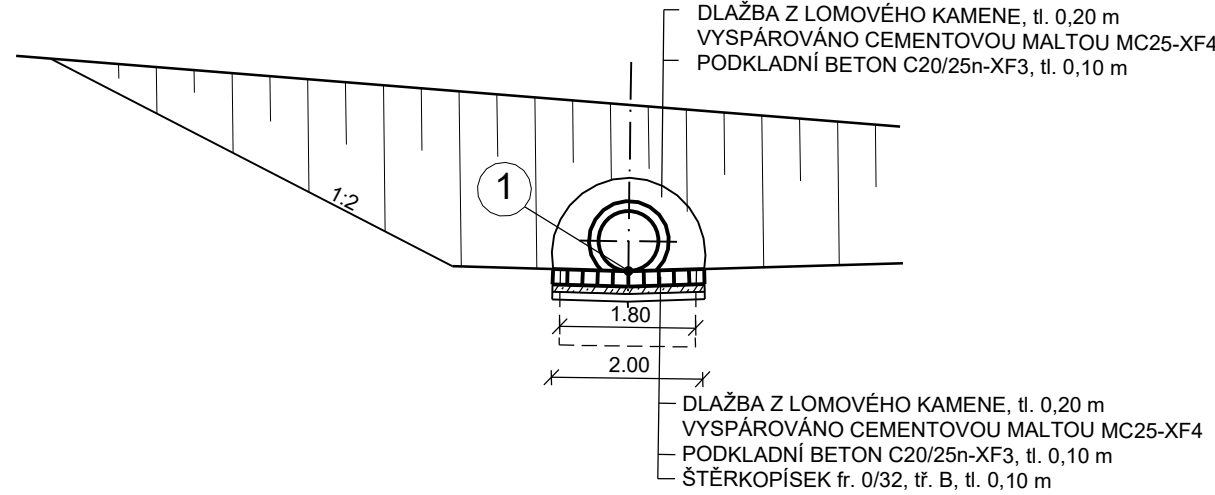

POHLED NA VÝTOK ŘEZ D-D'

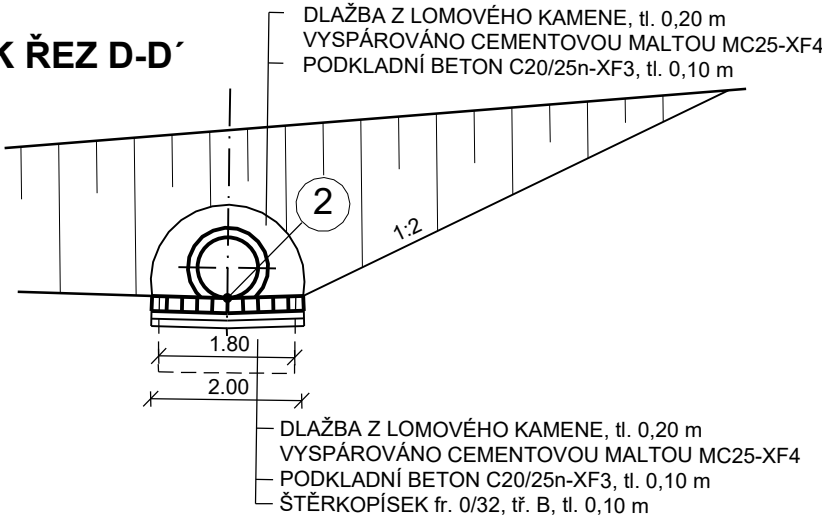

PŘÍČNÝ ŘEZ C-C'

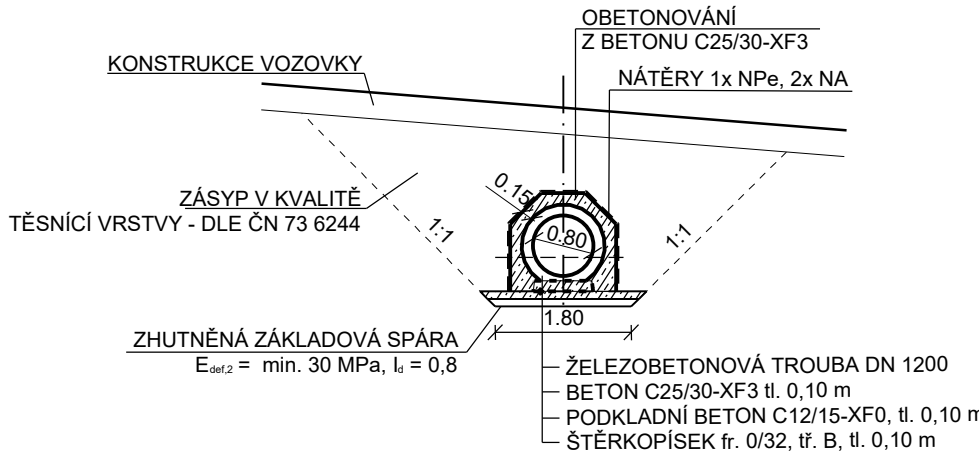

POZNÁMKY:

- SPÁROVÁNÍ DLAŽBY Z LOMOVÉHO KAMENE BUDE VYPLNĚNÉ CEMENTOVOU MALTOU MC25-XF4, tl. min. 0,20 m
- OBETONOVÁNÍ V MÍSTĚ HRDLA MINIMÁLNĚ 0,10 m
- VŠECHNY BETONOVÉ PRVKY, KTERÉ PŘÍJDOU DO STYKU SE ZEMINOU MUSÍ BÝT OPATŘENY NÁTĚRY: 1x NPe A 2x NA
- POČET PRAHŮ ZÁVISÍ NA TYPU ZVOLENÉ TROUBY A JEJÍHO ULOŽENÍ
- VYTÝČENÍ BUDE PROVEDENO DLE TKP 1 A SOUVEJÍJÍCÍCH PŘEDPISŮ
- SKLONY SVAHŮ JSOU URČENY SKLONEM SILNIČNÍHO TĚLESA A PŘÍLEHLÝCH PŘÍKOPŮ
- POKUD NEBUDOU NA KRAJÍCH OSAZENY ŠIKMÉ PREFABRIKÁTY, BUDOU PRO SEŘÍZNUTÍ POUŽITY BETONOVÉ TROUBY (Z DŮVODU KORODUJÍCÍ VÝZTUŽE)
- ŠÍŘE PODKLADNÍHO PRAHU JE 0,50 m NA KAŽDOU STRANU OD VNĚJŠÍHO OBRYSU TROUBY
- BETONOVÉ VÝROBKY VYSTAVENÉ PŘÍMÉMU OSTRÍKU ROZMRAZOVACÍCH PROSTŘEDKŮ A MRAZU A UMÍSTĚNÉ VE ZVZDALENOSTI MOŽNÉHO OSTRÍKU (OD HRANY VOZOVKY 10 m VČETNĚ SOLNĚ MLHY) MUSÍ SPLŇOVAT POŽADAVKY NA STUPEŇ VLIVU PROSTŘEDÍ XF4.

PARAMETRY PROPUSTKŮ					VYTÝČOVANÉ BODY	
STANIČENÍ [km]	TROUBA DN [mm]	DÉLKA DL [m]	SKLON S: [%]	ÚHEL α [°]	VTOK - 01 Y / X [S-JTSK] / Z [Bpv]	VÝTOK - 02 Y / X [S-JTSK] / Z [Bpv]
0,100	800	16,30	3,00	90	699393,756/1011350,421/218,53	699409,722/1011347,069/218,04

Souřadnicový systém: S-JTSK
Výškový systém: Bpv

SO 130 Přeložka místní komunikace v km 1,713



Ředitelství silnic a dálnic s. p.
Čerčanská 2023/12, Krč, 140 00 Praha 4



Valbek, spol. s r.o.
Vaňurova 505/17
460 07 Liberec 3



Zhotovitel:
Valbek, spol. s r.o.
Vaňurova 505/17
460 07 Liberec 3

Vypracoval	A. BARTONIČKOVÁ	Zak. číslo	21-L113-001
Zodp. projektant	ING. T. KLIMENT	Datum	02/2025
Tech. kontrola	ING. M. HANŽL	Stupeň	PDPS
Akce I/16 MLADÁ BOLESLAV - MARTINOVICE		Počet formátů	4 x A4
		Měřítko	1 : 100
Příloha PROPUSTEK DN 800 V km 0,100		Č. přílohy	Paré
		6	