


SO 140 - PŘÍJEZD K DUN v km 0,170
SITUACE
M 1 : 1000

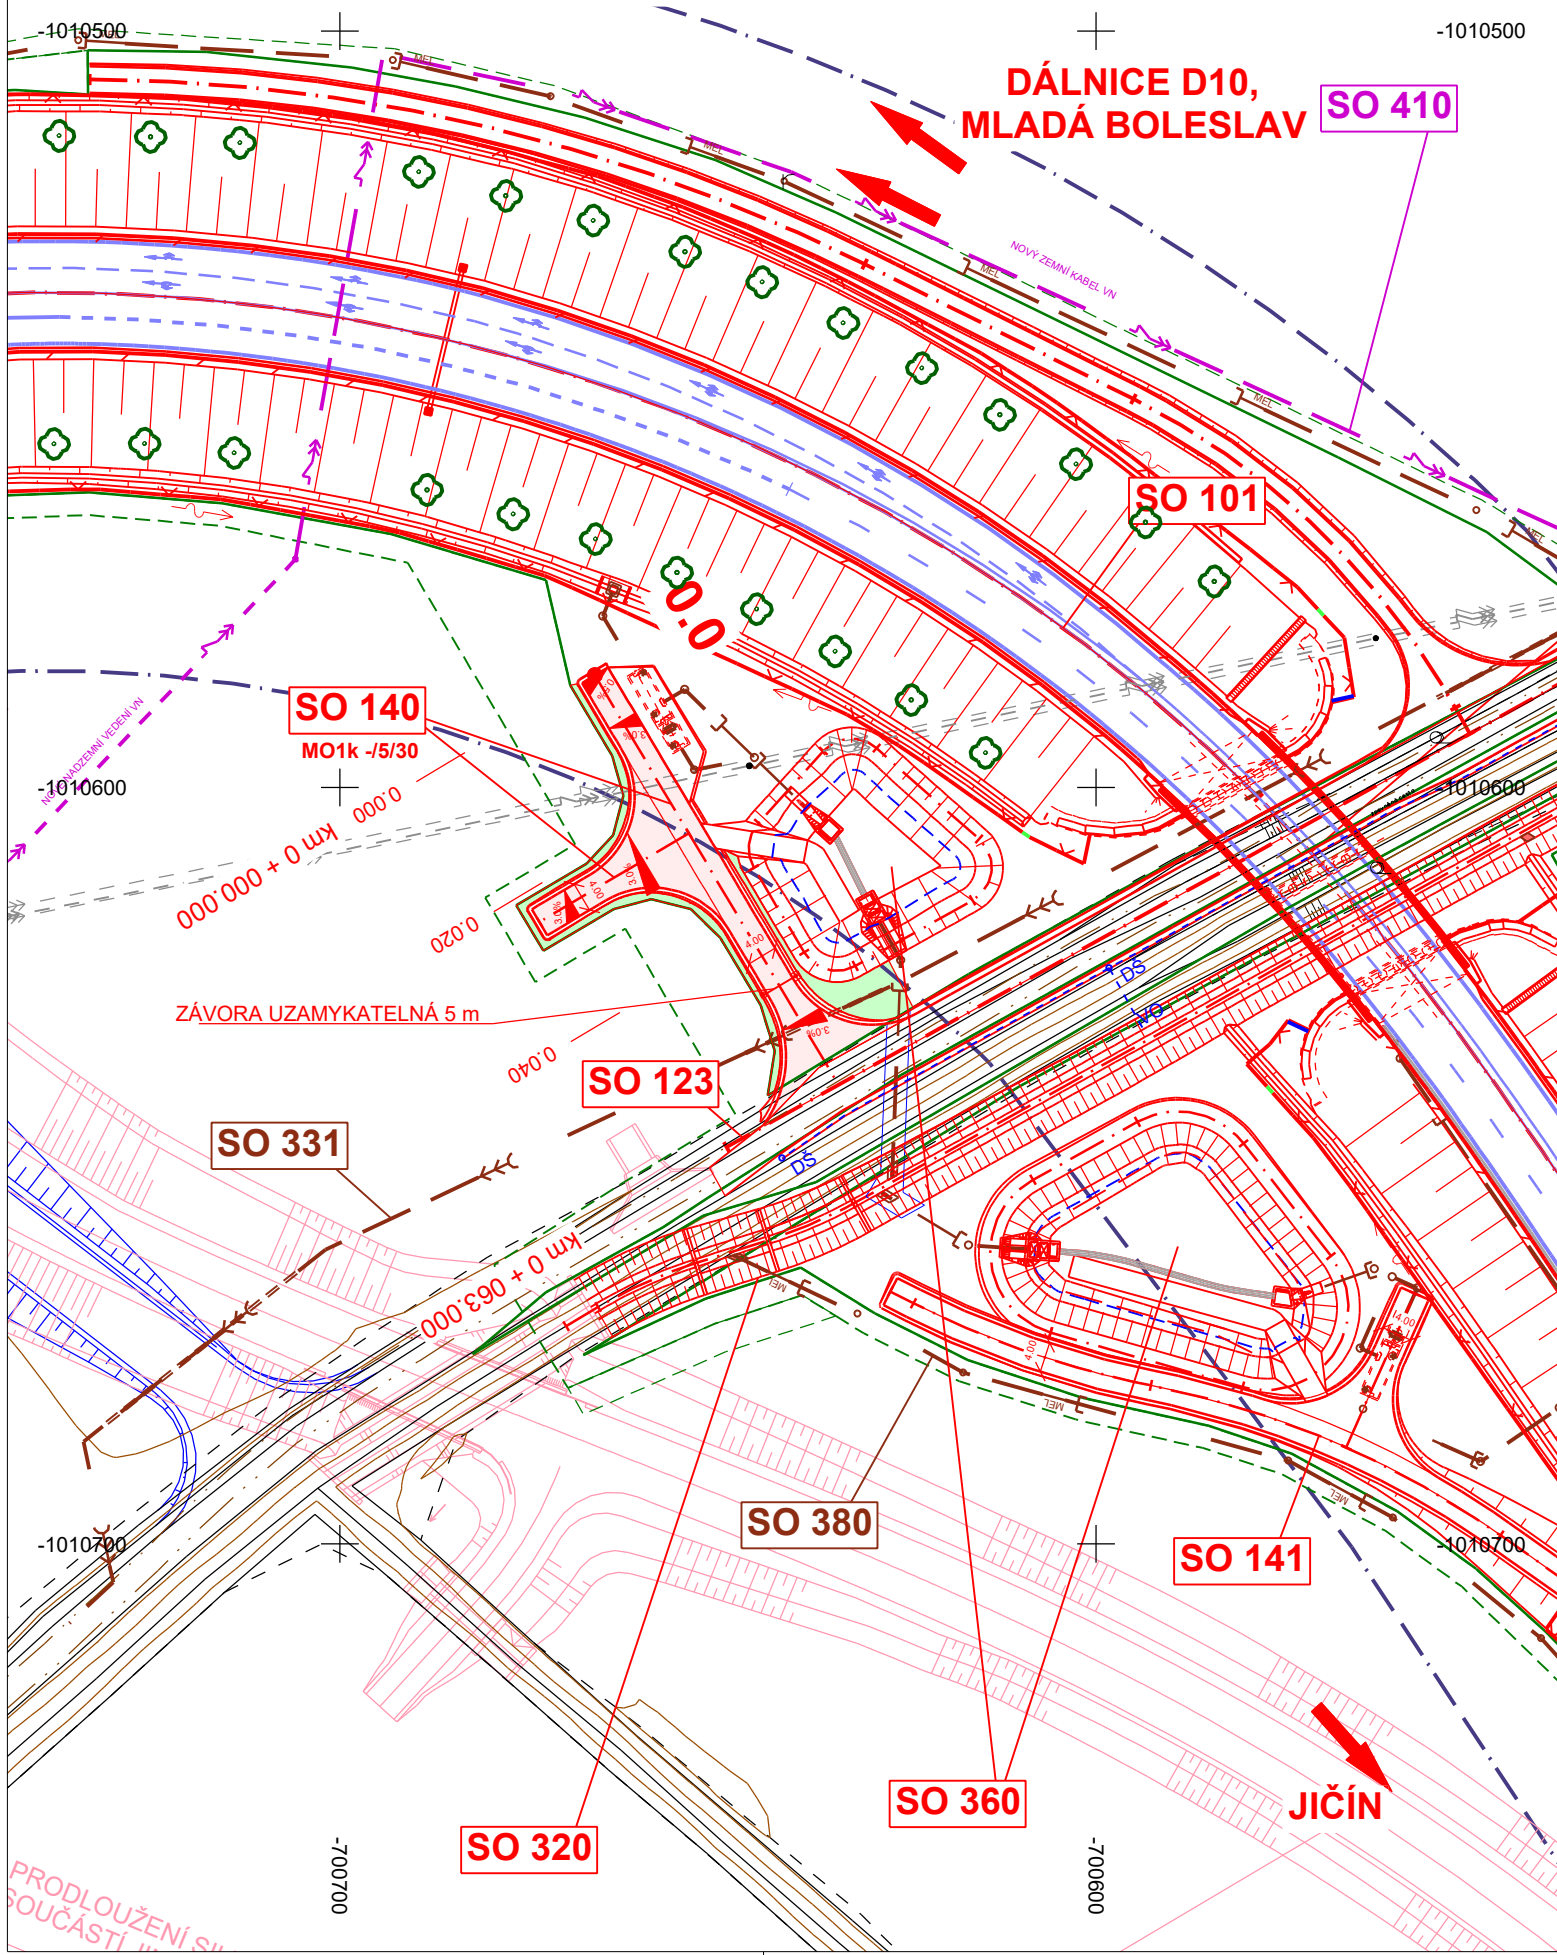

LEGENDA:

PLOCHY

[Pink Box]	VOZOVKA - ASFALTOVÝ KRYT
[Light Pink Box]	VOZOVKA - FRÉZOVANÁ
[Yellow Box]	VOZOVKA - POLNÍ CESTY
[Light Yellow Box]	CHODNÍK
[Light Blue Box]	DLAŽBA VOZOVKY
[Orange Box]	SWAHY VÝKOPU
[Light Green Box]	SWAHY NÁSYPU
[Green Box]	VEGETAČNÍ ÚPRAVY

OBVOD STAVBY

[Solid Green Line]	TRVALÝ ZÁBOR
[Dashed Green Line]	DOČASNÝ ZÁBOR

NOVÉ IS

[Brown Line]	DEŠŤOVÁ KANALIZACE
[Brown Line with MEL]	MELIORACE
[Brown Line with V]	VÝTLAK
[Green Line]	VODOVOD
[Dashed Green Line]	NADZEMNÍ VEDENÍ NN
[Dashed Green Line with V]	NADZEMNÍ VEDENÍ VN
[Dashed Green Line with VV]	PODZEMNÍ VEDENÍ NN
[Dashed Green Line with VV]	PODZEMNÍ SDĚLOVACÍ VEDENÍ
[Orange Line]	PLYNOVOD - STL

STÁVAJÍCÍ IS - INFORMATIVNÍ ZÁKRES

[Dashed Green Line]	PODZEMNÍ VEDENÍ NN
[Dashed Green Line with V]	PODZEMNÍ VEDENÍ VN
[Dashed Green Line]	NADZEMNÍ VEDENÍ NN
[Dashed Green Line with V]	NADZEMNÍ VEDENÍ VN
[Dashed Green Line with VV]	NADZEMNÍ VEDENÍ VVN
[Brown Line]	DEŠŤOVÁ KANALIZACE
[Orange Line]	PLYNOVOD - STL
[Dashed Green Line with VV]	PODZEMNÍ SDĚLOVACÍ VEDENÍ
[Green Line]	VODOVOD

Souřadnicový systém: S-JTSK
Výškový systém: Bpv

SO 140 Příjezd k DUN v km 0,170

Objednatel:



**ŘEDITELSTVÍ
SILNIC
A DÁLNIC**

Ředitelství silnic a dálnic s. p.
Čerčanská 2023/12, Krč, 140 00 Praha 4

Zhotovitel:



Valbek

Valbek, spol. s r.o.
Vaňurova 505/17
460 07 Liberec 3

	Vypracoval	Bc. J. HALABURKA	Zak. číslo	21-LI13-001
	Zodp. projektant	ING. T. KLIMENT	Datum	02/2025
	Tech. kontrola	ING. M. HANŽL	Stupeň	PDPS
	Akce I/16 MLADÁ BOLESLAV - MARTINOVICE		Počet formátů	2 x A4
			Měřítko	1 : 1000
Zhotovitel: Valbek, spol. s r.o. Vaňurova 505/17 460 07 Liberec 3	Příloha	SITUACE		Č. přílohy 2 Paré