

SO 141 - PŘÍJEZD K DUN v km 0,390

VZOROVÉ PŘÍČNÉ ŘEZY

M 1 : 50

KATEGORIE MO1k -/5/30


JEDNOPRUHOVÁ, OBOUSMĚRNÁ

TŘÍDA DOPRAVNÍHO ZATÍŽENÍ IV


NÁVRHOVÁ ÚROVEŇ PORUŠENÍ D1

TYP PODLOŽÍ PIII (D1-A-2)


D1-N-11, TDZ IV, P III (DLE STARÉHO KATALOGU)

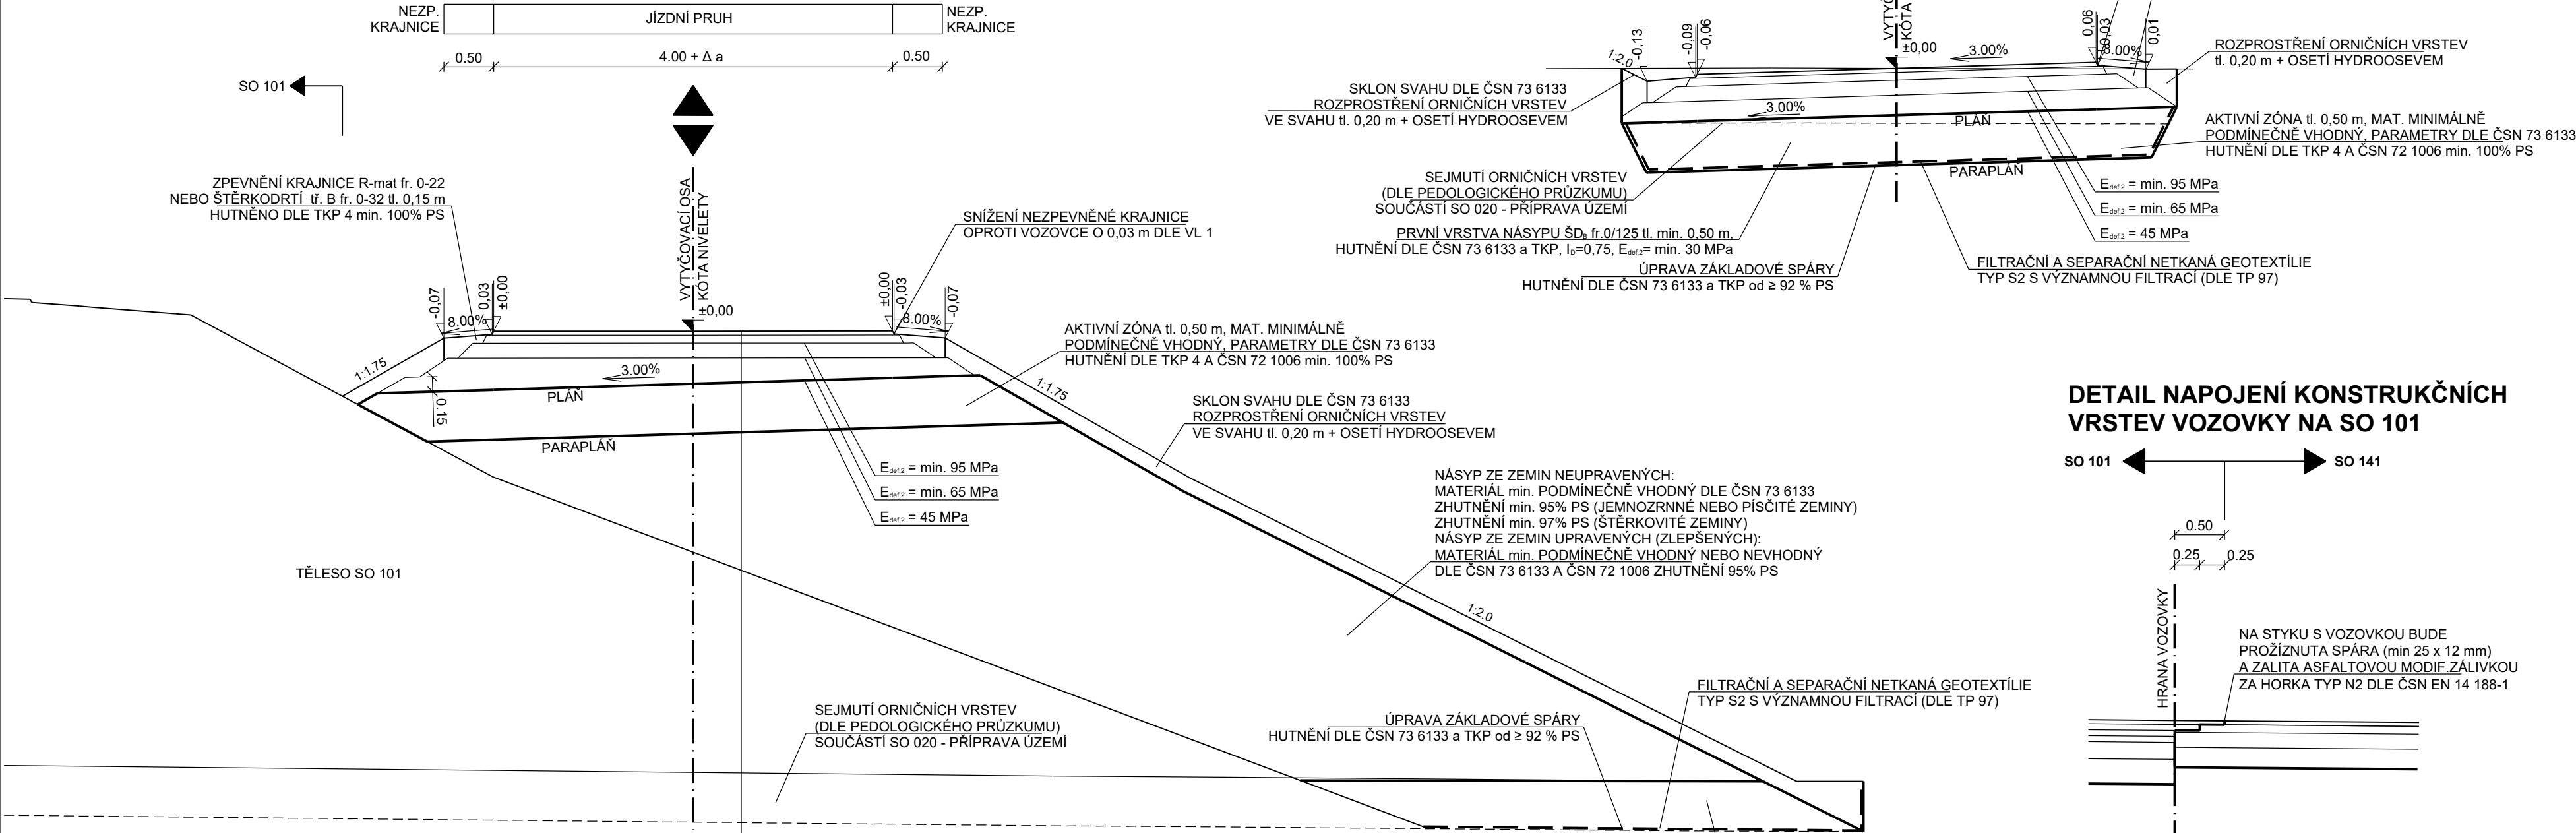

DETAIL UKONČENÍ VRSTEV VOZOVKY

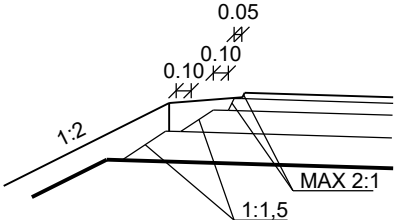

DETAIL NAPOJENÍ KONSTRUKČNÍCH VRSTEV VOZOVKY NA SO 101

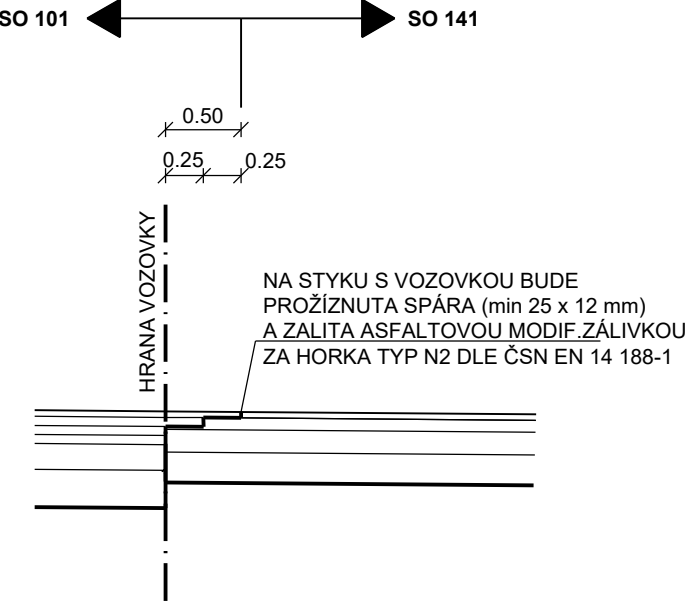

ASFALTOVÝ BETON PRO OBRUSNOU VRSTVU ASFALT 50/70	ACO 11	40 mm	ČSN EN 13 108-1, ČSN 73 6121
POSTŘÍK SPOJOVACÍ EMULZÍ	PS-C	0,35kg/m ²	ČSN EN 13808, ČSN 73 6129
ASFALTOVÝ BETON PRO PODKLADNÍ VRSTVU ASFALT 50/70	ACP 16+	80 mm	ČSN EN 13 108-1, ČSN 73 6121
POSTŘÍK INFILTRAČNÍ ŘEDĚNÍ ASF. EMULZÍ S POSYPEM KAMENIVEM fr. 2/4 V MNOŽSTVÍ 3,0 kg/m ²	PI-C	1,00kg/m ²	ČSN 73 6129
MECHANICKY ZPEVNĚNÉ KAMENIVO (0/32 G _s)	MZK	150 mm	ČSN EN 13 285, ČSN 73 6126-1
ŠTĚRKODRT' tř.A, (0/32 G _s)	ŠD _A	min. 200 mm	ČSN EN 13 285, ČSN 73 6126-1
CELKEM		min. 470 mm	

SO 141 Příjezd k DUN v km 0,390

Objednatel:



**ŘEDITELSTVÍ
SILNIC
A DÁLNIC**

Ředitelství silnic a dálnic s. p.
Čerčanská 2023/12, Krč, 140 00 Praha 4

Zhotovitel:



Valbek

Valbek, spol. s r.o.
Vaňurova 505/17
460 07 Liberec 3

	Vypracoval	Bc. J. HALABURKA	Zak. číslo	21-L13-001
	Zodp. projektant	ING. T. KLIMENT	Datum	02/2025
	Tech. kontrola	ING. M. HANŽL	Stupeň	PDPS
	Akce I/16 MLADÁ BOLESLAV - MARTINOVICE		Počet formátů	4 x A4
			Měřítko	1 : 50
Zhotovitel: Valbek, spol. s r.o. Vaňurova 505/17 460 07 Liberec 3	Příloha	VZOROVÉ PŘÍČNÉ ŘEZY		4