SO 141 - PŘÍJEZD K DUN v km 0,390
PŘÍČNÉ ŘEZY km 0,000 - 0,140
M 1 : 100

km 0 + 000.000

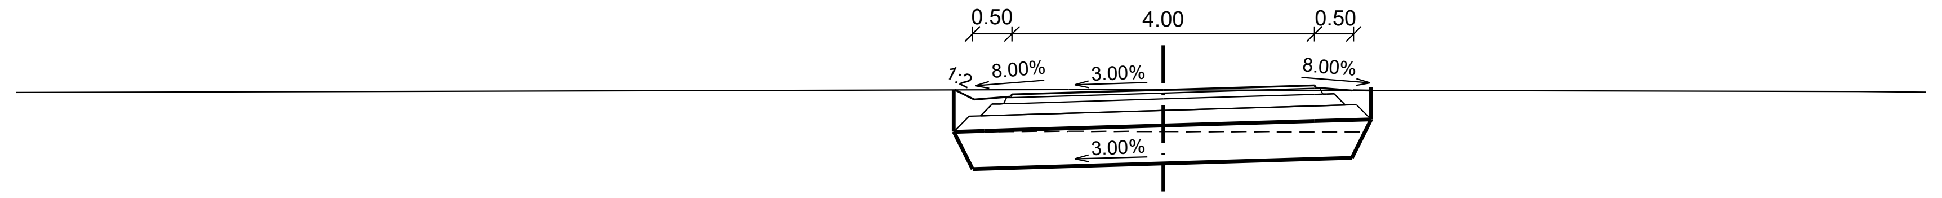
0.50
4.00
0.50
1:2
8.00%
3.00%
8.00%
3.00%

S. R. 210 m

PROJEKTOVANÝ STAV	212.37	212.24	212.31	212.37	212.43	212.36
ODSAZENÍ OD OSY	-2.76	-2.50	-2.00	0.00	2.00	2.50

STÁVAJÍCÍ TERÉN	212.37	212.37	212.35
ODSAZENÍ OD OSY	-1.25	0.00	9.20

km 0 + 020.000

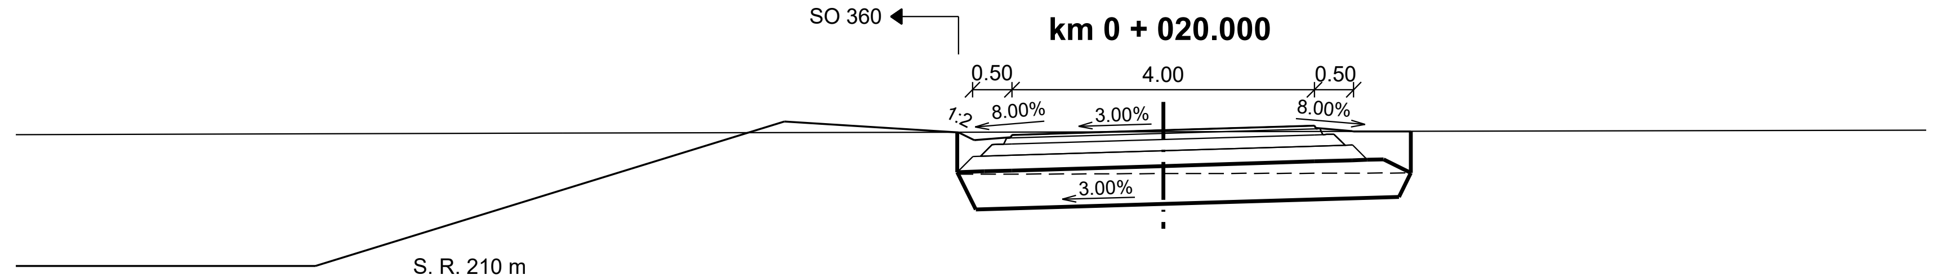
SO 360
0.50
4.00
0.50
1:2
8.00%
3.00%
8.00%
3.00%

S. R. 210 m

PROJEKTOVANÝ STAV	212.44	212.34	212.41	212.47	212.53	212.46	212.46
ODSAZENÍ OD OSY	-2.71	-2.50	-2.00	0.00	2.00	2.50	3.27

STÁVAJÍCÍ TERÉN	212.43	212.45
ODSAZENÍ OD OSY	-7.94	0.00

km 0 + 040.000

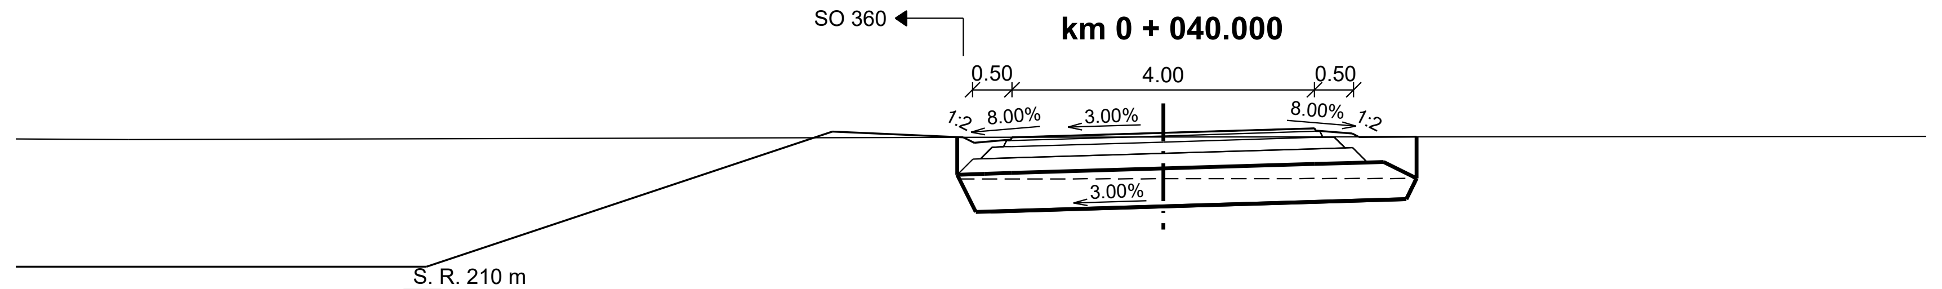
SO 360
0.50
4.00
0.50
1:2
8.00%
3.00%
8.00%
1:2
3.00%

S. R. 210 m

PROJEKTOVANÝ STAV	212.51	212.44	212.51	212.57	212.63	212.56	212.52	212.52
ODSAZENÍ OD OSY	-2.64	-2.50	-2.00	0.00	2.00	2.50	2.59	3.35

STÁVAJÍCÍ TERÉN	212.51	212.51
ODSAZENÍ OD OSY	-2.68	0.00

km 0 + 060.000

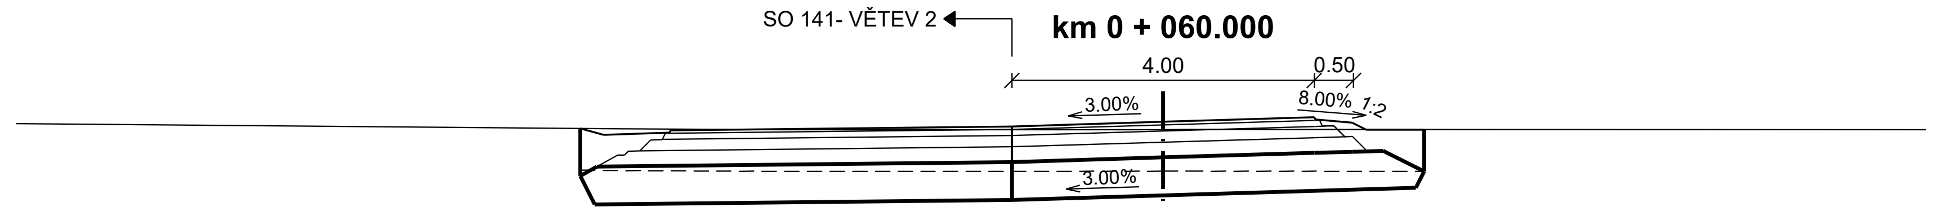
SO 141- VĚTEV 2
4.00
0.50
3.00%
8.00%
1:2
3.00%

S. R. 210 m

PROJEKTOVANÝ STAV	212.62	212.68	212.74	212.68	212.58	212.58
ODSAZENÍ OD OSY	-2.00	0.00	2.00	2.50	2.69	3.45

STÁVAJÍCÍ TERÉN	212.59	212.58	212.58	212.58
ODSAZENÍ OD OSY	-7.26	-5.03	0.00	0.33

km 0 + 080.000

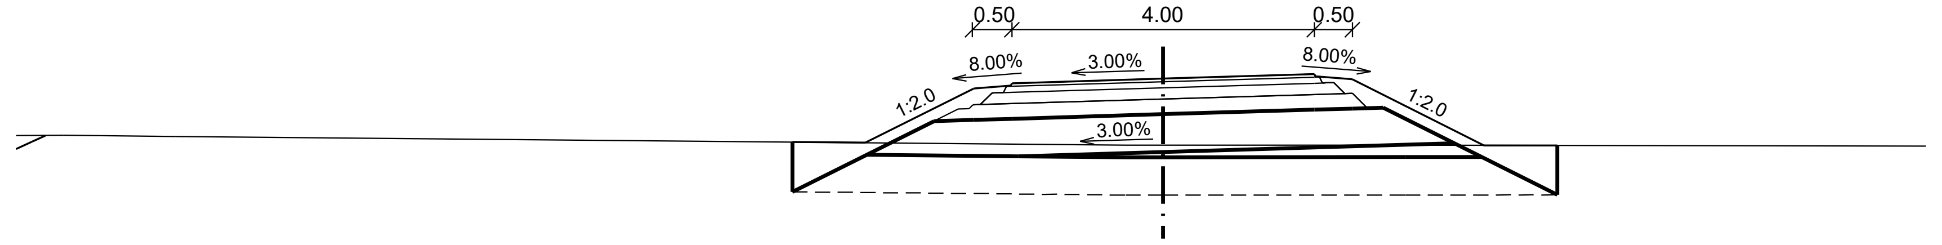
0.50
4.00
0.50
8.00%
3.00%
8.00%
1:2.0
1:2.0
3.00%

S. R. 210 m

PROJEKTOVANÝ STAV	212.62	212.61	213.33	213.40	213.46	213.52	213.45	212.58	212.58
ODSAZENÍ OD OSY	-4.90	-3.94	-2.50	-2.00	0.00	2.00	2.50	4.25	5.21

STÁVAJÍCÍ TERÉN	212.58	212.58	212.58
ODSAZENÍ OD OSY	-0.50	0.00	3.20

km 0 + 100.000

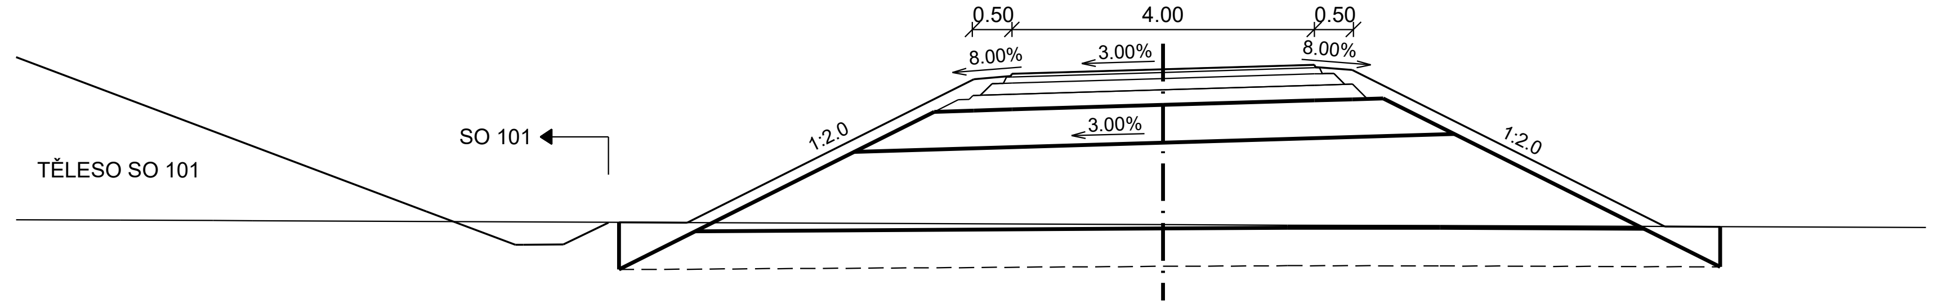
0.50
4.00
0.50
8.00%
3.00%
8.00%
1:2.0
1:2.0
3.00%
SO 101
TĚLESO SO 101

S. R. 210 m

PROJEKTOVANÝ STAV	212.64	212.63	214.53	214.60	214.66	214.72	214.65	212.58	212.58
ODSAZENÍ OD OSY	-7.20	-6.30	-2.50	-2.00	0.00	2.00	2.50	6.64	7.37

STÁVAJÍCÍ TERÉN	212.61	212.60	212.59
ODSAZENÍ OD OSY	0.00	1.65	3.66

km 0 + 120.000

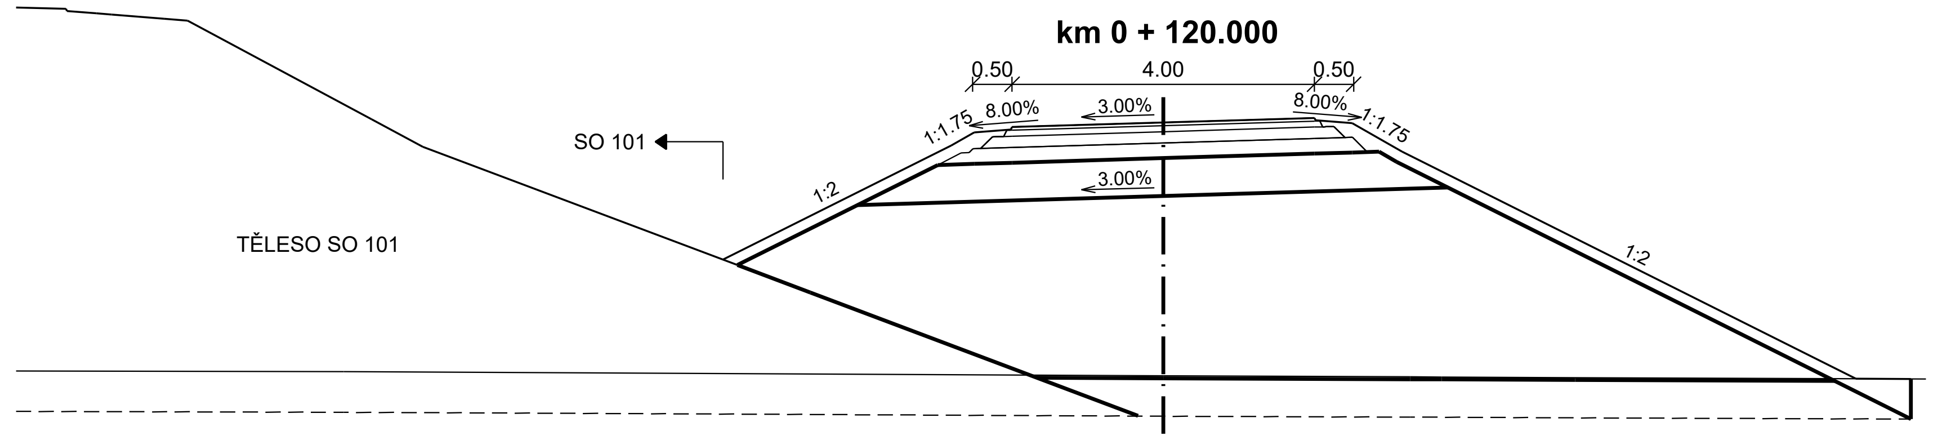
0.50
4.00
0.50
1:1.75
8.00%
3.00%
8.00%
1:1.75
SO 101
1:2
3.00%
1:2
TĚLESO SO 101

S. R. 210 m

PROJEKTOVANÝ STAV	214.05	215.56	215.73	215.80	215.86	215.92	215.85	215.47	212.47	212.47
ODSAZENÍ OD OSY	-5.82	-2.81	-2.50	-2.00	0.00	2.00	2.50	3.16	9.16	9.89

STÁVAJÍCÍ TERÉN	212.51	212.50	212.49	212.49
ODSAZENÍ OD OSY	0.00	3.26	3.68	5.45

km 0 + 140.000

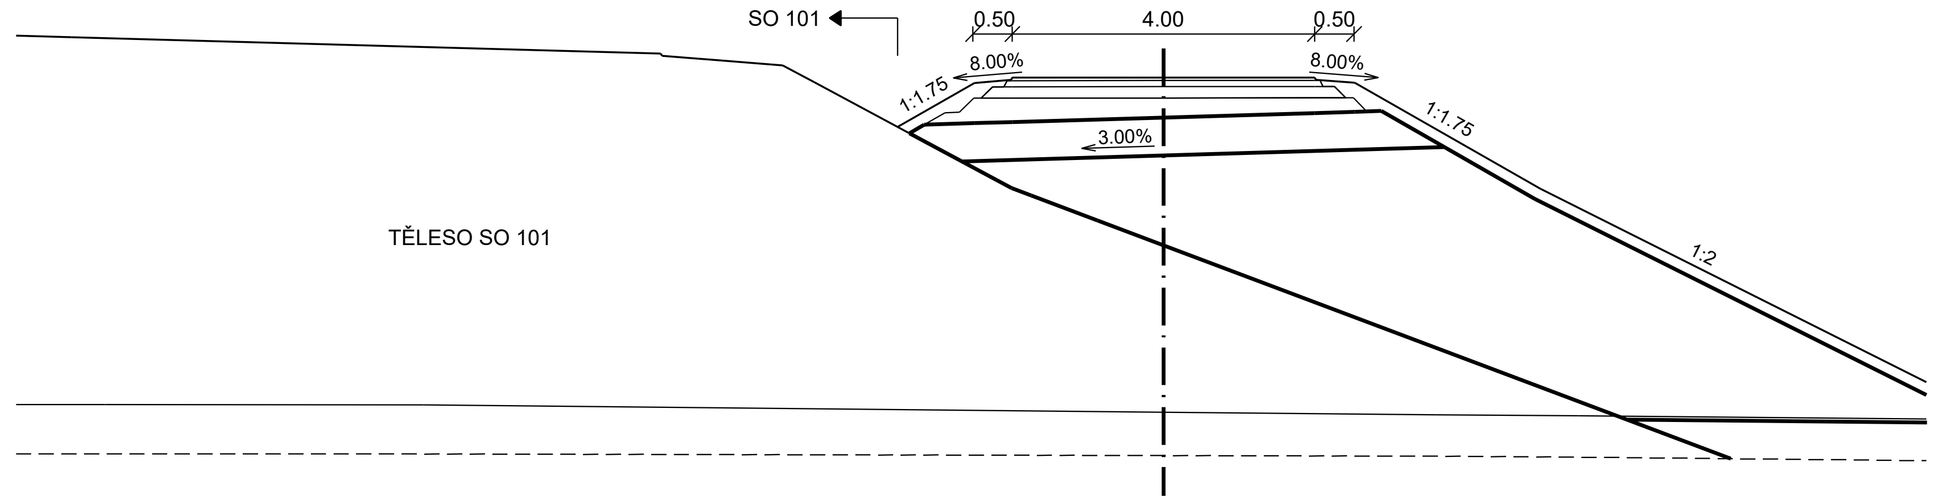
SO 101
0.50
4.00
0.50
1:1.75
8.00%
8.00%
1:1.75
3.00%
1:2
TĚLESO SO 101

S. R. 210 m

PROJEKTOVANÝ STAV	216.14	216.72	216.79	216.79	216.79	216.72	215.32
ODSAZENÍ OD OSY	-3.52	-2.50	-2.00	0.00	2.00	2.53	4.98

STÁVAJÍCÍ TERÉN	212.46	212.37	212.33	212.32
ODSAZENÍ OD OSY	-9.78	0.00	3.60	5.49

Výškový systém: Bpv

SO 141 Příjezd k DUN v km 0,390

Objednatel:

Ředitelství silnic a dálnic s. p.
Čerčanská 2023/12, Krč, 140 00 Praha 4

Zhotovitel:

Valbek, spol. s r.o.
Vaňurova 505/17
460 07 Liberec 3

Vypracoval	Bc. J. HALABURKA		**Zak. číslo**	**21-LI13-001**
Zodp. projektant	ING. T. KLIMENT		**Datum**	**02/2025**
Tech. kontrola	ING. M. HANŽL		**Stupeň**	**PDPS**
Akce	**I/16 MLADÁ BOLESLAV - MARTINOVICE**		**Počet formátů**	**10 x A4**
			Měřítko	**1 : 100**
			Č. přílohy	**Paré**
Příloha	PŘÍČNÉ ŘEZY km 0,000 - 0,140		**5**	

Zhotovitel:
Valbek, spol. s r.o.
Vaňurova 505/17
460 07 Liberec 3