
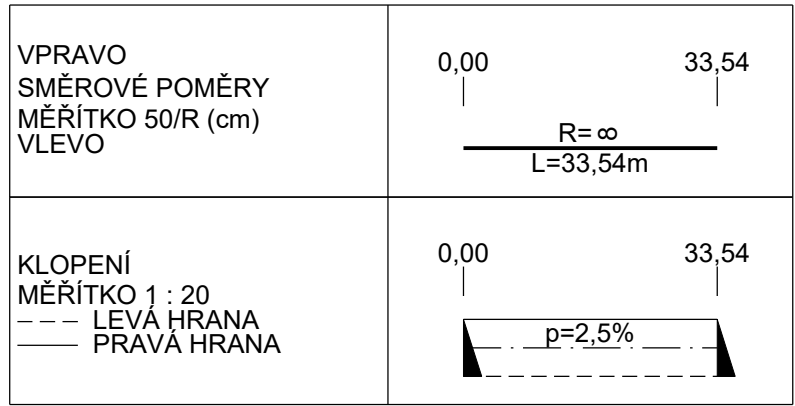


SO 142 - PŘÍJEZD K DUN v km 0,720

PODÉLNÝ PROFIL

M 1 : 1000 / 100

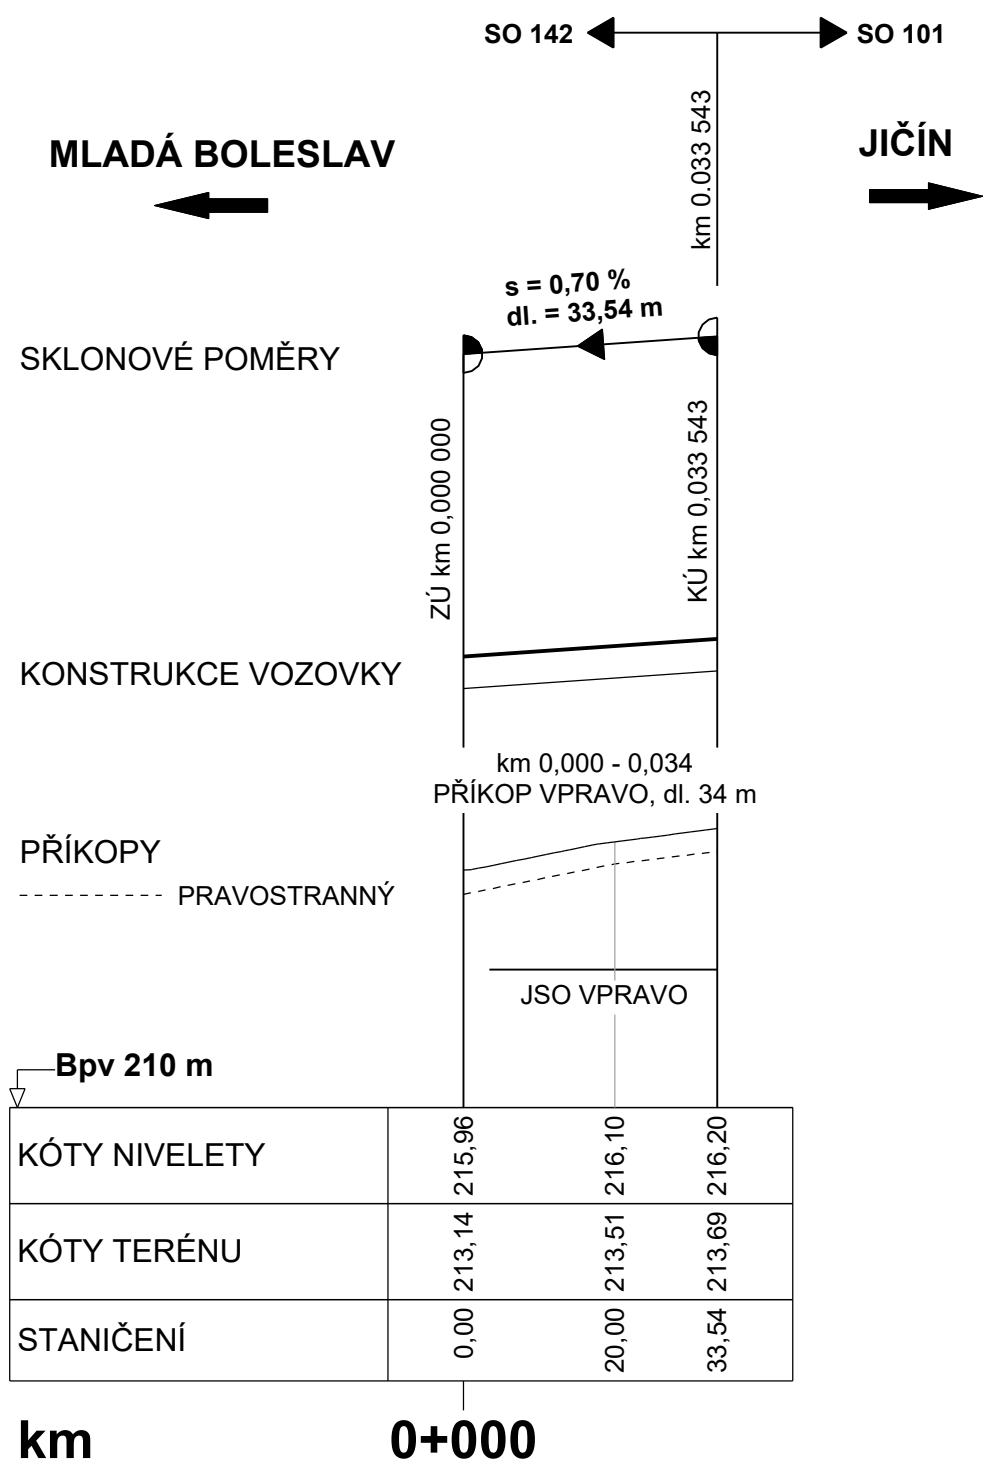

Výškový systém: Bpv

SO 142 Příjezd k DUN v km 0,720

Objednatel:



**ŘEDITELSTVÍ
SILNIC
A DÁLNIC**

Ředitelství silnic a dálnic s. p.
Čerčanská 2023/12, Krč, 140 00 Praha 4

Zhotovitel:



Valbek, spol. s r.o.
Vaňurova 505/17
460 07 Liberec 3

	Vypracoval	Bc. J. HALABURKA	Zak. číslo	21-LI13-001
	Zodp. projektant	ING. T. KLIMENT	Datum	02/2025
	Tech. kontrola	ING. M. HANŽL	Stupeň	PDPS
	Akce I/16 MLADÁ BOLESLAV - MARTINOVICE		Počet formátů	2 x A4
			Měřítko	1 : 1000 / 100
Zhotovitel: Valbek, spol. s r.o. Vaňurova 505/17 460 07 Liberec 3	Příloha PODÉLNÝ PROFIL		Č. přílohy 3	Paré