

SO 142 - PŘÍJEZD K DUN v km 0,720

VZOROVÉ PŘÍČNÉ ŘEZY

M 1 : 50

KATEGORIE MO1k -/5/30

JEDNOPRUHOVÁ, OBOUSMĚRNÁ

TŘÍDA DOPRAVNÍHO ZATÍŽENÍ IV



NÁVRHOVÁ ÚROVEŇ PORUŠENÍ D1

TYP PODLOŽÍ PIII (D1-A-2)


D1-N-11, TDZ IV, P III (DLE STARÉHO KATALOGU)

DETAIL NAPOJENÍ KONSTRUKČNÍCH

VRSTEV VOZOVKY NA SO 101

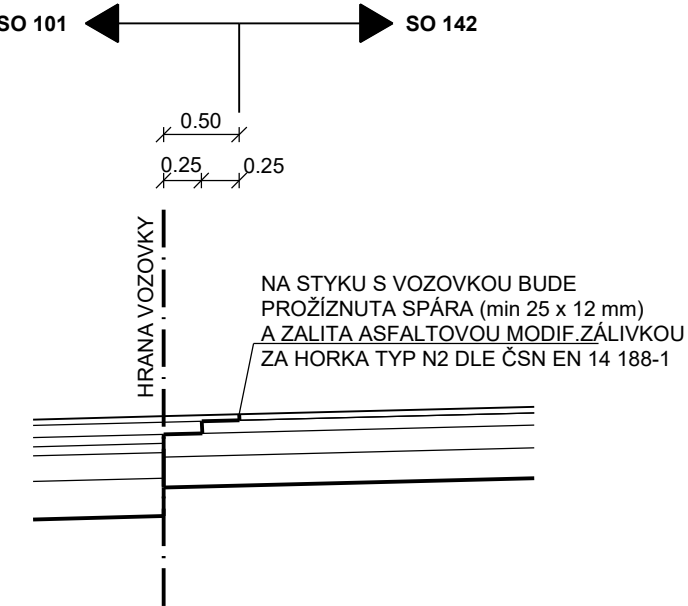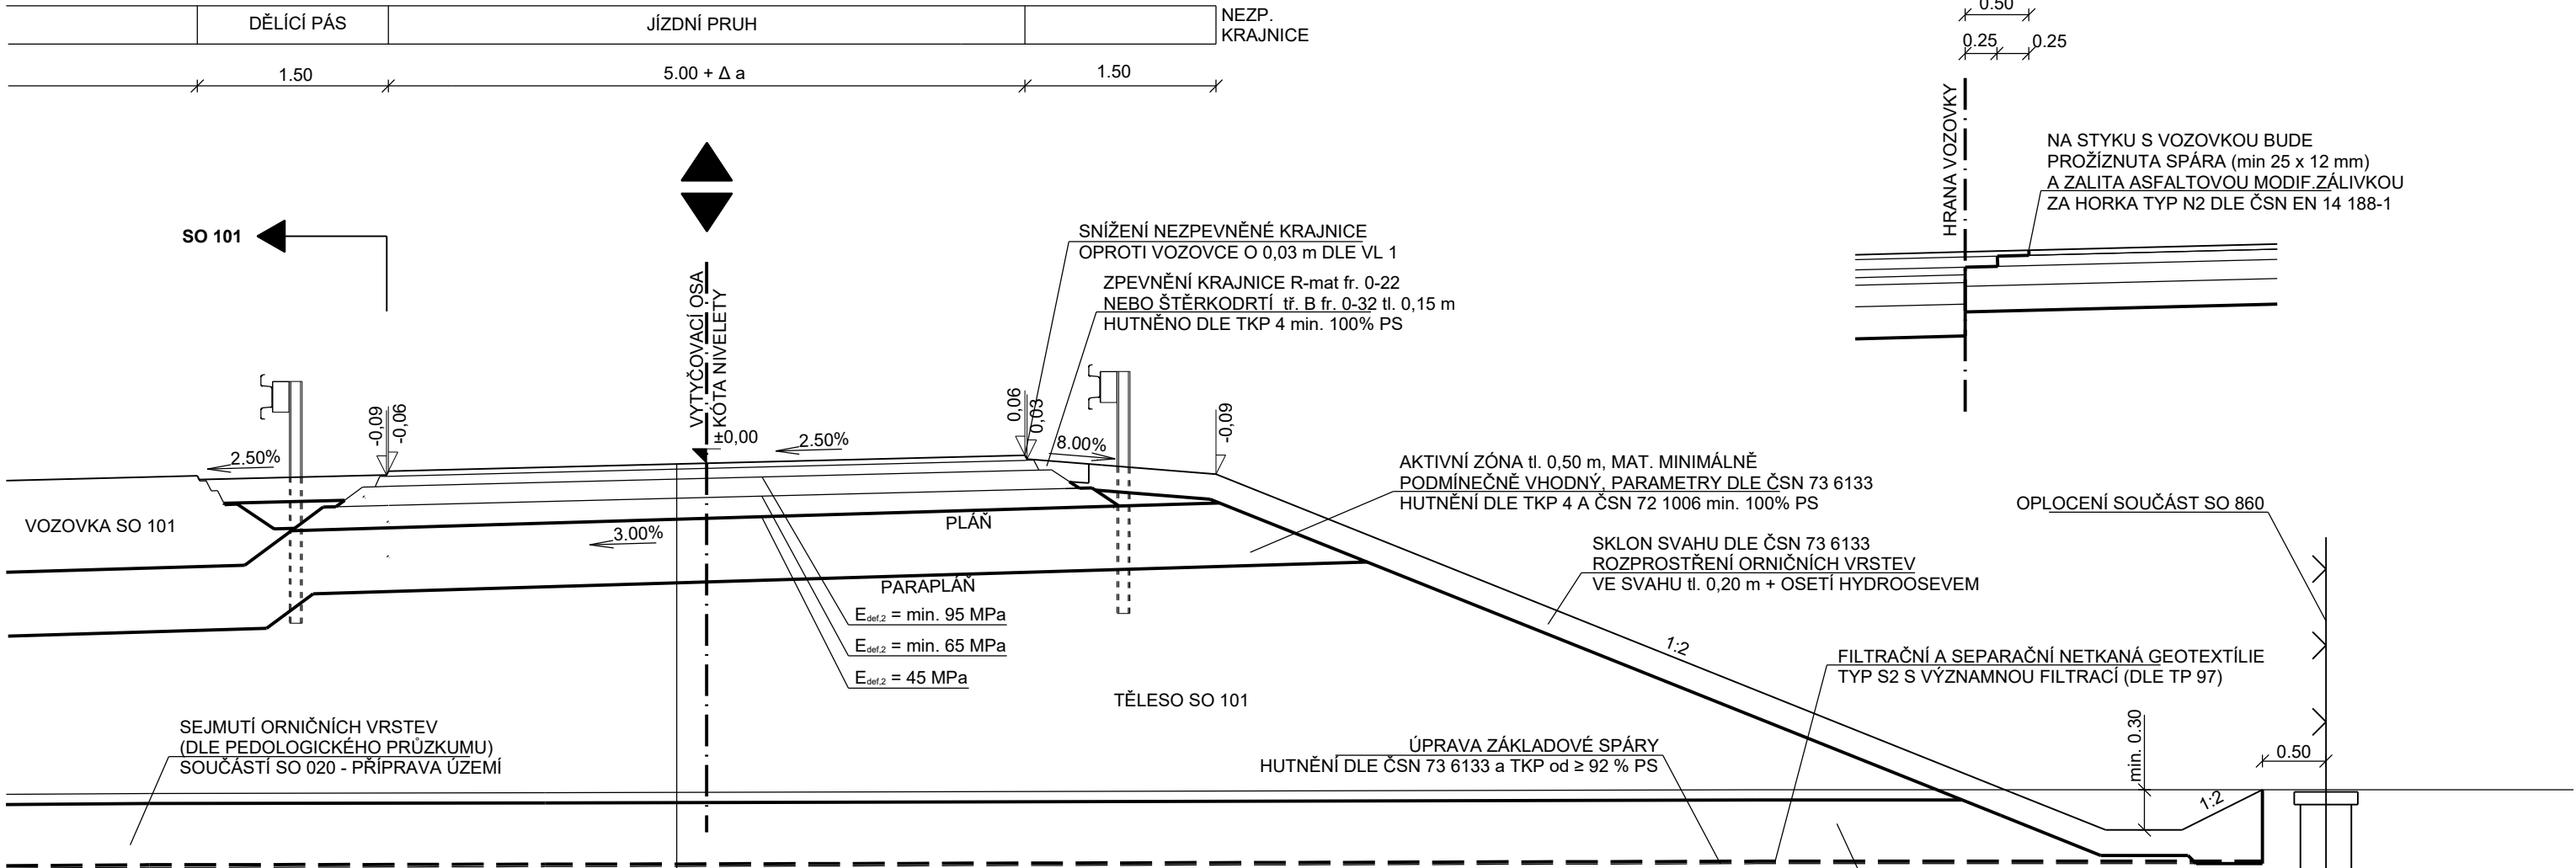

DETAIL UKONČENÍ VRSTEV VOZOVKY

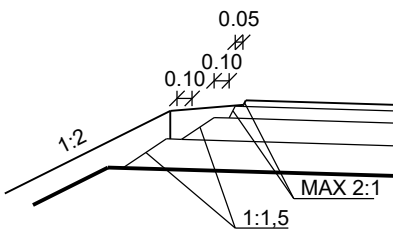

ASFALTOVÝ BETON PRO OBRUSNOU VRSTVU ASFALT 50/70	ACO 11	40 mm	ČSN EN 13 108-1, ČSN 73 6121
POSTŘÍK SPOJOVACÍ EMULZÍ	PS-C	0,35kg/m²	ČSN EN 13808, ČSN 73 6129
ASFALTOVÝ BETON PRO PODKLADNÍ VRSTVU ASFALT 50/70	ACP 16+	80 mm	ČSN EN 13 108-1, ČSN 73 6121
POSTŘÍK INFILTRAČNÍ ŘEDĚNÍ ASF. EMULZÍ S POSYPEM KAMENIVEM fr. 2/4 V MNOŽSTVÍ 3,0 kg/m²	PI-C	1,00kg/m²	ČSN 73 6129
MECHANICKY ZPEVNĚNÉ KAMENIVO (0/32 G _s)	MZK	150 mm	ČSN EN 13 285, ČSN 73 6126-1
ŠTĚRKODRTĚ tř.A, (0/32 G _e)	ŠD _A	min. 200 mm	ČSN EN 13 285, ČSN 73 6126-1
CELKEM		min. 470 mm	

SO 142 Přijezd k DUN v km 0,720

Objednatel:



ŘEDITELSTVÍ
SILNIC
A DÁLNIC

Ředitelství silnic a dálnic s. p.

Čerčanská 2023/12, Krč, 140 00 Praha 4

Zhotovitel:



Valbek, spol. s r.o.

Vaňurova 505/17
460 07 Liberec 3



Vypracoval Bc. J. HALABURKA
Zodp. projektant ING. T. KLIMENT
Tech. kontrola ING. M. HANŽL

Akce
I/16 MLADÁ BOLESLAV - MARTINOVICE

Zak. číslo	21-LI13-001
Datum	02/2025
Stupeň	PDPS
Počet formátů	3 x A4
Měřítko	1 : 50
Č. přílohy	Paré

Zhotovitel:
Valbek, spol. s r.o.
Vaňurova 505/17
460 07 Liberec 3

Příloha

VZOROVÉ PŘÍČNÉ ŘEZY

4