


SO 143 - PŘÍJEZD K DUN v km 1,500
SITUACE
M 1 : 1000

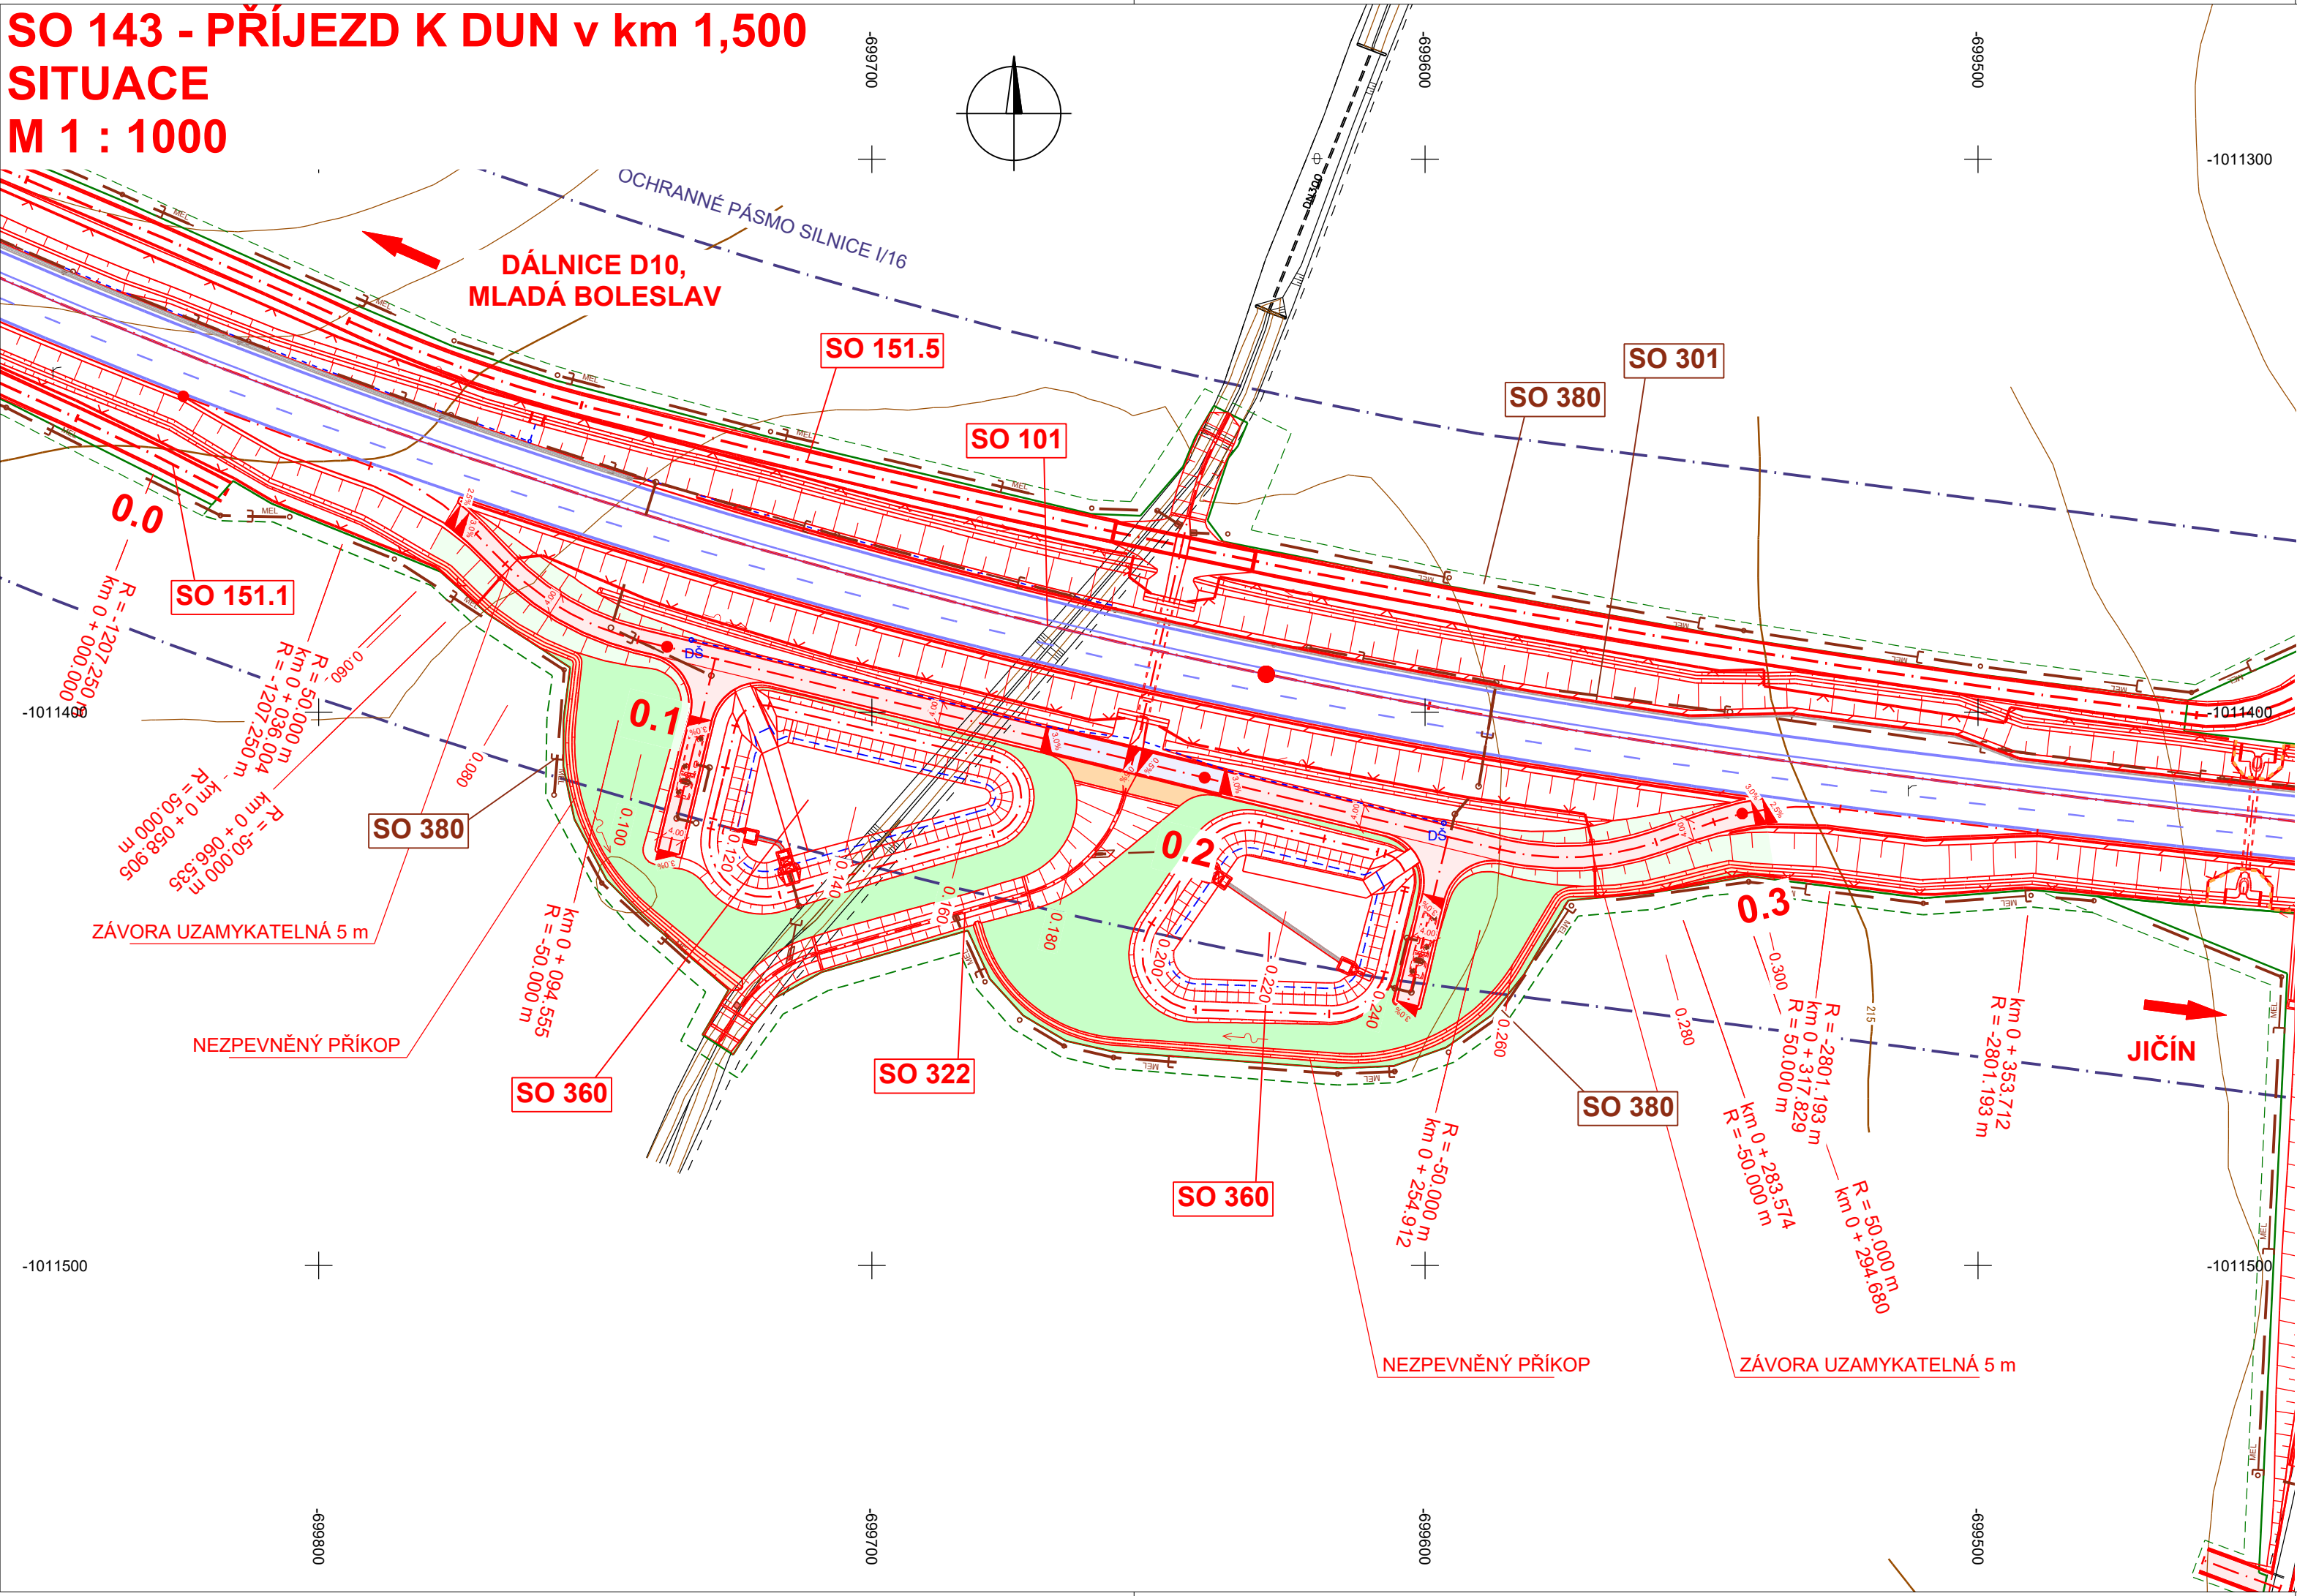

LEGENDA:

PLOCHY

- VOZOVKA - ASFALTOVÝ KRYT
- VOZOVKA - FRÉZOVANÁ
- VOZOVKA - POLNÍ CESTY
- CHODNÍK
- DLAŽBA VOZOVKY
- SVAHY VÝKOPU
- SVAHY NÁSYPU
- VEGETAČNÍ ÚPRAVY

OBVOD STAVBY

- TRVALÝ ZÁBOR
- DOČASNÝ ZÁBOR

NOVÉ IS

- DEŠŤOVÁ KANALIZACE
- MELIORACE
- VÝTLAK
- VODOVOD
- NADZEMNÍ VEDENÍ NN
- NADZEMNÍ VEDENÍ VN
- PODZEMNÍ VEDENÍ NN
- PODZEMNÍ SDĚLOVACÍ VEDENÍ
- PLYNOVOD - STL

STÁVAJÍCÍ IS - INFORMATIVNÍ ZÁKRES

- PODZEMNÍ VEDENÍ NN
- PODZEMNÍ VEDENÍ VN
- NADZEMNÍ VEDENÍ NN
- NADZEMNÍ VEDENÍ VN
- NADZEMNÍ VEDENÍ VVN
- DEŠŤOVÁ KANALIZACE
- PLYNOVOD - STL
- PODZEMNÍ SDĚLOVACÍ VEDENÍ
- VODOVOD

Souřadnicový systém: S-JTSK
Výškový systém: Bpv

SO 143 Příjezd k DUN v km 1,500

Objednatel:



ŘEDITELSTVÍ
SILNIC
A DÁLNIC

Ředitelství silnic a dálnic s. p.
Čerčanská 2023/12, Krč, 140 00 Praha 4

Zhotovitel:



Valbek, spol. s r.o.
Vaňurova 505/17
460 07 Liberec 3



Zhotovitel:
Valbek, spol. s r.o.
Vaňurova 505/17
460 07 Liberec 3

Vypracoval	Bc. J. HALABURKA	Zak. číslo	21-L113-001
Zodp. projektant	ING. T. KLIMENT	Datum	02/2025
Tech. kontrola	ING. M. HANŽL	Stupeň	PDPS
Akce I/16 MLADÁ BOLES LAV - MARTINOVICE		Počet formátů	3 x A4
		Měřítko	1 : 1000
		Č. přílohy	Paré
Příloha SITUACE		2	