


SO 143 - PŘÍJEZD K DUN v km 1,500
VZOROVÉ PŘÍČNÉ ŘEZY
M 1 : 50

KATEGORIE MO1k -/5/30
JEDNOPRUHOVÁ, OBOUSMĚRNÁ


TRIDA DOPRAVNÍHO ZATÍŽENÍ IV
NÁVRHOVÁ ÚROVEŇ PORUŠENÍ D1
TYP PODLOŽÍ PIII (D1-A-2)
D1-N-11, TDZ IV, P III (DLE STARÉHO KATALOGU)

ŘEZ V MÍSTĚ NÁSYPU

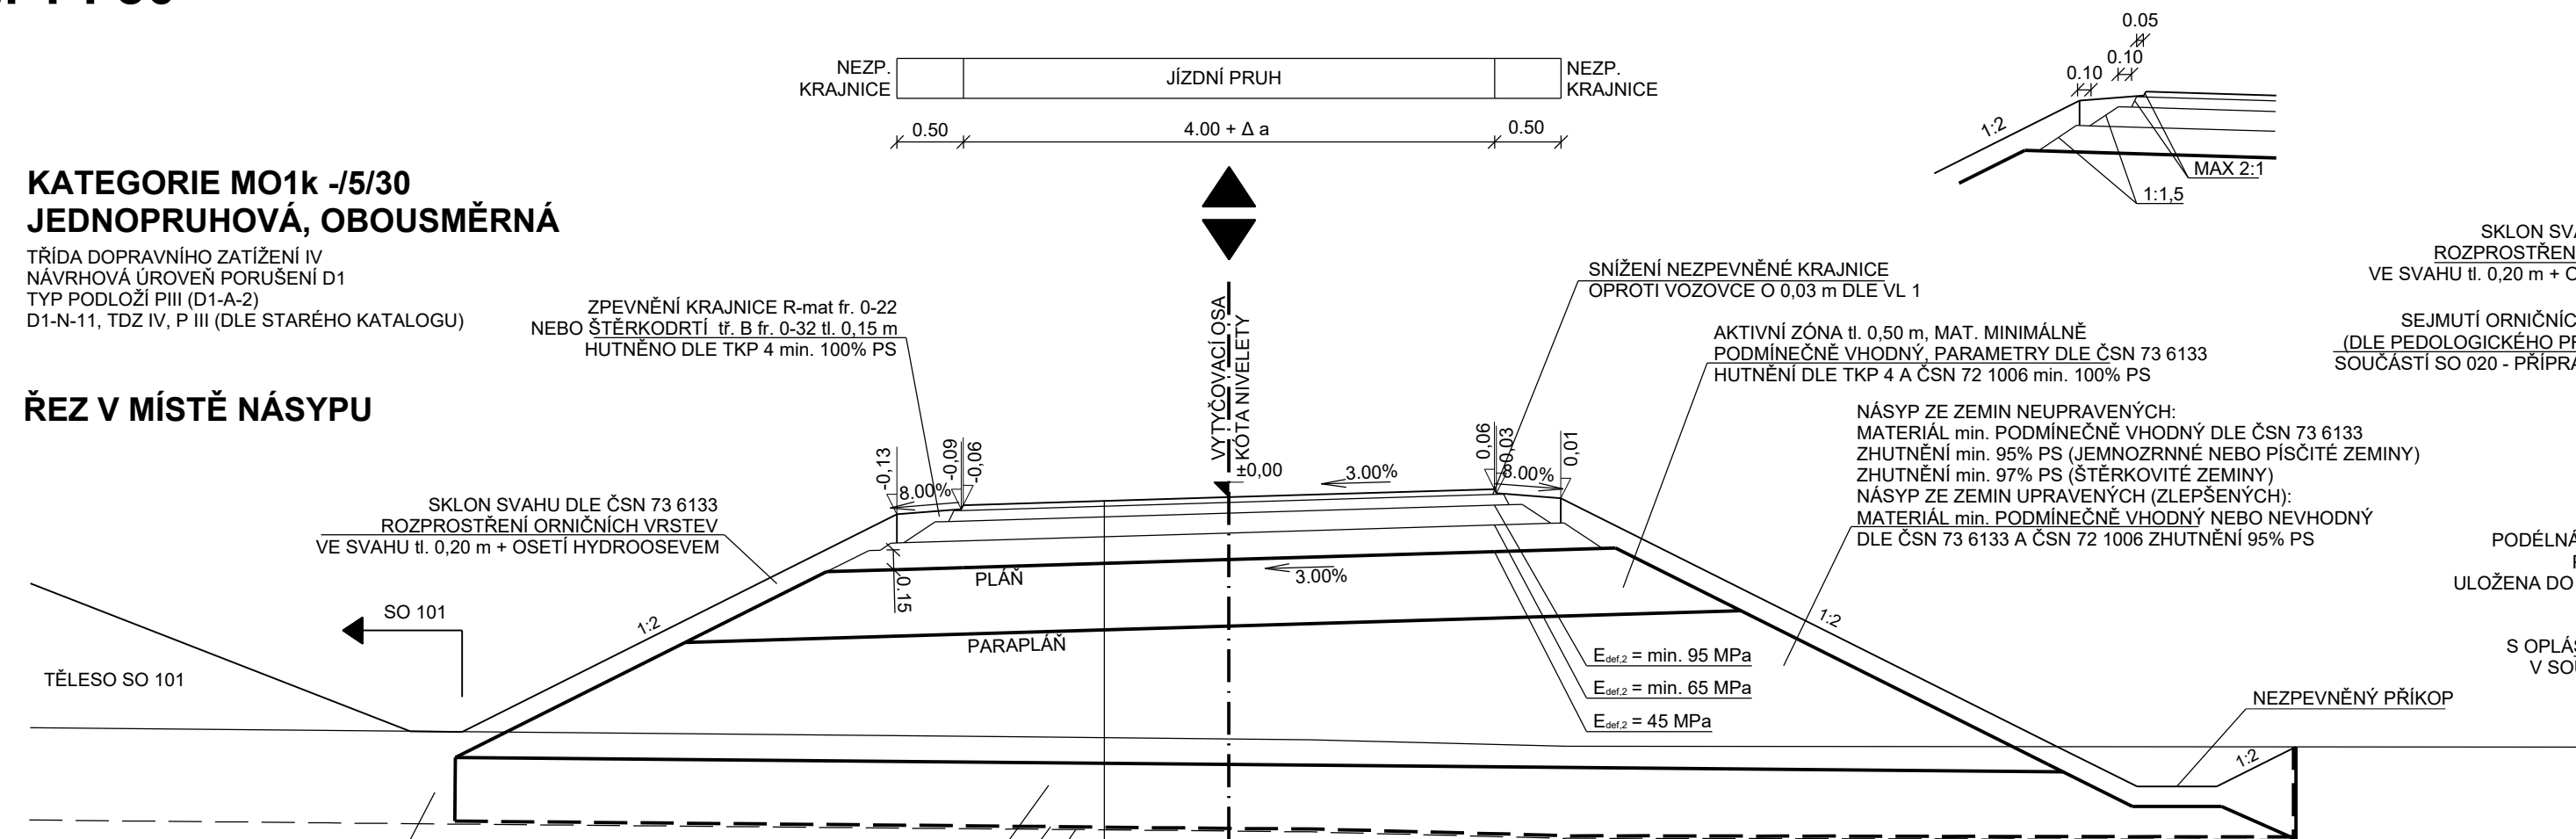


ASFALTOVÝ BETON PRO OBRUSNOU VRSTVU ASFALT 50/70	ACO 11	40 mm	ČSN EN 13 108-1, ČSN 73 6129
POSTRÍK SPOJOVACÍ EMULZÍ	PS-C	0,35kg/m ²	ČSN EN 13808, ČSN 73 6129
ASFALTOVÝ BETON PRO PODKLADNÍ VRSTVU ASFALT 50/70	ACP 16+	80 mm	ČSN EN 13 108-1, ČSN 73 6129
POSTRÍK INFILTRAČNÍ ŘEDĚNÍ ASF. EMULZÍ S POSYPKEM KAMENIVEM fr. 2/4 V MNOŽSTVÍ 3,0 kg/m ²	PI-C	1,00kg/m ²	ČSN 73 6129
MECHANICKÝ ZPEVNĚNÉ KAMENIVO (0/32 G _s)	MZK	150 mm	ČSN EN 13 285, ČSN 73 6126-1
ŠTĚRKODŮT II/A, (0/32 G _s)	ŠD _A	min. 200 mm	ČSN EN 13 285, ČSN 73 6126-1
CELKEM		min. 470 mm	


SCHÉMA BRODU V OSE POLNÍ CESTY

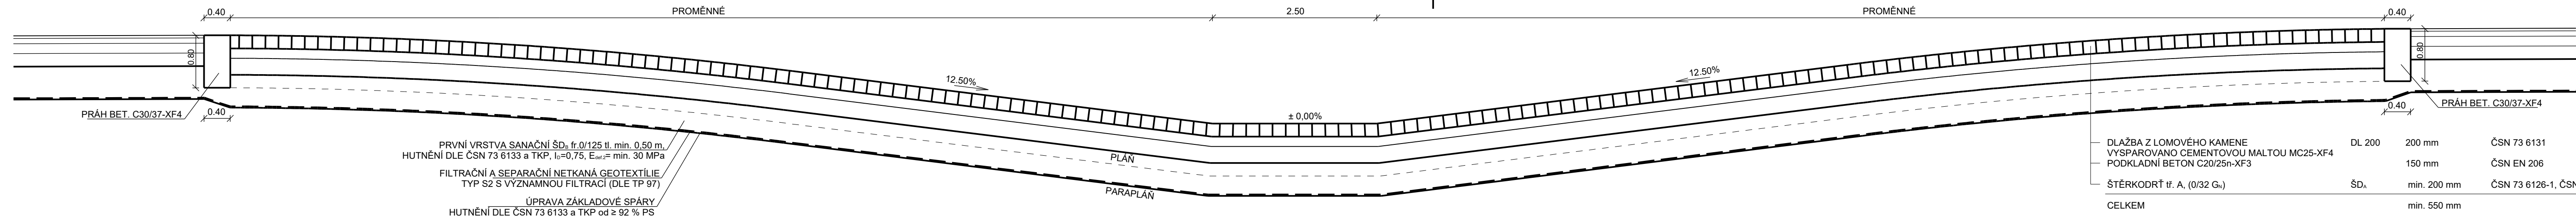


DETAIL UKONČENÍ VRSTEV VOZOVKY

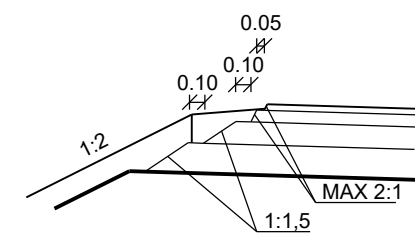


PŘÍČNÝ ŘEZ BRODEM

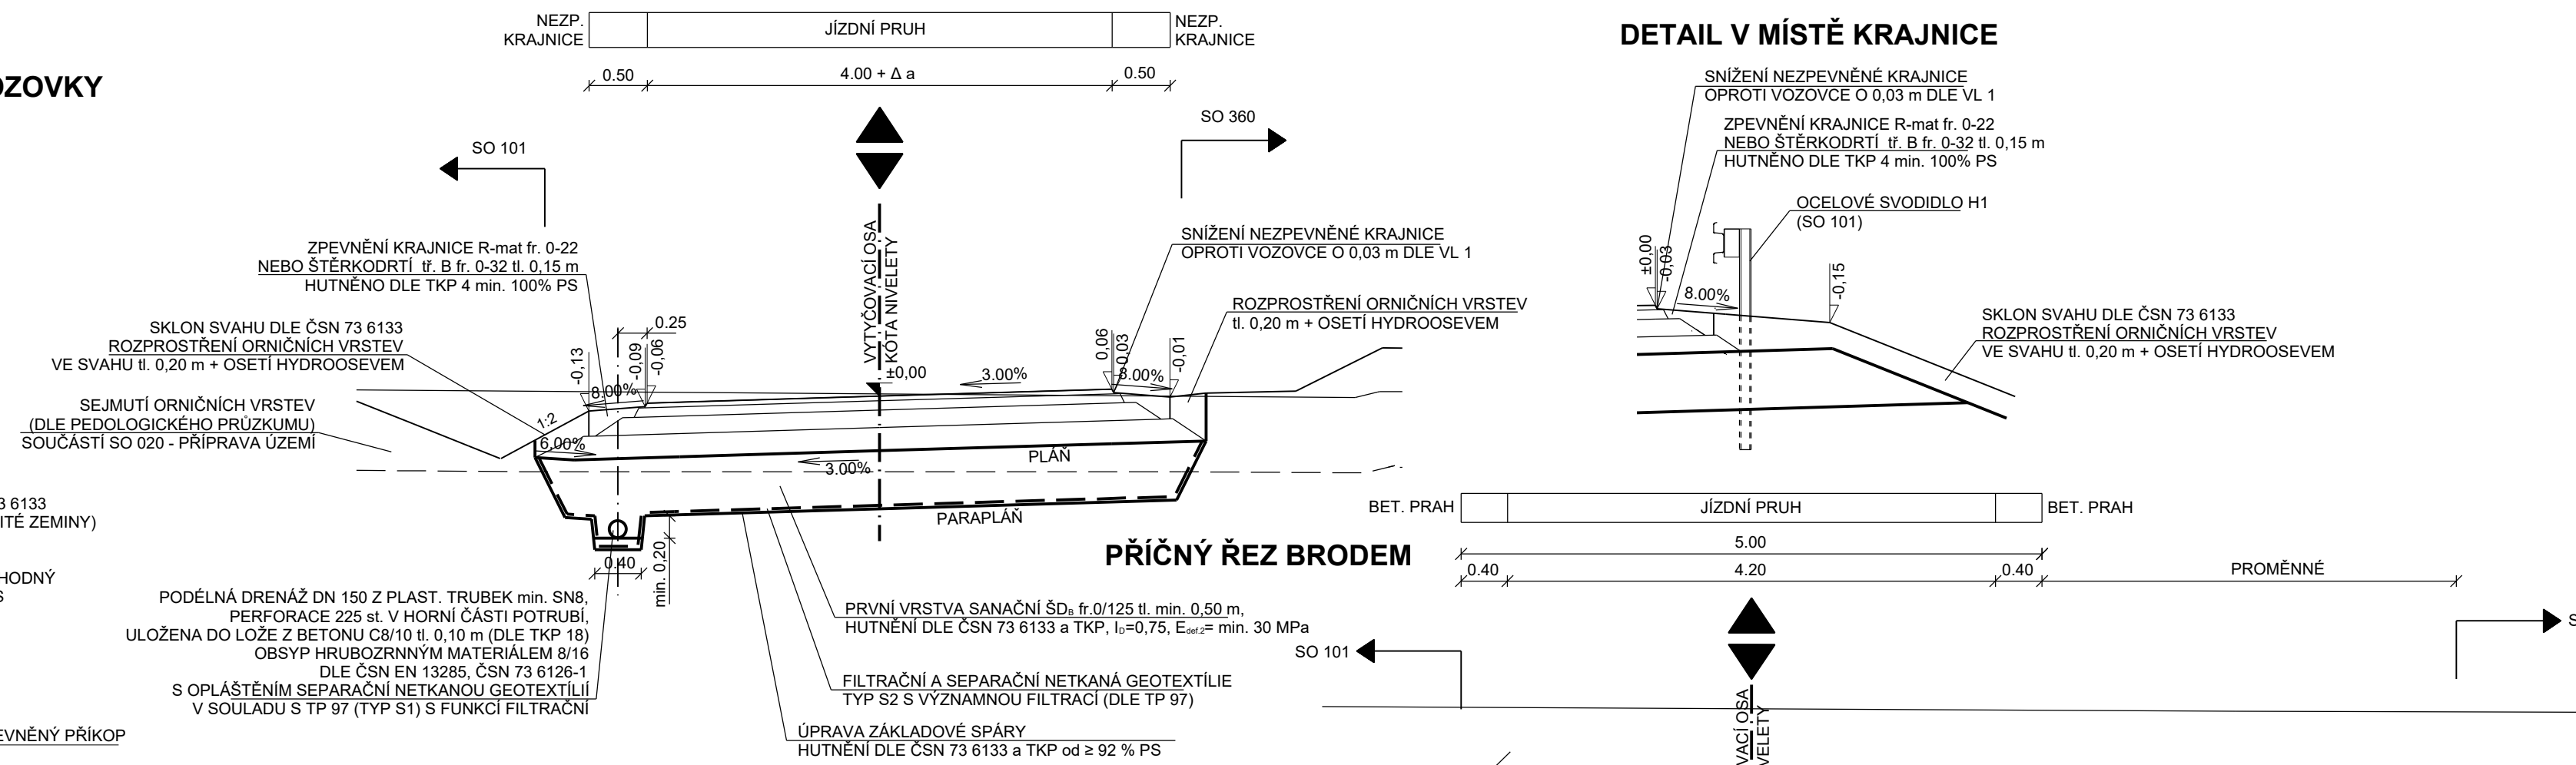

DETAIL NAPOJENÍ KONSTRUKČNÍCH VRSTEV VOZOVKY NA SO 101

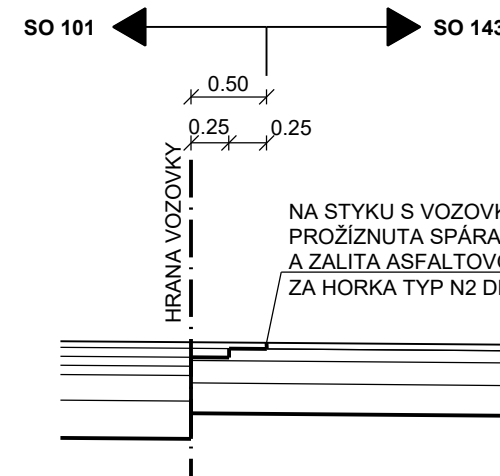

DETAIL V MÍSTĚ KRAJNICE

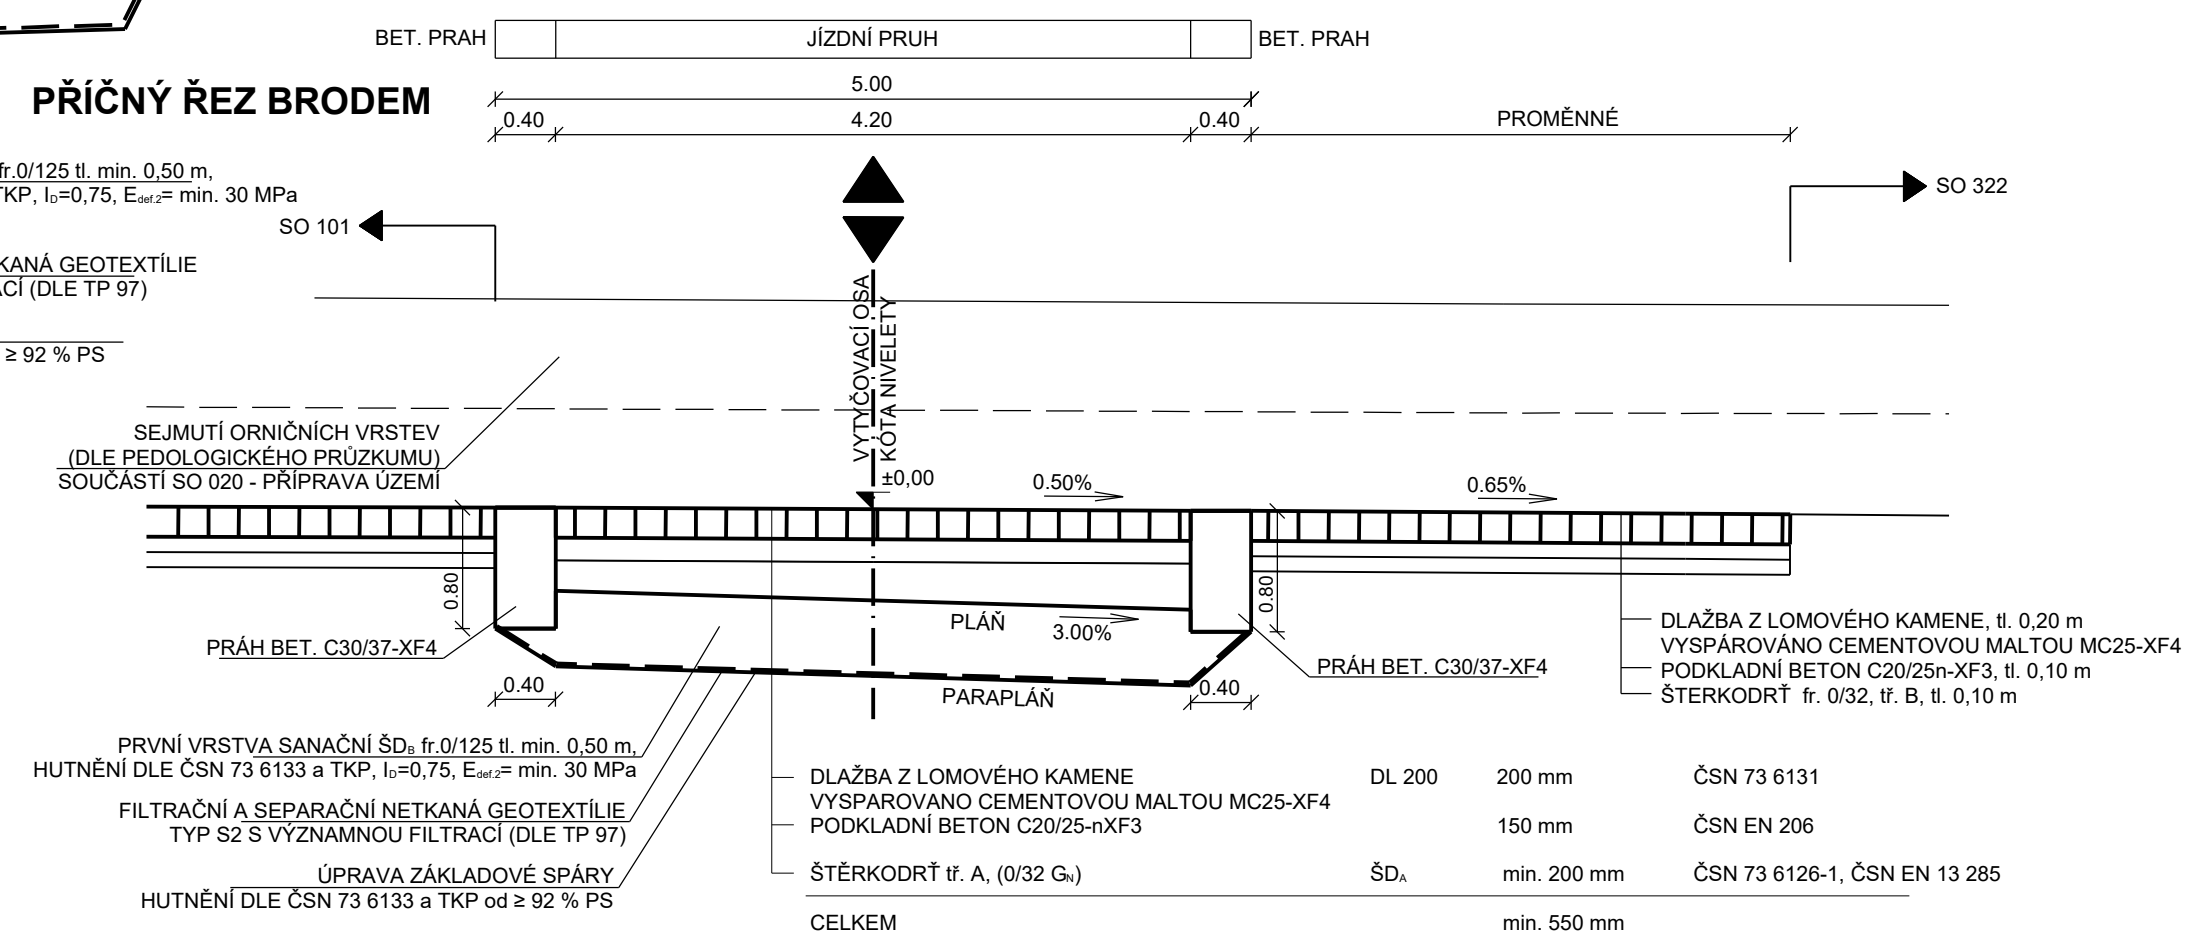

DLAŽBA Z LOMOVÉHO KAMENE	DL 200	200 mm	ČSN 73 6131
VYSPAROVANO CEMENTOVOU MALTOU MC25-XF4		150 mm	ČSN EN 206
PODKLADNÍ BETON C20/25-nXF3			
ŠTĚRKODRŤ tř. A _s (0/32 G _{ss})	ŠD _s	min. 200 mm	ČSN 73 6126-1, ČSN EN 13 285
CELKEM		min. 550 mm	

SO 143 Příjezd k DUN v km 1,500

Objednatel:



ŘEDITELSTVÍ SILNIC A DÁLNIC

Ředitelství silnic a dálnic s. p.
Čerčanská 2023/12, Krč, 140 00 Praha 4

Zhotovitel:



Valbek, spol. s r.o.
Vaňurova 505/17
460 07 Liberec 3



Zhotovitel:
Valbek, spol. s r.o.
Vaňurova 505/17
460 07 Liberec 3

Vypracoval	Bc. J. HALABURKA	Zak. číslo	21-L113-001
Zodp. projektant	ING. T. KLIMENT	Datum	02/2025
Tech. kontrola	ING. M. HANŽL	Stupeň	PDPŠ
Akce I/16 MLADÁ BOLESLAV - MARTINOVICE		Počet formátů	5 x A4
		Měřítko	1 : 50
		Č. přílohy	Paré
Příloha VZOROVÉ PŘÍČNÉ ŘEZY		4	